

การประกอบเลขที่ 3113
ASSEMBLY NO.

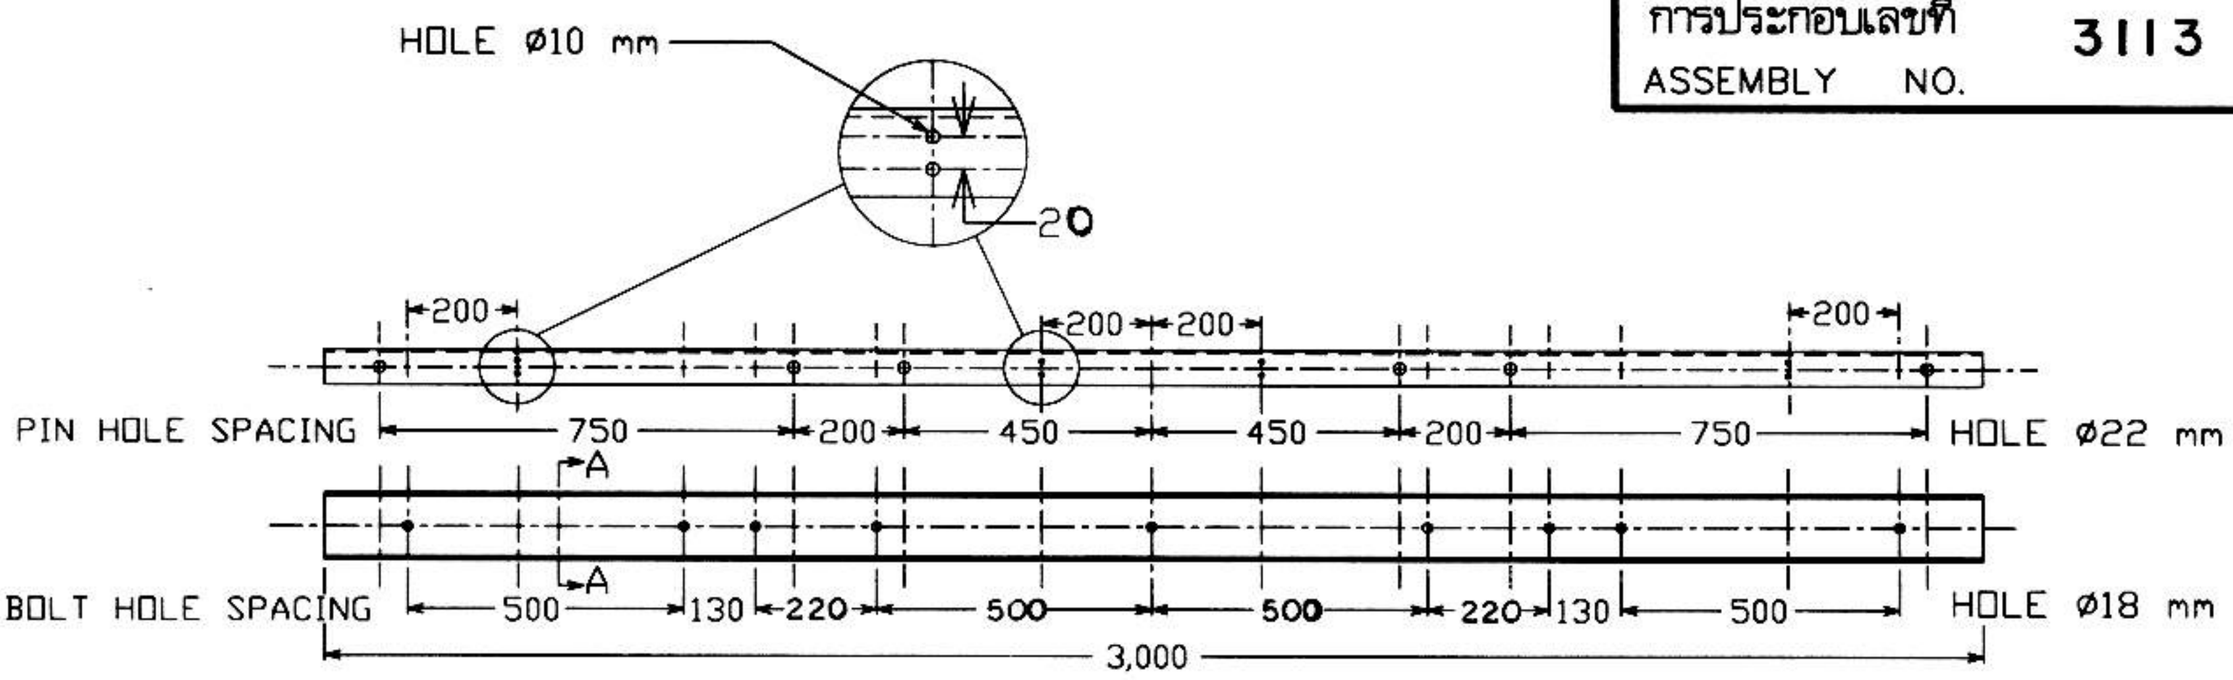

คอนเหล็กรูปรางน้ำ ขนาด 125 X 65 X 6 มม. ยาว 3,000 มม.

CHANNEL STEEL CROSSARM , 125 X 65 X 6 mm , 3,000 mm LONG

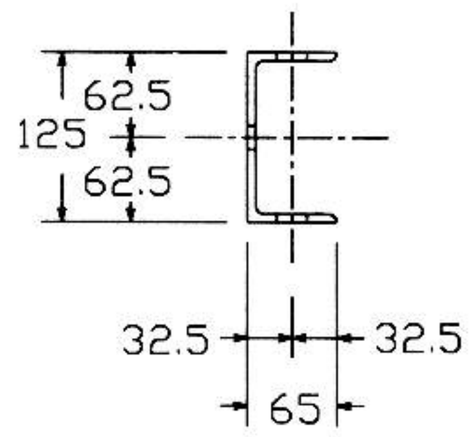

SECTION รูปตัด A-A

รายละเอียดการใช้งาน

1. ใช้เป็นคอนพาดสายเปลือยในระบบจำหน่าย 33 กิโลโวลต์ สำหรับการก่อสร้างแนวทางตรงมุมไม่เกิน 5 องศา ระยะห่างเสาสูงสุดไม่เกิน 80 ม.
2. ใช้เป็นคอนพาดสายเปลือยในระบบจำหน่าย 33 กิโลโวลต์ สำหรับการก่อสร้างแนวทางโค้งมุมไม่เกิน 30 องศา ระยะห่างเสาสูงสุดไม่เกิน 40 ม.
3. ใช้เป็นคอนพาดสายเปลือยในระบบจำหน่าย 33 กิโลโวลต์ สำหรับโครงสร้างเสาต้นเข้าปลายสาย, เข้าปลายสายสองข้าง และต้นทางโค้งมุม 30-60 องศา ระยะห่างเสาสูงสุดไม่เกิน 40 ม.

APPLICATION

1. USE AS 33 kV CROSSARM (FOR BARE CONDUCTOR) FOR TANGENT STRUCTURE NOT EXCEEDING 5° , SPAN LENGTH NOT EXCEEDING 80 m .
2. USE AS 33 kV CROSSARM (FOR BARE CONDUCTOR) FOR ANGLE STRUCTURE NOT EXCEEDING 30° , SPAN LENGTH NOT EXCEEDING 40 m .
3. USE AS 33 kV CROSSARM (FOR BARE CONDUCTOR) FOR DEADEND STRUCTURE, DOUBLE DEADEND STRUCTURE AND 30°-60° ANGLE STRUCTURE, SPAN LENGTH NOT EXCEEDING 40 m .

หมายเหตุ

1. เหล็กรูปรางน้ำ มีรายละเอียดตาม มอก. 1227 ตารางที่ 4
2. ให้อาบสังกะสีตามมาตรฐาน กฟภ.

NOTES

1. CHANNEL STEEL ACCORDING TO TIS 1227 TABLE 4 .
2. TO BE HOT DIP GALVANIZED ACCORDING TO PEA STANDARD .

กองวิศวกรรมไฟฟ้าและเครื่องกล ฝ่ายวิศวกรรม	การไฟฟ้าส่วนภูมิภาค	ใช้แทนแบบ ..... ถูกแทนโดยแบบ .....
ผู้เขียน EMD COMP. ผู้สำรวจ ..... วิศวกร ..... หัวหน้าแผนก ..... ผู้อำนวยการกอง ..... ผู้อำนวยการฝ่าย	ผู้ว่าการ	เขียนเสร็จวันที่ 20. พ.ย. 2539 แก้แบบวันที่ 29. ม.ค. 2540 มิติเป็น ..... มิลลิเมตร ..... มาตราส่วน .... 1 : 25 .....
รองผู้ว่าการ	คอนเหล็กรูปรางน้ำ 125 X 65 X 6 มม. ยาว 3,000 มม. CHANNEL STEEL CROSSARM 125 X 65 X 6 mm , 3,000 mm LONG	แบบเลขที่ SA4-015/39019 แผ่นที่ 1 ของจำนวน 1 แผ่น

13 S.A. 2539