การประกอบเลขที่ ASSEMBLY NO. **5215**

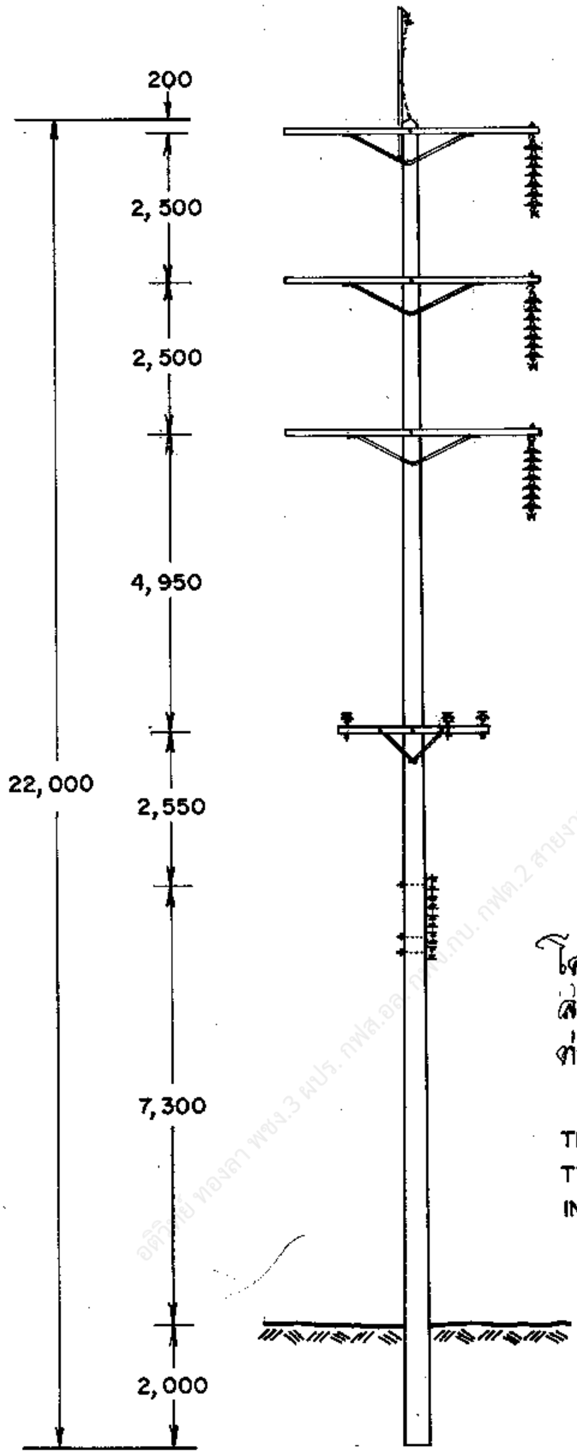

อดิวิทย์ ทองลา พชง.3 ผปร. กฟส.อล. กฟจ.กบ. กฟต.2 สายงาน (ต) ผวก. @PEA

โครงสร้างนี้ใช้งานได้เช่นเดียวกับโครงสร้าง แบบ SS–TG–1 (โครงสร้างแตกต่างกันที่วัสดุรายการที่ ② และ ⑦)

THIS STRUCTURE IS USED AS SS–TG–1 TYPE STRUCTURE (MATERIAL DIFFERENCE IN ITEM ② AND ⑦ FOR EACH STRUCTURE)

กองวิศวกรรมไฟฟ้าและเครื่องกล
ฝ่ายวิศวกรรม

ผู้เขียน
ผู้ตรวจ
วิศวกร
หัวหน้าแผนก
ผู้อำนวยการกอง
ผู้อำนวยการฝ่าย

รองผู้ว่าการฝ่ายเทคนิค

การไฟฟ้าส่วนภูมิภาค

ผู้ว่าการ

115 kV วงจรเดี่ยว สายไฟฟ้าเดี่ยว
เสาสำหรับทางตรง
แบบ SS–TG–3

115 kV SINGLE CIRCUIT SINGLE CONDUCTOR
TANGENT STRUCTURE
TYPE SS–TG–3

ใช้แทนแบบ
ถูกแทนโดยแบบ
เขียนเสร็จวันที่ 29 มิ.ย. 35
แก้แบบวันที่ 27 ก.ค. 38
มิติเป็น มิลลิเมตร
มาตราส่วน 1 : 125

แบบเลขที่ SAI–015/35022
แผ่นที่ 1 ของจำนวน 3 แผ่น

3 ก.ค. 2[illegible]

การประกอบเลขที่
ASSEMBLY NO. **5215**

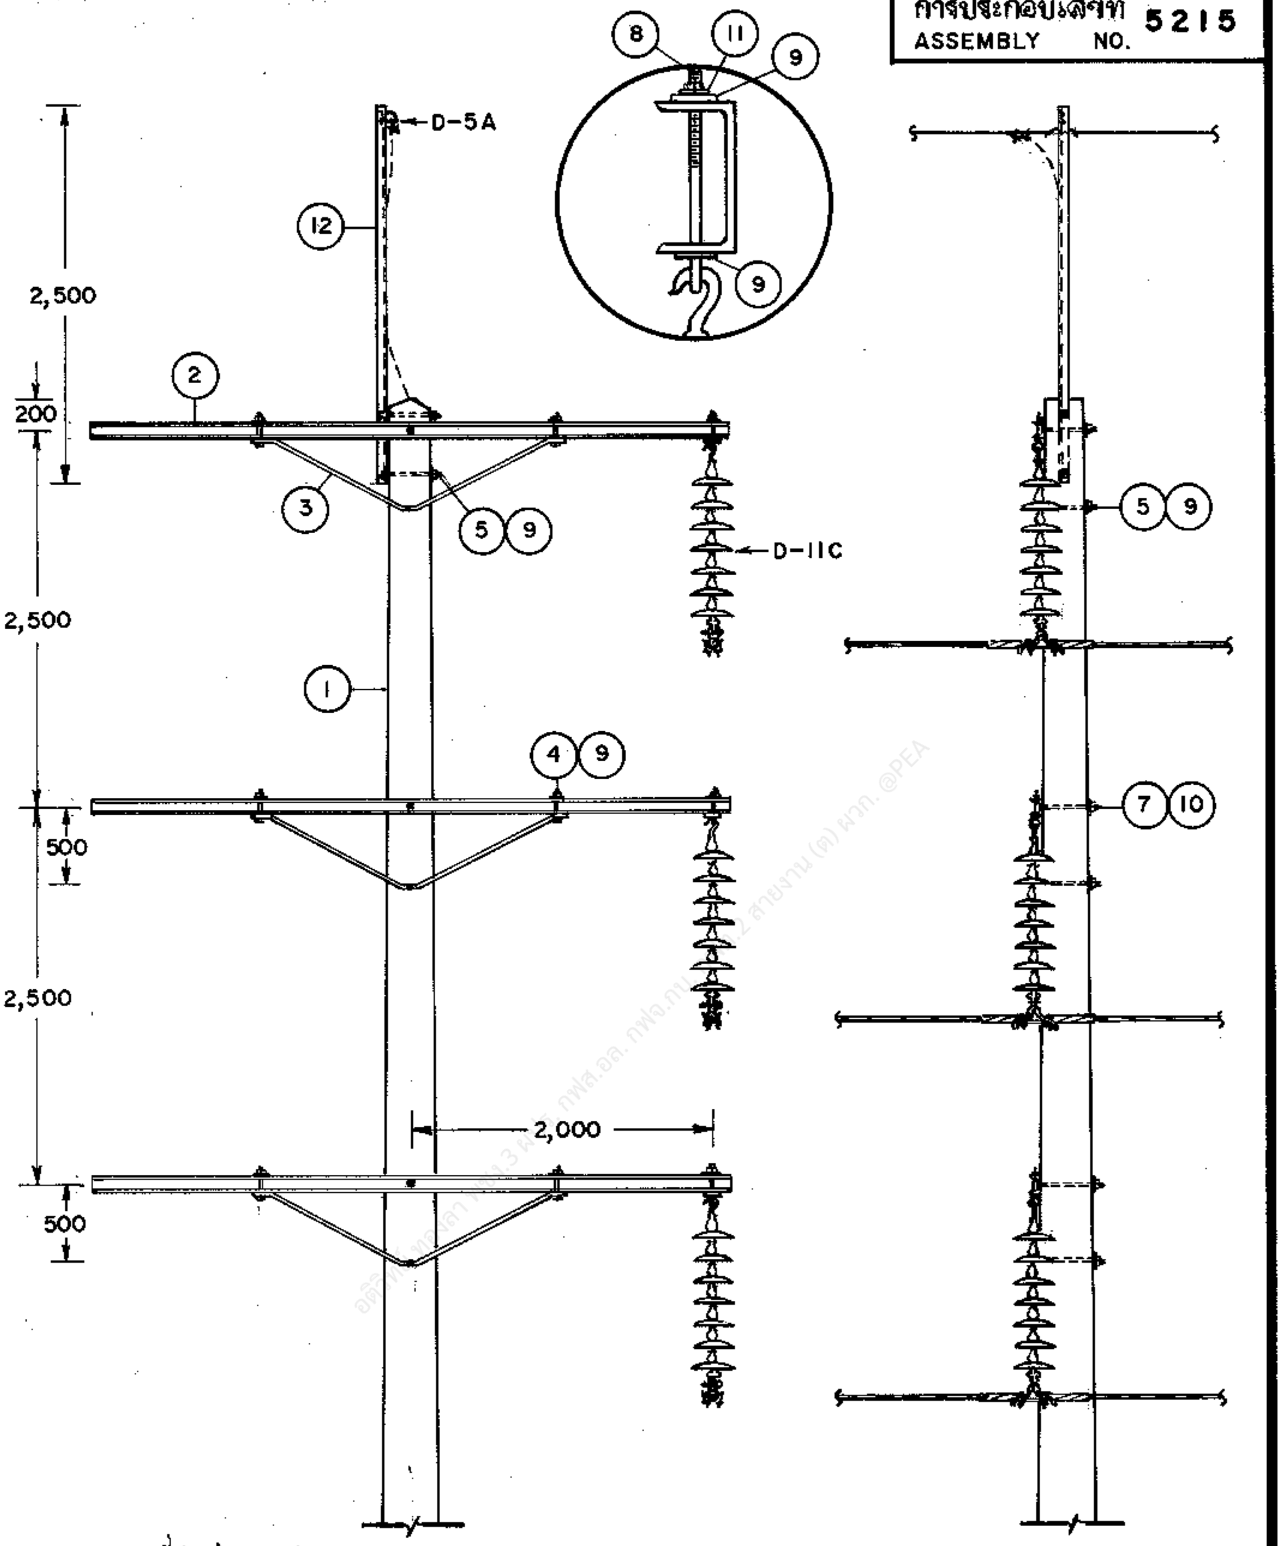

โครงสร้างนี้ ใช้งานได้เช่นเดียวกับโครงสร้าง แบบ SS-TG-1
THIS STRUCTURE IS USED AS SS-TG-1 TYPE STRUCTURE .

กองวิศวกรรมไฟฟ้าและเครื่องกล ฝ่ายวิศวกรรม	**การไฟฟ้าส่วนภูมิภาค**	ใช้แทนแบบ ____ ถูกแทนโดยแบบ ____
ผู้เขียน ____ ผู้สำรวจ ____ วิศวกร ____ หัวหน้าแผนก ____ ผู้อำนวยการกอง ____ ผู้อำนวยการฝ่าย ____	ผู้ว่าการ ____ 16 ก.ค.35	เขียนเสร็จวันที่ 29 มิ.ย.35 แก้แบบวันที่ 27 ต.ค.38
	115 kV วงจรเดี่ยว สายไฟฟ้าเดี่ยว เสาสำหรับทางตรง แบบ SS-TG-3	มิติเป็น มิลลิเมตร มาตราส่วน 1 : 5, 1 : 50
รองผู้ว่าการฝ่ายเทคนิค	115 kV SINGLE CIRCUIT SINGLE CONDUCTOR TANGENT STRUCTURE TYPE SS-TG-3	แบบเลขที่ SAI-015/35022 แผ่นที่ 2 ของจำนวน 3 แผ่น

การประกอบเลขที่ 5215
ASSEMBLY NO. 5215

บัญชีวัสดุ
BILL OF MATERIAL

ลำดับที่ ITEM	รายละเอียด DESCRIPTION	จำนวน REQ'D	วัสดุเลขที่ MAT. NO.
1	เสาคอนกรีต 22 ม. POLE, CONCRETE 22 m LONG	1	00010011 (0041)
2	คอนสายแบบเหล็ก ขนาด ⊏ 100X50X5 มม. ยาว 4.20 ม. มอก. 116 CROSSARM, STEEL ⊏ 100X50X5 mm, 4.20 m LONG, TIS 116	3	
3	เหล็กฉากรับคอนสาย ขนาด 50X50X6 มม. ช่วงกว้าง 1,800 มม. ดรอพ450มม. BRACE, ANGLE STEEL, 50X50X6 mm, 1,800 mm, WIDE 450 mm, DROP	3	00120007 (0119)
4	สลักเกลียว M 16X130 มม. BOLT, MACHINE, M 16X130 mm	6	01110200 (0220)
5	สลักเกลียว M 16X300 มม. BOLT, MACHINE, M 16X300 mm	3	01110204 (0224)
6	สลักเกลียว M 16X350 มม. BOLT, MACHINE, M 16X350 mm	2	01110205 (0225)
7	สลักเกลียว M 20X350 มม. BOLT, MACHINE, M 20X350 mm	3	01110300 (0232)
8	สลักห่วงโอแวล M 16X150 มม. BOLT, OVAL EYE M 16X150 mm	3	01150000 (0257)
9	แหวนสี่เหลี่ยมแบน 52X52X4.5 มม. รู Ø 18 มม. มอก. 258 WASHER, SQUARE FLAT 52X52X4.5 mm, HOLE Ø 18 mm, TIS 258	17	01180100 (0355)
10	แหวนสี่เหลี่ยมแบน 62X62X6 มม. รู Ø 22 มม. มอก. 258 WASHER, SQUARE FLAT 62X62X6 mm, HOLE Ø 22 mm, TIS 258	6	01180101 (0356)
11	แหวนสปริง M 16 มอก. 259 WASHER, LOCK, M 16, TIS 259	3	01180301 (0365)
12	เหล็กฉากรับสายล่อฟ้าทางตรง ยาว 2.50 ม. OVERHEAD GROUND WIRE BAYONET 2.50 m LONG	1	01010004 (0135)

รายละเอียด
DETAIL

D-11C	การประกอบลูกถ้วยแขวน SUSPENSION INSULATOR ASSEMBLY	3	
D-5A	การต่อสายล่อฟ้า OVERHEAD GROUND WIRE CONNECTION	1	
D-10A	ฐานรากเสา POLE FOUNDATION	1	

วัสดุลำดับที่ ②
MAT. ITEM ②

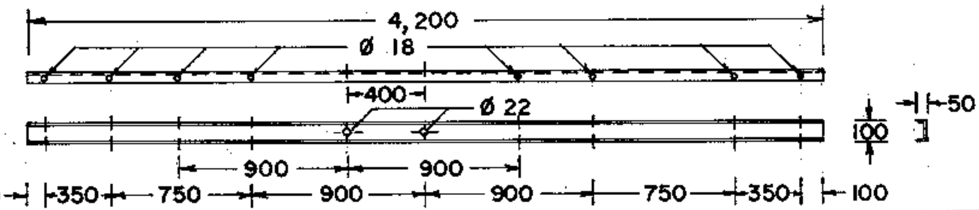

กองวิศวกรรมไฟฟ้าและเครื่องกล ฝ่ายวิศวกรรม	การไฟฟ้าส่วนภูมิภาค	ใช้แทนแบบ
ผู้เขียน ผู้ลอกลาย วิศวกร หัวหน้าแผนก ผู้อำนวยการกอง ผู้อำนวยการฝ่าย	ผู้ว่าการ ๒ ก.ค.35	ถูกแทนโดยแบบ เขียนเสร็จวันที่ 29 มิ.ย.35
	115 kV วงจรเดี่ยว สายไฟฟ้าเดี่ยว เสาสำหรับทางตรง แบบ SS-TG-3	แก้แบบวันที่ 27 ก.ค.38 มิติเป็น มิลลิเมตร มาตราส่วน 1 : 40
รองผู้ว่าการฝ่ายเทคนิค	115 kV SINGLE CIRCUIT SINGLE CONDUCTOR TANGENT STRUCTURE TYPE SS-TG-3	แบบเลขที่ SAL-015/35022 แผ่นที่ 3 ของจำนวน 3 แผ่น

3 ก.ค. 25[illegible]