
การประกอบเลขที่ 3808
ASSEMBLY NO.

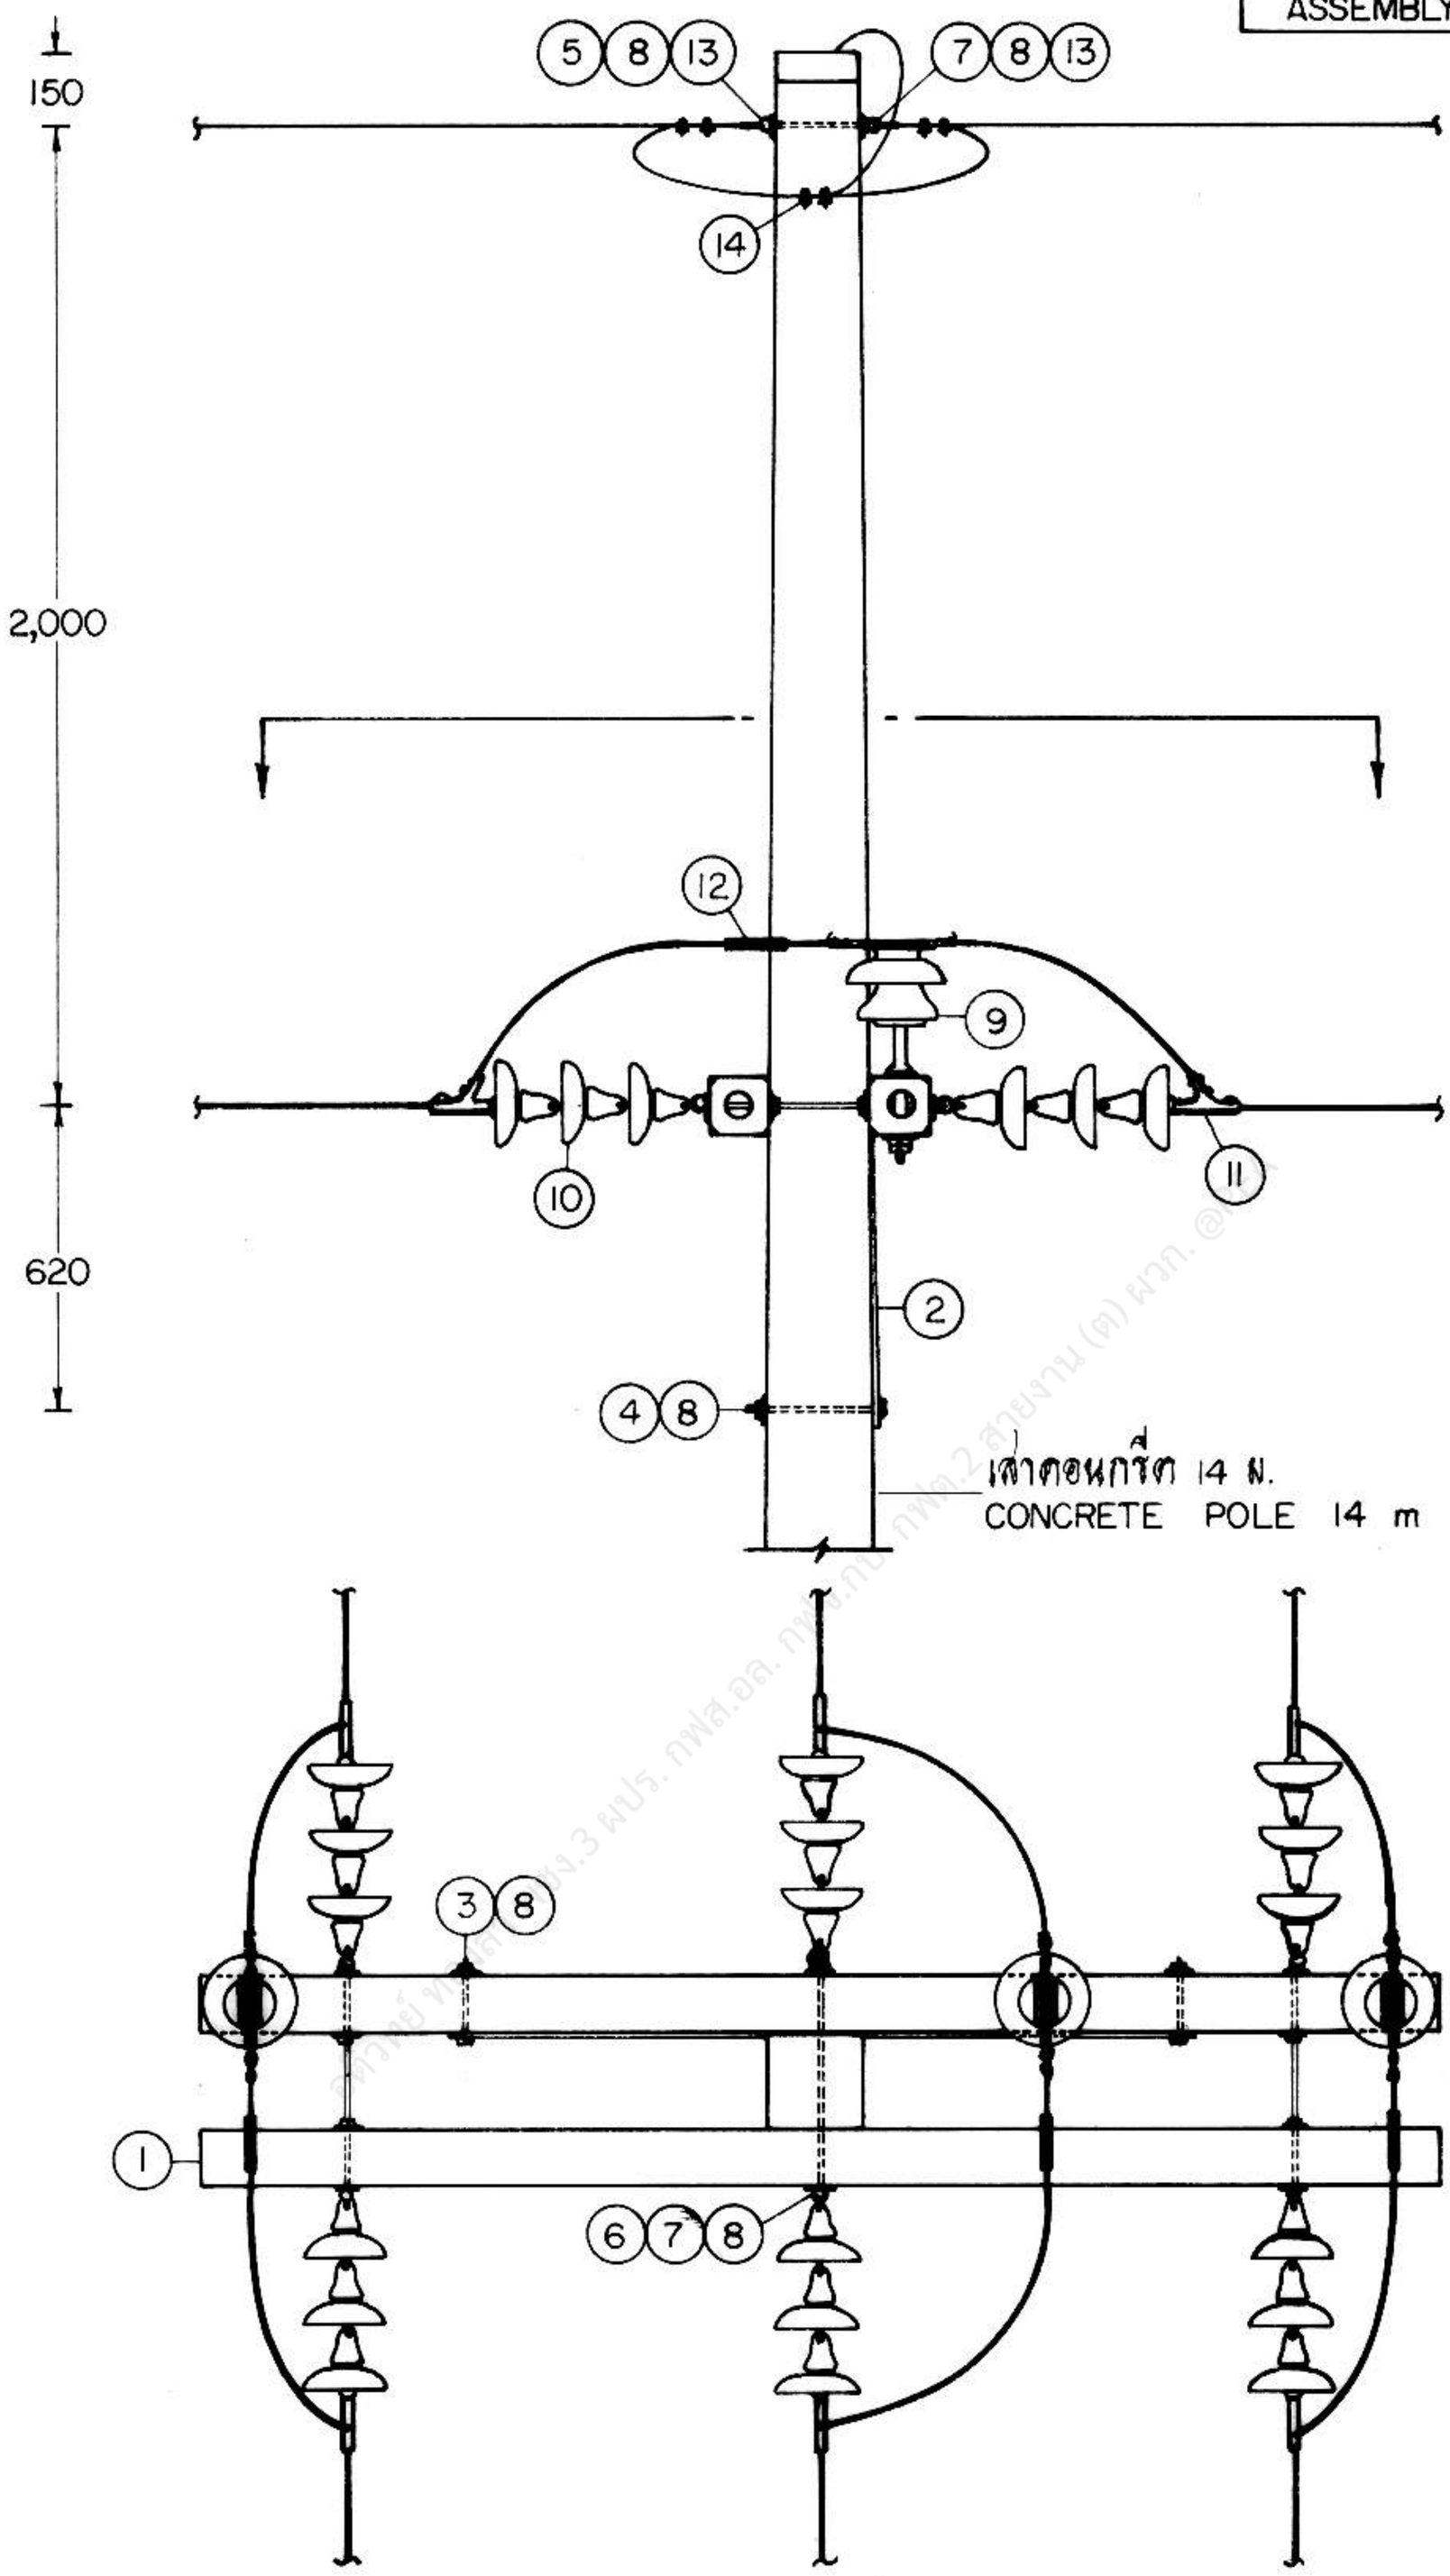

กองวิศวกรรมไฟฟ้าและเครื่องกล ฝ่ายวิศวกรรม	การไฟฟ้าส่วนภูมิภาค	ใช้แทนแบบ ถูกแทนโดยแบบ เขียนเสร็จวันที่ 28 พ.ค. 24 แก้แบบวันที่ มิติเป็น มม. มาตราส่วน 1 : 25
ผู้เขียน ผู้สำรวจ วิศวกร หัวหน้าแผนก หัวหน้ากอง ผู้อำนวยการฝ่าย รองผู้ว่าการฝ่ายเทคนิค	ผู้ว่าการ การประกอบคอน คอร. สปัน กับเสาคอนกรีต ระบบ 33 kV โครงสร้างเจ้าปลายสายสองข้าง SPUN PRESTRESSED CONCRETE CROSSARM ASSEMBLY 33 kV SYSTEM DOUBLE DEADEND STRUCTURE	แบบเลขที่ SAI-015/24018 แผ่นที่ 1 ของจำนวน 2 แผ่น

การประกอบเลขที่ ASSEMBLY NO. 3808

บัญชีวัสดุ
BILL OF MATERIAL

ลำดับที่ ITEM	รายละเอียด DESCRIPTION	จำนวน REQ'D	วัสดุเลขที่ MAT. NO.
1	คอน คอร. สปัน (สำหรับเข้าปลายสาย) 120X120X2,500 มม. CROSSARM, SPUN PRESTRESSED (FOR DEADENDING) 120 X 120 X 2,500 mm	2	00110004
2	เหล็กประกับไม้คอน 40 X 6 X 1,000 มม. BRACE, FLAT, FOR CROSSARM 40 X 6 X 1,000 mm	2	01200002
3	สลักเกลียว M 16 X 170 มม. BOLT, MACHINE, M 16 X 170 mm	2	01110201
4	สลักเกลียว M 16 X 250 มม. BOLT, MACHINE, M 16 X 250 mm	1	01110203
5	สลักห่วงกลม M 16 X 200 มม. BOLT, ROUND EYE, M 16 X 200 mm	1	01140001
6	สลักเกลียวห่วงกลม M 16 X 500 มม. BOLT, DOUBLE ARMING, ROUND EYE, M 16 X 500 mm	3	01130002
7	นัทรูปห่วง M 16 DIN 582 NUT, EYE M 16 DIN 582	4	01180001
8	แหวนสี่เหลี่ยมแผน 52 X 52 X 4.5 มม. รู Ø 18 มม. มอก. 258 WASHER, SQUARE, FLAT 52 X 52 X 4.5 mm HOLE Ø 18 mm TIS 258	15	01180100
9	ลูกถ้วยก้านตรง 33 kV มอก. 279 แบบ ค (แบบ 56-3) พร้อมก้าน INSULATOR, PIN TYPE, 33 kV TIS 279 TYPE C (CLASS 56-3) COMP. WITH PIN	3	03000002 03100001
10	ลูกถ้วยแขวน มอก. 354 แบบ ง (แบบ 52-4) INSULATOR, SUSPENSION TYPE, TIS 354 TYPE D (CLASS 52-4)	18	03020002
11	สเตรนแคล้มป์ สำหรับสายอะลูมิเนียม และอะลูมิเนียมแกนเหล็ก ขนาดตามต้องการ CLAMP, STRAIN, FOR AI AND ACSR SIZE AS REQUIRED	6	03110000_ 03110101
12	หลอดต่อสายชนิดมียไม่รับแรงดึง สายอะลูมิเนียม ขนาด 35 - 185 ต.มม. และอะลูมิเนียมแกนเหล็ก ขนาด 25/4 - 95/15 ต.มม. CONNECTOR, SPLICE, COMPRESSION TYPE, TENSIONLESS AI 35-185 mm^2 AND ACSR 25/4 - 95/15 mm^2	3	02410001-5 02410100_ 02410007
13	กายทิมเบิล สำหรับสายยึดโยง 50-95 ต.มม. THIMBLE, GUY, FOR STEEL WIRE 50-95 mm^2	2	01210304
14	ยูแคล้มป์ สลัก 1 ตัว M 8 (ไวร์โรป คลิ๊ป) CLAMP, SINGLE U-BOLT, M 8 (WIRE ROPE CLIP)	6	01230000

หมายเหตุ
1 รายละเอียดและข้อกำหนดการใช้งานของ คอน คอร.สปัน(สำหรับเข้าปลายสาย) ดูแบบเลขที่ SAI-015/24011
2 ในกรณีที่ขาดแคลนหลอดต่อสาย อนุโลมให้ใช้ พี.จี. คอนเนคเตอร์ 2 อัน ต่อจุด แทนได้

NOTES
1 DETAIL AND APPLICATION OF SPUN PRESTRESSED CONCRETE CROSSARM (FOR DEADENDING) SEE DWG. NO. SAI-015/24011
2 IN CASE OF LACKING TENSIONLESS SPLICE CONNECTOR, PERMIT TO USE 2 PG. CONNECTERS.

กองวิศวกรรมไฟฟ้าและเครื่องกล ฝ่ายวิศวกรรม	การไฟฟ้าส่วนภูมิภาค	ใช้แทนแบบ ถูกแทนโดยแบบ เขียนเสร็จวันที่ 28 พ.ค. 24 แก้แบบวันที่ มิติเป็น มาตราส่วน
ผู้เขียน ผู้สำรวจ วิศวกร หัวหน้าแผนก หัวหน้ากอง ผู้อำนวยการฝ่าย	ผู้ว่าการ การประกอบคอน คอร.สปัน กับเสาคอนกรีต ระบบ 33 kV โครงสร้างเข้าปลายสายสองข้าง	
รองผู้ว่าการฝ่ายเทคนิค	SPUN PRESTRESSED CONCRETE CROSSARM ASSEMBLY 33 kV SYSTEM DOUBLE DEADEND STRUCTURE	แผนเลขที่ SAI-015/24018 แผ่นที่ 2 ของจำนวน 2 แผ่น