

การประกอบเลขที่ ASSEMBLY NO. 0208

N – สายเป็นกลาง NEUTRAL LINE
A,B,C – สายเฟส PHASE LINE
L – สายดับไฟถนน STREET LIGHTING LINE

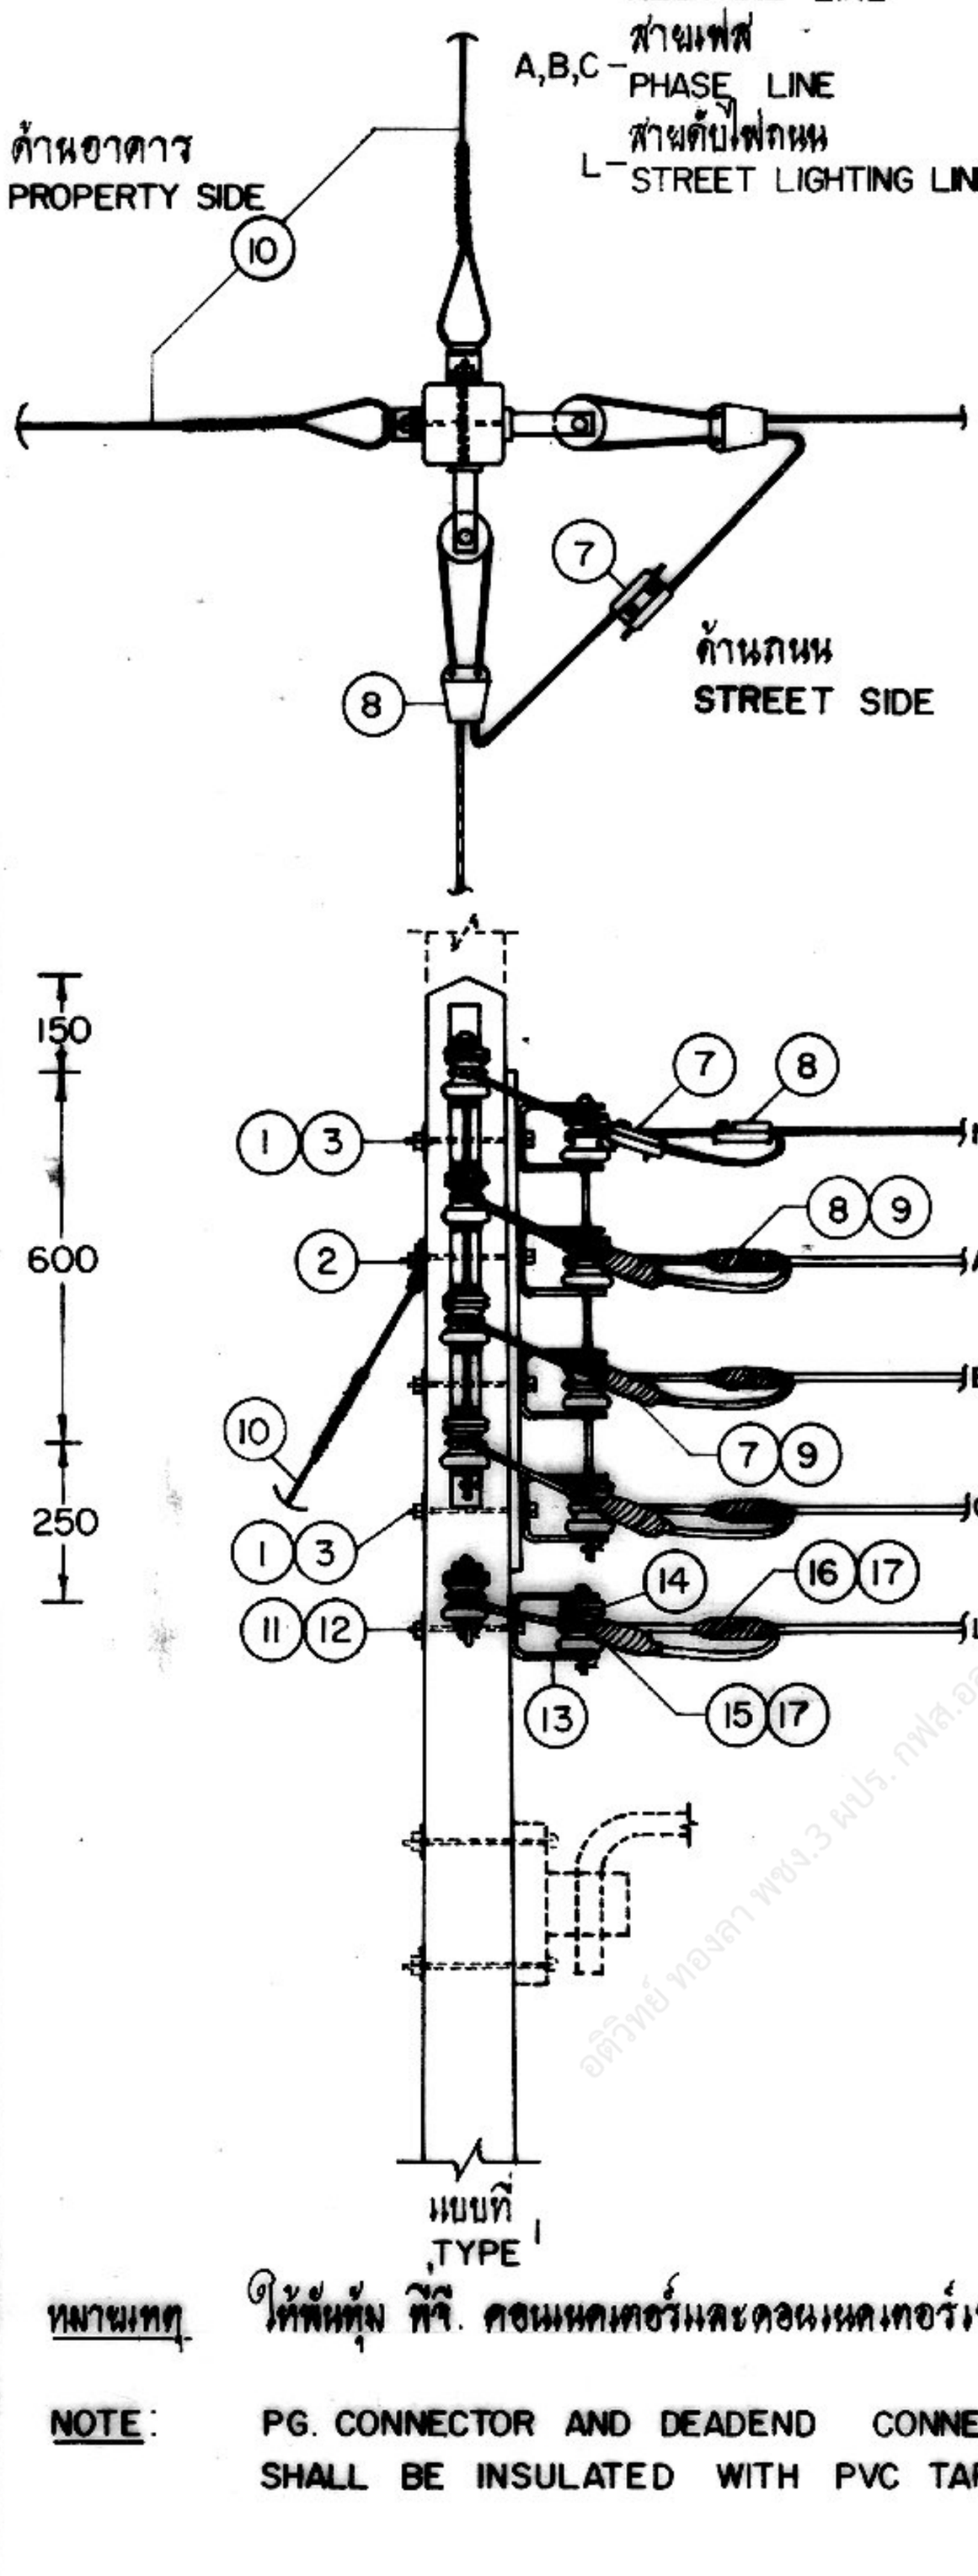


แบบที่ TYPE 1

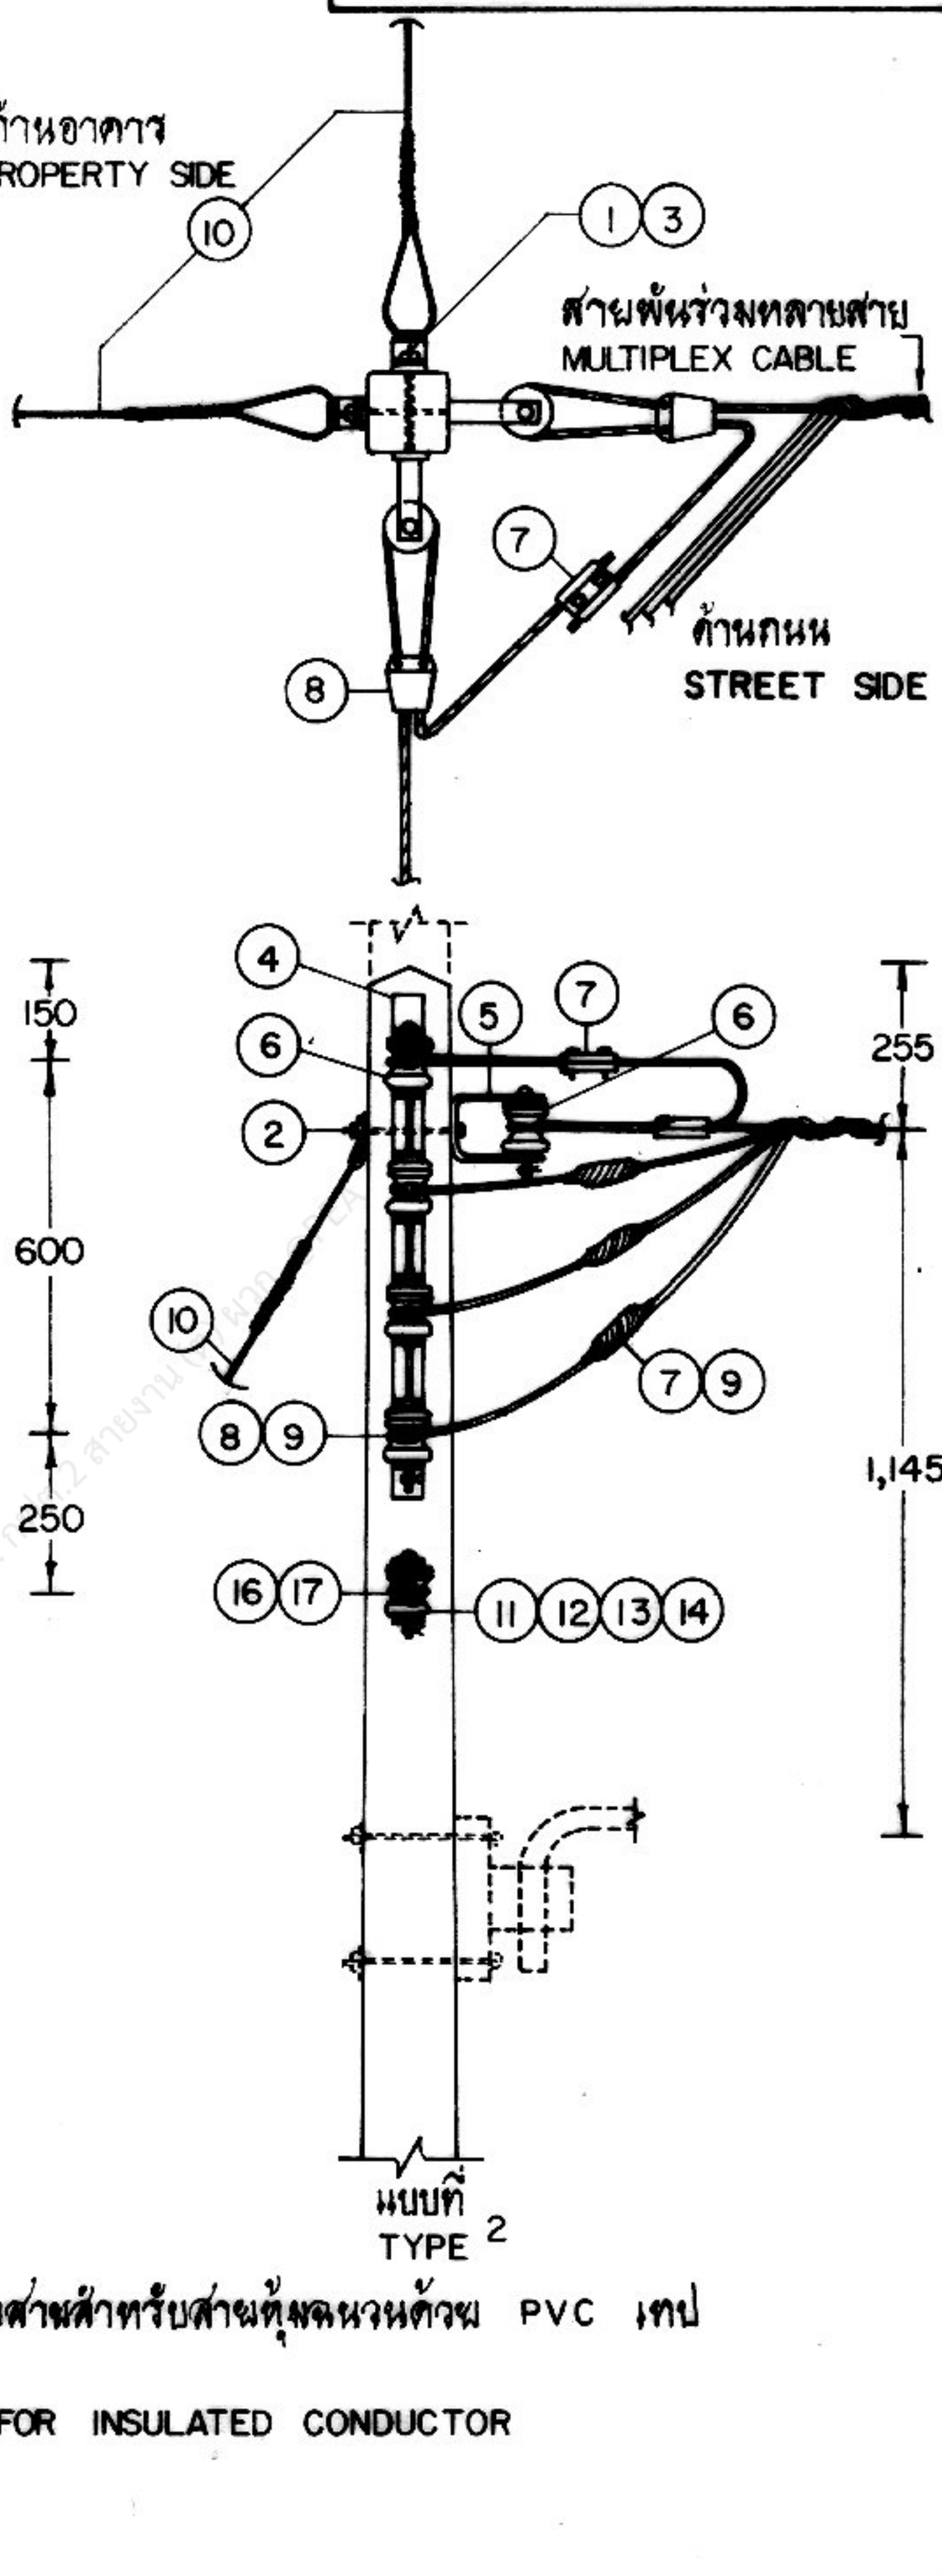


แบบที่ TYPE 2

หมายเหตุ ให้พันหุ้ม พี.จี. คอนเนคเตอร์และดอนเนคเตอร์เข้าปลายสายสำหรับสายหุ้มฉนวนด้วย PVC เทป

NOTE: PG. CONNECTOR AND DEADEND CONNECTOR FOR INSULATED CONDUCTOR SHALL BE INSULATED WITH PVC TAPE.

| | | |
|---|---|---|
| กองวิศวกรรมไฟฟ้าและเครื่องกล<br>ฝ่ายวิศวกรรม | การติดตั้งแร็คแรงต่ำกับเสาคอนกรีต 9 ม.<br>สำหรับทางโค้ง 60° ขึ้นไป | ใช้แทนแบบ<br>ถูกแทนโดยแบบ<br>เขียนเสร็จวันที่ 15 ส.ค. 21<br>แก้แบบวันที่<br>มิติเป็น มม.<br>มาตราส่วน 1:20 |
| ผู้เขียน<br>ผู้สำรวจ<br>วิศวกร<br>หัวหน้าแผนก<br>หัวหน้ากอง<br>ผู้อำนวยการฝ่าย<br>รองผู้ว่าการฝ่ายเทคนิค<br>29 ส.ค. 2521 | ผู้ว่าการ | แบบแสดงที่ SAI-015/21044<br>แผ่นที่ 1 ของจำนวน 2 แผ่น |
| | SECONDARY RACK INSTALLATION ON 9m CONCRETE POLE FOR ANGLE STRUCTURE OVER 60° | |

การประกอบเลขที่ ASSEMBLY NO. 0208

# บัญชีวัสดุ
BILL OF MATERIAL

| ลำดับที่ ITEM | รายละเอียด DESCRIPTION | จำนวน REQ'D 1 | จำนวน REQ'D 2 | วัสดุเลขที่ MAT. NO. |
|---|---|---|---|---|
| 1 | สลักเกลียว M 16 X 170 มม.<br>BOLT, MACHINE, M 16 X 170 mm | 6 | 3 | 01110201 |
| 1a | สลักเกลียว M 16 X 250 มม. สำหรับเสาคอนกรีต 12 ม.<br>BOLT, MACHINE, M 16 X 250 mm FOR 12 m CONCRETE POLE | 6 | 3 | 01110203 |
| 2 | สลักเกลียว M 16 X 200 มม.<br>BOLT, MACHINE, M 16 X 200 mm | 2 | 2 | 01110202 |
| 2a | สลักเกลียว M 16 X 250 มม. สำหรับเสาคอนกรีต 12 ม.<br>BOLT, MACHINE, M 16 X 250 mm FOR 12 m CONCRETE POLE | 2 | 2 | 01110203 |
| 3 | แหวนสี่เหลี่ยมแบน 52 X 52 X 4.5 มม. รู Ø 18 มม. มอก. 258<br>WASHER, SQUARE, FLAT, 52 X 52 X 4.5 mm HOLE Ø 18 mm TIS 258 | 6 | 3 | 01180100 |
| 4 | แร็ค 4 X 200 มม. แบบหลังฉีน<br>RACK, SECONDARY, MEDIUM PRESSED STEEL, 4 X 200 mm EXT. BACK | 2 | 1 | 03130002 |
| 5 | ที่จับลูกรอก สำหรับลูกรอก มอก. 227 ( แบบ 53-2)<br>CLEVIS, FLAT STEEL, FOR INSULATOR TIS 227 ( CLASS 53-2) | – | 1 | 03130100 |
| 6 | ลูกรอกแรงต่ำ มอก. 227 แบบ ข ( แบบ 53-2)<br>INSULATOR, SPOOL TYPE, L.T. TIS 227 TYPE B ( CLASS 53-2 ) | 8 | 5 | 03030000 |
| 7 | พี.จี. คอนเนคเตอร์ สำหรับสายอะลูมิเนียม ขนาดตามต้องการ<br>CONNECTOR, PARALLEL GROOVE, Al SIZE AS REQUIRED | 4 | 4 | 02300102 - 02300103 |
| 8 | คอนเนคเตอร์เข้าปลายสายอะลูมิเนียม ขนาดตามต้องการ<br>CONNECTOR, DEADEND, Al SIZE AS REQUIRED | 8 | 5 | 02310000 - 02310002 |
| 9 | PVC เทป กว้าง 19 มม. ( ใช้ความยาว 2 ม. ต่อจุด ) มอก. 386<br>PVC TAPE 19 mm WIDE ( 2 m LONG PER POINT ) TIS 386 | | | 02180001 or 02180002 |
| 10 | การประกอบสายยึดโยง GY-01<br>GUY ASSEMBLY GY-01 | 2 | 2 | — |
| 10a | การประกอบสายยึดโยง GY-02 สำหรับเสาคอนกรีต 12 ม.<br>GUY ASSEMBLY GY-02 FOR 12 m CONCRETE POLE | 2 | 2 | — |
| | สำหรับการติดตั้งสายดันไฟถนน<br>FOR STREET LIGHTING INSTALLATION | | | |
| 11 | สลักเกลียว M 16 X 170 มม.<br>BOLT, MACHINE, M 16 X 170 mm | 2 | 1 | 01110201 |
| 11a | สลักเกลียว M 16 X 250 มม. สำหรับเสาคอนกรีต 12 ม.<br>BOLT, MACHINE, M 16 X 250 mm FOR 12 m CONCRETE POLE | 2 | 1 | 01110203 |
| 12 | แหวนสี่เหลี่ยมแบน 52 X 52 X 4.5 มม. รู Ø 18 มม. มอก. 258<br>WASHER, SQUARE, FLAT, 52 X 52 X 4.5 mm HOLE Ø 18 mm TIS 258 | 2 | 1 | 01180100 |
| 13 | ที่จับลูกรอก สำหรับลูกรอก มอก. 227 ( แบบ 53-2)<br>CLEVIS, FLAT STEEL, FOR INSULATOR TIS 227 ( CLASS 53-2) | 2 | 1 | 03130100 |
| 14 | ลูกรอกแรงต่ำ มอก. 227 แบบ ข ( แบบ 53-2)<br>INSULATOR, SPOOL TYPE, L.T. TIS 227 TYPE B ( CLASS 53-2 ) | 2 | 1 | 03030000 |
| 15 | พี.จี. คอนเนคเตอร์ สลักคู่ สำหรับสายอะลูมิเนียม 25-95 ต.มม.<br>CONNECTOR, PARALLEL GROOVE, DOUBLE BOLT, Al 25 – 95 $mm^2$ | 1 | – | 02300102 |
| 16 | คอนเนคเตอร์เข้าปลายสายอะลูมิเนียม 25-35 ต.มม.<br>CONNECTOR, DEADEND, Al 25 – 35 $mm^2$ | 2 | 1 | 02310000 |
| 17 | PVC เทป กว้าง 19 มม. ( ใช้ความยาว 2 ม. ต่อจุด ) มอก. 386<br>PVC TAPE, 19 mm WIDE ( 2 m LONG PER POINT) TIS 386 | | | 02180001 or 02180002 |

| | | |
|---|---|---|
| กองวิศวกรรมไฟฟ้าและเครื่องกล<br>ฝ่ายวิศวกรรม | การไฟฟ้าส่วนภูมิภาค | ใช้แทนแบบ<br>ถูกแทนโดยแบบ<br>เขียนเสร็จวันที่ 15 สค. 21<br>แก้แบบวันที่<br>มิติเป็น<br>มาตราส่วน |
| ผู้เขียน พรชัย<br>ผู้สำรวจ<br>วิศวกร<br>หัวหน้าแผนก<br>หัวหน้ากอง<br>ผู้อำนวยการฝ่าย<br>รองผู้ว่าการฝ่ายเทคนิค | ผู้ว่าการ<br>การติดตั้งแร็คแรงต่ำกับเสาคอนกรีต 9 ม.<br>สำหรับทางโค้ง 60° ขึ้นไป<br>SECONDARY RACK INSTALLATION ON 9m CONCRETE POLE<br>FOR ANGLE STRUCTURE OVER 60° | แบบเลขที่ SAI-015/21044<br>แผ่นที่ 2 ของจำนวน 2 แผ่น |