

การประกอบเลขที่ ASSEMBLY NO.	3101

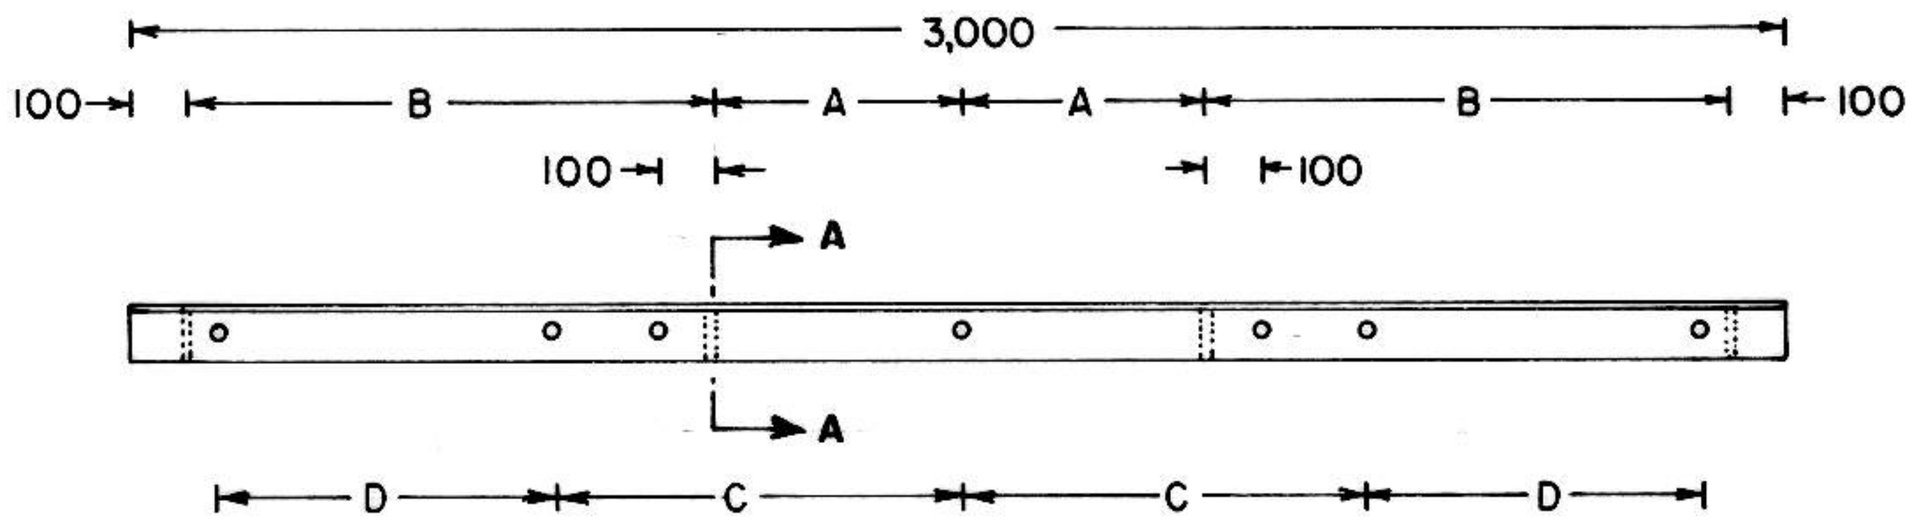

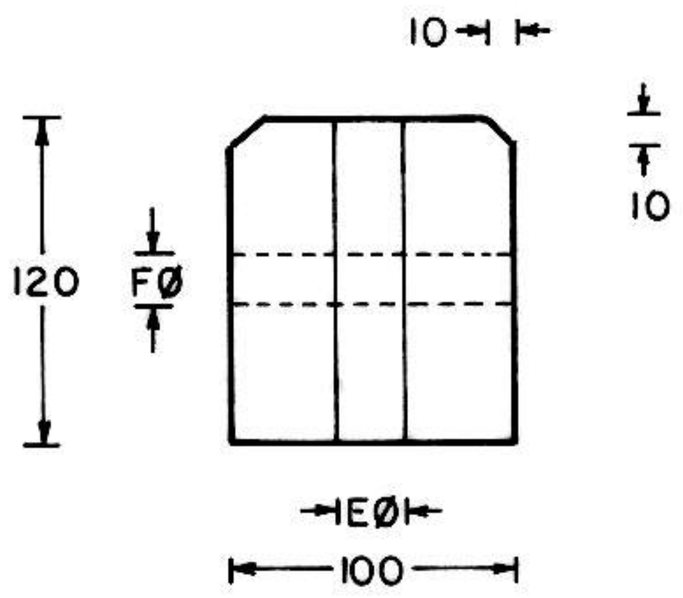

รูปตัด
SECTION A-A

การเจาะรูไม้คอน
CROSSARM DRILLING PLAN

กฟภ. PEA วัสดุเลขที่ MATERIAL NO.	A	B	C	D	E Ø	F Ø	วัสดุ MATERIAL
	มิติ	มม.	DIMENSIONS			mm	
00100003 (0101)	450	950	720	630	22	18	ไม้ WOOD ดูวัสดุเลขที่ SEE MAT. NO.

กองแผนการ	การไฟฟ้าส่วนภูมิภาค	ใช้แทนแบบ ..... ถูกแทนโดยแบบ ..... เขียนเสร็จวันที่ 23/2/08 แก้แบบวันที่ ..... มิติเป็น มม. มาตราส่วน 1:5, 1:25
ผู้เขียน ..... สถาปนิก ..... วิศวกร ประจักษ์ จิระ/คร ..... หัวหน้าแผนก ..... หัวหน้ากอง	ผู้ว่าการ ..... ไม้คอน 3.00 เมตร	
รองผู้ว่าการฝ่ายเทคนิค	CROSSARM 3.00 m	แผนเลขที่ I50-015/080237 แผ่นที่ 1 จากจำนวน 1 แผ่น