การประกอบเลขที่
ASSEMBLY NO. 5687 I

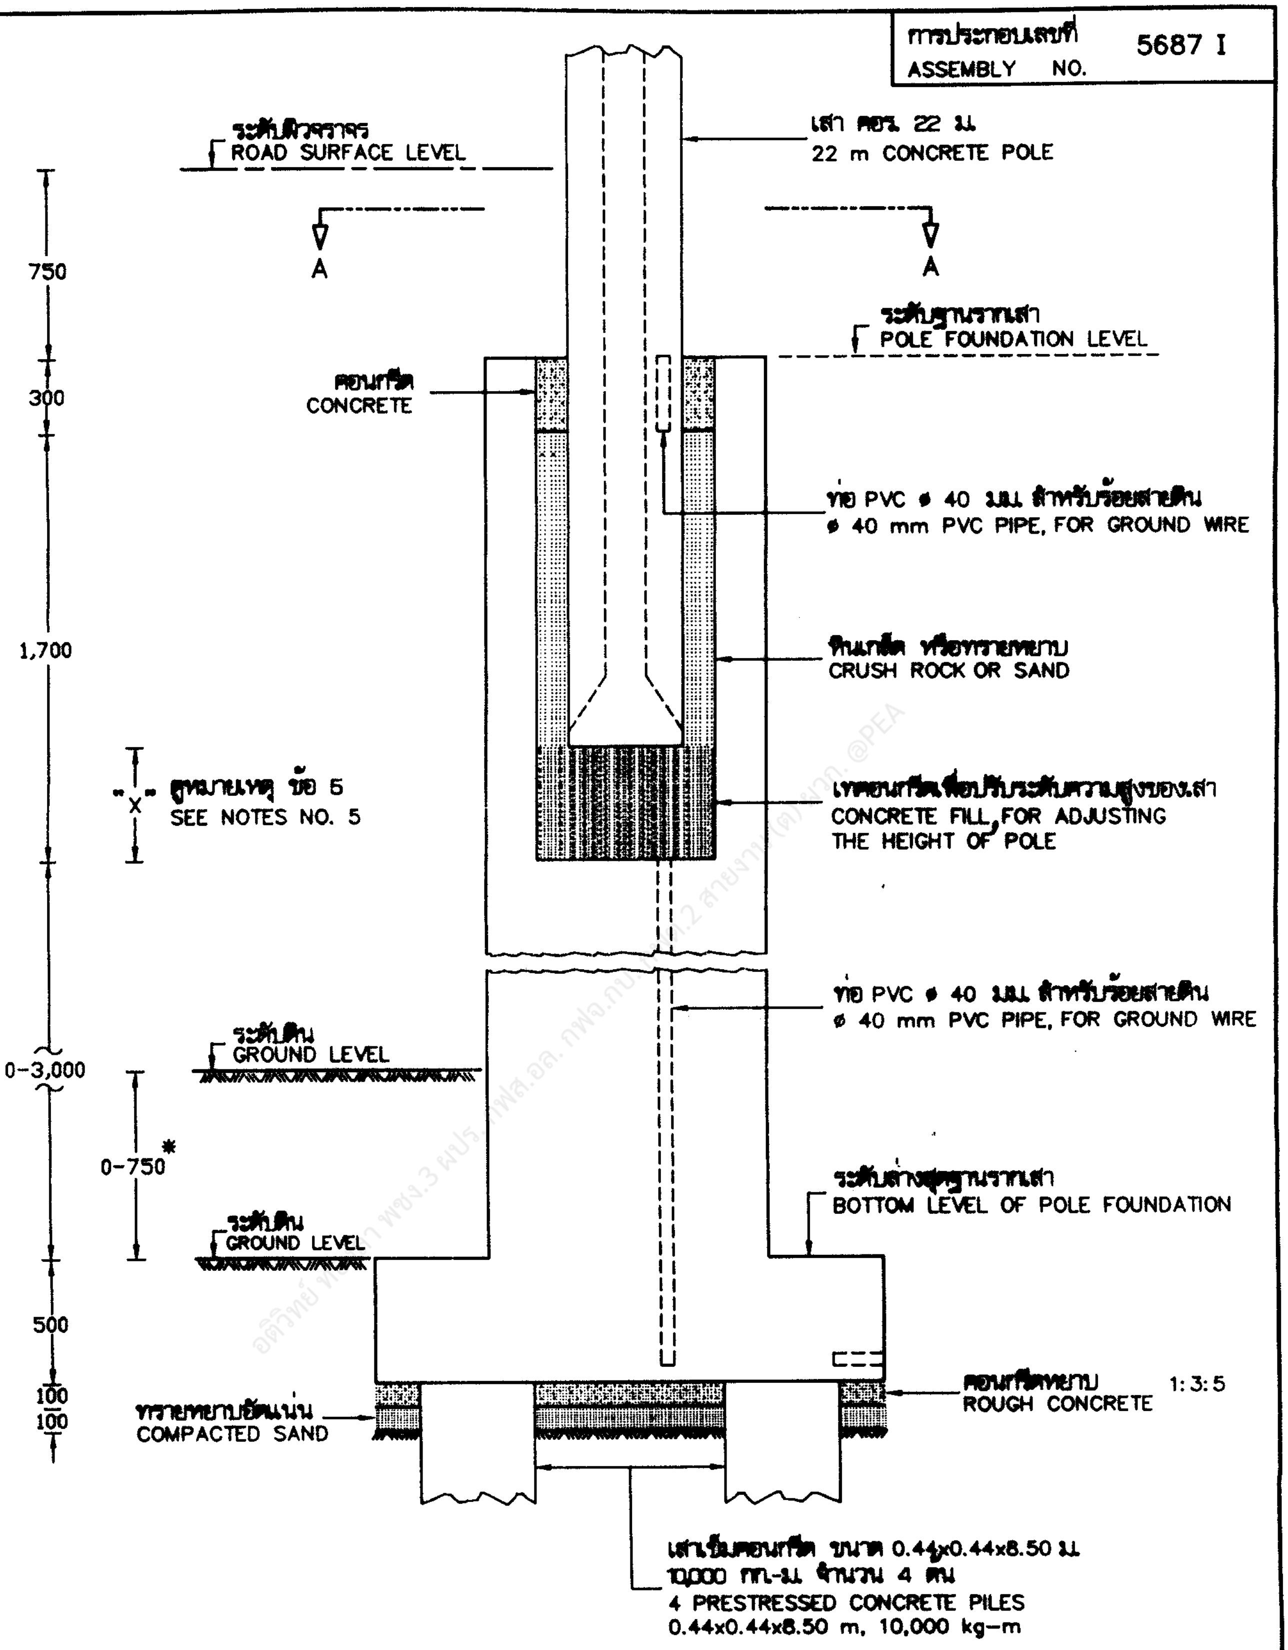
ระดับผิวจราจร
ROAD SURFACE LEVEL
เสา คอร. 22 ม.
22 m CONCRETE POLE
A
A
750
300
1,700
0–3,000
0–750*
500
100
100
ระดับฐานรากเสา
POLE FOUNDATION LEVEL
คอนกรีต
CONCRETE
ท่อ PVC ø 40 มม. สำหรับร้อยสายดิน
ø 40 mm PVC PIPE, FOR GROUND WIRE
หินเกล็ด หรือทรายหยาบ
CRUSH ROCK OR SAND
"X"
ดูหมายเหตุ ข้อ 5
SEE NOTES NO. 5
เทคอนกรีตเพื่อปรับระดับความสูงของเสา
CONCRETE FILL, FOR ADJUSTING THE HEIGHT OF POLE
ท่อ PVC ø 40 มม. สำหรับร้อยสายดิน
ø 40 mm PVC PIPE, FOR GROUND WIRE
ระดับดิน
GROUND LEVEL
ระดับดิน
GROUND LEVEL
ระดับล่างสุดฐานรากเสา
BOTTOM LEVEL OF POLE FOUNDATION
คอนกรีตหยาบ 1:3:5
ROUGH CONCRETE
ทรายหยาบอัดแน่น
COMPACTED SAND
เสาเข็มคอนกรีต ขนาด 0.44x0.44x8.50 ม.
10,000 กก.-ม. จำนวน 4 ต้น
4 PRESTRESSED CONCRETE PILES
0.44x0.44x8.50 m, 10,000 kg–m

อดิวิทย์ ... พชง.3 ผปร. กฟส.อล. กฟจ.กบ. ...2 สายงาน (ต) ผวภ. @PEA

กองมาตรฐานระบบไฟฟ้า ฝ่ายมาตรฐานและความปลอดภัย	การไฟฟ้าส่วนภูมิภาค	ใช้แทนแบบ SA1–015/45018 ถูกแทนโดยแบบ ....
ผู้เขียน ..สมชาย.......... ผู้ตรวจ .... วิศวกร .... หัวหน้าแผนก .... ผู้อำนวยการกอง .... ผู้อำนวยการฝ่าย	ผู้ว่าการ	เขียนเสร็จวันที่ .10. ส.ค. 2547. แก้แบบวันที่ ....
	รายละเอียดที่ 10 A ฐานรากเสา (แบบที่ 23)	มิติเป็น มิลลิเมตร.......... มาตราส่วน....1:30..........
รองผู้ว่าการวางแผนและพัฒนาระบบไฟฟ้า	DETAIL 10 A POLE FOUNDATION (TYPE 23)	แบบเลขที่ SA1–015/47026 แผ่นที่ .1. ของจำนวน .2. แผ่น

2 ก.ย. 2547

การประกอบเลขที่
ASSEMBLY NO. 5687 I

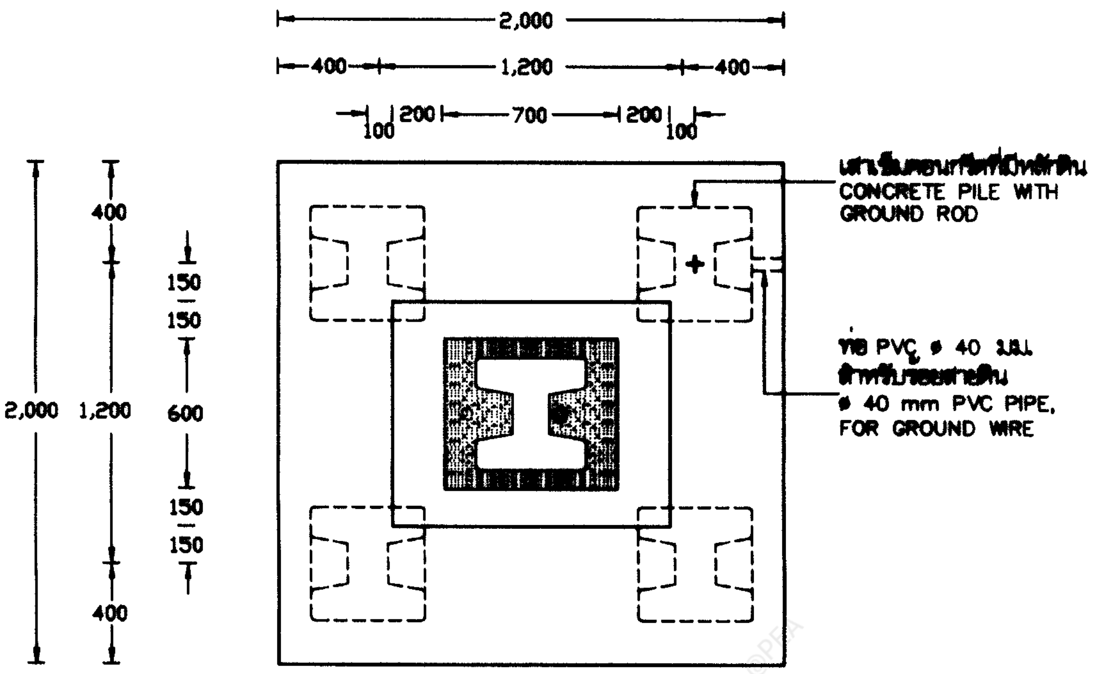
2,000
400
1,200
400
100
200
700
200
100
2,000
1,200
400
400
150
150
600
150
150
เสาเข็มคอนกรีตที่มีหลักดิน
CONCRETE PILE WITH GROUND ROD
ท่อ PVC ø 40 มม.
สำหรับร้อยสายดิน
ø 40 mm PVC PIPE,
FOR GROUND WIRE

รูปตัด A–A
SECTION A–A

หมายเหตุ

1 ใช้ในกรณีทางตรงหรือทางโค้ง ที่มีสายยึดโยง (กรณีพื้นที่ก่อสร้างฐานรากเสามีระดับต่ำกว่าระดับผิวจราจร 2.00-5.75 ม.)

2 ดูรายละเอียดเพิ่มเติมใน แบบเลขที่ IB2-011/44020

3 ดูข้อกำหนดการติดตั้งฐานรากเสาในเขตทางหลวง ตามแบบเลขที่ SA1-015/43012 (การประกอบเลขที่ 5687)

4* กรณีพื้นที่ก่อสร้างฐานรากเสามีระดับต่ำกว่าระดับผิวจราจร ระหว่าง 2.00-2.75 ม. ให้ก่อสร้างฐานรากเสาต่ำกว่าระดับดิน ระหว่าง 0.75-0.00 ม. (ระดับล่างสุดฐานรากเสาจะต่ำกว่าระดับผิวจราจร 2.75 ม.)

5 ระยะ "X"= 450 มม. สำหรับการก่อสร้างฐานรากเสาในพื้นที่ทางหลวงที่ไม่มีทางเท้า ส่วนพื้นที่อื่นๆ ระยะ "X"= 0 มม.

NOTES

1 USE FOR STRAIGHT OR ANGLE LINE WITH GUY (IN CASE OF GROUND SURFACE LEVEL IS BETWEEN 2.00–5.75 m LOWER THAN ROAD SURFACE LEVEL) .

2 SEE ADDITIONAL DETAIL, DWG. NO. IB2–011/44020 .

3 SEE RECOMMENDATION, FOR POLE FOUNDATION INSTALLATION IN HIGHWAY AREA, DWG. NO. SA1–015/43012 (ASSEMBLY NO. 5687) .

4* IN CASE OF GROUND SURFACE LEVEL IS BETWEEN 2.00–2.75 m LOWER THAN ROAD SURFACE LEVEL, CONSTRUCTED FOUNDATION SHALL BE BETWEEN 0.75–0.00 m LOWER THAN GROUND SURFACE LEVEL (BOTTOM LEVEL OF POLE FOUNDATION IS 2.75 m. LOWER THAN ROAD SURFACE LEVEL) .

5 THE "X" IS 450 mm HEIGHT FOR FOUNDATION CONSTRUCTION IN HIGHWAY AREA WHICH HAVE NO PAVEMENT, OTHER AREA THE "X" IS ZERO .

กองมาตรฐานระบบไฟฟ้า ฝ่ายมาตรฐานและความปลอดภัย	การไฟฟ้าส่วนภูมิภาค	ใช้แทนแบบ SA1–015/45018 ถูกแทนโดยแบบ ....
ผู้เขียน ..สมชาย.......... ผู้ตรวจ .... วิศวกร .... หัวหน้าแผนก .... ผู้อำนวยการกอง .... ผู้อำนวยการฝ่าย	ผู้ว่าการ	เขียนเสร็จวันที่ .10. พ.ค. 2547 แก้แบบวันที่ ....
	รายละเอียดที่ 10 A 23 ก.ย. ฐานรากเสา (แบบที่ 23)	หน่วยเป็น ...มิลลิเมตร... มาตราส่วน ....1:30.....
รองผู้ว่าการวางแผนและพัฒนาระบบไฟฟ้า	DETAIL 10 A POLE FOUNDATION (TYPE 23)	แบบเลขที่ SA1–015/47026 แผ่นที่ .2. ของจำนวน .2. แผ่น

2[illegible] ก.ย. 2547