การประกอบเลขที่
ASSEMBLY NO. 5207

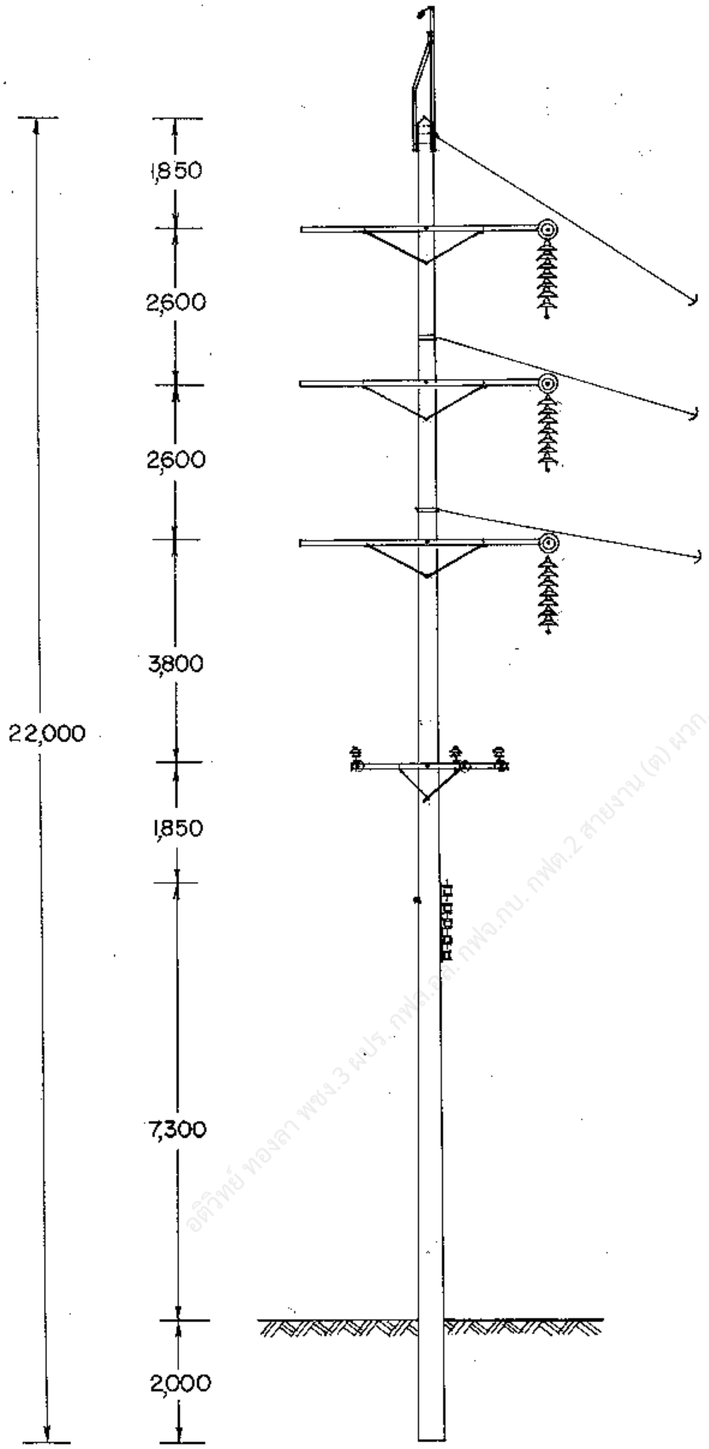

อดิศักดิ์ ทองลา พชง.3 ผปร. กฟส.[illegible] กฟจ.กบ. กฟต.2 สายงาน (ต) ผวก. @PEA

แบบ
TYPE SS-AS-3

JAPANESE EXPERT TO PEA. Y. Yamada

กองวิศวกรรม

ผู้เขียน
สถาปนิก
วิศวกร
หัวหน้าแผนก
ผู้อำนวยการกอง
รองผู้ว่าการฝ่ายเทคนิค

การไฟฟ้าส่วนภูมิภาค

ผู้ว่าการ 26 มิ.ย. 19

แบบโครงสร้างเสาส่งระบบ 115 kV
วงจรเดี่ยว
แบบเสาสำหรับทางโค้ง

115 kV LINE STRUCTURE CONSTRUCTION
SINGLE CIRCUIT
ANGLE STRUCTURE

ใช้แทนแบบ
ถูกแทนโดยแบบ
เขียนเสร็จวันที่ 17 มิ.ย. 19
แก้แบบวันที่ 24 มิ.ย. 23
มิติเป็น มม.
มาตราส่วน 1:125
แบบเลขที่ S02-015/19023
แผ่นที่ 1 ของจำนวน 4 แผ่น

การประกอบเลขที่ ASSEMBLY NO. 5207

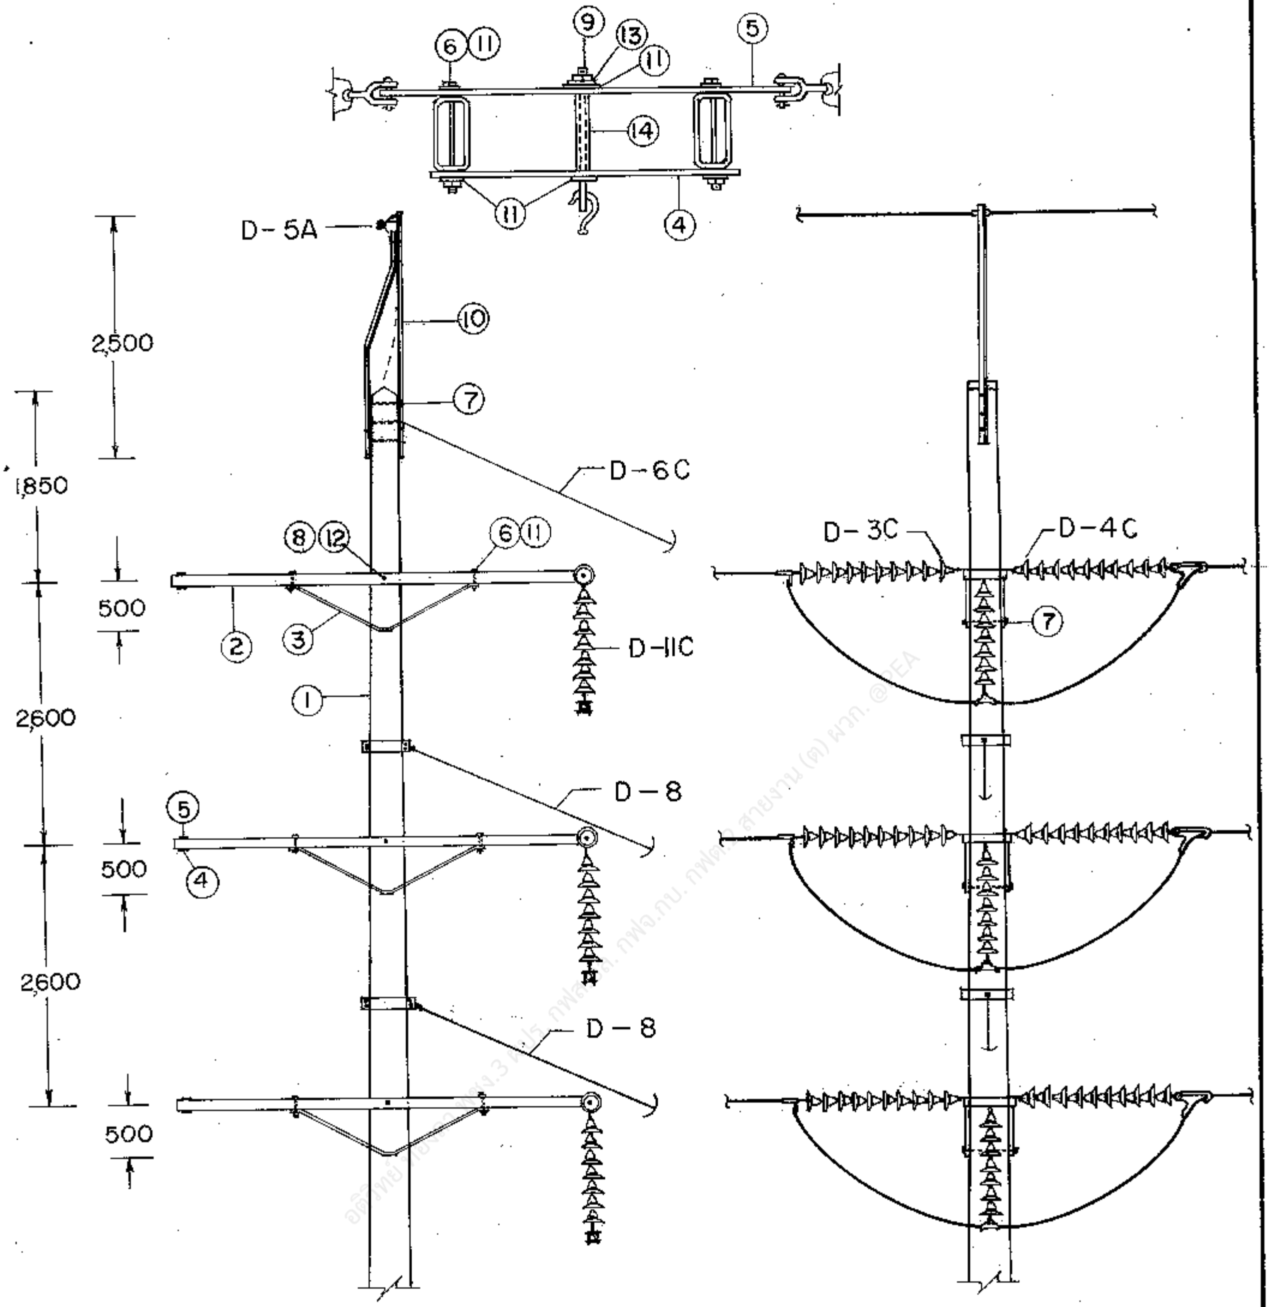

JAPANESE EXPERT TO PEA.

กองวิศวกรรม	การไฟฟ้าส่วนภูมิภาค	ใช้แทนแบบ..........
ผู้เขียน.......... สถาปนิก.......... วิศวกร.......... หัวหน้าแผนก.......... ผู้อำนวยการกอง..........	ผู้ว่าการ.......... 26 มี.ค. 19	ถูกแทนโดยแบบ.......... เขียนเสร็จวันที่ 17 มี.ค. 19 แก้แบบวันที่ 24 มี.ค. 23
	แบบโครงสร้างเสาส่งระบบ 115 kV. วงจรเดี่ยว แบบเสาสำหรับทางโค้ง	มิติเป็น มม. มาตราส่วน 1:75
รองผู้ว่าการฝ่ายเทคนิค	115 kV LINE STRUCTURE CONSTRUCTION SINGLE CIRCUIT ANGLE STRUCTURE	แบบเลขที่ S02-015/19023 แผ่นที่ 2 ของจำนวน 4 แผ่น

การประกอบเลขที่
ASSEMBLY NO. 5207

บัญชีวัสดุ
BILL OF MATERIAL

ลำดับที่ ITEM	รายละเอียด DESCRIPTION	จำนวน REQ D	วัสดุเลขที่ MAT. NO.
1	เสาคอนกรีต 22 ม. POLE, CONCRETE 22 m.LONG	1	00010011 (0041)
2	คอนสายแบบเหล็กขนาด 100x50x3.2 มม.ยาว 4.20 ม. CROSSARM, STEEL 100 x 50 x 3.2 mm. 4.20 m.LONG	6	00120001 (0116)
3	เหล็กฉากรับคอนสายขนาด 50x50x6 มม.ช่วงกว้าง 1800 มม. ตกลง 450 มม. BRACE, ANGLE STEEL 50x50x6 mm. 1800 mm WIDE 450 mm. DROP.	6	00120007 (1119)
4	เหล็กแผ่นขนาด 6 x 100 x 450 มม. PLATE, STEEL 6 x 100 x 450 mm.	6	01030002 (0143)
5	แผ่นเหล็กปีนสองผสานขนาด 12 x 100 x 650 มม. PLATE, STEEL, DOUBLE ARMING 12 x 100 x 650 mm.	6	01030100 (0415)
6	สลักเกลียว M 16x170 มม. BOLT, MACHINE M 16x170 mm.	24	01110201 (0221)
7	สลักเกลียว M 16 x 350 มม. BOLT, MACHINE M 16 x 350 mm.	5	01110205 (0225)
8	สลักเกลียว M 20x450 มม. BOLT, MACHINE M 20x 450 mm.	3	01110302 (0234)
9	สลักห่วงโอแวล M 16 x 150 มม. BOLT, OVAL EYE M 16 x 150 mm.	3	01150000 (0257)
10	เหล็กฉากรับสายล่อฟ้าทางโค้ง OVERHEAD GROUND WIRE CORNER BAYONET	1	01010005 (0136)
11	แหวนสี่เหลี่ยมแบน 52X52X4.5 มม. รู Ø 18 มม. มอก. 258 WASHER, SQUARE, FLAT 52X52X4.5 mm.HOLE Ø 18 mm. TIS. 258	42	01180100 (0355)
12	แหวนสี่เหลี่ยมโค้ง 62X62X6 มม. รู Ø 22 มม. WASHER, SQUARE, FLAT 62X62X6 mm.HOLE Ø 22 mm.	6	01180101 (0356)
13	แหวนสปริง M 16 มอก. 259 WASHER, LOCK, M 16, TIS 259	3	01180301 (0365)
14	ท่อเหล็ก ชื่อขนาด 20 มม. หนา 2.65 มม. ยาว 100 มม. มอก. 277 ประเภท 2 PIPE, IRON, DIA. 20 mm ID., 2.65 mm THICKNESS, 100 mm LONG TIS 227 TYPE 2	3	01050000 (0905)
	รายละเอียด DETAIL		
D-3C	การประกอบลูกถ้วยแขวน SUSPENSION INSULATOR ASSEMBLY	3	
D-4C	การประกอบลูกถ้วยแขวน SUSPENSION INSULATOR ASSEMBLY	3	
D-11C	การประกอบลูกถ้วยแขวน SUSPENSION INSULATOR ASSEMBLY	3	
D-5A	การต่อสายล่อฟ้า OVERHEAD GROUND WIRE CONNECTION	1	
D-6C	การประกอบสายยึดโยงลวดเหล็กตีเกลียว 50 ต.มม. STEEL STRANDED WIRE 50 mm^2 GUY ASSEMBLY	1	

กองวิศวกรรม	การไฟฟ้าส่วนภูมิภาค	ใช้แทนแบบ..........
ผู้เขียน........ สถาปนิก........ วิศวกร........ หัวหน้าแผนก........ ผู้อำนวยการกอง........	ผู้ว่าการ........ 26 มี.ค. 19	ถูกแทนโดยแบบ.......... เขียนเสร็จวันที่ 17 มี.ค.19 แก้แบบวันที่ 24 มิ.ย.23 มิติเป็น มม. มาตราส่วน..........
รองผู้ว่าการฝ่ายเทคนิค	แบบโครงสร้างเสาส่งระบบ 115 kV วงจรเดี่ยว แบบเสาสำหรับทางโค้ง	แบบเลขที่ SO2-015/19023
....	115 kV. LINE STRUCTURE CONSTRUCTION SINGLE CIRCUIT ANGLE STRUCTURE	แผ่นที่ 3 ของจำนวน 4 แผ่น

การประกอบเลขที่
ASSEMBLY NO. 5207

บัญชีวัสดุ
BILL OF MATERIAL

ลำดับที่ ITEM	รายละเอียด DESCRIPTION	จำนวน REQ'D	วัสดุเลขที่ MAT. NO.
	รายละเอียด DETAIL		
D-8	การประกอบสายยึดโยงด้านข้างลวดเหล็กตีเกลียว 95 ต.มม. STEEL STRANDED WIRE 95 mm^2 SIDE GUY ASSEMBLY	2	
D-9C	สมอบกคอนกรีต CONCRETE ANCHOR	1	
D-10A	ฐานรากเสา POLE FOUNDATION	1	

อดิวิทย์ ทองลา พชง.3 ผปร. กฟส.อล. กฟจ.กน. กฟต.2 สายงาน (ต) ผวก. @PEA

JAPANESE EXPERT TO PEA. Yamada

กองวิศวกรรม
ผู้เขียน
สถาปนิก
วิศวกร
หัวหน้าแผนก
ผู้อำนวยการกอง
รองผู้ว่าการฝ่ายเทคนิค

การไฟฟ้าส่วนภูมิภาค
ผู้ว่าการ

แบบโครงสร้างเสาส่งระบบ 115 kV
วงจรเดี่ยว
แบบเสาสำหรับทางโค้ง

115 kV LINE STRUCTURE CONSTRUCTION
SINGLE CIRCUIT
ANGLE STRUCTURE

ใช้แทนแบบ
ถูกแทนโดยแบบ
เขียนเสร็จวันที่ 17 มี.ค. 19
แก้แบบวันที่ 24 มี.ค. 23
มิติเป็น
มาตราส่วน
แบบเลขที่ S02-015/19023
แผ่นที่ 4 ของจำนวน 4 แผ่น