การประกอบเลขที่
ASSEMBLY NO. **5354**

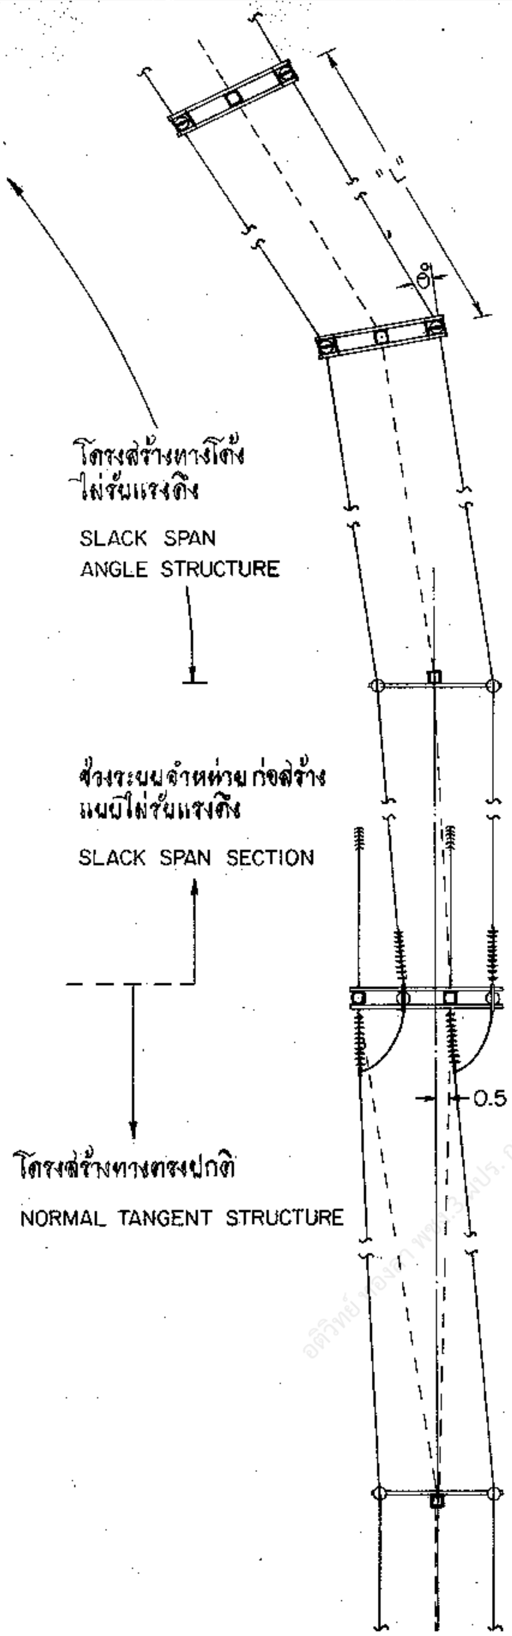

ข้อกำหนด ระยะห่างระหว่างช่วงเสาของโครงสร้าง สายส่ง 115 kV ดูรายละเอียดตามแบบเลขที่ IBI—015/24009 (การประกอบเลขที่ 5151)

THE REGULATION OF SPAN LENGTHS FOR 115 kV CONSTRUCTION STRUCTURE SEE DETAIL IN DRAWING NO. IBI—015/24009 (ASSEMBLY NO. 5151)

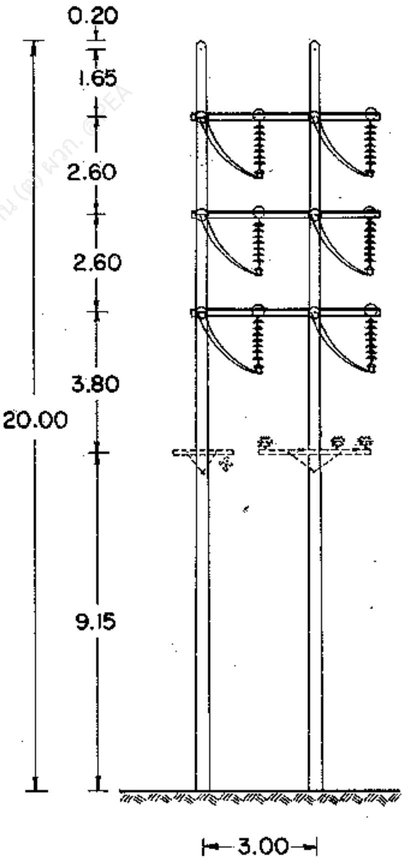

กองวิศวกรรมไฟฟ้าและเครื่องกล
ฝ่ายวิศวกรรม

ผู้เขียน
ผู้สำรวจ
วิศวกร
หัวหน้าแผนก
ผู้อำนวยการกอง
ผู้อำนวยการฝ่าย

รองผู้ว่าการฝ่ายเทคนิค

28 มิ.ย. 2525

การไฟฟ้าส่วนภูมิภาค

ผู้ว่าการ 28 พ.ค. 25

115 kV วงจรคู่ สายไฟฟ้าคู่
โครงสร้างเข้าปลายสายสองข้าง แบบเสาคู่
แบบ DD—DD—1

115 kV DOUBLE CIRCUIT DOUBLE CONDUCTOR
DOUBLE POLE; DOUBLE DEAD END STRUCTURE
TYPE DD—DD—1

ใช้แทนแบบ
ถูกแทนโดยแบบ
เขียนเสร็จวันที่ 29 มี.ค. 25
แก้แบบวันที่ 26 ต.ค. 32
มิติเป็น เมตร
มาตราส่วน 1:200, 1:250

แบบเลขที่ SAI—015/25005
แผ่นที่ 1 ของจำนวน 5 แผ่น

การประกอบเลขที่ 5354
ASSEMBLY NO.

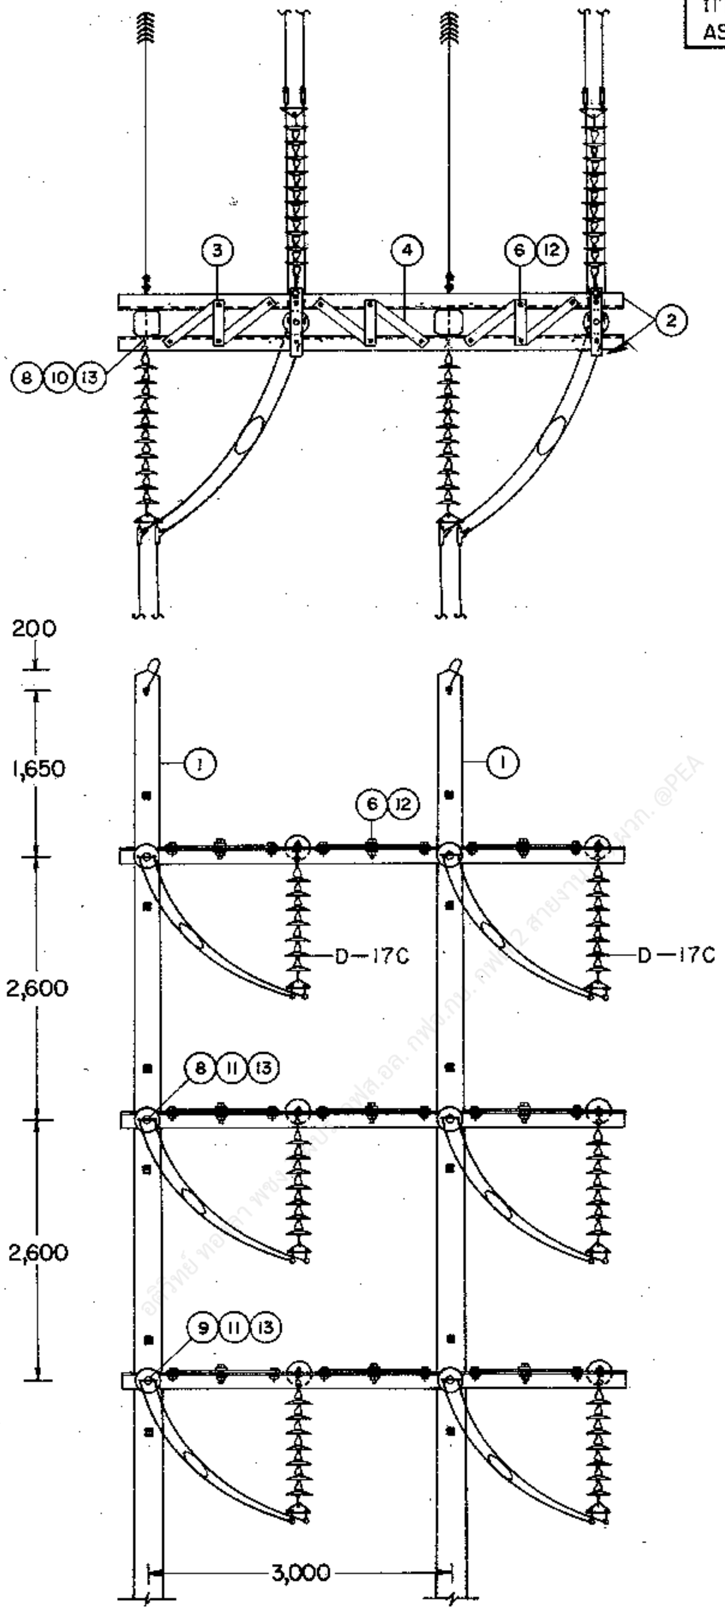

กองวิศวกรรมไฟฟ้าและเครื่องกล ฝ่ายวิศวกรรม	การไฟฟ้าส่วนภูมิภาค	ใช้แทนแบบ.......... ถูกแทนโดยแบบ..........
ผู้เขียน.......... ผู้ตรวจ.......... วิศวกร.......... หัวหน้าแผนก.......... ผู้อำนวยการกอง.......... ผู้อำนวยการฝ่าย..........	ผู้ว่าการ.......... 28 พ.ค. 25	เขียนเสร็จวันที่ 29 มี.ค. 25 แก้แบบวันที่ 26 ต.ค. 32 คิดเป็น มม. มาตราส่วน 1 : 75
	115 kV วงจรคู่ สายไฟฟ้าคู่ โครงสร้างเข้าปลายสายสองข้าง แบบเสาคู่ แบบ DD—DD—1	
รองผู้ว่าการฝ่ายเทคนิค	115 kV DOUBLE CIRCUIT DOUBLE CONDUCTOR DOUBLE POLE, DOUBLE DEAD END STRUCTURE TYPE DD—DD—1	แบบเลขที่ SAI—015/25005 แผ่นที่ 2 ของจำนวน 5 แผ่น

28 พ.ค. 2525

การประกอบเลขที่ ASSEMBLY NO.	5354

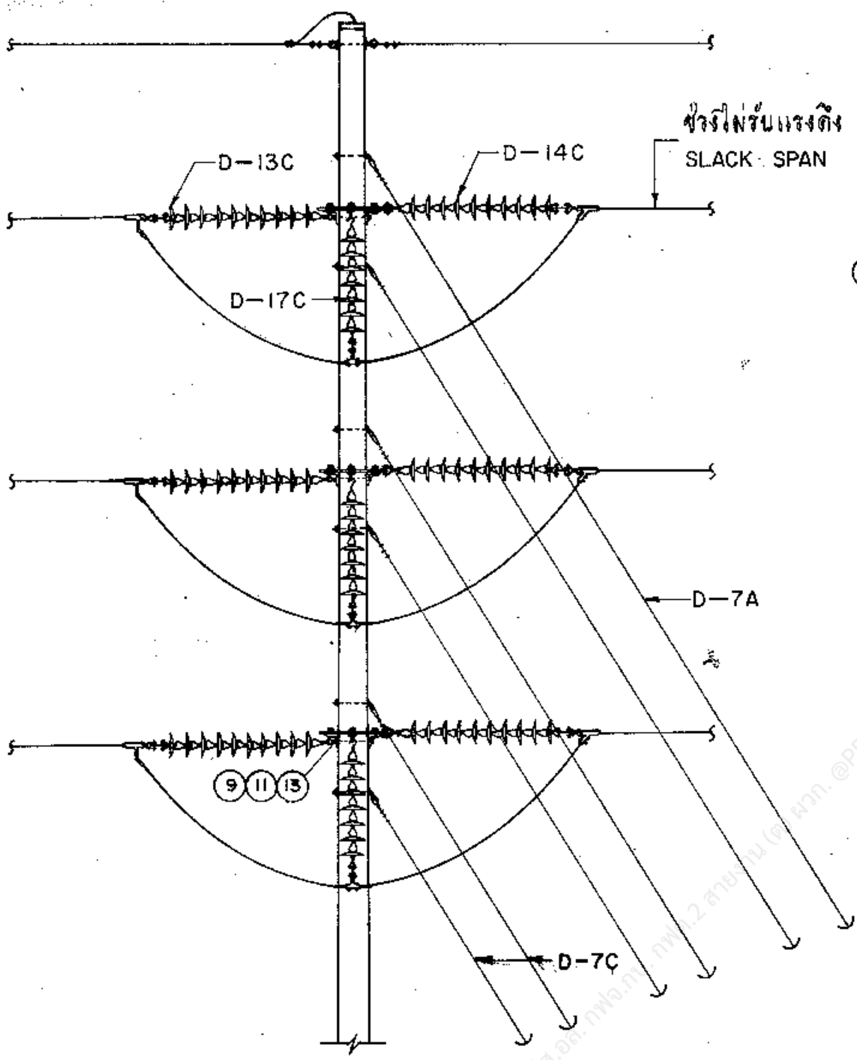

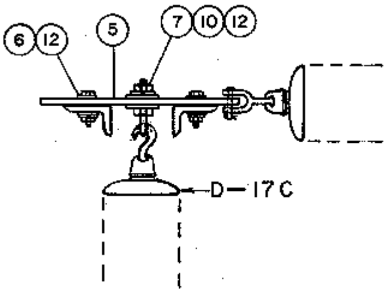

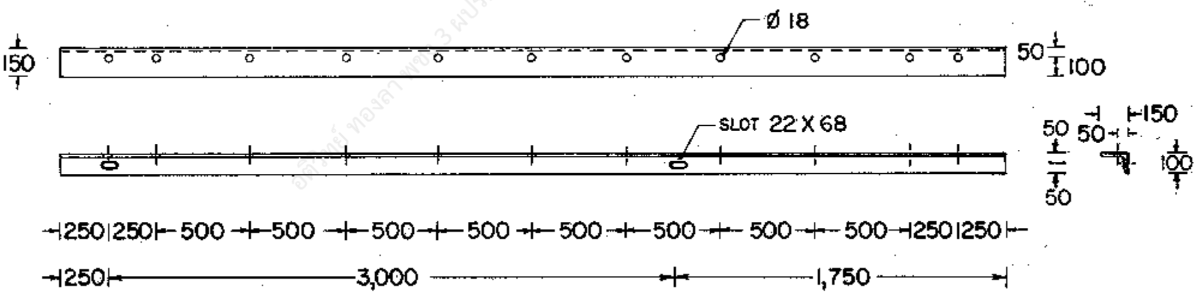

L 150 X 100 X 12 mm 5,000 LONG

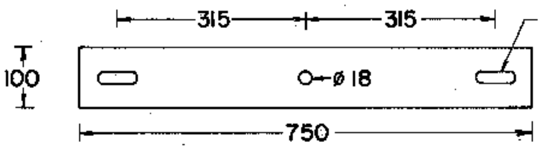

STEEL PLATE 6 X 100 X 750 mm

กองวิศวกรรมไฟฟ้าและเครื่องกล ฝ่ายวิศวกรรม	การไฟฟ้าส่วนภูมิภาค	ใช้แทนแบบ ถูกแทนโดยแบบ
ผู้เขียน ผู้สำรวจ วิศวกร หัวหน้าแผนก ผู้อำนวยการกอง ผู้อำนวยการฝ่าย	ผู้ว่าการ 28 พ.ค.25 115 kV วงจรคู่ สายไฟฟ้าคู่ โครงสร้างเข้าปลายสายสองข้าง แบบเสาคู่ แบบ DD—DD—1	เขียนเสร็จวันที่ 29 มี.ค.25 แก้แบบวันที่ 26 ต.ค.32 15 ก.ย.40 มิติเป็น มม. มาตราส่วน 1:12.5, 1:40, 1:75
รองผู้ว่าการฝ่ายเทคนิค	115 kV DOUBLE CIRCUIT, DOUBLE CONDUCTOR DOUBLE POLE, DOUBLE DEAD END STRUCTURE TYPE DD—DD—1	แบบเลขที่ SAI—015/25005 แผ่นที่ 3 ของจำนวน 5 แผ่น

2 8 พ.ค. 2525

การประกอบเลขที่
ASSEMBLY NO. 5354

บัญชีวัสดุ
BILL OF MATERIAL

ลำดับที่ ITEM	รายละเอียด DESCRIPTION	จำนวน REQ'D	วัสดุเลขที่ MAT. NO.
1	เสาคอนกรีต 22 ม. POLE, CONCRETE 22 m LONG	2	00010011 (0041)
2	คอนสายแบบเหล็กฉาก ขนาด 150 X 100 X 12 มม. ยาว 5.00 ม. CROSSARM, STEEL ANGLE 150 X 100 X 12 mm 5.00 m LONG	6	00120003 (6002)
3	เหล็กแผ่น ขนาด 6 X 100 X 450 มม. PLATE, STEEL 6 X 100 X 450 mm	9	01030002 (0143)
4	เหล็กแผ่น ขนาด 6 X 100 X 750 มม. PLATE, STEEL 6 X 100 X 750 mm	18	01030004 (6005)
5	แผ่นเหล็กยึดสองปลาย ขนาด 12 X 100 X 650 มม. PLATE, STEEL, DOUBLE ARMING 12 X 100 X 650 mm	6	01030100 (0145)
6	สลักเกลียว M 16 X 75 มม. พร้อมแหวนกลม 2 อัน BOLT, MACHINE M 16 X 75 mm COMPLETE WITH 2 ROUND WASHERS	48	01110400 (0236)
7	สลักห่วงโอแวล M 16 X 150 มม. (เพิ่มน๊ตอีกหนึ่งอัน) BOLT, OVAL EYE M 16 X 150 mm (ADD ONE SQUARE NUT)	6	01150000 (0257)
8	สลักห่วงโอแวล M 20 X 350 มม. BOLT, OVAL EYE M 20 X 350 mm	4	01150100 (0260)
9	สลักห่วงโอแวล M 20 X 450 มม. BOLT, OVAL EYE M 20 X 450 mm	2	01150101 (0261)
10	แหวนสี่เหลี่ยมแบน 52X52X4.5 มม. รู Ø 18 มม. มอก. 258 WASHER, SQUARE, FLAT 52X52X4.5 mm HOLE Ø 18 mm, TIS 258	12	01180100 (0355)
11	แหวนสี่เหลี่ยมแบน 62 X 62 X 6 มม. รู Ø 22 มม. มอก. 258 WASHER, SQUARE, FLAT 62 X 62 X 6 mm HOLE Ø 22 mm, TIS 258	12	01180101 (0356)
12	แหวนสปริง M 16 มอก. 259 WASHER, LOCK, M 16, TIS 259	54	01180301 (0365)
13	แหวนสปริง M 20 มอก. 259 WASHER, LOCK, M 20, TIS 259	6	01180302 (0366)
14	ปรีฟอร์มแยกสาย SPACER, HELICAL ROD, PREFORMED	12	02240000 (0918)

กองวิศวกรรมไฟฟ้าและเครื่องกล
ฝ่ายวิศวกรรม

ผู้เขียน
ผู้สำรวจ
วิศวกร ชัยรัตน์
หัวหน้าแผนก ชัยรัตน์
ผู้อำนวยการกอง
ผู้อำนวยการฝ่าย
รองผู้ว่าการฝ่ายเทคนิค

การไฟฟ้าส่วนภูมิภาค

ผู้ว่าการ ๒๘ พ.ค.๒๕

115 kV วงจรคู่ สายไฟฟ้าคู่
โครงสร้างเข้าปลายสายสองข้าง แบบเสาคู่
แบบ DD—DD—1

115 kV DOUBLE CIRCUIT, DOUBLE CONDUCTOR
DOUBLE POLE, DOUBLE DEAD END STRUCTURE
TYPE DD—DD—1

ใช้แทนแบบ
ถูกแทนโดยแบบ
เขียนเสร็จวันที่ 29 พ.ค.25
แก้แบบวันที่ 26 ต.ค.32
มิติเป็น
มาตราส่วน
แบบเลขที่ SAI—015/25005
แผ่นที่ 4 ของจำนวน 5 แผ่น

28 พ.ค. 2525

การประกอบเลขที่ ASSEMBLY NO. **5354**

	รายละเอียด DETAIL		
D-13C	การประกอบลูกถ้วยแขวน SUSPENSION INSULATOR ASSEMBLY	6	
D-14C	การประกอบลูกถ้วยแขวน SUSPENSION INSULATOR ASSEMBLY	6	
D-17C	การประกอบลูกถ้วยแขวน SUSPENSION INSULATOR ASSEMBLY	6	
D-5E	การต่อสายล่อฟ้า OVERHEAD GROUND WIRE CONNECTION	2	
D-7A	การประกอบสายยึดโยงลวดเหล็กตีเกลียว 95 ต.มม. STEEL STRANDED WIRE 95 mm^2 GUY ASSEMBLY	8	
D-7C	**การประกอบสายยึดโยงลวดเหล็กตีเกลียว 95 ต.มม.** **STEEL STRANDED WIRE 95 mm^2 GUY ASSEMBLY**	4	
D-9B	**สมอบกคอนกรีต ตามแบบเลขที่ IBI-015/240027 (การประกอบเลขที่ 5652)** **CONCRETE ANCHOR ACCORDING TO DWG. NO. IBI-015/240027 (ASS. NO. 5652)**	2	
D-10A	**ฐานรากเสา ตามแบบเลขที่ IBI-015/240025 (การประกอบเลขที่ 5568) *** **POLE FOUNDATION ACCORDING IBI-015/240025 (ASS. NO. 5568)**	2	

* **ฐานรากเสา คอร. 22 ม. ใช้เฉพาะกรณีทางโค้งที่มีสายยึดโยง รายละเอียดเพิ่มเติมตามแบบเลขที่**
IBI-017/240011 (การประกอบเลขที่ 5908)

อดิวิทย์ ทองลา พชง.3 ผปร. กฟส.อล. กฟจ.กบ. กฟต.2 สายงาน (ต) ผวก. @PEA

กองวิศวกรรมไฟฟ้าและเครื่องกล ฝ่ายวิศวกรรม	การไฟฟ้าส่วนภูมิภาค	ใช้แทนแบบ.......... ถูกแทนโดยแบบ..........
ผู้เขียน .... ผู้สำรวจ .... วิศวกร .... หัวหน้าแผนก .... ผู้อำนวยการกอง .... ผู้อำนวยการฝ่าย	ผู้ว่าการ .... 28 พ.ค. 25 115 kV วงจรคู่ สายไฟฟ้าคู่ โครงสร้างเข้าปลายสายสองข้าง แบบเสาคู่ แบบ DD-DD-1	เขียนเสร็จวันที่ 29 มี.ค.25 แก้แบบวันที่ 26 ต.ค.32 15 ก.ย.40 ผลิตเป็น.......... มาตราส่วน..........
รองผู้ว่าการฝ่ายเทคนิค	115 kV DOUBLE CIRCUIT, DOUBLE CONDUCTOR DOUBLE POLE, DOUBLE DEAD END STRUCTURE TYPE DD-DD-1	แบบเลขที่ SAI-015/25005 แผ่นที่ 5 ของจำนวน 5 แผ่น

28 พ.ค. 2525