การประกอบเลขที่ 5217
ASSEMBLY NO.

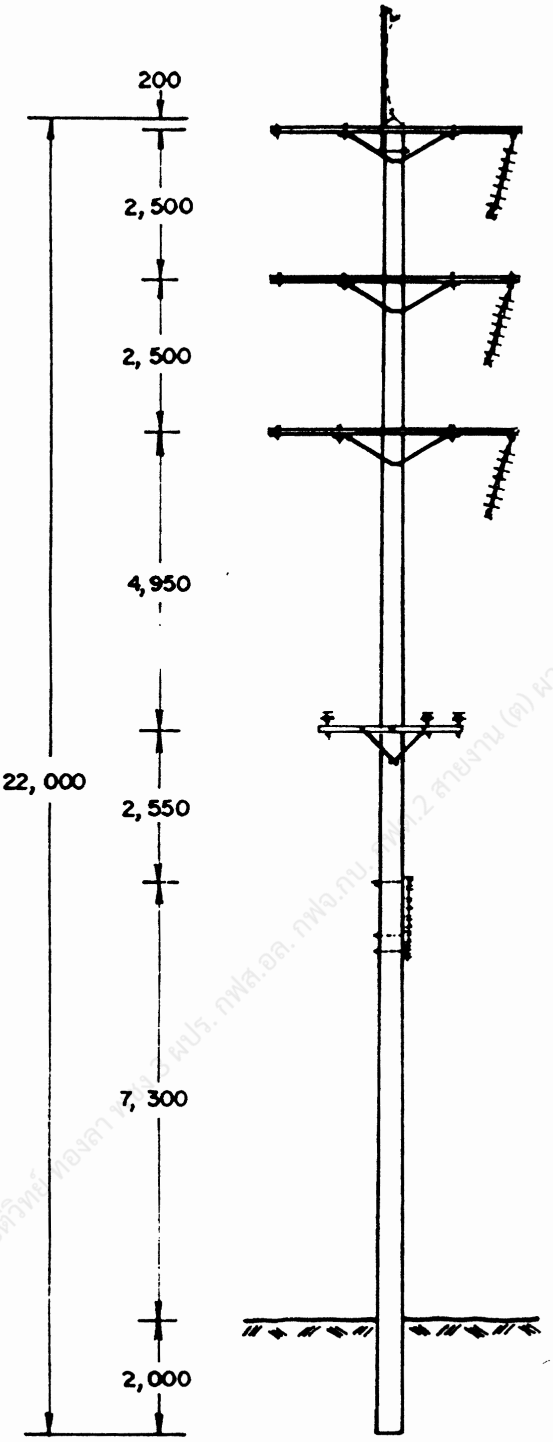

อดิวิทย์ ทองลา ... ผบร. กฟส.อล. กฟจ.กน. ... 2 สายงาน (ต) ผวก. @PEA

กองวิศวกรรมไฟฟ้าและเครื่องกล
ฝ่ายวิศวกรรม

ผู้เขียน
ผู้สำรวจ
วิศวกร
หัวหน้าแผนก
ผู้อำนวยการกอง
ผู้อำนวยการฝ่าย

รองผู้ว่าการฝ่ายเทคนิค

การไฟฟ้าส่วนภูมิภาค

ผู้ว่าการ

115 kV วงจรเดี่ยว สายไฟฟ้าเดี่ยว
เสาต้นทางตรง ก่อนเสาต้นเข้าปลายสาย
แบบ SS-TG-4

115kV SINGLE CIRCUIT SINGLE CONDUCTOR
TANGENT STRUCTURE ADJACENT TO DEADEND POLE
TYPE SS-TG-4

ใช้แทนแบบ
ถูกแทนโดยแบบ
เขียนเสร็จวันที่ 15 ธค.2536
แก้แบบวันที่ 27 กค.38
มิติเป็น มิลลิเมตร
มาตราส่วน 1 : 125

แบบเลขที่ SAI-015/36008
แผ่นที่ 1 จากจำนวน 3 แผ่น

การประกอบเลขที่ 5217
ASSEMBLY NO.

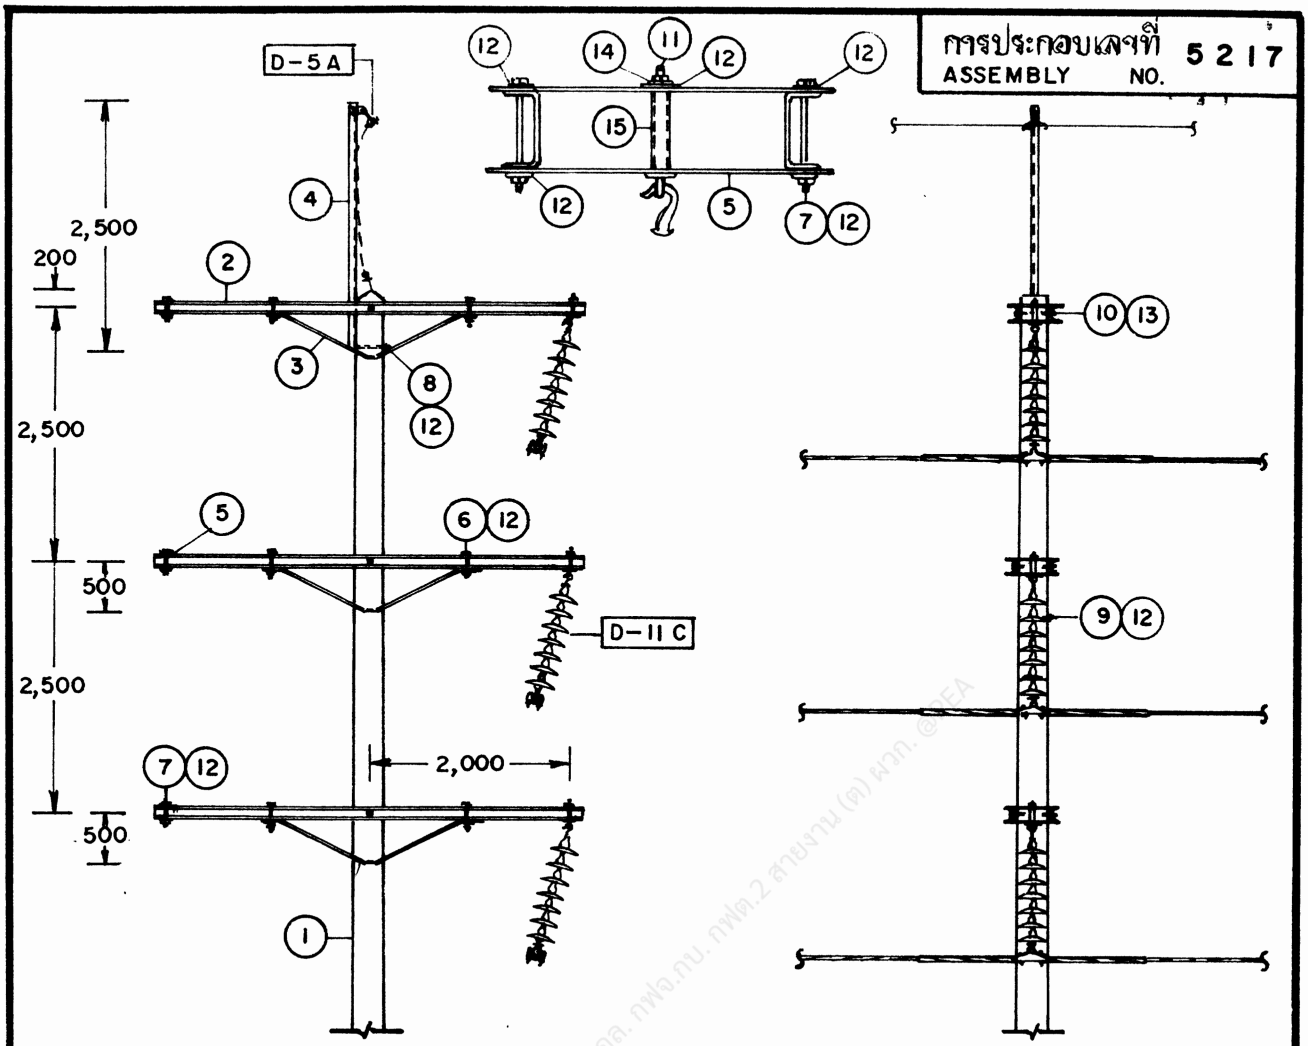
D-5A
2,500
200
2,500
500
2,500
500
2,000
D-11 C
① ② ③ ④ ⑤ ⑥ ⑦ ⑧ ⑨ ⑩ ⑪ ⑫ ⑬ ⑭ ⑮

SS-TG-4

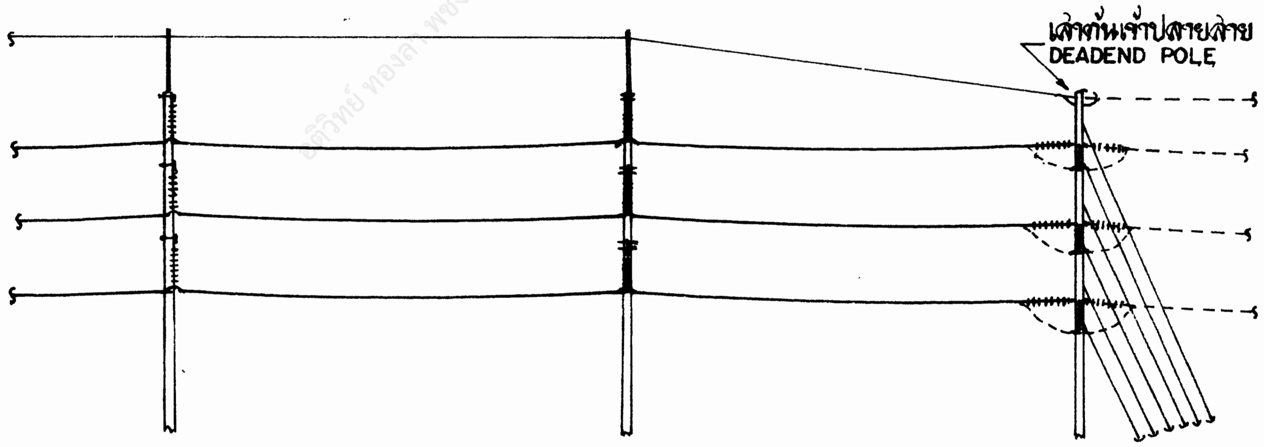
เสาต้นเจ้าปลายสาย
DEADEND POLE

SS-TG-1 **SS-TG-4**

กองวิศวกรรมไฟฟ้าและเครื่องกล ฝ่ายวิศวกรรม	**การไฟฟ้าส่วนภูมิภาค**	ใช้แทนแบบ ถูกแทนโดยแบบ เขียนเสร็จวันที่ 15 ธค. 2536 แก้แบบวันที่ 27 ก.ค. 38 มิติเป็น มิลลิเมตร มาตราส่วน 1 : 75
ผู้เขียน สพพ๑. ผู้ตรวจ วิศวกร หัวหน้าแผนก ผู้อำนวยการกอง ผู้อำนวยการฝ่าย	ผู้ว่าการ 115 kV วงจรเดี่ยว สายไฟฟ้าเดี่ยว เสาต้นทางตรง ก่อนเสาต้นเจ้าปลายสาย แบบ SS-TG-4	
รองผู้ว่าการฝ่ายเทคนิค	115 kV SINGLE CIRCUIT SINGLE CONDUCTOR TANGENT STRUCTURE ADJACENT TO DEADEND POLE TYPE SS-TG-4	แบบเลขที่ SAI-015/36008 แผ่นที่ 2 ของจำนวน 3 แผ่น

การประกอบเลขที่ ASSEMBLY NO. 5217

บัญชีพัสดุ
BILL OF MATERIAL

ลำดับที่ ITEM	รายละเอียด DESCRIPTION	จำนวน REQ'D	พัสดุเลขที่ MAT. NO.
1	เสาคอนกรีต 22 ม. POLE, CONCRETE 22 m LONG	1	00010011 (0041)
2	คอนสายแบบเหล็กรูปรางน้ำ ขนาด 100X50X5 มม. ยาว 4.20 ม. มอก. 116 CROSSARM, STEEL, CHANNEL 100X50X5 mm 4.20 m LONG TIS 116	6	
3	เหล็กฉากรับคอนสาย ขนาด 50X50X6 มม. ช่วงกว้าง 1,800 มม. ดรอพ 450มม. BRACE, ANGLE STEEL, 50X50X6 mm, 1,800 mm WIDE, 450 mm DROP	6	00120007 (0119)
4	เหล็กฉากรับสายล่อฟ้าทางตรง ยาว 2.50 ม. OVERHEAD GROUND WIRE BAYONET, 2.50 m LONG	1	01010004 (0135)
5	เหล็กแผ่น ขนาด 6X100X450 มม. PLATE, STEEL, 6X100X450 mm	12	01030002 (0143)
6	สลักเกลียว M 16X130 มม. BOLT, MACHINE, M 16X130 mm	12	01110200 (0220)
7	สลักเกลียว M 16X170 มม. BOLT, MACHINE, M 16X170 mm	12	01110201 (0221)
8	สลักเกลียว M 16X300 มม. BOLT, MACHINE, M 16X300 mm	3	01110204 (0224)
9	สลักเกลียว M 16X350 มม. BOLT, MACHINE, M 16X350 mm	2	01110205 (0225)
10	สลักเกลียว M 20X350 มม. BOLT, MACHINE, M 20X350 mm	3	01110300
11	สลักห่วงโอแวล M 16X150 มม. BOLT, OVAL EYE, M 16X150 mm	3	01150000 (0257)
12	แหวนสี่เหลี่ยมแบน 52X52X4.5 มม. รู ø 18 มม. มอก. 258 WASHER, SQUARE, FLAT 52X52X4.5 mm, HOLE ø 18 mm, TIS 258	47	01180100 (0355)
13	แหวนสี่เหลี่ยมแบน 62X62X6 มม. รู ø 22 มม. มอก. 258 WASHER, SQUARE, FLAT 62X62X6 mm, HOLE ø 22 mm, TIS 258	6	01180101 (0356)
14	แหวนสปริง M 16 มอก. 259 WASHER, LOCK, M 16, TIS 259	3	01180301 (0365)
15	ท่อเหล็ก ชื่อขนาด 20 มม. หนา 2.65 มม. ยาว 100 มม. มอก. 277 ประเภท 2 PIPE, IRON, DIA. 20 mm I.D., 2.65 mm THICKNESS, 100 mm LONG, TIS 277, TYPE 2	3	01050000 (0905)
D-11C	การประกอบลูกถ้วยแขวน SUSPENSION INSULATOR ASSEMBLY	3	
D-5A	การต่อสายล่อฟ้า OVERHEAD GROUND WIRE CONNECTION	1	
D-10A	ฐานรากเสา POLE FOUNDATION	1	

กองวิศวกรรมไฟฟ้าและเครื่องกล
ฝ่ายวิศวกรรม

ผู้เขียน [illegible]
ผู้สำรวจ
วิศวกร [illegible]
หัวหน้าแผนก [illegible]
ผู้อำนวยการกอง
ผู้อำนวยการฝ่าย

รองผู้ว่าการฝ่ายเทคนิค [illegible]

การไฟฟ้าส่วนภูมิภาค

ผู้ว่าการ

5 มี.ค. [illegible]

115 kV วงจรเดี่ยว สายไฟฟ้าเดี่ยว
เสาต้นทางตรง ก่อนเสาต้นเข้าปลายสาย
แบบ SS-TG-4

115 kV SINGLE CIRCUIT SINGLE CONDUCTOR
TANGENT STRUCTURE ADJACENT TO DEADEND POLE
TYPE SS-TG-4

ใช้แทนแบบ
ถูกแทนโดยแบบ
เขียนเสร็จวันที่ 15 ธค. 2536
แก้แบบวันที่ 27 ก.ค. 38
ผลิตเป็น
มาตราส่วน

แบบเลขที่ SAI-015/36008
แผ่นที่ 3 ของจำนวน 3 แผ่น