การประกอบเลขที่ ASSEMBLY NO. **3701 D**

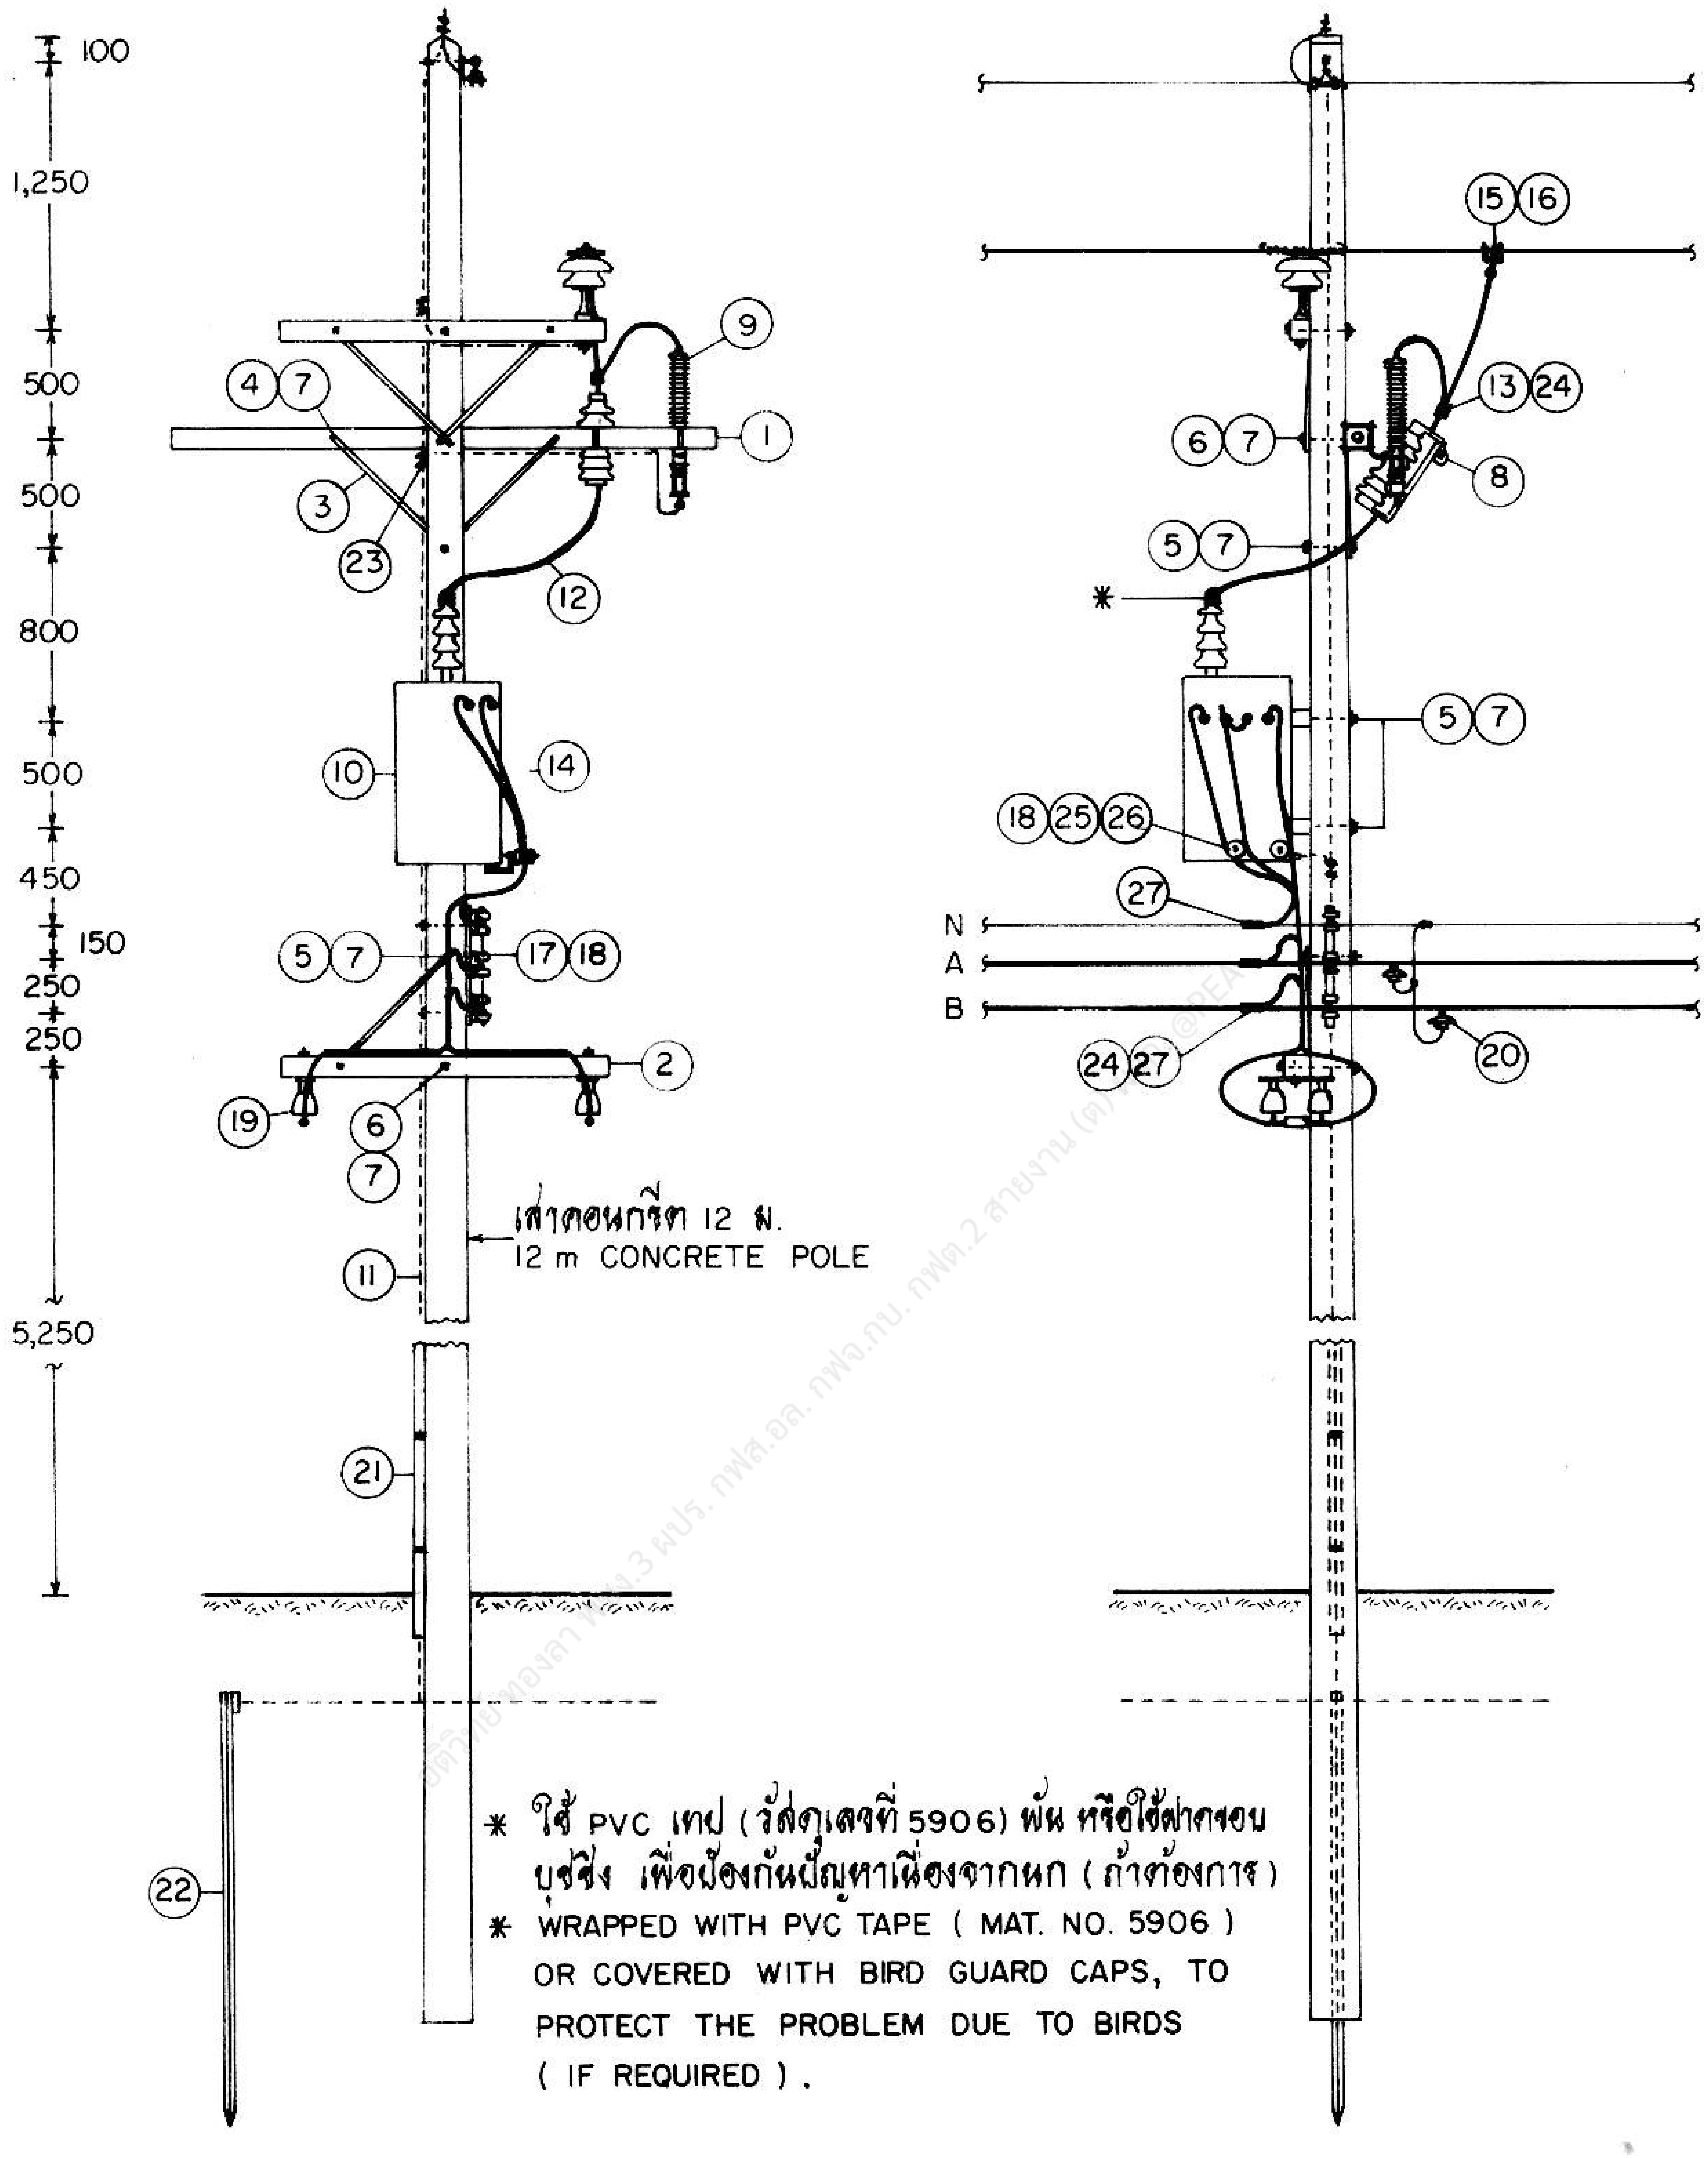

* ใช้ PVC เทป (วัสดุเลขที่ 5906) พัน หรือใช้ฝาครอบบุชชิ่ง เพื่อป้องกันปัญหาเนื่องจากนก (ถ้าต้องการ)

* WRAPPED WITH PVC TAPE (MAT. NO. 5906) OR COVERED WITH BIRD GUARD CAPS, TO PROTECT THE PROBLEM DUE TO BIRDS (IF REQUIRED).

กองวิศวกรรมไฟฟ้าและเครื่องกล
ฝ่ายวิศวกรรม

ผู้เขียน
ผู้สำรวจ
วิศวกร
หัวหน้าแผนก
ผู้อำนวยการกอง
ผู้อำนวยการฝ่าย
รองผู้ว่าการฝ่ายเทคนิค

การไฟฟ้าส่วนภูมิภาค

ผู้ว่าการ 9 เม.ย. 34

การติดตั้งหม้อแปลงซิงเกิลบุชชิ่ง 19 kV ในสายระบบจำหน่าย 1 เฟส 19 kV

19 kV SINGLE BUSHING TRANSFORMER INSTALLATION ON 1-PHASE 19 kV DISTRIBUTION LINE

ใช้แทนแบบ
ถูกแทนโดยแบบ
เขียนเสร็จวันที่ 26 มี.ค. 34
แก้แบบวันที่ 4 ก.ย. 35
มิติเป็น มิลลิเมตร
มาตราส่วน 1 : 50

แบบเลขที่ SAI-015/34009
แผ่นที่ 1 ของจำนวน 4 แผ่น

18 มิ.ย. 2534

การประกอบเลขที่
ASSEMBLY NO. 3701 D

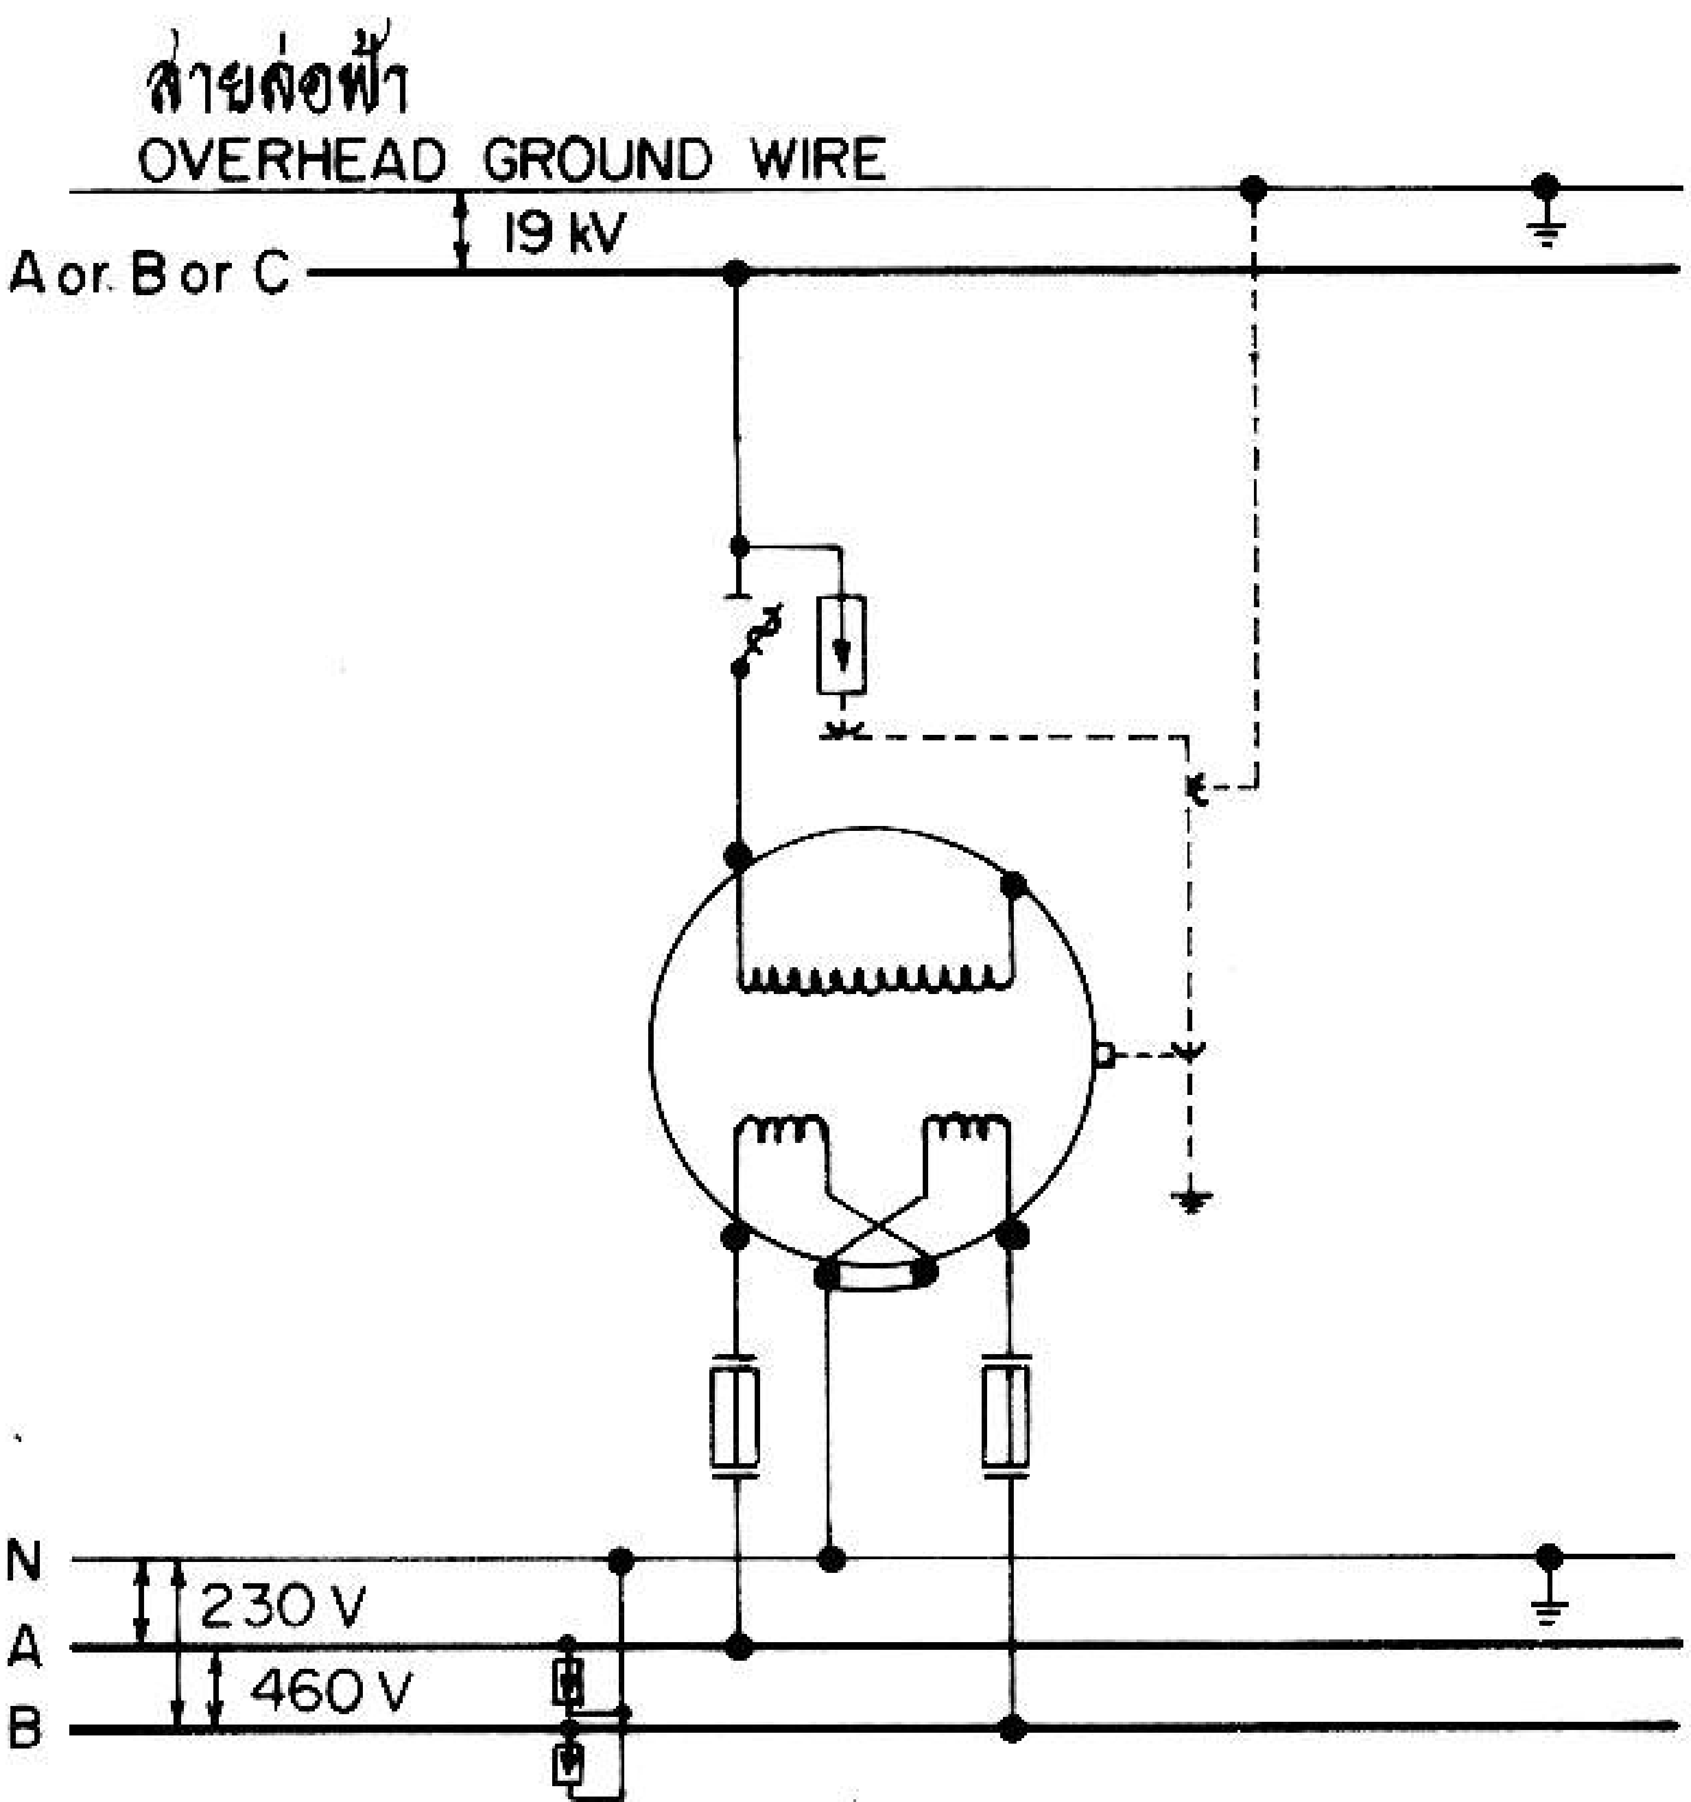

ไดอะแกรมแสดงการต่อหม้อแปลง 1 เฟส 3 สาย
1-PHASE 3-WIRE TRANSFORMER WIRING DIAGRAM

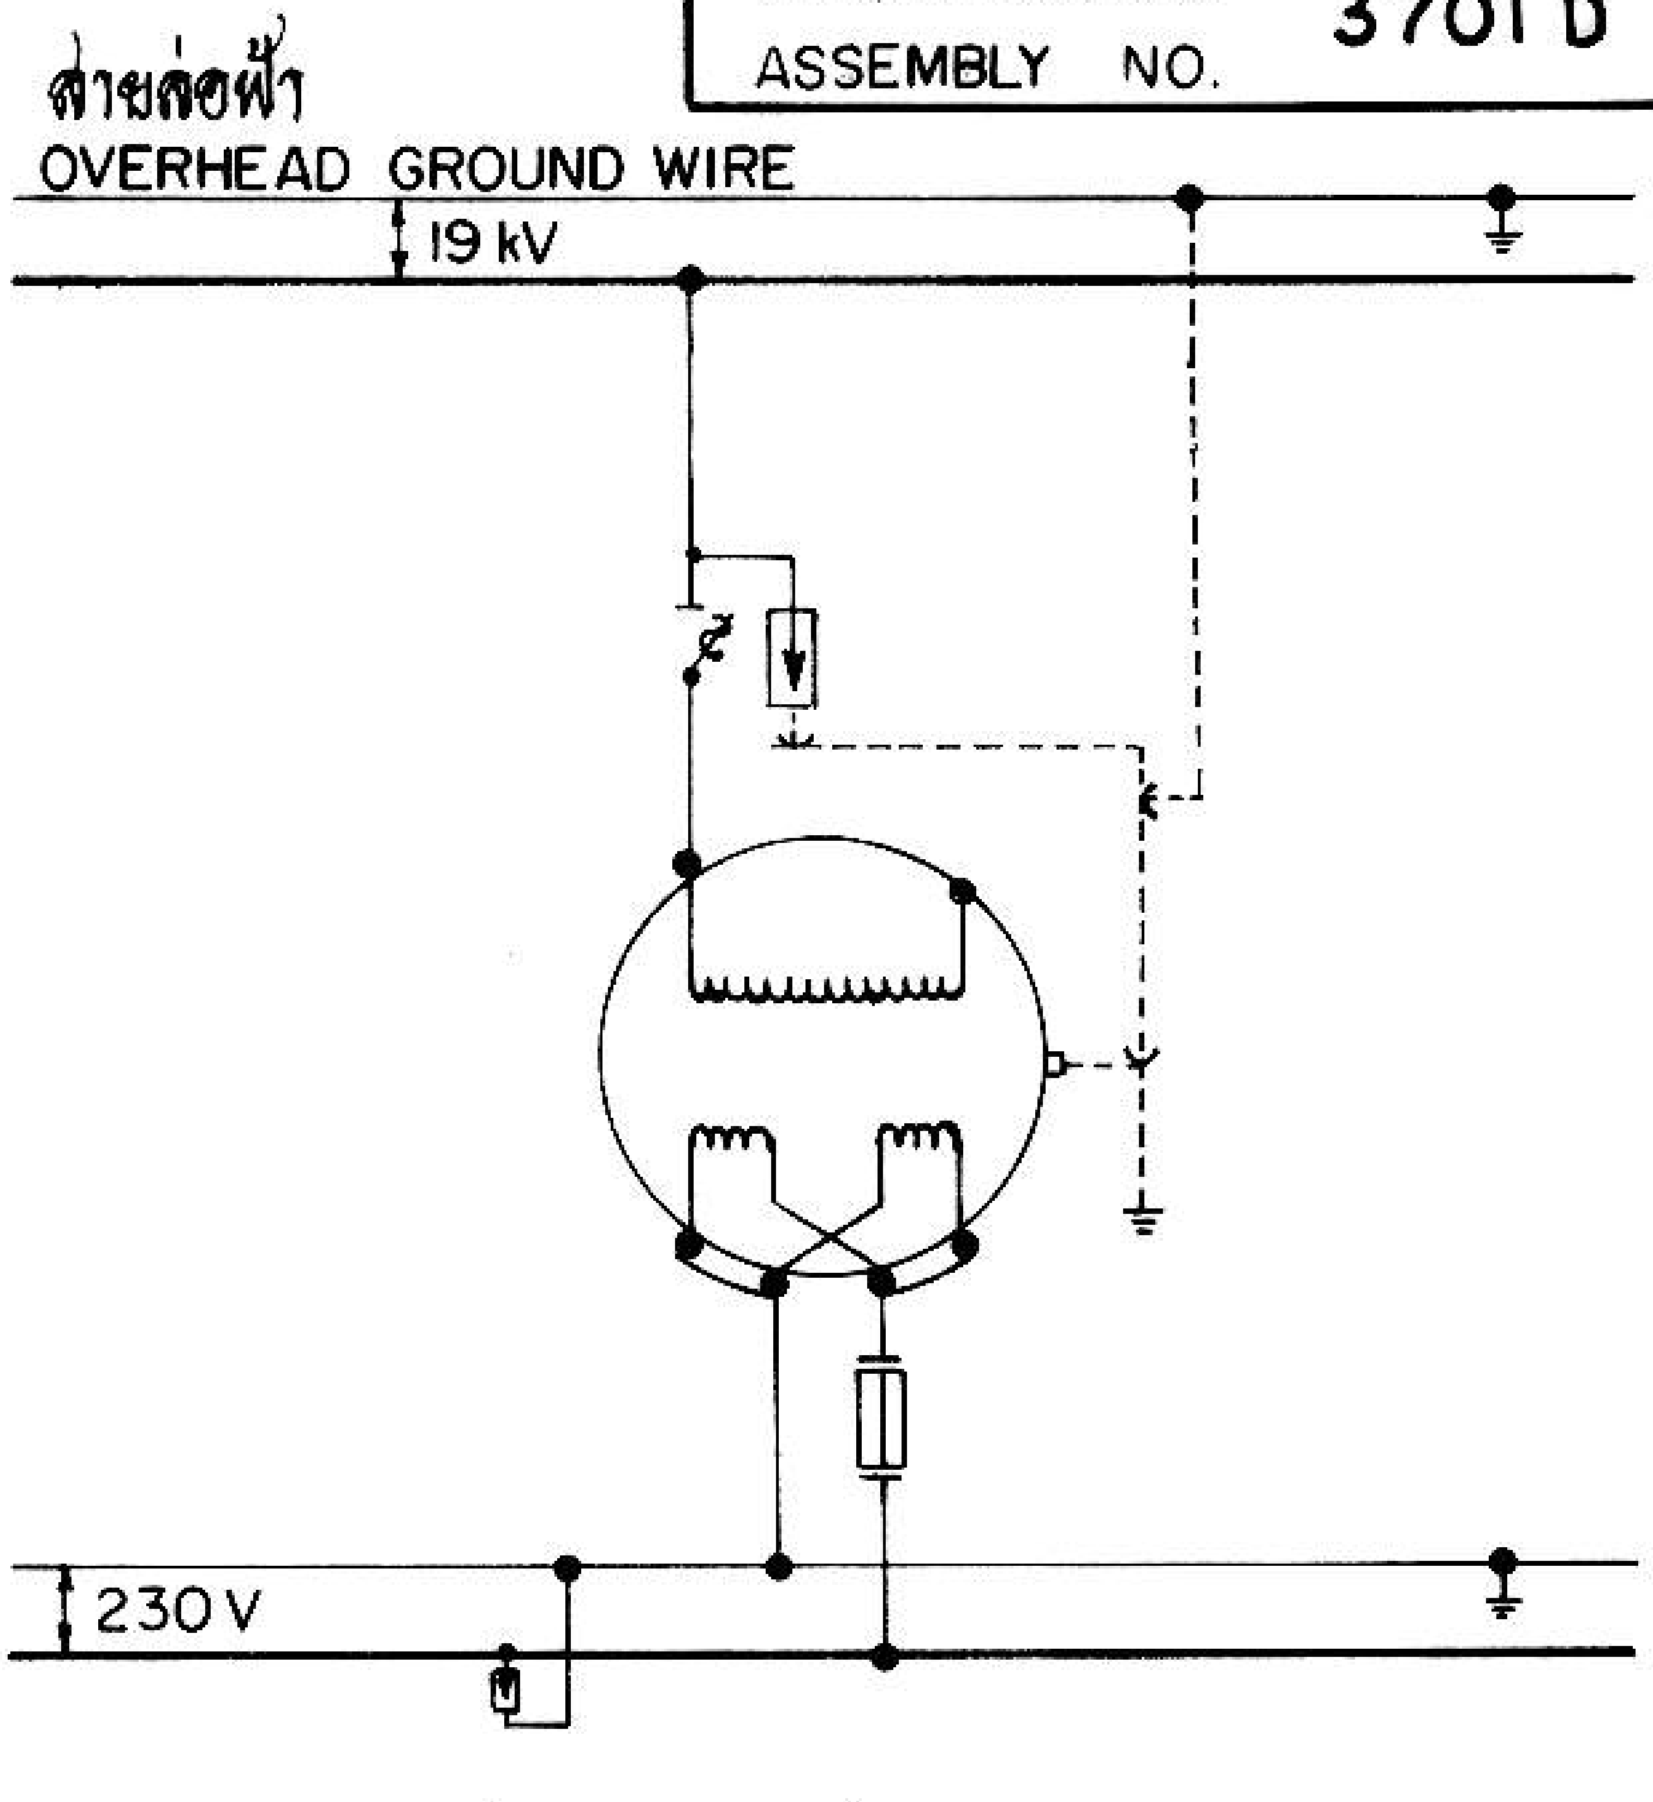

ไดอะแกรมแสดงการต่อหม้อแปลง 1 เฟส 2 สาย
1-PHASE 2-WIRE TRANSFORMER WIRING DIAGRAM

บัญชีวัสดุ
BILL OF MATERIAL

ลำดับที่ ITEM	รายละเอียด DESCRIPTION	จำนวน REQ'D	วัสดุเลขที่ MAT. NO.
1	คอน คอร. สปัน ขนาด 100 X 100 X 2,500 มม. CROSSARM, PRESTRESSED CONCRETE, SPUN, 100 X 100 X 2,500 mm	1	00110001
2	คอน คอร. ขนาด 100 X 100 X 1,500 มม. CROSSARM, PRESTRESSED CONCRETE, 100 X 100 X 1,500 mm	1	00110000
3	เหล็กประกับคอน 30 X 6 X 760 มม. BRACE, FLAT, FOR CROSSARM, 30 X 6 X 760 mm	3	01200001
4	สลักเกลียว M 16 X 130 มม. BOLT, MACHINE, M 16 X 130 mm	3	01110200
5	สลักเกลียว M 16 X 250 มม. BOLT, MACHINE, M 16 X 250 mm	6	01110203
6	สลักเกลียว M 16 X 350 มม. BOLT, MACHINE, M 16 X 350 mm	2	01110205
7	แหวนสี่เหลี่ยมแบน 52 X 52 X 4.5 มม. รู Ø 18 มม. มอก. 258 WASHER, SQUARE, FLAT, 52 X 52 X 4.5 mm, HOLE Ø 18 mn, TIS 258	13	01180100
8	ดรอพเอาท์ ฟิวส์คัทเอาท์ หนึ่งอินซูเลเตอร์ 33 kV, 100 แอมป์ CUT-OUT, FUSE, OPEN TYPE, SINGLE INSULATOR, DROPOUT, 33 kV, 100 A	1	04010100
9	ล่อฟ้าแรงสูง 30 kV, 5 กิโลแอมแปร์ LIGHTNING ARRESTER, 30 kV, 5 kA	1	04000100
10	หม้อแปลงซิงเกิลบุชชิ่ง 33 GRDY / 19 / 0.46-0.23 kV, 10-50 kVA TRANSFORMER, SINGLE BUSHING, 33 GRDY / 19 / 0.46-0.23 kV, 10-50 kVA	1	05000201 05000203

กองวิศวกรรมไฟฟ้าและเครื่องกล
ฝ่ายวิศวกรรม

ผู้เขียน
ผู้สำรวจ
วิศวกร
หัวหน้าแผนก
ผู้อำนวยการกอง
ผู้อำนวยการฝ่าย

รองผู้ว่าการฝ่ายเทคนิค

การไฟฟ้าส่วนภูมิภาค

ผู้ว่าการ ๙ เม.ย. ๓๔

การติดตั้งหม้อแปลงซิงเกิลบุชชิ่ง 19 kV
ในสายระบบจำหน่าย 1 เฟส 19 kV

19 kV SINGLE BUSHING TRANSFORMER INSTALLATION
ON 1-PHASE 19 kV DISTRIBUTION LINE

ใช้แทนแบบ
ถูกแทนโดยแบบ
เขียนเสร็จวันที่ 26 มี.ค. 34
แก้แบบวันที่ 4 ก.ย. 35
ผิดเป็น
มาตราส่วน

แบบเลขที่ SAI-015/34009
แผ่นที่ 2 ของจำนวน 4 แผ่น

- 5 เม.ย. 2536

การประกอบเลขที่
ASSEMBLY NO. **3701 D**

บัญชีวัสดุ
BILL OF MATERIAL

ลำดับที่ ITEM	รายละเอียด DESCRIPTION	จำนวน REQ'D	วัสดุเลขที่ MAT. NO.
11	ลวดเหล็กตีเกลียว 50/7 ต.มม. มอก. 404 พร้อมอุปกรณ์ยึด WIRE, STEEL, STRANDED, 50/7 mm^2, TIS 404 COMP. WITH FIXING ACCESS.	22 ม. m	01100004
12	สายอะลูมิเนียมหุ้มฉนวน PVC 750V, 75°C มอก. 293 หรือหุ้มฉนวนแบบไม่เต็มพิกัด 33 kV ขนาด 35 ต.มม. CABLE, Al, PVC INSULATED, 750V, 75°C, TIS 293 OR PARTIALLY INSULATED, 33 kV, 35 mm^2	10 ม. m	02070001 or 02060100
13	พี.จี. คอนเนคเตอร์ สลักคู่ สำหรับสายอะลูมิเนียม 25 - 95 ต.มม. CONNECTOR, PARALLEL GROOVE, DOUBLE BOLT, Al 25 - 95 mm^2	1	02300102
14	สายอะลูมิเนียมหุ้มฉนวน PVC 750 V, 75°C มอก. 293 ขนาดตามต้องการ CABLE, Al, PVC INSULATED, 750 V, 75°C, TIS 293; SIZE AS REQUIRED	20 ม. m	02070001 - 02070004
15	ฮอทไลน์แคล้มป์ สำหรับสายเมนอะลูมิเนียม ขนาดตามต้องการ CLAMP, HOT LINE, MAIN LINE, Al; SIZE AS REQUIRED	1	02330100 02330101
16	สเตอร์รัพแคล้มป์ หรือเบลแคล้มป์ สำหรับสายเมนอะลูมิเนียม ขนาดตามต้องการ CLAMP, STIRRUP OR BAIL, MAIN LINE, Al; SIZE AS REQUIRED	1	02330000 02330001
17	แร็ค 3 X 200 มม. แบบหลังยื่น RACK, SECONDARY, MEDIUM PRESSED STEEL 3 X 200 mm EXT. BACK	1	03130001
18	ลูกรอกแรงต่ำ แบบ ข (แบบ 53-2) มอก. 227 INSULATOR, SPOOL TYPE, L.T., TYPE B (CLASS 53-2), TIS 227	5	03030000
19	ฟิวส์สวิตช์แรงต่ำ 1 X 400 แอมป์ 500 โวลต์ L.T. - FUSE SWITCH 1 X 400 A, 500 V	2	04020100
20	ล่อฟ้า 250-500 โวลต์ 2.5-5.0 กิโลแอมแปร์ LIGHTNING ARRESTER 250 - 500V, 2.5 - 5.0 kA	2	04000300
21	ท่อ PVC แข็ง ขนาด Ø 20X2,500 มม. หรือ Ø 20 X 4,000 มม. มอก. 216 พร้อมอุปกรณ์ยึด CONDUIT, PVC, RIGID, Ø 20 X 2,500 mm OR Ø 20 X 4,000 mm, TIS 216, COMPLETE WITH FIXING ACCESS.	1	08040002 or 08040001
22	หลักดิน 60 X 60 X 5 มม. ยาว 2 ม. ROD, GROUND 60 X 60 X 5 mm, 2 m LONG	1	01220002
23	ยูแคล้มป์ สลัก 1 ตัว M 8 CLAMP, SINGLE U-BOLT, M 8	6	01230000
24	PVC เทป กว้าง 19 มม. (ใช้ความยาว 2 ม. ต่อ 1 จุด) PVC TAPE, 19 mm WIDE (2 m LONG PER POINT)	ม้วน rolls	02180002
25	เหล็กจับขอบถังหม้อแปลง สำหรับยึดสายแรงต่ำ BRACKET, STEEL, FOR TRANSFORMER SECONDARY LEAD	2	05100003
26	ลวดอะลูมิเนียมกลม Ø 4 มม. ความยาวตามต้องการ TIE WIRE, Al, Ø 4 mm; LENGTH AS REQUIRED	ม. m	02200002
27	คอนเนคเตอร์ ชนิดบีบ แบบ H สำหรับสายอะลูมิเนียม ขนาดตามต้องการ CONNECTOR, COMPRESSION, H TYPE, Al, SIZE AS REQUIRED	3	02320003 or 02320002

กองวิศวกรรมไฟฟ้าและเครื่องกล
ฝ่ายวิศวกรรม

ผู้เขียน
ผู้สำรวจ
วิศวกร
หัวหน้าแผนก
ผู้อำนวยการกอง
ผู้อำนวยการฝ่าย
รองผู้ว่าการฝ่ายเทคนิค

การไฟฟ้าส่วนภูมิภาค

ผู้ว่าการ 9 เม.ย. 34

การติดตั้งหม้อแปลงซิงเกิลบุชชิ่ง 19 kV
ในสายระบบจำหน่าย 1 เฟส 19 kV

19 kV SINGLE BUSHING TRANSFORMER INSTALLATION
ON 1-PHASE 19 kV DISTRIBUTION LINE

ใช้แทนแบบ
ถูกแทนโดยแบบ
เขียนเสร็จวันที่ 26 มี.ค. 34
แก้แบบวันที่ 4 ก.ย. 35
มิติเป็น
มาตราส่วน
แบบเลขที่ SAI-015/34009
แผ่นที่ 3 ของจำนวน 4 แผ่น

- 5 เม.ย. 2534

การประกอบเลขที่ ASSEMBLY NO. **3701 D**

	แบบอ้างอิง REFERENCE DRAWING	แบบเลขที่ DWG. NO.	การประกอบเลขที่ ASSEMBLY NO.
1	การประกอบคอนคอนกรีต กับเสาคอนกรีต CONCRETE CROSSARM ASSEMBLY ON CONCRETE POLE	SAI-015/29023	3308
2	การติดตั้งล่อฟ้าแรงต่ำ ในระบบจำหน่ายแรงต่ำ L.T. LIGHTNING ARRESTER INSTALLATION IN L.T. DISTRIBUTION LINE	SAI-015/22040	0402
3	การติดตั้งฟิวส์สวิตช์แรงต่ำบนคอน คอร. 100 X 100 X 1,500 มม. L.T. FUSE SWITCH INSTALLATION ON PRESTRESSED CROSSARM 100 X 100 X 1,500 mm	SAI-015/22012	0406
4	ขนาดของสายไฟฟ้าแรงต่ำที่ออกจากหม้อแปลง THE SIZE OF L.T. CABLE FROM TRANSFORMER	SAI-015/22034	0601
5	การต่อลงดิน ระบบแรงสูง และแรงต่ำ H.T. AND L.T. EARTHING SYSTEM	S02-015/20039	9701
6	การประกอบสายลงดิน วิธียึดลวดเหล็ก GROUND LEAD ASSEMBLY, STEEL WIRE FITTING	S02-015/19166 SAI-015/31012	9703 9703 A
7	การประกอบที่ยึดท่อ PVC สำหรับสายดิน PVC PIPE FITTING ASSEMBLY, FOR GROUND WIRE	S02-015/19128 SAI-015/31013	9704 9704 A
8	พื้นที่หน้าตัดสำหรับสายเป็นกลาง ระบบแรงต่ำ NOMINAL CROSS-SECTIONS FOR NEUTRAL, L.T. SYSTEM	S02-015/16036	0201

อดิวิทย์ ทองลา พชง.3 ผปร. กฟส.อล. กฟจ.กบ. กฟต.2 สายงาน (ต) ผวก. @PEA

กองวิศวกรรมไฟฟ้าและเครื่องกล
ฝ่ายวิศวกรรม

ผู้เขียน
ผู้สำรวจ
วิศวกร
หัวหน้าแผนก
ผู้อำนวยการกอง
ผู้อำนวยการฝ่าย
รองผู้ว่าการฝ่ายเทคนิค

การไฟฟ้าส่วนภูมิภาค

ผู้ว่าการ 9 เม.ย. 34

การติดตั้งหม้อแปลงซิงเกิลบุชชิ่ง 19 kV ในสายระบบจำหน่าย 1 เฟส 19 kV

19 kV SINGLE BUSHING TRANSFORMER INSTALLATION ON 1- PHASE 19 kV DISTRIBUTION LINE

ใช้แทนแบบ
ถูกแทนโดยแบบ
เขียนเสร็จวันที่ 26 มี.ค. 34
แก้แบบวันที่ 4 ก.ย. 35
ผิดเป็น
มาตราส่วน

แบบเลขที่ SAI-015/34009
แผ่นที่ 4 จากจำนวน 4 แผ่น

5 เม.ย. 2534