การประกอบเลขที่
ASSEMBLY NO. 3311

สำเนา

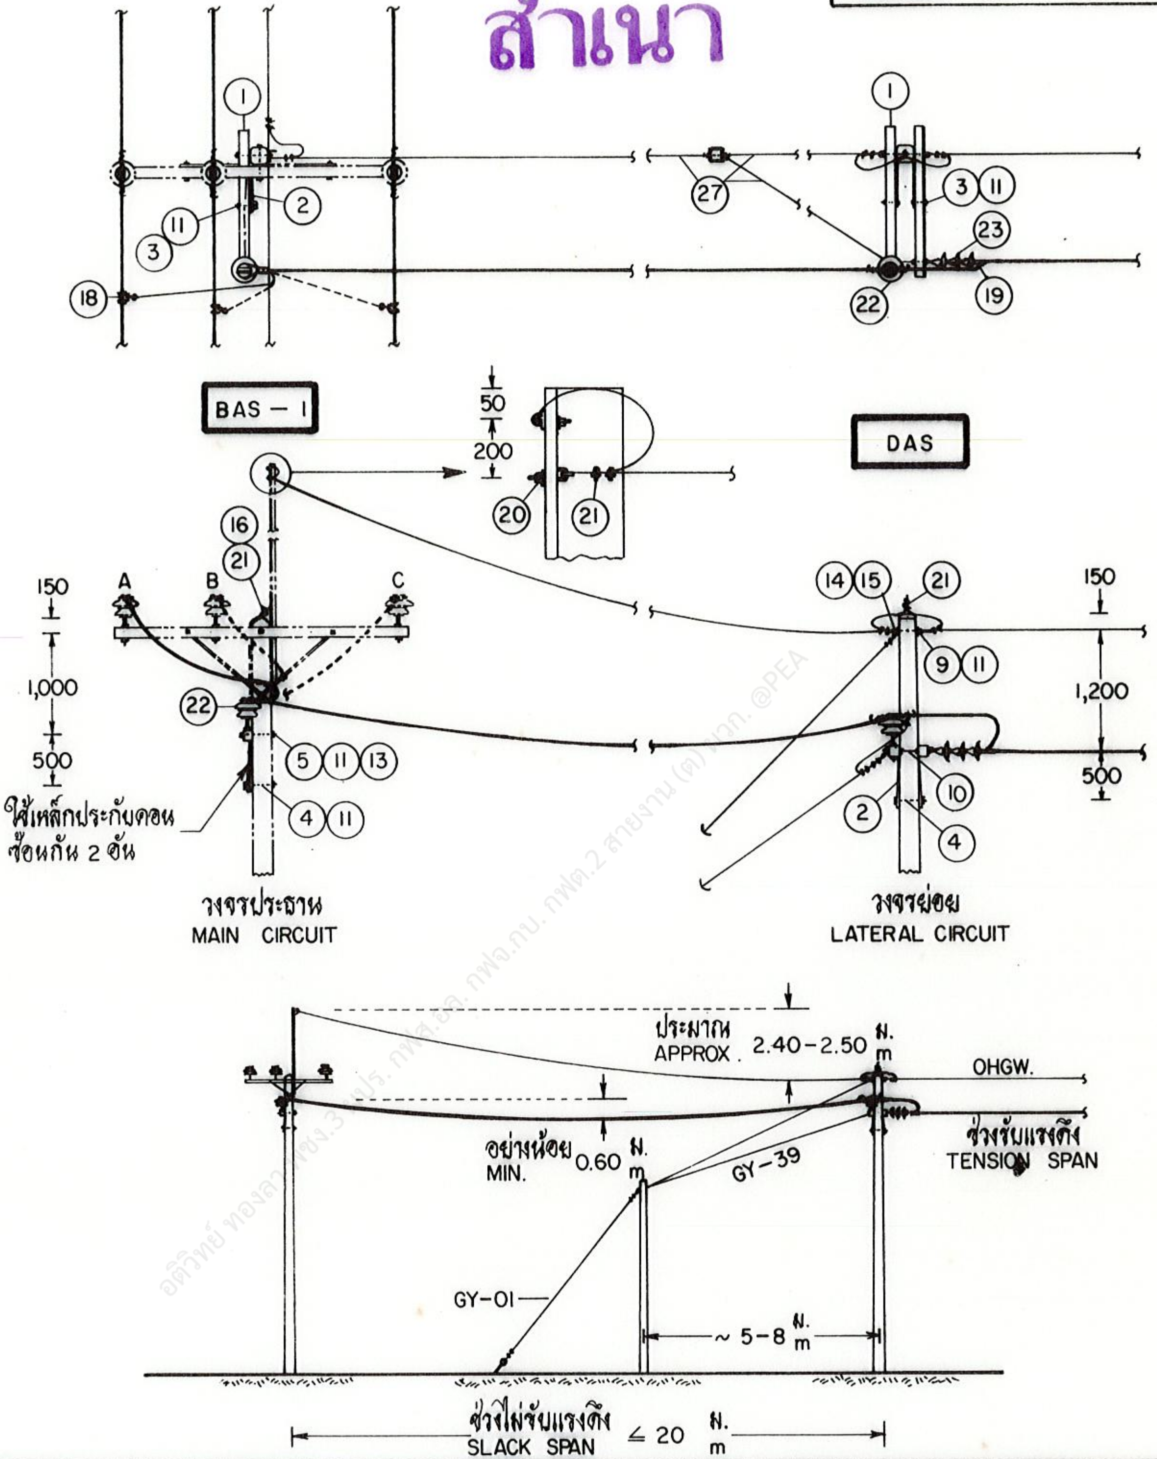

อดิวิทย์ ทองลา ชง.3 ปร. กฟส.อล. กฟจ.กบ. กฟต.2 สายงาน (ต) นวก. @PEA

สำหรับใช้ก่อสร้างในบริเวณที่มีโหลดน้อย และไม่มีการปรับปรุงเป็น ระบบ 3 เฟส 33 กิโลโวลต์ ในอนาคตอันใกล้
FOR CONSTRUCTION IN LIGHT LOAD SITE WHERE SHALL NOT BE REVAMPED TO 3-PHASE, 33 kV SYSTEM IN THE NEAR FUTURE.

กองวิศวกรรมไฟฟ้าและเครื่องกล
ฝ่ายวิศวกรรม

การไฟฟ้าส่วนภูมิภาค

ผู้เขียน ....
ผู้สำรวจ ....
วิศวกร ....
หัวหน้าแผนก ....
ผู้อำนวยการกอง ....
ผู้อำนวยการฝ่าย ....
รองผู้ว่าการฝ่ายเทคนิค

ผู้ว่าการ ....
2 มิ.ย. 2531

การติดตั้งบัคอาร์มแบบท้าวแขน ระบบ 1 เฟส 19 kV
(กรณีใช้คอนคอนกรีต)
สำหรับการพาดสายช่วงสั้นไม่รับแรงดึง

1-PHASE, 19 kV ALLEY BUCKARM INSTALLATION
(CONCRETE CROSSARM)
SLACK SPAN LATERAL

ใช้แทนแบบ ....
ถูกแทนโดยแบบ ....
เขียนเสร็จวันที่ 18 พ.ค. 31
แก้แบบวันที่ ....
มิติเป็น มม.
มาตราส่วน 1 : 75 , 1 : 250
แบบเลขที่ SA1-015/31047
แผ่นที่ 1 ของจำนวน 4 แผ่น

การประกอบเลขที่ ASSEMBLY NO.	3311

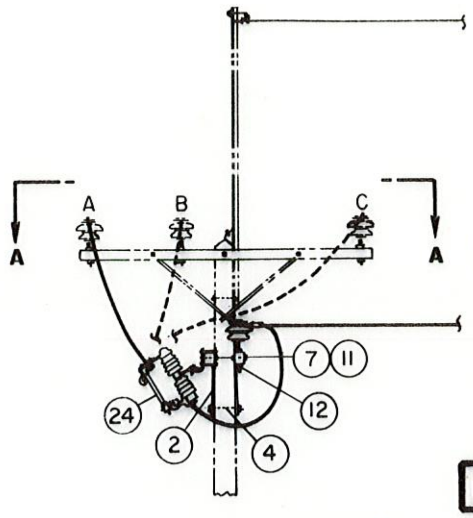

BAS – 2

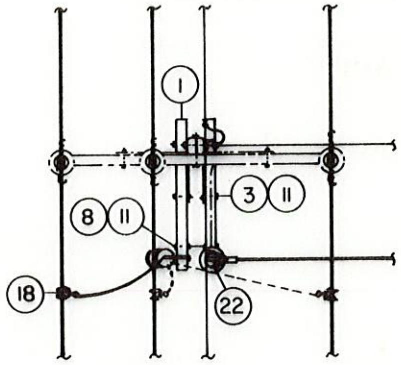

รูปตัด
SECTION A – A

วิธีผูกลูกถ้วย (การเข้าปลายสายช่วงไม่รับแรงดึงบนลูกถ้วยก้านตรง)
TYING METHOD (SLACK SPAN DEADENDING ON PIN INSULATOR)

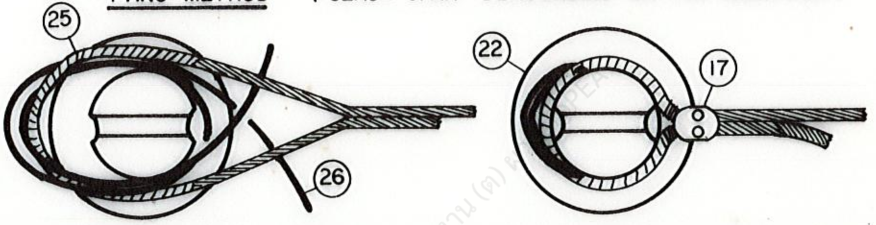

ให้พันลวดอะลูมิเนียมแบนรอบสายไฟหนึ่งชั้น แล้วใช้ลวดอะลูมิเนียมกลมพันรอบลูกถ้วย และสายไฟ พร้อมกับใช้คอนเนคเตอร์เข้าปลายสาย 1 ชุด จับสายไฟให้ใกล้ลูกถ้วยมากที่สุด

CONDUCTOR SHOULD BE WRAPPED WITH ALUMINIUM ARMOUR TAPE ONE LAYER AND TIED WITH THE TIE WIRE. THE CONDUCTOR SHOULD BE CLAMPED WITH DEADEND CONNECTOR CLOSE TO INSULATOR.

ข้อกำหนดการใช้งาน	**RECOMMENDATION**
1. ระยะห่างระหว่างช่วงเสาประธานไม่เกิน 50 ม.	1. MAXIMUM MAIN SPAN 50 m
2. ระยะห่างระหว่างช่วงเสาไม่รับแรงดึงไม่เกิน 20 ม.	2. MAXIMUM SLACK SPAN LATERAL 20 m
3. สายไฟฟ้าขนาดสูงสุด	3. CONDUCTOR, MAXIMUM SIZE
สายอะลูมิเนียม หรืออะลูมิเนียมอัลลอย ขนาด 50 ต.มม.	Al OR Al-ALLOY 50 mm^2
สายอะลูมิเนียมแกนเหล็ก ขนาด 50/8 ต.มม.	ACSR 50/8 mm^2

สำเนา

กองวิศวกรรมไฟฟ้าและเครื่องกล ฝ่ายวิศวกรรม	**การไฟฟ้าส่วนภูมิภาค**	ใช้แทนแบบ ถูกแทนโดยแบบ
ผู้เขียน ผู้สำรวจ วิศวกร หัวหน้าแผนก ผู้อำนวยการกอง ผู้อำนวยการฝ่าย	ผู้ว่าการ 2 มิ.ย. 2531 การติดตั้งบัคอาร์มแบบท้าวแขน ระบบ 1 เฟส 19 kV (กรณีใช้คอนคอนกรีต) สำหรับการพาดสายช่วงสั้นไม่รับแรงดึง	เขียนเสร็จวันที่ 18 พ.ค. 31 แก้แบบวันที่ มิติเป็น มาตราส่วน
รองผู้ว่าการฝ่ายเทคนิค	I-PHASE, 19 kV ALLEY BUCKARM INSTALLATION (CONCRETE CROSSARM) SLACK SPAN LATERAL	แบบเลขที่ SAL-015/31047 แผ่นที่ 2 ของจำนวน 4 แผ่น

การประกอบเลขที่ ASSEMBLY NO.	3311

บัญชีวัสดุ
BILL OF MATERIAL

สำเนา

ลำดับที่ ITEM	รายละเอียด DESCRIPTION	จำนวน REQ'D			วัสดุเลขที่ MAT. NO.
		BAS-1	BAS-2	DAS	
1	คอน คอร. ขนาด 100 X 100 X 1,500 มม. CROSSARM, PRESTRESSED CONCRETE 100 X 100 X 1,500 mm	1	2	2	00110000
2	เหล็กประกับคอน 30 X 6 X 760 มม. BRACE, FLAT, FOR CROSSARM, 30 X 6 X 760 mm	2	2	2	01200001
3	สลักเกลียว M 16 X 130 มม. BOLT, MACHINE M 16 X 130 mm	1	2	2	01110200
4	สลักเกลียว M 16 X 250 มม. BOLT, MACHINE M 16 X 250 mm	1	1	1	01110203
5	สลักเกลียว M 16 X 350 มม. BOLT, MACHINE M 16 X 350 mm	1	–	–	01110205
6	สลักเกลียว M 16 X 400 มม. BOLT, MACHINE M 16 X 400 mm	–	–	1	01110206
7	สลักเกลียว M 16 X 450 มม. BOLT, MACHINE M 16 X 450 mm	–	1	–	01110207
8	สลักเกลียวตลอด M 16 X 450 มม. BOLT, DOUBLE ARMING, M 16 X 450 mm	–	1	–	01120001
9	สลักห่วงกลม M 16 X 200 มม. BOLT, ROUND EYE, M 16 X 200 mm	–	–	1	01140001
10	สลักเกลียวห่วงกลม M 16 X 400 มม. BOLT, DOUBLE ARMING, ROUND EYE, M 16 X 400 mm	–	–	1	01130000
11	แหวนสี่เหลี่ยมแบน 52 X 52 X 4.5 มม. รู Ø 18 มม. มอก. 258 WASHER, SQUARE, FLAT, 52 X 52 X 4.5 mm, HOLE Ø 18 mm, TIS 258	4	8	10	01180100
12	แหวนสี่เหลี่ยมโค้ง 60 X 60 X 5 มม. รู Ø 22 มม. WASHER, SQUARE, CURVED, 60 X 60 X 5 mm, HOLE Ø 22 mm	1	1	–	01180300
13	แหวนสปริง M 16 มอก. 259 WASHER, LOCK, M 16, TIS 259	1	1	1	01180301
14	นัทรูปห่วง M 16 DIN 582 NUT, EYE M 16 DIN 582	–	–	1	01180001
15	กายทิมเบิ้ล สำหรับสายยึดโยง 50-95 ต.มม. THIMBLE, GUY, FOR STEEL WIRE 50-95 mm^2	–	–	2	01210304
16	ลวดเหล็กกลมเส้นผ่านศูนย์กลาง 4 มม. เส้นเดี่ยว มอก. 71 นน. ประมาณ 0.1 กก./ม. WIRE, STEEL, SOLID, DIAMETER 4 mm TIS 71 WEIGHT APPROX. 0.1 kg / m	2.0 ม. m	2.5 ม. m	–	01100000
17	คอนเนคเตอร์เข้าปลายสายอะลูมิเนียม ขนาดตามต้องการ CONNECTOR, DEADEND, Al SIZE AS REQUIRED	1	1	–	02310000 02310001
18	เบล (สเตอร์รัพ) แคล้มป์ และฮอทไลน์แคล้มป์ ขนาดตามต้องการ CLAMP, BAIL (STIRRUP); AND HOT LINE CLAMP; SIZE AS REQUIRED	1	1	–	02330000-1 02330100-1
19	สเตรนแคล้มป์สำหรับสายอะลูมิเนียม 35-95 ต.มม. อะลูมิเนียมแกนเหล็ก 35-50 ต.มม. CLAMP, STRAIN FOR Al 35-95 mm^2, ACSR. 35-50 mm^2	–	–	1	03110000 03110001
20	กราวด์วายแคล้มป์ แบบ J 1152 GROUND WIRE SUPPORT AND CLAMP, J 1152	1	1	–	01230200

กองวิศวกรรมไฟฟ้าและเครื่องกล
ฝ่ายวิศวกรรม

การไฟฟ้าส่วนภูมิภาค

ผู้เขียน
ผู้สำรวจ
วิศวกร
หัวหน้าแผนก
ผู้อำนวยการกอง
ผู้อำนวยการฝ่าย
รองผู้ว่าการฝ่ายเทคนิค

ผู้ว่าการ

2 มิ.ย. 2531

การติดตั้งบัคอาร์มแบบท้าวแขน ระบบ 1 เฟส 19 kV
(กรณีใช้คอนคอนกรีต)
สำหรับการพาดสายช่วงสั้นไม่รับแรงดึง

1-PHASE, 19 kV ALLEY BUCKARM INSTALLATION
(CONCRETE CROSSARM)
SLACK SPAN LATERAL

ใช้แทนแบบ
ถูกแทนโดยแบบ
เขียนเสร็จวันที่ 18 พ.ค. 31
แก้แบบวันที่
มิติเป็น
มาตราส่วน
แบบเลขที่ SAI-015/31047
แผ่นที่ 3 ของจำนวน 4 แผ่น

การประกอบเลขที่ ASSEMBLY NO.	3311

บัญชีวัสดุ
BILL OF MATERIAL

ลำดับที่ ITEM	รายละเอียด DESCRIPTION	จำนวน REQ'D BAS-1	 BAS-2	 DAS	วัสดุเลขที่ MAT NO.
21	ยูแคล้มป์ สลัก 1 ตัว M8 (ไวร์ โร้ป คลิ้ฟ) CLAMP, SINGLE U-BOLT, M 8 (WIRE ROPE CLIP)	6	6	4	01230000
22	ลูกถ้วยก้านตรง 33 kV มอก. 279 แบบ ค (แบบ 56-3) พร้อมก้าน INSULATOR, PIN TYPE, 33 kV, TIS 279 TYPE C (CLASS 56-3), COMP. WITH PIN	1	1	1	03000002 03100001
23	ลูกถ้วยแขวน มอก. 354 แบบ ง (แบบ 52-4) INSULATOR, SUSPENSION TYPE, TIS 354 TYPE D (CLASS 52-4)	–	–	3	03020002
24	ดรอพเอาต์ ฟิวส์คัทเอาท์ หนึ่งอินซูเลเตอร์ 33 kV 100 แอมป์ CUTOUT, FUSE, DROPOUT, SINGLE INSULATOR, 33 kV, 100 A	–	1	–	04010100
25	ลวดอะลูมิเนียมแบน 1X10 มม. ความยาวตามต้องการ ARMOUR TAPE, Al 1X10 mm, LENGTH AS REQUIRED				02200000
26	ลวดอะลูมิเนียมกลม Ø 4 มม. ความยาวตามต้องการ TIE WIRE, Al Ø 4 mm, LENGTH AS REQUIRED				02200002
27	การประกอบสายยึดโยง GY-39 และ GY-01 GUY ASSEMBLY GY-39 AND GY-01	–	–	1	

กบ. กฟต.2 สายงาน (ต) ผวก. @PEA

	แบบอ้างอิง REFERENCE DRAWING	แบบเลขที่ DWG. NO.	การประกอบเลขที่ ASSEMBLY NO.
1	ข้อแนะนำในการก่อสร้างระบบจำหน่าย 1 เฟส 19 kV CONSTRUCTION SUGGESTION OF 1-PHASE 19 kV SYSTEM	S02-015/20016	3305
2	รายละเอียดการประกอบสายยึดโยง ชุด GY-39 DETAIL OF GUY ASSEMBLY GY-39	SA1-015/21071	8455
3	รายละเอียดการประกอบสายยึดโยง ชุด GY-01 DETAIL OF GUY ASSEMBLY GY-01	SA1-015/20037	8451
4	การประกอบสายลงดินด้วยวิธียึดลวดเหล็ก GROUND LEAD ASSEMBLY STEEL WIRE FITTING	S02-015/19166	9703

สำเนา

กองวิศวกรรมไฟฟ้าและเครื่องกล ฝ่ายวิศวกรรม	**การไฟฟ้าส่วนภูมิภาค**	ใช้แทนแบบ ถูกแทนโดยแบบ
ผู้เขียน ผู้สำรวจ วิศวกร หัวหน้าแผนก ผู้อำนวยการกอง ผู้อำนวยการฝ่าย	ผู้ว่าการ มิ.ย. 2531	เขียนเสร็จวันที่ 18 พ.ค. 31 แก้แบบวันที่ มิติเป็น มาตราส่วน
	การติดตั้งบัคอาร์มแบบท้าวแขน ระบบ 1 เฟส 19 kV (กรณีใช้คอนคอนกรีต) สำหรับการพาดสายช่วงสั้นไม่รับแรงดึง	
รองผู้ว่าการฝ่ายเทคนิค	I-PHASE, 19 kV ALLEY BUCKARM INSTALLATION (CONCRETE CROSSARM SLACK SPAN LATERAL	แบบเลขที่ SA1-015/31047 แผ่นที่ 4 ของจำนวน 4 แผ่น