การประกอบเลขที่
ASSEMBLY NO. **5 2 2 2 A**

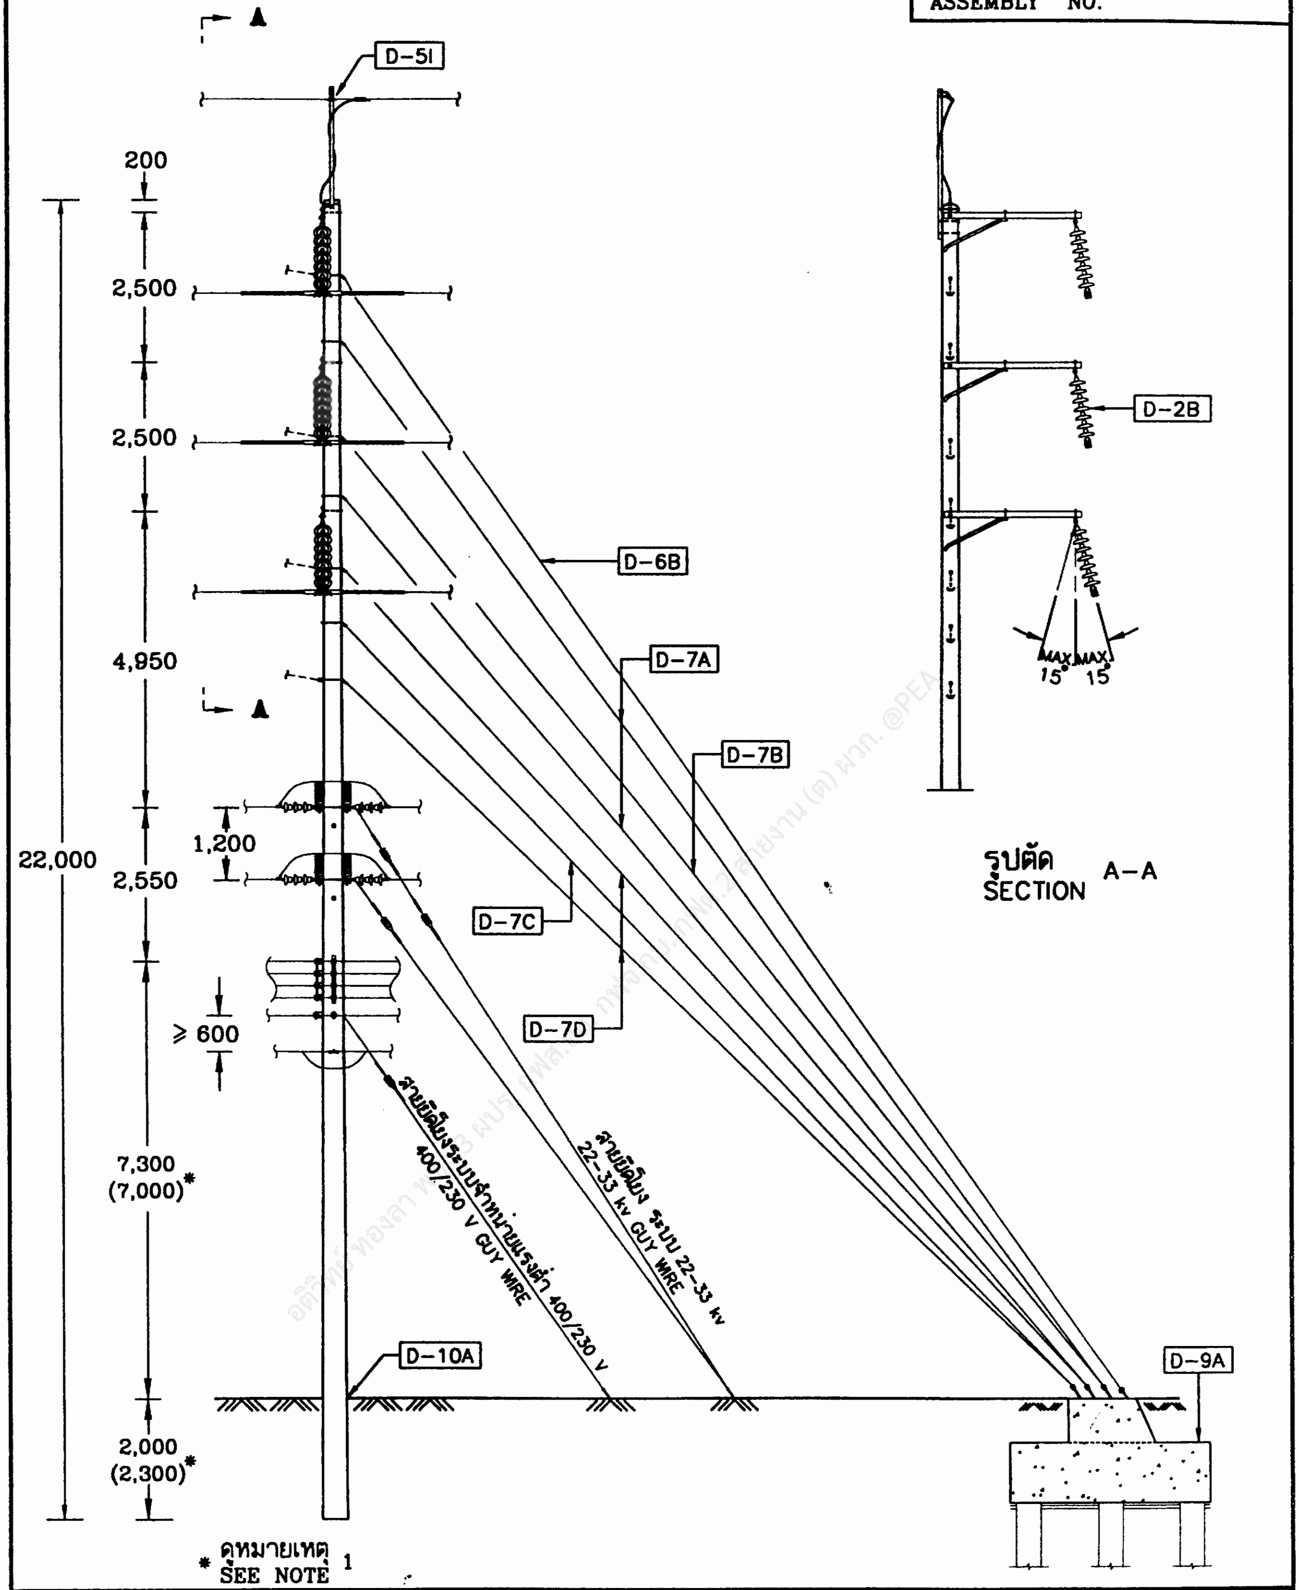
A
D-5I
200
2,500
2,500
4,950
A
22,000
1,200
2,550
≥ 600
7,300
(7,000)*
2,000
(2,300)*
D-6B
D-7A
D-7B
D-7C
D-7D
D-10A
D-9A
D-2B
MAX. 15°
MAX. 15°
สายยึดโยงระบบจำหน่ายแรงต่ำ 400/230 V
400/230 V GUY WIRE
สายยึดโยง ระบบ 22-33 kV
22-33 kV GUY WIRE
รูปตัด
SECTION A-A

* ดูหมายเหตุ 1
SEE NOTE 1

กองมาตรฐานระบบไฟฟ้า ฝ่ายมาตรฐานและความปลอดภัย	**การไฟฟ้าส่วนภูมิภาค**	ใช้แทนแบบ .... ถูกแทนโดยแบบ ....
ผู้เขียน ...สมชาย......... ผู้สำรวจ.................. วิศวกร...................... หัวหน้าแผนก............... ผู้อำนวยการกอง.............. ผู้อำนวยการฝ่าย..............	ผู้ว่าการ.................................. 115 kV วงจรเดี่ยว สายไฟฟ้าเดี่ยว เสา คอร. (ชนิดมีกราวด์เพลทในเสา) สำหรับทางโค้ง ต่อจากต้นเข้าปลายสายสองข้าง แบบ SS-SA-4	เขียนเสร็จวันที่.3..ม.ค..2549 แก้แบบวันที่ .... มิติเป็น...มิลลิเมตร........ มาตราส่วน...1:125........
รองผู้ว่าการฝ่ายวางแผนและพัฒนาระบบไฟฟ้า	115 kV SINGLE CIRCUIT SINGLE CONDUCTOR CONCRETE POLE (WITH GROUND PLATE IN POLE) ANGLE STRUCTURE ADJACENT TO DOUBLE DEADEND STRUCTURE TYPE SS-SA-4	แบบเลขที่ SA1-015/49004 แผ่นที่.1.ของจำนวน.4.แผ่น

การประกอบเลขที่
ASSEMBLY NO. **5222A**

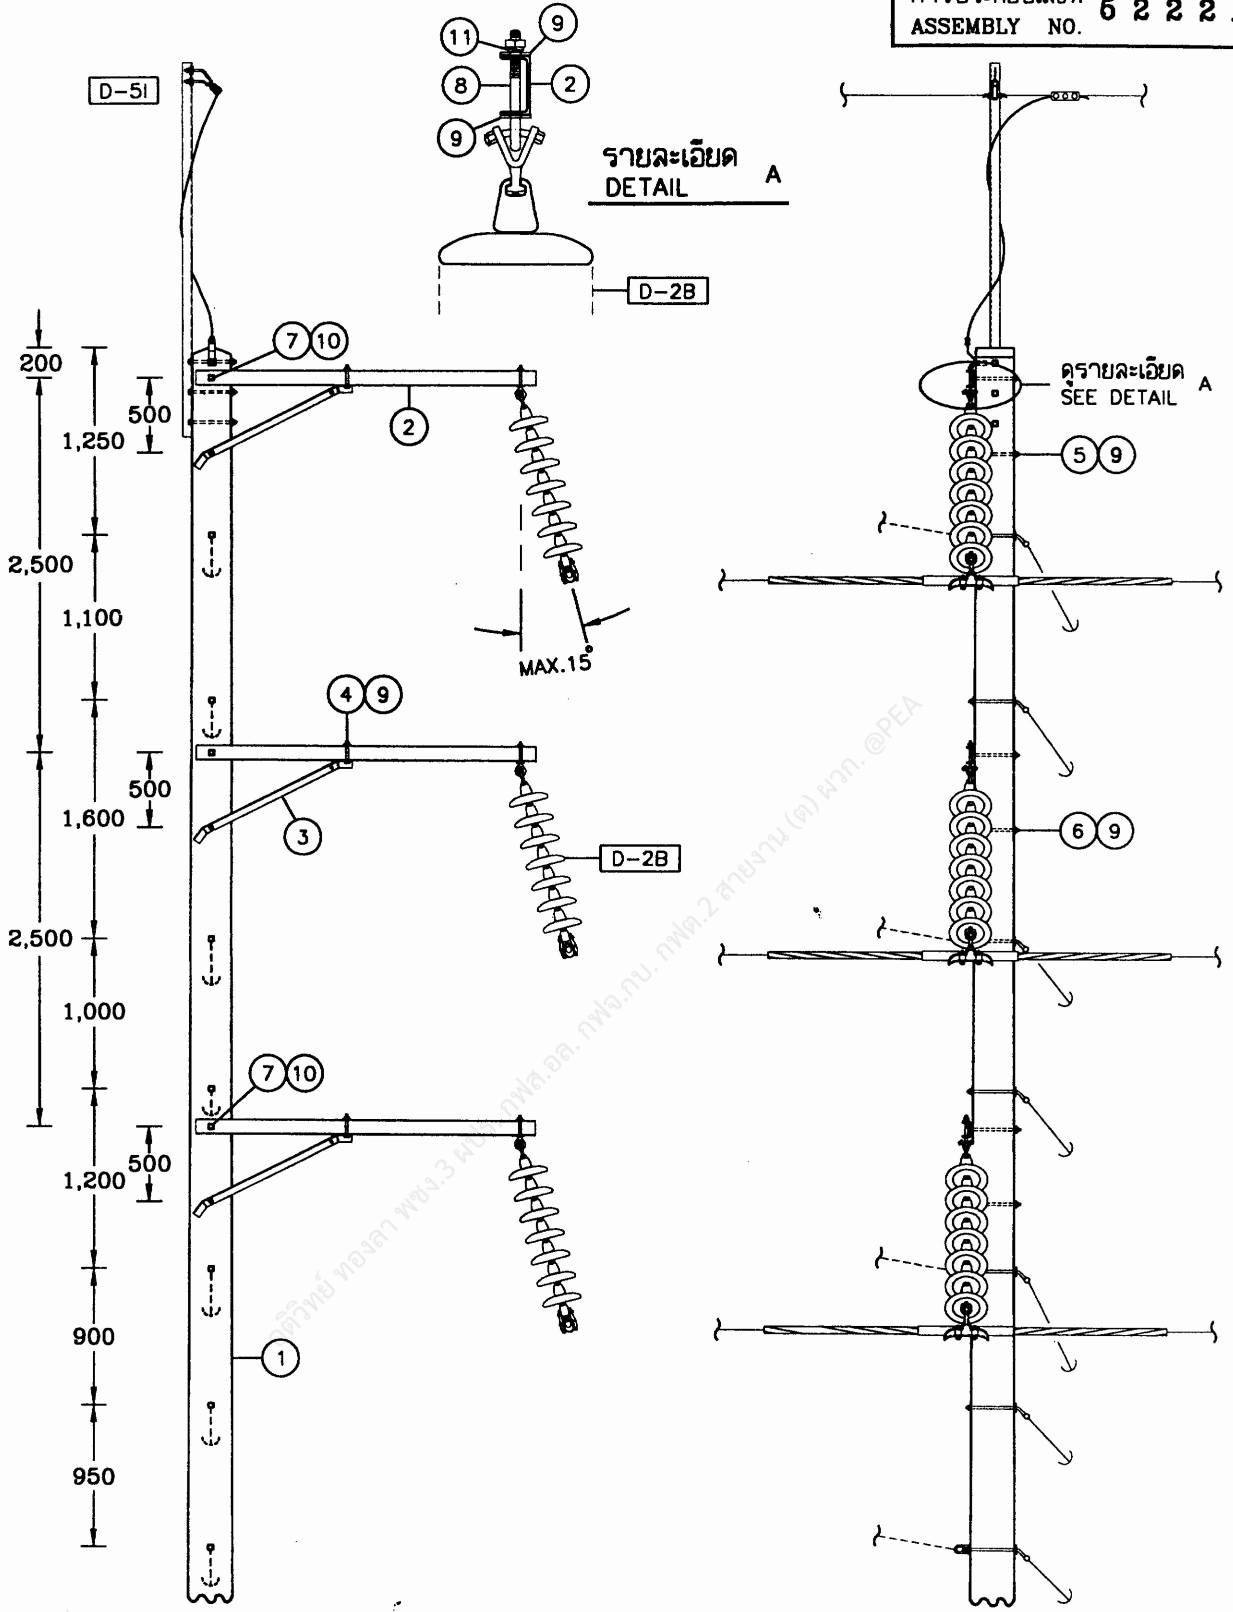

11
9
8
2
9
รายละเอียด A
DETAIL A
D-2B
D-5I
7 10
2
200
500
1,250
2,500
1,100
MAX.15°
4 9
500
1,600
3
D-2B
2,500
1,000
7 10
500
1,200
900
1
950
ดูรายละเอียด A
SEE DETAIL A
5 9
6 9

ติวิทย์ ทองลา พชง.3 ผปร. กฟส.อล. กฟจ.กบ. กฟต.2 สายงาน (ต) ผวก. @PEA

กองมาตรฐานระบบไฟฟ้า
ฝ่ายมาตรฐานและความปลอดภัย

การไฟฟ้าส่วนภูมิภาค

ผู้เขียน ...สมชาย...........
ผู้สำรวจ....................
วิศวกร.......................
หัวหน้าแผนก..................
ผู้อำนวยการกอง................
ผู้อำนวยการฝ่าย...............

รองผู้ว่าการฝ่ายวางแผนและพัฒนาระบบไฟฟ้า
....

ผู้ว่าการ..............................

115 kV วงจรเดี่ยว สายไฟฟ้าเดี่ยว
เสา คอร. (ชนิดมีกราวด์เพลทในเสา)
สำหรับทางโค้ง ต่อจากต้นเข้าปลายสายสองข้าง
แบบ SS-SA-4

115 kV SINGLE CIRCUIT SINGLE CONDUCTOR
CONCRETE POLE (WITH GROUND PLATE IN POLE)
ANGLE STRUCTURE ADJACENT TO DOUBLE DEADEND STRUCTURE
TYPE SS-SA-4

ใช้แทนแบบ ....
ถูกแทนโดยแบบ ....
เขียนเสร็จวันที่.3. ม.ค. 2549
แก้แบบวันที่ ....
มิติเป็น...มิลลิเมตร........
มาตราส่วน...1:50.........

แบบเลขที่ SA1-015/49004

แผ่นที่.2.ของจำนวน.4.แผ่น

การประกอบเลขที่ ASSEMBLY NO.	5 2 2 2 A

บัญชีวัสดุ
BILL OF MATERIAL

ลำดับที่ ITEM	รายละเอียด DESCRIPTION	จำนวน REQ.D	วัสดุเลขที่ MAT. NO.
1	เสา คอร. ยาว 22.00 ม. ชนิดมีกราวด์เพลทในเสา POLE, CONCRETE, 22.00 m LONG, WITH GROUND PLATE IN POLE	1	00010015
2	เหล็กรูปรางน้ำ ขนาด 100x50x5 มม. ยาว 2,250 มม. มอก. 1227 STEEL CHANNEL, 100x50x5 mm, 2,250 mm LONG, TIS 1227	3	01000100
3	เหล็กประกับคอนสายแบบทาวแขน ขนาด 50x50x6 มม. ยาว 1,000 มม. BRACE, ALLEY ARM, 50x50x6 mm, 1,000 mm LONG	3	01200009
4	สลักเกลียว M 16x130 มม. BOLT, MACHINE, M 16x130 mm	3	01110200
5	สลักเกลียว M 16x300 มม. BOLT, MACHINE, M 16x300 mm	1	01110204
6	สลักเกลียว M 16x350 มม. BOLT, MACHINE, M 16x350 mm	2	01110205
7	สลักเกลียว M 20x350 มม. BOLT, MACHINE, M 20x350 mm	3	01110300
8	สลักห่วงโอแวล M 16x150 มม. BOLT, OVAL EYE, M 16x150 mm	3	01150000
9	แหวนสี่เหลี่ยมแบน 52x52x4.5 มม. รู ø18 มม. มอก.258 WASHER, SQUARE, FLAT, 52x52x4.5 mm, HOLE Ø 18 mm, TIS 258	12	01180100
10	แหวนสี่เหลี่ยมแบน 62x62x6 มม. รู ø22 มม. มอก.258 WASHER, SQUARE, FLAT, 62x62x6 mm, HOLE Ø 22 mm, TIS 258	6	01180101
11	แหวนสปริง M 16 มอก. 259 WASHER, LOCK, M 16, TIS 259	3	01180301

รายละเอียด
DETAIL

D-2B	การประกอบลูกถ้วยแขวน SUSPENSION INSULATOR ASSEMBLY	3	
D-5I	การประกอบสายล่อฟ้า OVERHEAD GROUND WIRE ASSEMBLY	1	
D-6B	การประกอบสายยึดโยง ลวดเหล็กตีเกลียว 50 ต.มม. STEEL STRANDED WIRE 50 mm^2 GUY ASSEMBLY	1	
D-7A	การประกอบสายยึดโยง ลวดเหล็กตีเกลียว 95 ต.มม. STEEL STRANDED WIRE 95 mm^2 GUY ASSEMBLY	2	
D-7B	การประกอบสายยึดโยง ลวดเหล็กตีเกลียว 95 ต.มม. STEEL STRANDED WIRE 95 mm^2 GUY ASSEMBLY	1	
D-7C	การประกอบสายยึดโยง ลวดเหล็กตีเกลียว 95 ต.มม. STEEL STRANDED WIRE 95 mm^2 GUY ASSEMBLY	1	
D-7D	การประกอบสายยึดโยง ลวดเหล็กตีเกลียว 95 ต.มม. STEEL STRANDED WIRE 95 mm^2 GUY ASSEMBLY	2	
D-9A	สมอบกคอนกรีต CONCRETE ANCHOR	1	
D-10A	ฐานรากเสา POLE FOUNDATION	1	

กองมาตรฐานระบบไฟฟ้า ฝ่ายมาตรฐานและความปลอดภัย	การไฟฟ้าส่วนภูมิภาค	ใช้แทนแบบ .... ถูกแทนโดยแบบ ....
ผู้เขียน ...สมชาย........... ผู้สำรวจ .... วิศวกร .... หัวหน้าแผนก .... ผู้อำนวยการกอง .... ผู้อำนวยการฝ่าย	ผู้ว่าการ .... 115 kV วงจรเดี่ยว สายไฟฟ้าเดี่ยว เสา คอร. (ชนิดมีกราวด์เพลทในเสา) สำหรับทางโค้ง ต่อจากต้นเข้าปลายสายสองข้าง แบบ SS-SA-4	เขียนเสร็จวันที่ 3 ม.ค. 2549 แก้แบบวันที่ .... มิติเป็น .... มาตราส่วน ....
รองผู้ว่าการฝ่ายวางแผนและพัฒนาระบบไฟฟ้า	115 kV SINGLE CIRCUIT SINGLE CONDUCTOR CONCRETE POLE (WITH GROUND PLATE IN POLE) ANGLE STRUCTURE ADJACENT TO DOUBLE DEADEND STRUCTURE TYPE SS-SA-4	แบบเลขที่ SA1-015/49004 แผ่นที่ 3 ของจำนวน 4 แผ่น

การประกอบเลขที่
ASSEMBLY NO. **5 2 2 2 A**

รายละเอียด DETAIL			
D-25	การต่อลงดิน GROUNDING	1	

หมายเหตุ

1.* กรณีก่อสร้างในพื้นที่เขตทางหลวง ให้ใช้ค่าระยะห่างตามแนวดิ่งในวงเล็บ โดยดูรายละเอียดเพิ่มเติมในแบบเลขที่ SA1-015/43012 (การประกอบเลขที่ 5687)
2. ระยะห่างระหว่างช่วงเสาของโครงสร้างสายส่ง 115 kV ให้ดูแบบเลขที่ SA1-015/48001 (การประกอบเลขที่ 5151)
3. การประยุกต์ใช้งาน (โดยการปลดสายยึดโยงออก)
   3.1 ใช้ก่อสร้างในช่วงทางตรง กรณีที่มีปัญหาการหลุดของชุดพวงลูกถ้วยแขวน ออกจากคอนรับสายบ่อยครั้ง
   3.2 ใช้ก่อสร้างในช่วงทางโค้งไม่รับแรงดึง สำหรับกรณีมุมเบี่ยงเบนระหว่างเสา (θ) มีค่าไม่เกิน 10°

NOTES

1.* IN CASE OF CONSTRUCTING IN HIGHWAY AREA, USE THE VERTICAL CLEARANCE IN THE PARENTHESIS. FOR ADDITIONAL DETAIL, SEE DWG NO. SA1-015/43012 (ASSEMBLY NO. 5687) .
2. SPAN LENGTHS FOR 115 kV CONSTRUCTION STRUCTURE, SEE DWG. NO. SA1-015/48001 (ASSEMBLY NO. 5151) .
3. APPLICATION (TO OMIT THE GUYS)
   3.1 FOR TANGENT LINE CONSTRUCTING, IN CASE THE SET OF SUSPENSION INSULATOR IS OFTEN LETTED OUT FROM A CROSSARM .
   3.2 FOR SLACK SPAN ANGLE STRUCTURE, IN CASE THE LINE DEFLECTION ANGLE (θ) IS NOT MORE THAN 10° .

อติวิทย์ ทองลา ผชง.3 ผบ. กฟส.[illegible] กฟต.2 สายงาน (ต) ผวก. @PEA

กองมาตรฐานระบบไฟฟ้า
ฝ่ายมาตรฐานและความปลอดภัย

การไฟฟ้าส่วนภูมิภาค

ใช้แทนแบบ ....
ถูกแทนโดยแบบ ....

ผู้เขียน ...สมชาย...........
ผู้สำรวจ..................
วิศวกร..................
หัวหน้าแผนก..................
ผู้อำนวยการกอง..................
ผู้อำนวยการฝ่าย..................

ผู้ว่าการ.......................(แทน).............

เขียนเสร็จวันที่ 3 ม.ค. 2549
แก้แบบวันที่ ....
มิติเป็น..................
มาตราส่วน...............

115 kV วงจรเดี่ยว สายไฟฟ้าเดี่ยว
เสา คอร. (ชนิดมีกราวด์เพลทในเสา)
สำหรับทางโค้ง ต่อจากต้นเขาปลายสายสองข้าง
แบบ SS-SA-4

รองผู้ว่าการฝ่ายวางแผนและพัฒนาระบบไฟฟ้า
.........(แทน).

115 kV SINGLE CIRCUIT SINGLE CONDUCTOR
CONCRETE POLE (WITH GROUND PLATE IN POLE)
ANGLE STRUCTURE ADJACENT TO DOUBLE DEADEND STRUCTURE
TYPE SS-SA-4

แบบเลขที่ SA1-015/49004
แผ่นที่ 4 ของจำนวน 4 แผ่น