

การประกอบเลขที่ ASSEMBLY NO. 5687 B

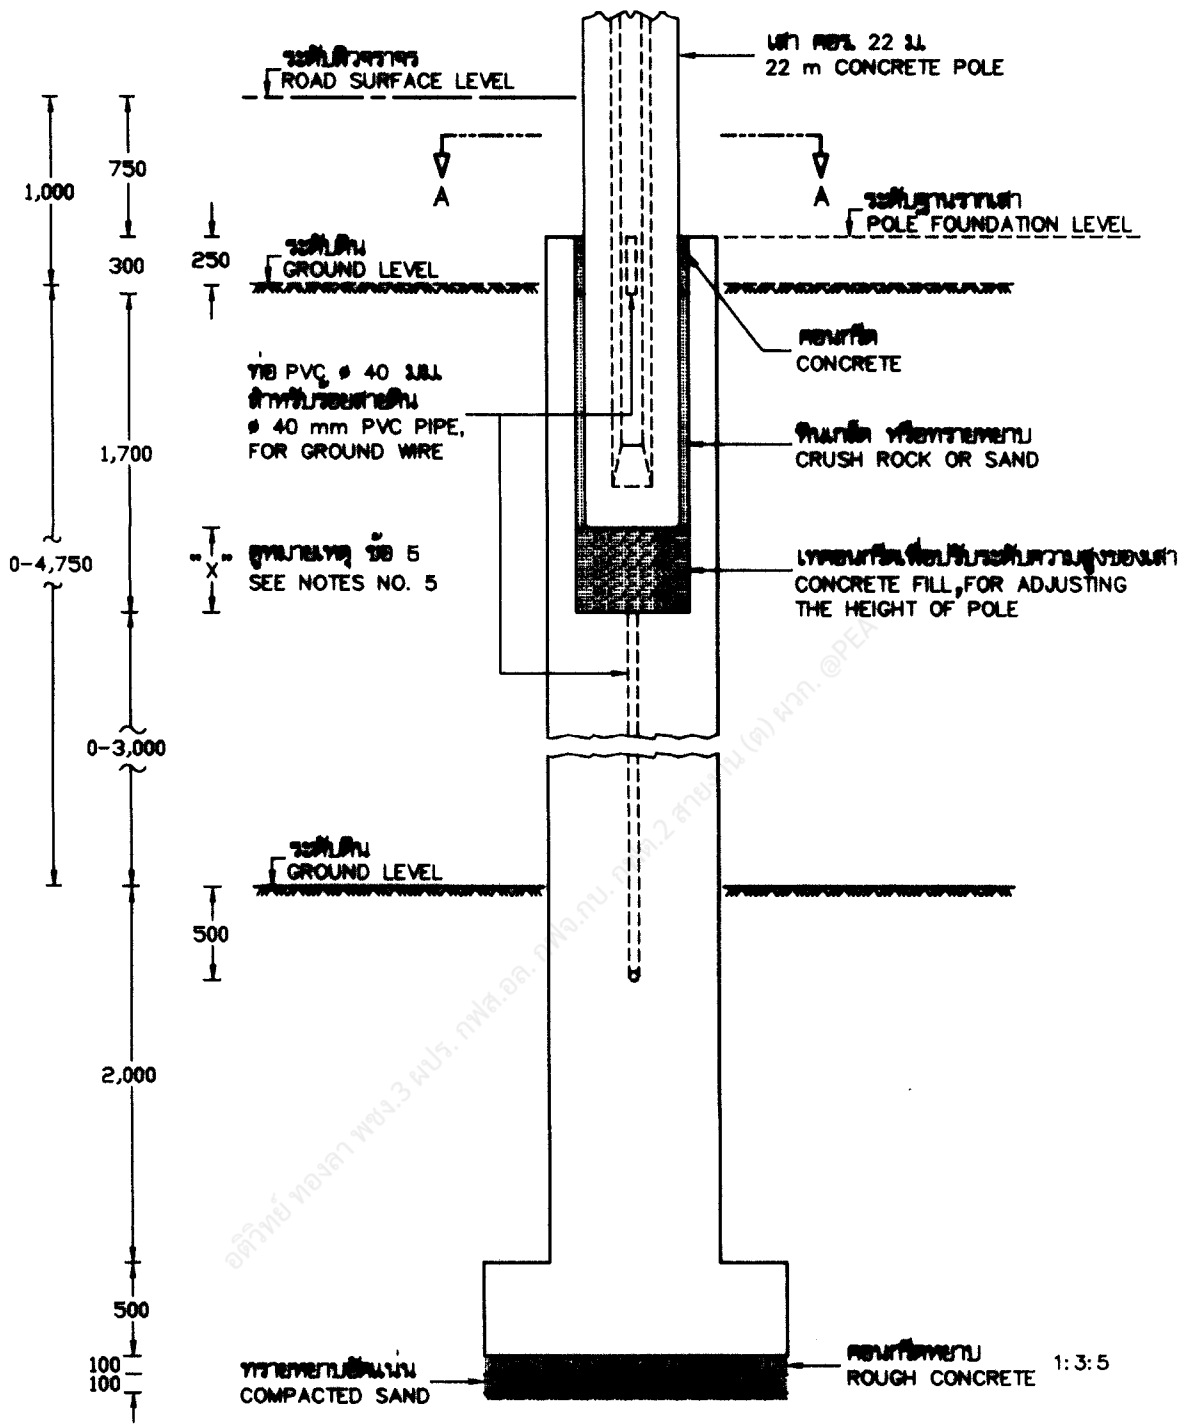

กองมาตรฐานระบบไฟฟ้า ฝ่ายมาตรฐานและความปลอดภัย	การไฟฟ้าส่วนภูมิภาค	ใช้แทนแบบ SA1-015/45011 ถูกแทนโดยแบบ .....
ผู้เขียน	ผู้ว่าการ	เขียนเสร็จวันที่ 10 มิ.ย. 2547
ผู้ตรวจ		แก้แบบวันที่ .....
วิศวกร	รายละเอียดที่ 10A 23 ก.ย. 2547	มิติเป็น มิลลิเมตร
หัวหน้าแผนก	ฐานราเสา (แบบที่ 18)	มาตราส่วน 1:40
ผู้อำนวยการกอง		
ผู้อำนวยการฝ่าย		
.....	DETAIL 10A POLE FOUNDATION (TYPE 18)	แบบเลขที่ SA1-015/47019 แผ่นที่ 1 ของจำนวน 2 แผ่น

23 ก.ย. 2547

การประกอบเลขที่ ASSEMBLY NO.	5687 B

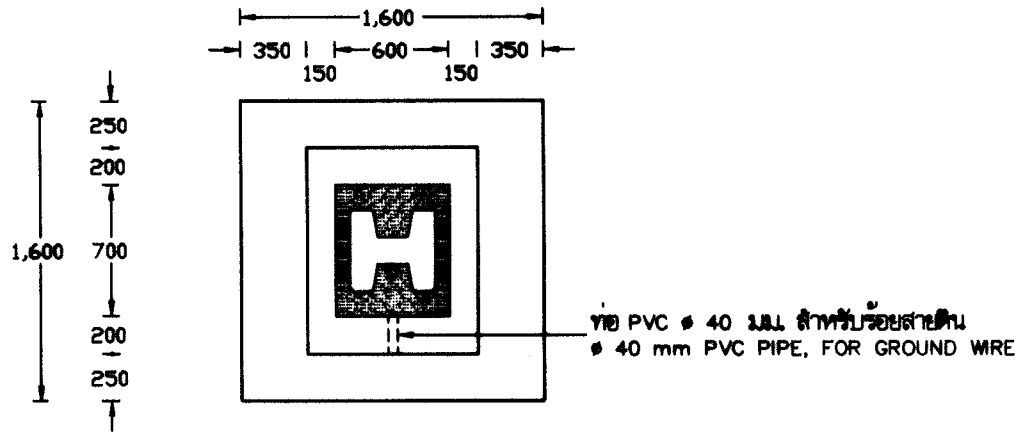

รูปตัด
SECTION A–A

หมายเหตุ

1 ฐานรากนี้ใช้ในการออกแบบสามารถรับน้ำหนักปลอดภัยได้ตั้งแต่ 12 ตัน / ตารางเมตรขึ้นไป
2 ใช้ในการเดินทางตรงหรือทางโค้ง ที่มีและไม่มีสายยึดโยง (กรณีพื้นที่ก่อสร้างฐานรากสามารถขุดได้ต่ำกว่าระดับผิวจราจร 1.00 - 5.75 ม.)
3 รายละเอียดเพิ่มเติมใน แบบเลขที่ IB2-011/44011
4 ดูข้อกำหนดการติดตั้งฐานรากเสาในบริเวณทางหลวง ตามแบบเลขที่ SA1-015/43012 (การประกอบเลขที่ 5687)
5 ระยะ "X"= 450 มม. สำหรับการก่อสร้างฐานรากเสาในพื้นที่ทางหลวงที่ไม่มีทางเท้า ส่วนพื้นที่อื่นๆ ระยะ "X"= 0 มม.

NOTES

1 THIS FOUNDATION IS USED IN CASE ALLOWABLE SOIL BEARING CAPACITY OF 12 TON/m^2 OR MORE .
2 USE FOR STRAIGHT OR ANGLE LINE WITH AND WITHOUT GUY (IN CASE OF GROUND SURFACE LEVEL IS BETWEEN 1.00–5.75 m LOWER THAN ROAD SURFACE LEVEL) .
3 SEE ADDITIONAL DETAIL, DWG. NO. IB2-011/44011 .
4 SEE RECOMMENDATION FOR POLE FOUNDATION INSTALLATION IN HIGHWAY AREA, DWG. NO. SA1-015/43012 (ASSEMBLY NO. 5687) .
5 THE "X" IS 450 mm HEIGHT FOR FOUNDATION CONSTRUCTION IN HIGHWAY AREA WHICH HAVE NO PAVEMENT, OTHER AREA THE "X" IS ZERO .

กองมาตรฐานระบบไฟฟ้า ฝ่ายมาตรฐานและความปลอดภัย	การไฟฟ้าส่วนภูมิภาค	ใช้แทนแบบ SA1-015/45011 ถูกแทนโดยแบบ .....
ผู้เขียน	ผู้ว่าการ	เขียนเสร็จวันที่ 10 มิ.ย. 2547
ผู้สำรวจ		แก้แบบวันที่ .....
วิศวกร	รายละเอียดที่ 10A 23 มิ.ย. 2547	มีเป็น มิลลิเมตร
หัวหน้าแผนก	ฐานรากเสา (แบบที่ 18)	มาตราส่วน 1:40
ผู้อำนวยการกอง		
ผู้อำนวยการฝ่าย		
รองผู้ว่าการวางแผนและพัฒนาระบบไฟฟ้า	DETAIL 10A POLE FOUNDATION (TYPE 18)	แบบเลขที่ SA1-015/47019 แผ่นที่ 2. ของจำนวน 2. แผ่น

23 มิ.ย. 2547