
การประกอบเลขที่ ASSEMBLY NO. 0206

N — สายเป็นกลาง NEUTRAL LINE

A,B,C — สายเฟส PHASE LINE

L — สายดับไฟถนน STREET LIGHTING LINE

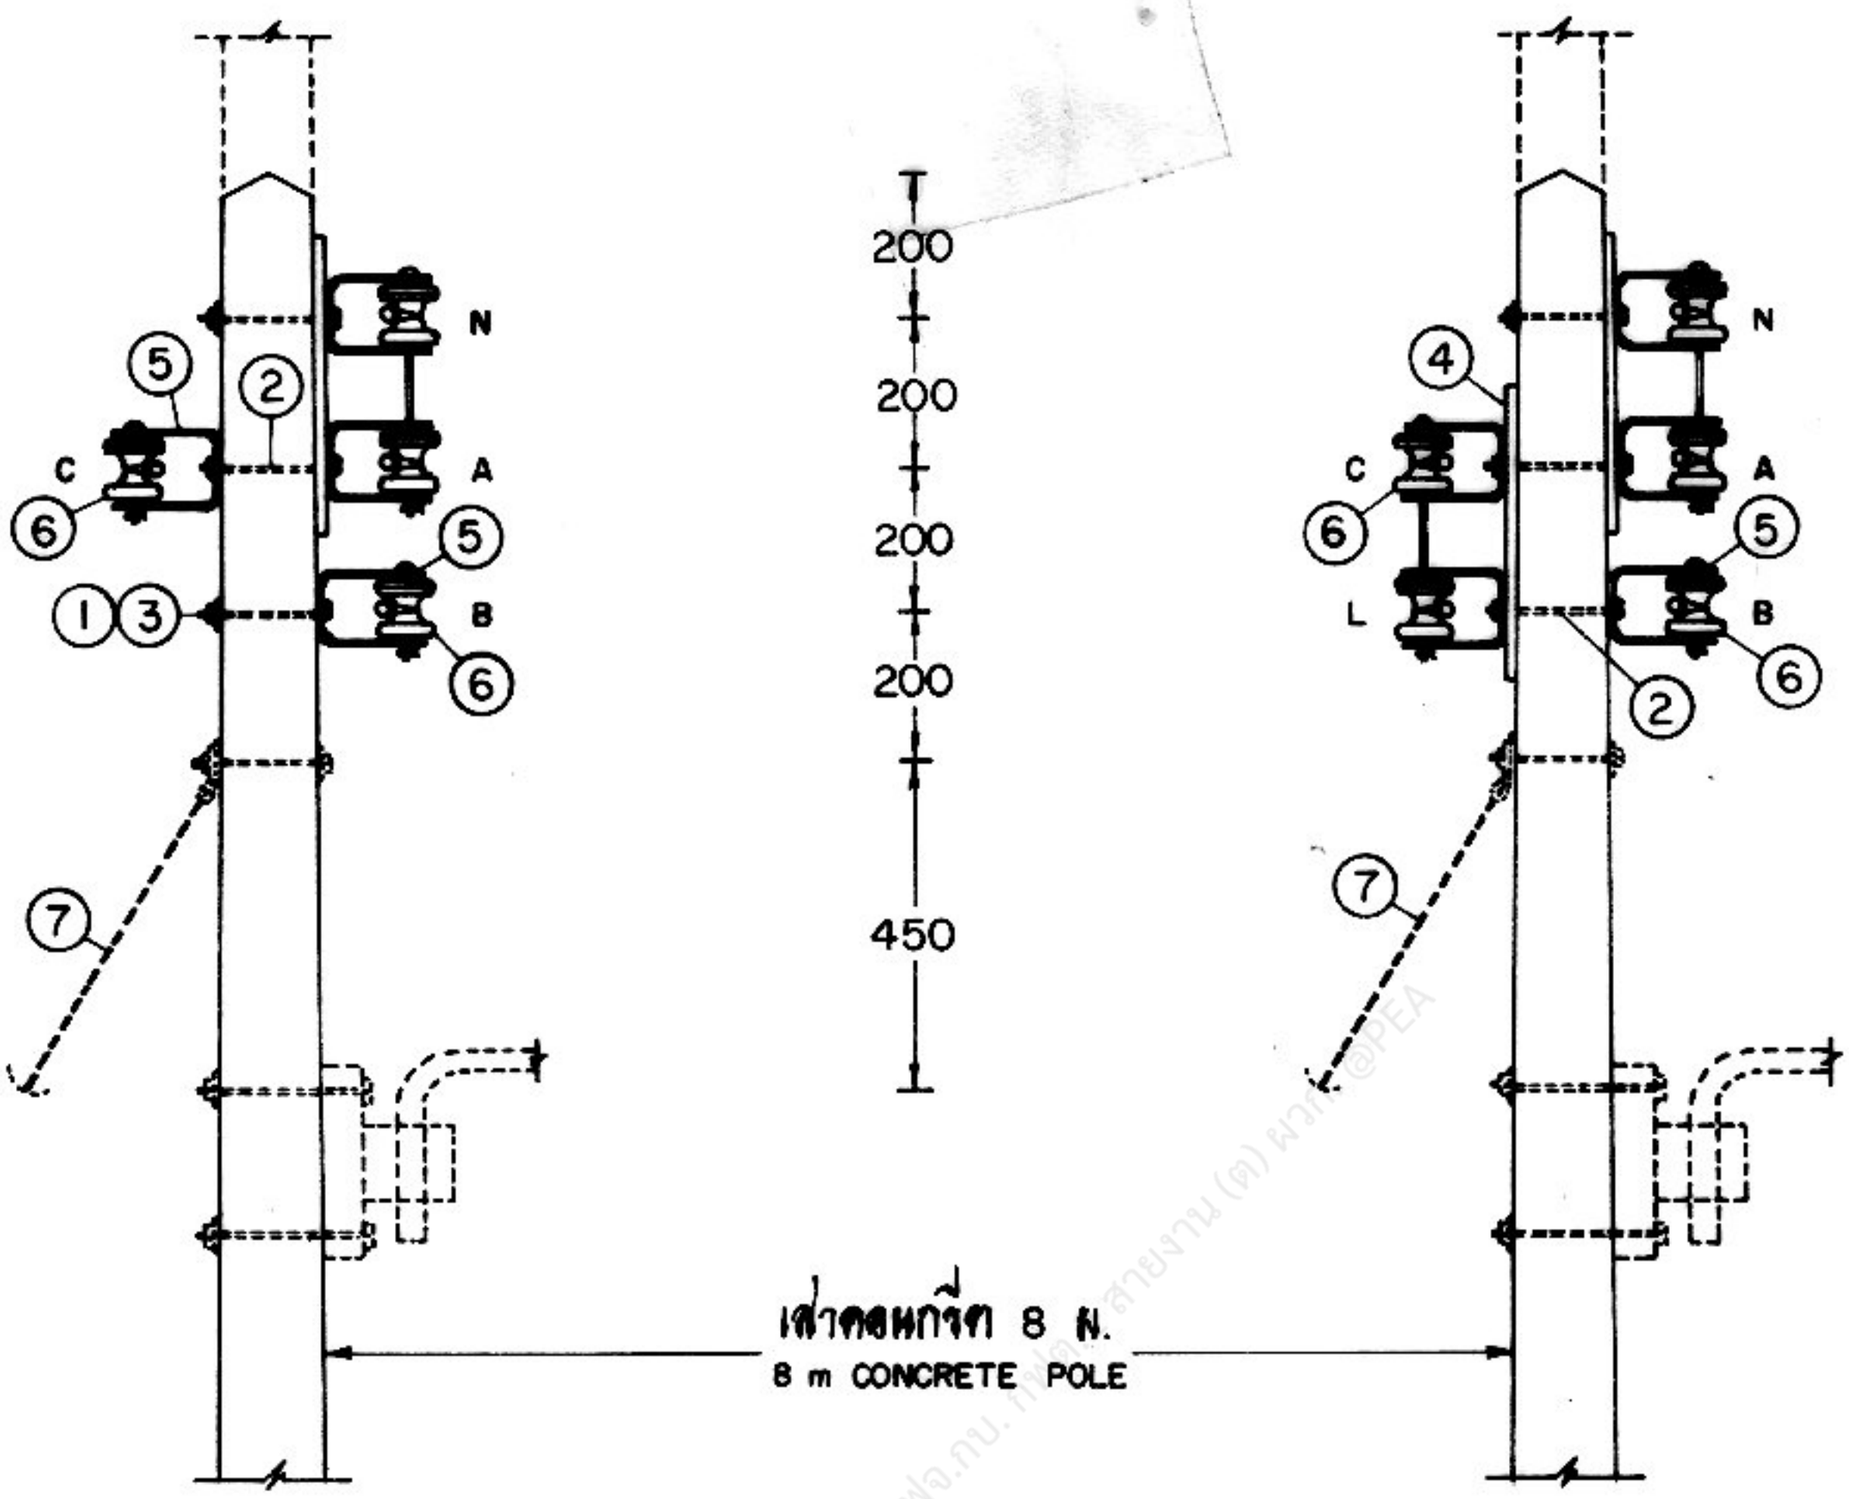


① สำหรับปรับปรุงระบบจำหน่ายแรงต่ำ 1 เฟส 2 สาย เป็นระบบจำหน่ายแรงต่ำ 3 เฟส 4 สาย
FOR DEVELOPING 1-PHASE 2-WIRE L.T. DISTRIBUTION LINE INTO 3-PHASE 4-WIRE SYSTEM.

② สำหรับปรับปรุงระบบจำหน่ายแรงต่ำ 1 เฟส 2 สาย เป็นระบบจำหน่ายแรงต่ำ 3 เฟส 4 สาย พร้อมสายดับไฟถนน
FOR DEVELOPING 1-PHASE 2-WIRE L.T. DISTRIBUTION LINE INTO 3-PHASE 4-WIRE SYSTEM WITH STREET LIGHTING LINE.

กองวิศวกรรมไฟฟ้าและเครื่องกล ฝ่ายวิศวกรรม	การไฟฟ้าส่วนภูมิภาค	ใช้แทนแบบ ..... ถูกแทนโดยแบบ ..... เขียนเสร็จวันที่ 25 ต.ค. 22 แก้แบบวันที่ ..... มิติเป็น มม. มาตราส่วน 1 : 20
ผู้เขียน ..... ผู้สำรวจ ..... วิศวกร ..... หัวหน้าแผนก ..... หัวหน้ากอง ..... ผู้อำนวยการฝ่าย ..... รองผู้ว่าการฝ่ายเทคนิค	ผู้ว่าการ ..... ต.ค. 2522 การติดตั้งแร็คแรงต่ำกับเสาคอนกรีต 8 ม. สำหรับปรับปรุงระบบจำหน่ายแรงต่ำเป็น 3 เฟส 4 สาย	
	SECONDARY RACK INSTALLATION ON 8 m CONCRETE POLE FOR DEVELOPING L.T. DISTRIBUTION LINE INTO 3-PHASE 4-WIRE	แบบแสดงที่ SAI-015/22049 แผ่นที่ 1 ของจำนวน 3 แผ่น

30 ต.ค. 2522

การประกอบเลขที่ ASSEMBLY NO. 0206

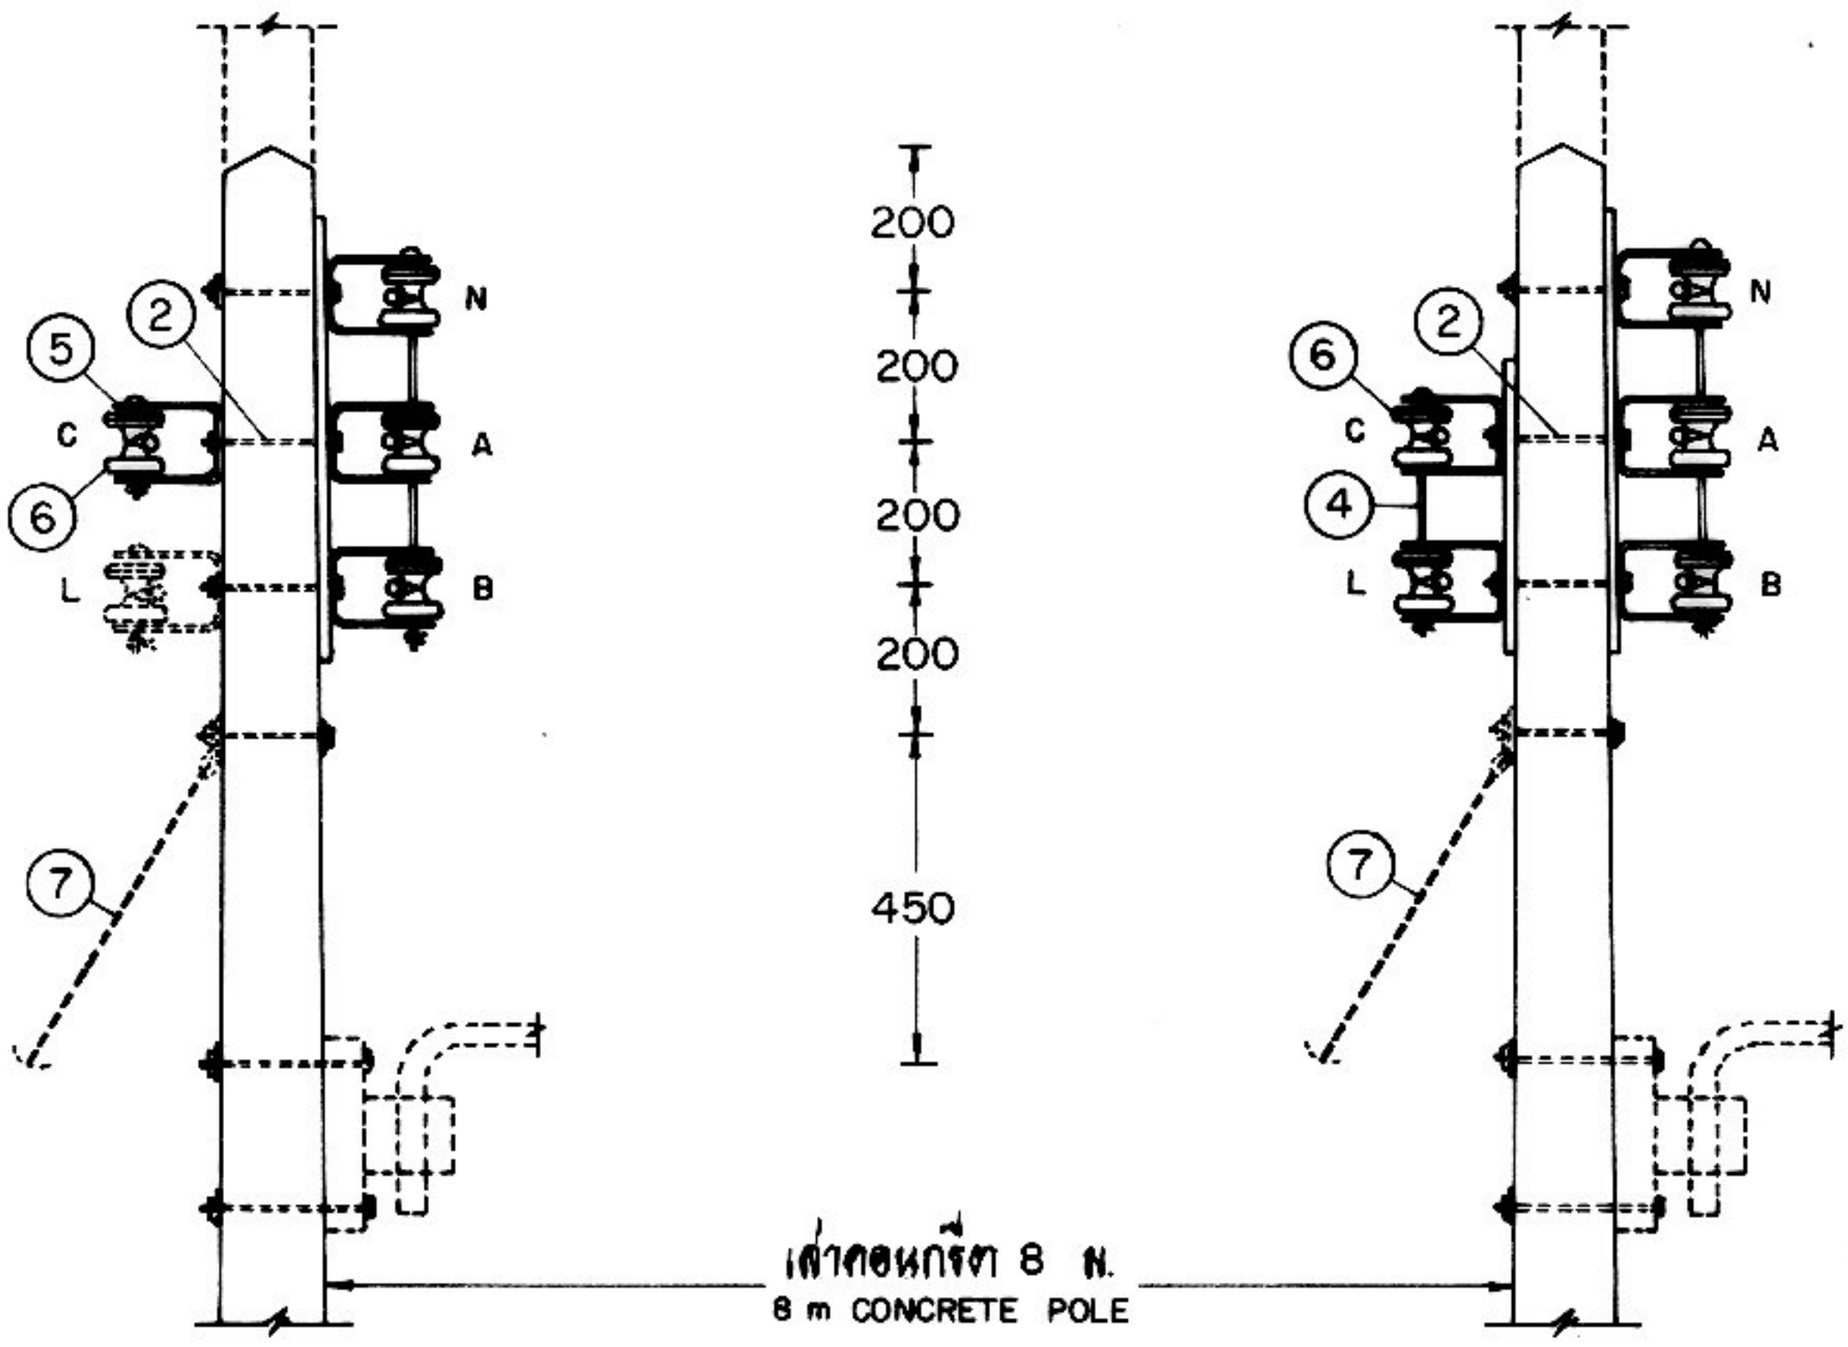

เสาคอนกรีต 8 ม.
8 m CONCRETE POLE

(3) สำหรับปรับปรุงระบบจำหน่ายแรงต่ำ 1 เฟส 3 สาย ที่มีหรือไม่มีสายดับไฟถนน เป็นระบบจำหน่ายแรงต่ำ 3 เฟส 4 สาย

FOR DEVELOPING 1-PHASE 3-WIRE L.T. DISTRIBUTION LINE WITH OR WITHOUT STREET LIGHTING LINE INTO 3-PHASE 4-WIRE SYSTEM.

(4) สำหรับปรับปรุงระบบจำหน่ายแรงต่ำ 1 เฟส 3 สาย ที่ไม่มีสายดับไฟถนน เป็นระบบจำหน่ายแรงต่ำ 3 เฟส 4 สาย พร้อมสายดับไฟถนน

FOR DEVELOPING 1-PHASE 3-WIRE L.T. DISTRIBUTION LINE WITHOUT STREET LIGHTING LINE INTO 3-PHASE 4-WIRE SYSTEM WITH STREET LIGHTING LINE.

ข้อกำหนดการใช้งาน

1. แบบนี้ให้ก่อสร้างเฉพาะกรณีต้องการปรับปรุงระบบจำหน่ายแรงต่ำ ที่เสาคอนกรีต 8 ม. เป็น 3 เฟส 4 สาย เท่านั้น
2. ระยะห่างระหว่างช่วงเสาสูงสุด ไม่เกิน 40 ม.
3. สำหรับการเข้าปลายสายที่เสาต้นสุดท้าย อนุโลมให้ก่อสร้างเช่นเดียวกับกรณีเสาคอนกรีต 9 ม. ตามแบบเลขที่ SAI-015/21045 (การประกอบเลขที่ 0209)

RECOMMENDATION

1. THIS CONSTRUCTION IS USED FOR DEVELOPING L.T. DISTRIBUTION LINE ON 8 m CONCRETE POLE INTO 3-PHASE 4-WIRE SYSTEM ONLY.
2. THE MAXIMUM SPAN LENGTH DO NOT EXCEED 40 m.
3. FOR DEAD END STRUCTURE, CONSTRUCT AS THE 9 m CONCRETE POLE ACCORDING TO DWG. NO. SAI-015/21045 (ASS, NO. 0209)

รองวิศวกรรมไฟฟ้าและเครื่องกล ฝ่ายวิศวกรรม	การไฟฟ้าส่วนภูมิภาค	ใช้แทนแบบ ..... ถูกแทนโดยแบบ ..... เขียนเสร็จวันที่ 25 ต.ค. 22 แก้แบบวันที่ ..... มิติเป็น มม. มาตราส่วน 1 : 20
ผู้เขียน ..... ผู้สำรวจ ..... วิศวกร ..... หัวหน้าแผนก ..... หัวหน้ากอง ..... ผู้อำนวยการฝ่าย	ผู้ว่าการ ..... 1 ก.ค. 2522	
รองผู้ว่าการฝ่ายเทคนิค	การติดตั้งแร็คแรงต่ำกับเสาคอนกรีต 8 ม. สำหรับปรับปรุงระบบจำหน่ายแรงต่ำเป็น 3 เฟส 4 สาย SECONDARY RACK INSTALLATION ON 8 m CONCRETE POLE FOR DEVELOPING L.T. DISTRIBUTION LINE INTO 3-PHASE 4-WIRE	แบบเลขที่ SAI-015/22049 แต่นที่ 2 ของจำนวน 3 แต่น

30 ต.ค. 2522

การประกอบเลขที่ ASSEMBLY NO. 0206

บัญชีวัสดุ
BILL OF MATERIAL

ลำดับที่ ITEM	รายละเอียด DESCRIPTION	จำนวน REQ'D 1	2	3	4	วัสดุเลขที่ MAT. NO.
1	สลักเกลียว M 16 X 170 มม. BOLT, MACHINE, M 16 X 170 mm	1	-	-	-	01110201
1 a	สลักเกลียว M 16 X 250 มม. สำหรับเสาคอนกรีต 12 ม. BOLT, MACHINE, M 16 X 250 mm FOR 12 m CONCRETE POLE	1	-	-	-	01110203
2	สลักเกลียว M 16 X 200 มม. BOLT, MACHINE, M 16 X 200 mm	1	2	1	2	01110202
2a	สลักเกลียว M 16 X 300 มม. สำหรับเสาคอนกรีต 12 ม. BOLT, MACHINE, M 16 X 300 mm FOR 12 m CONCRETE POLE	1	2	1	2	01110204
3	แหวนสี่เหลี่ยมแบน 52 X 52 X 4.5มม. รู Ø 18 มม. มอก. 258 WASHER, SQUARE FLAT 52 X 52 X 4.5mm HOLE Ø 18 mm, TIS 258	1	-	-	-	01180100
4	แร็ค 2 X 200 มม. แบบหลังยื่น RACK, SECONDARY, MEDIUM PRESSED STEEL 2 X 200 mm EXT. BACK	-	1	-	1	03130000
5	ที่จับลูกถ้วยสำหรับลูกถ้วย มอก. 227 (แมม 53-2) CLEVIS, FLAT STEEL, FOR INSULATOR, TIS 227 (CLASS 53-2)	2	1	1	-	03130001
6	ลูกถ้วยแรงต่ำ มอก. 227 แมม ข (แมม 53-2) INSULATOR, SPOOL TYPE, L.T., TIS 227, TYPE B (CLASS 53-2)	2	3	1	2	03030000
7	การประกอบสายยึดโยง GY-01 พร้อมสลักเกลียว M 16 X 170 มม. และแหวนสี่เหลี่ยมแบน 52X52X4.5 มม. สำหรับเสาคอนกรีต 8 ม. กรณีทางโค้ง 5°-60° GUY ASSEMBLY GY-01 COMPLETE WITH M 16 X 170 mm MACHINE BOLT & 52X52X4.5 mm SQUARE WASHER FOR 5°-60° ANGLE STRUCTURE WHICH INSTALL ON 8 m CONCRETE POLE	1	1	1	1	01110201 01180100
7 a	การประกอบสายยึดโยง GY-02 พร้อมสลักเกลียว M 16 X 250 มม. และแหวนสี่เหลี่ยมแบน 52X52X4.5 มม. สำหรับเสาคอนกรีต 12 ม. กรณีทางโค้ง 30°-60° GUY ASSEMBLY GY-02 COMPLETE WITH M 16 X 250 mm MACHINE BOLT & 52X52X4.5 mm SQUARE WASHER FOR 30°-60° ANGLE STRUCTURE WHICH INSTALL ON 12 m CONCRETE POLE	1	1	1	1	01110203 01180100

หมายเหตุ บัญชีวัสดุข้างต้น แสดงเฉพาะจำนวนวัสดุที่เพิ่มขึ้นในการปรับปรุงระบบจำหน่าย เป็นระบบ 3 เฟส 4 สาย

NOTE THE ABOVE BILL OF MATERIAL SHOW THE ADDITIONAL MATERIAL FOR DEVELOPING THE DISTRIBUTION LINE INTO 3-PHASE 4-WIRE SYSTEM ONLY .

กองวิศวกรรมไฟฟ้าและเครื่องกล ฝ่ายวิศวกรรม	การไฟฟ้าส่วนภูมิภาค	ใช้แทนแบบ ถูกแทนโดยแบบ
ผู้เขียน ผู้สำรวจ วิศวกร หัวหน้าแผนก หัวหน้ากอง ผู้อำนวยการฝ่าย รองผู้ว่าการฝ่ายเทคนิค	ผู้ว่าการ 1 ต.ค. 2522 การติดตั้งแร็คแรงต่ำกับเสาคอนกรีต 8 ม. สำหรับปรับปรุงระบบจำหน่ายแรงต่ำเป็น 3 เฟส 4 สาย SECONDARY RACK INSTALLATION ON 8 m CONCRETE POLE FOR DEVELOPING L.T. DISTRIBUTION LINE INTO 3-PHASE 4-WIRE	เขียนเสร็จวันที่ 25 ต.ค. 22 แก้แบบวันที่ มิติเป็น มาตราส่วน แบบเลขที่ SAI-015/22049 แผ่นที่ 3 ของจำนวน 3 แผ่น

30 ต.ค. 2522