การประกอบเลขที่
ASSEMBLY NO. 3239

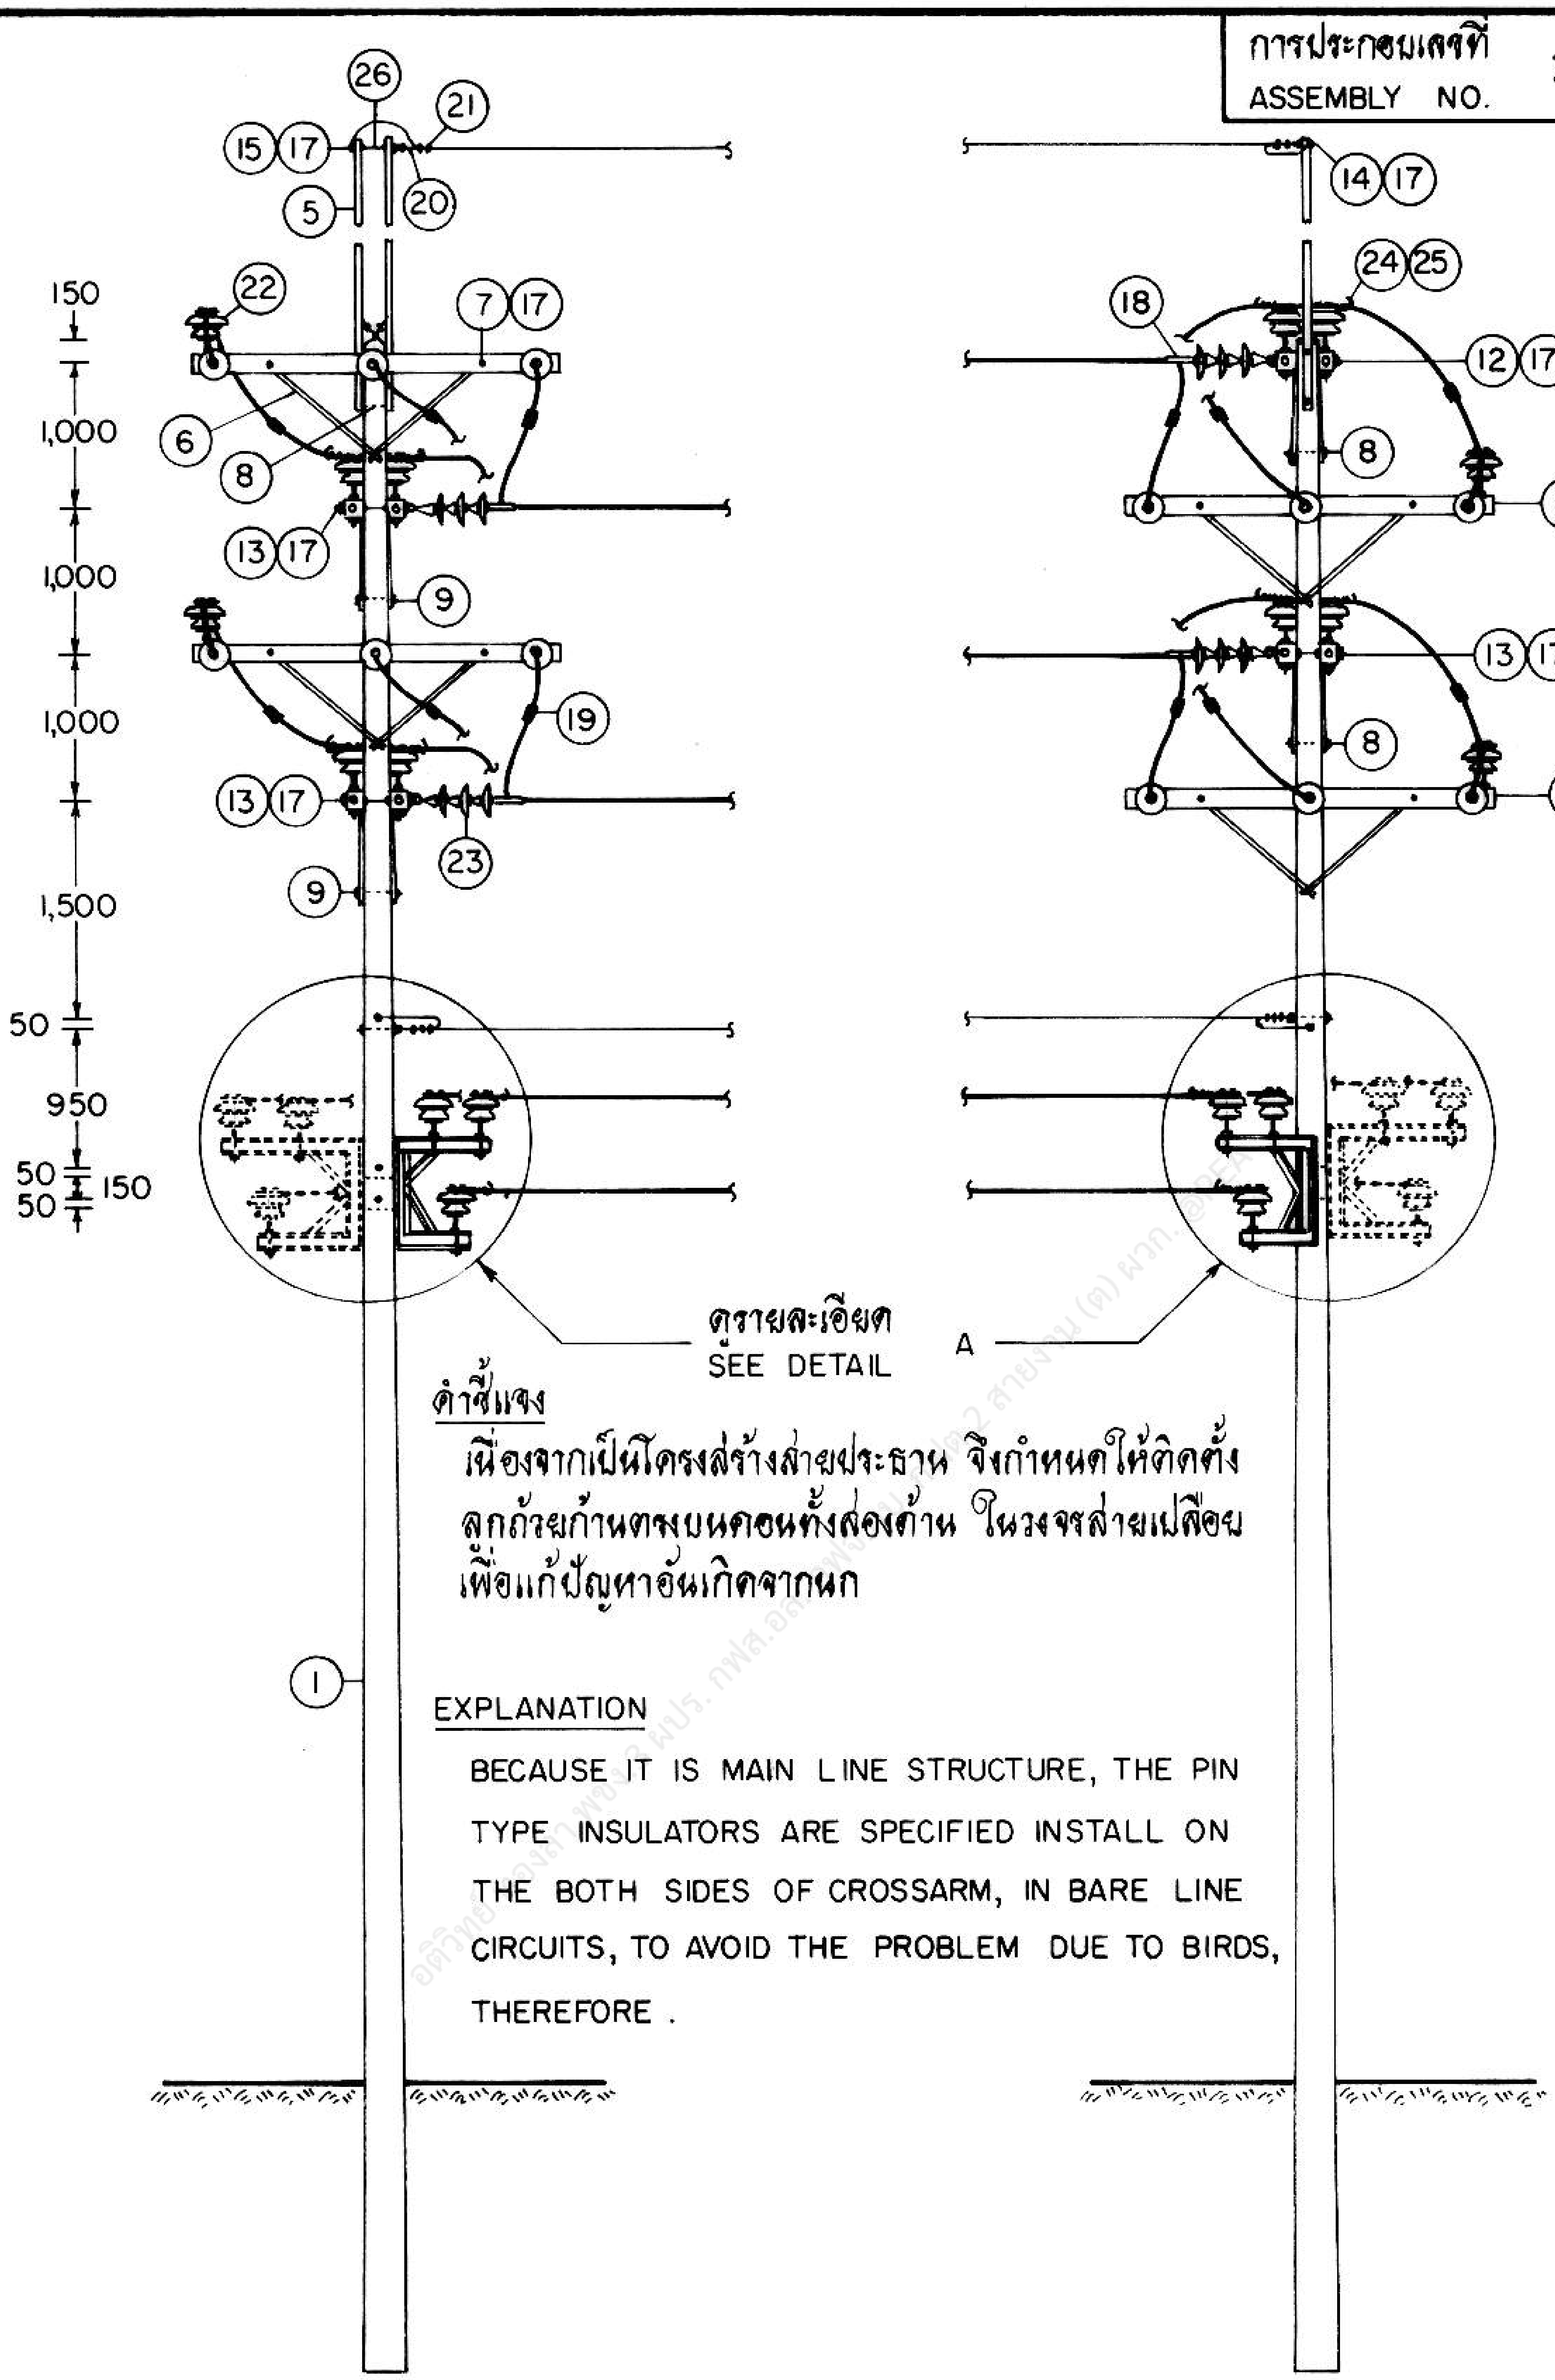

26
21
15 17
20
5
14 17
150
22
7 17
24 25
18
12 17
1,000
6
8
8
13 17
2
1,000
9
13 17
1,000
19
8
13 17
2
23
1,500
9
50
950
50
50
150
ดูรายละเอียด
SEE DETAIL
A
1

คำชี้แจง

เนื่องจากเป็นโครงสร้างสายประธาน จึงกำหนดให้ติดตั้งลูกถ้วยก้านตรงบนคอนทั้งสองด้าน ในวงจรสายเปลือย เพื่อแก้ปัญหาอันเกิดจากนก

EXPLANATION

BECAUSE IT IS MAIN LINE STRUCTURE, THE PIN TYPE INSULATORS ARE SPECIFIED INSTALL ON THE BOTH SIDES OF CROSSARM, IN BARE LINE CIRCUITS, TO AVOID THE PROBLEM DUE TO BIRDS, THEREFORE .

กองวิศวกรรมไฟฟ้าและเครื่องกล
ฝ่ายวิศวกรรม

ผู้เขียน
ผู้สำรวจ
วิศวกร
หัวหน้าแผนก
ผู้อำนวยการกอง
ผู้อำนวยการฝ่าย

รองผู้ว่าการฝ่ายเทคนิค

การไฟฟ้าส่วนภูมิภาค

ผู้ว่าการ 29 ต ค 35

โครงสร้างเสาต้นทางโค้ง ระบบ 33 kV, มุม 60°-90°
3 - 4 วงจร

33 kV ANGLE STRUCTURE, LINE ANGLE 60°-90°
3 - 4 CIRCUIT

ใช้แทนแบบ
ถูกแทนโดยแบบ
เขียนเสร็จวันที่ 13 ต.ค. 35
แก้แบบวันที่
มิติเป็น มิลลิเมตร
มาตราส่วน 1 : 75
แบบเลขที่ SA4-015/35012
แผ่นที่ 1 ของจำนวน 6 แผ่น

26 ต.ค. 2535

การประกอบเลขที่ ASSEMBLY NO.	3239

วัสดุลำดับที่
MAT. NO. ④

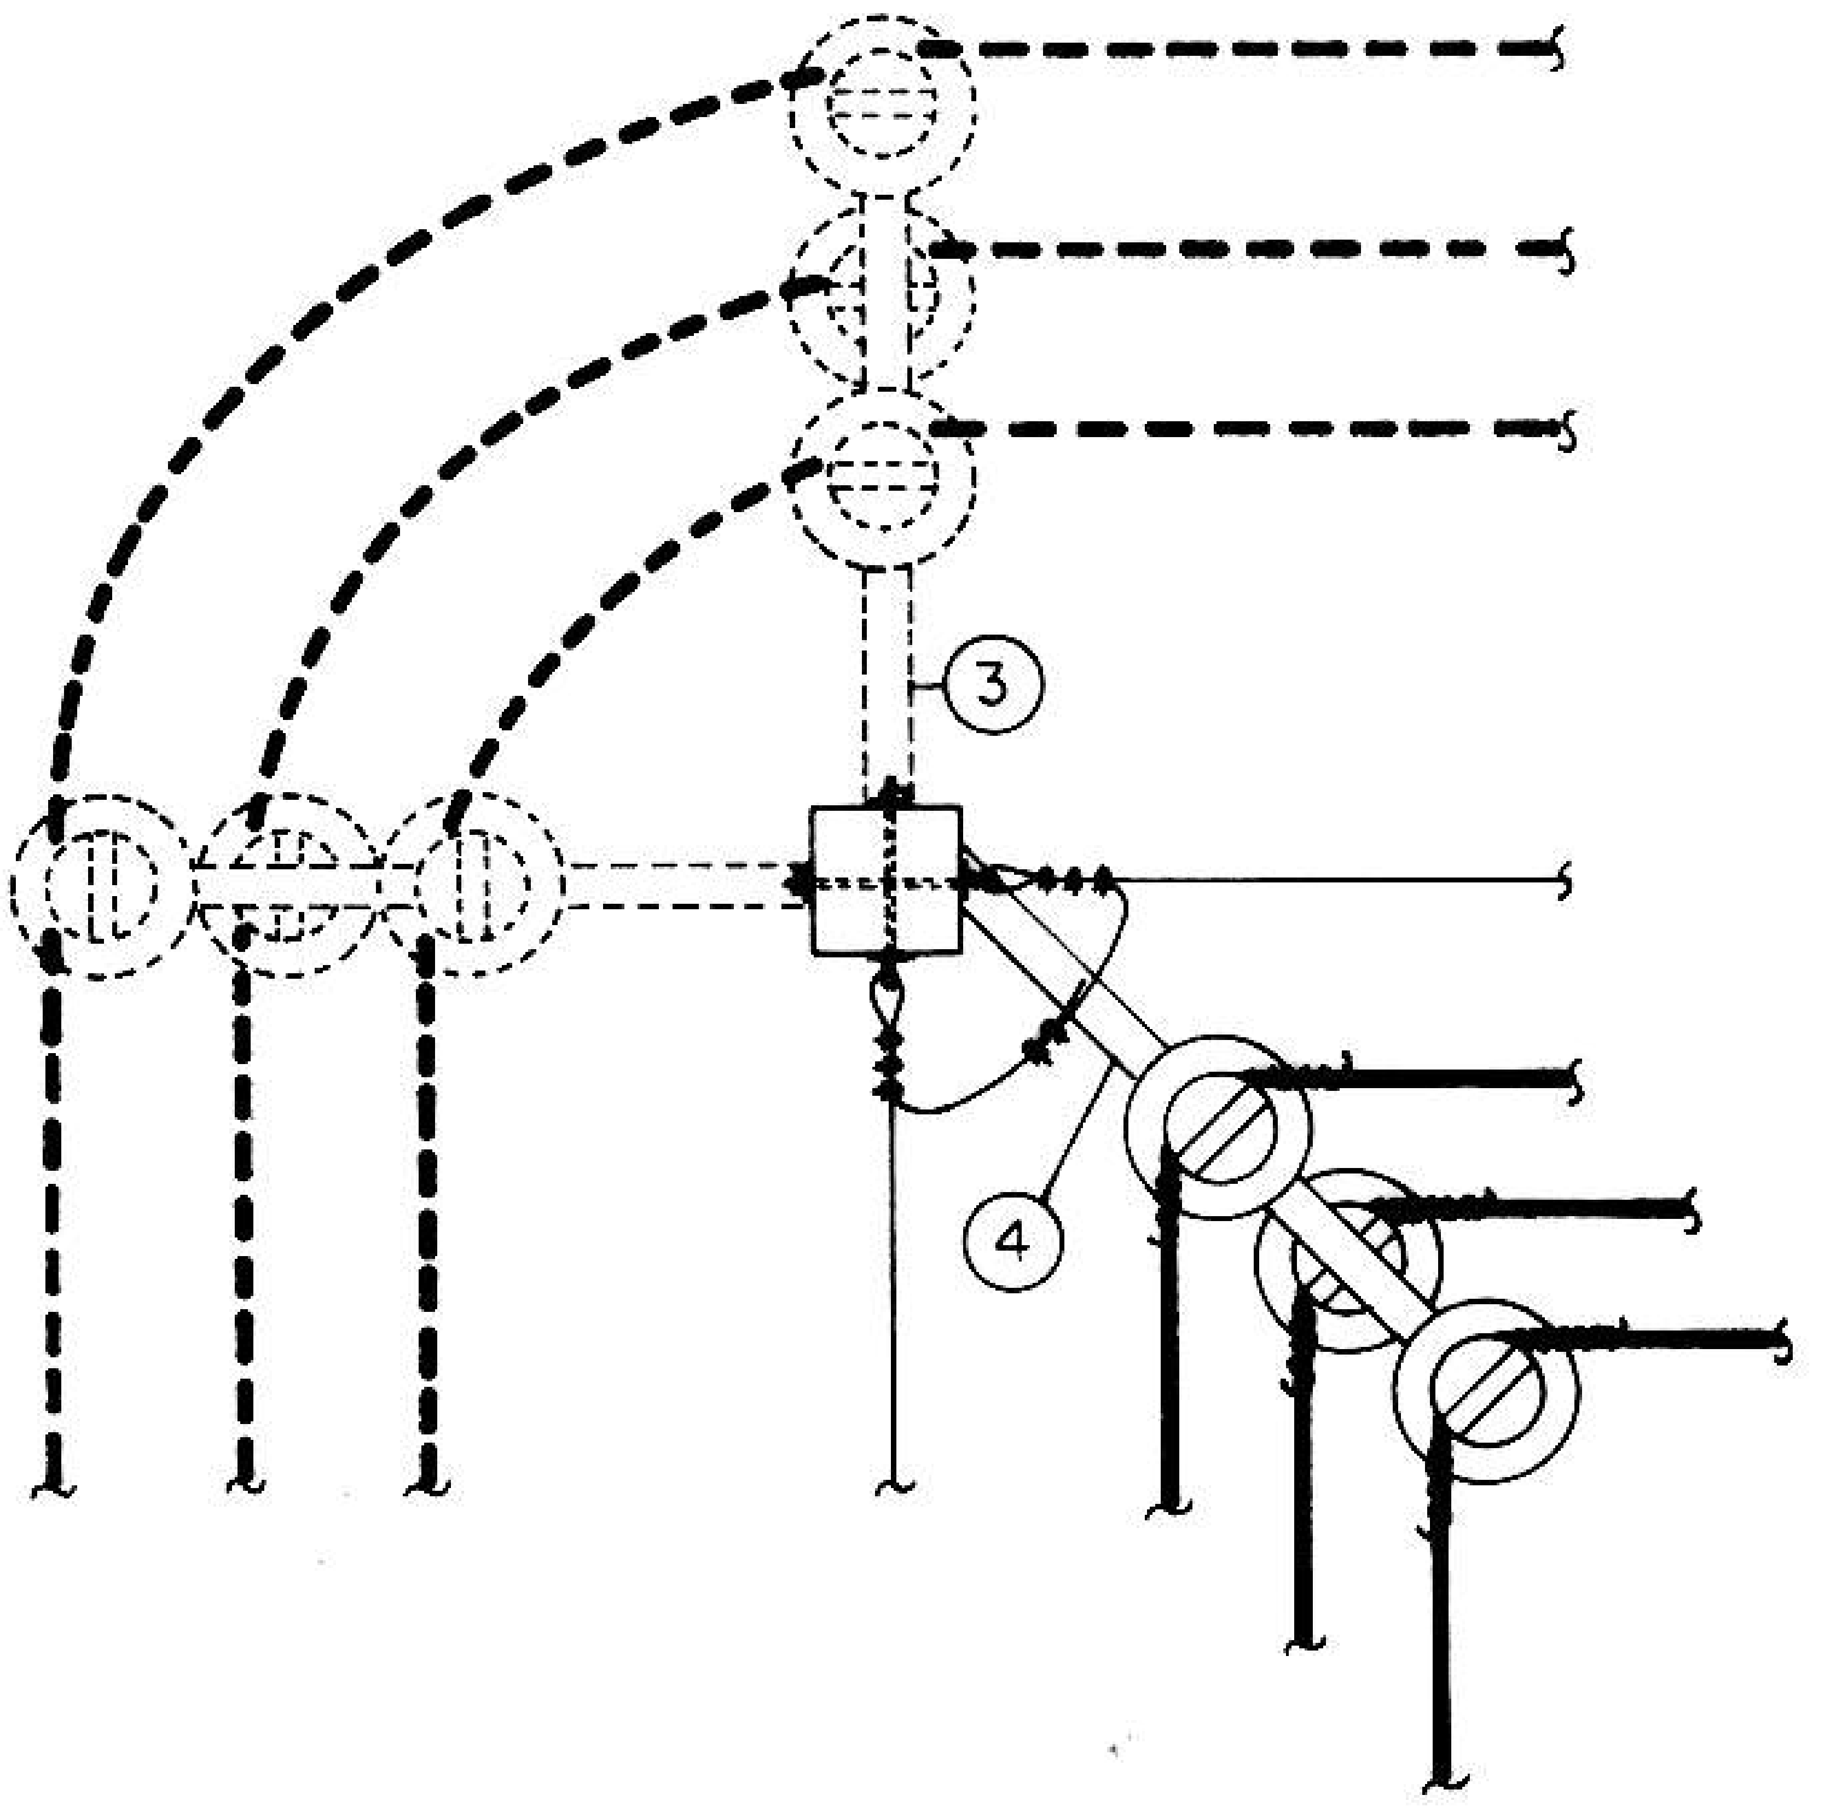

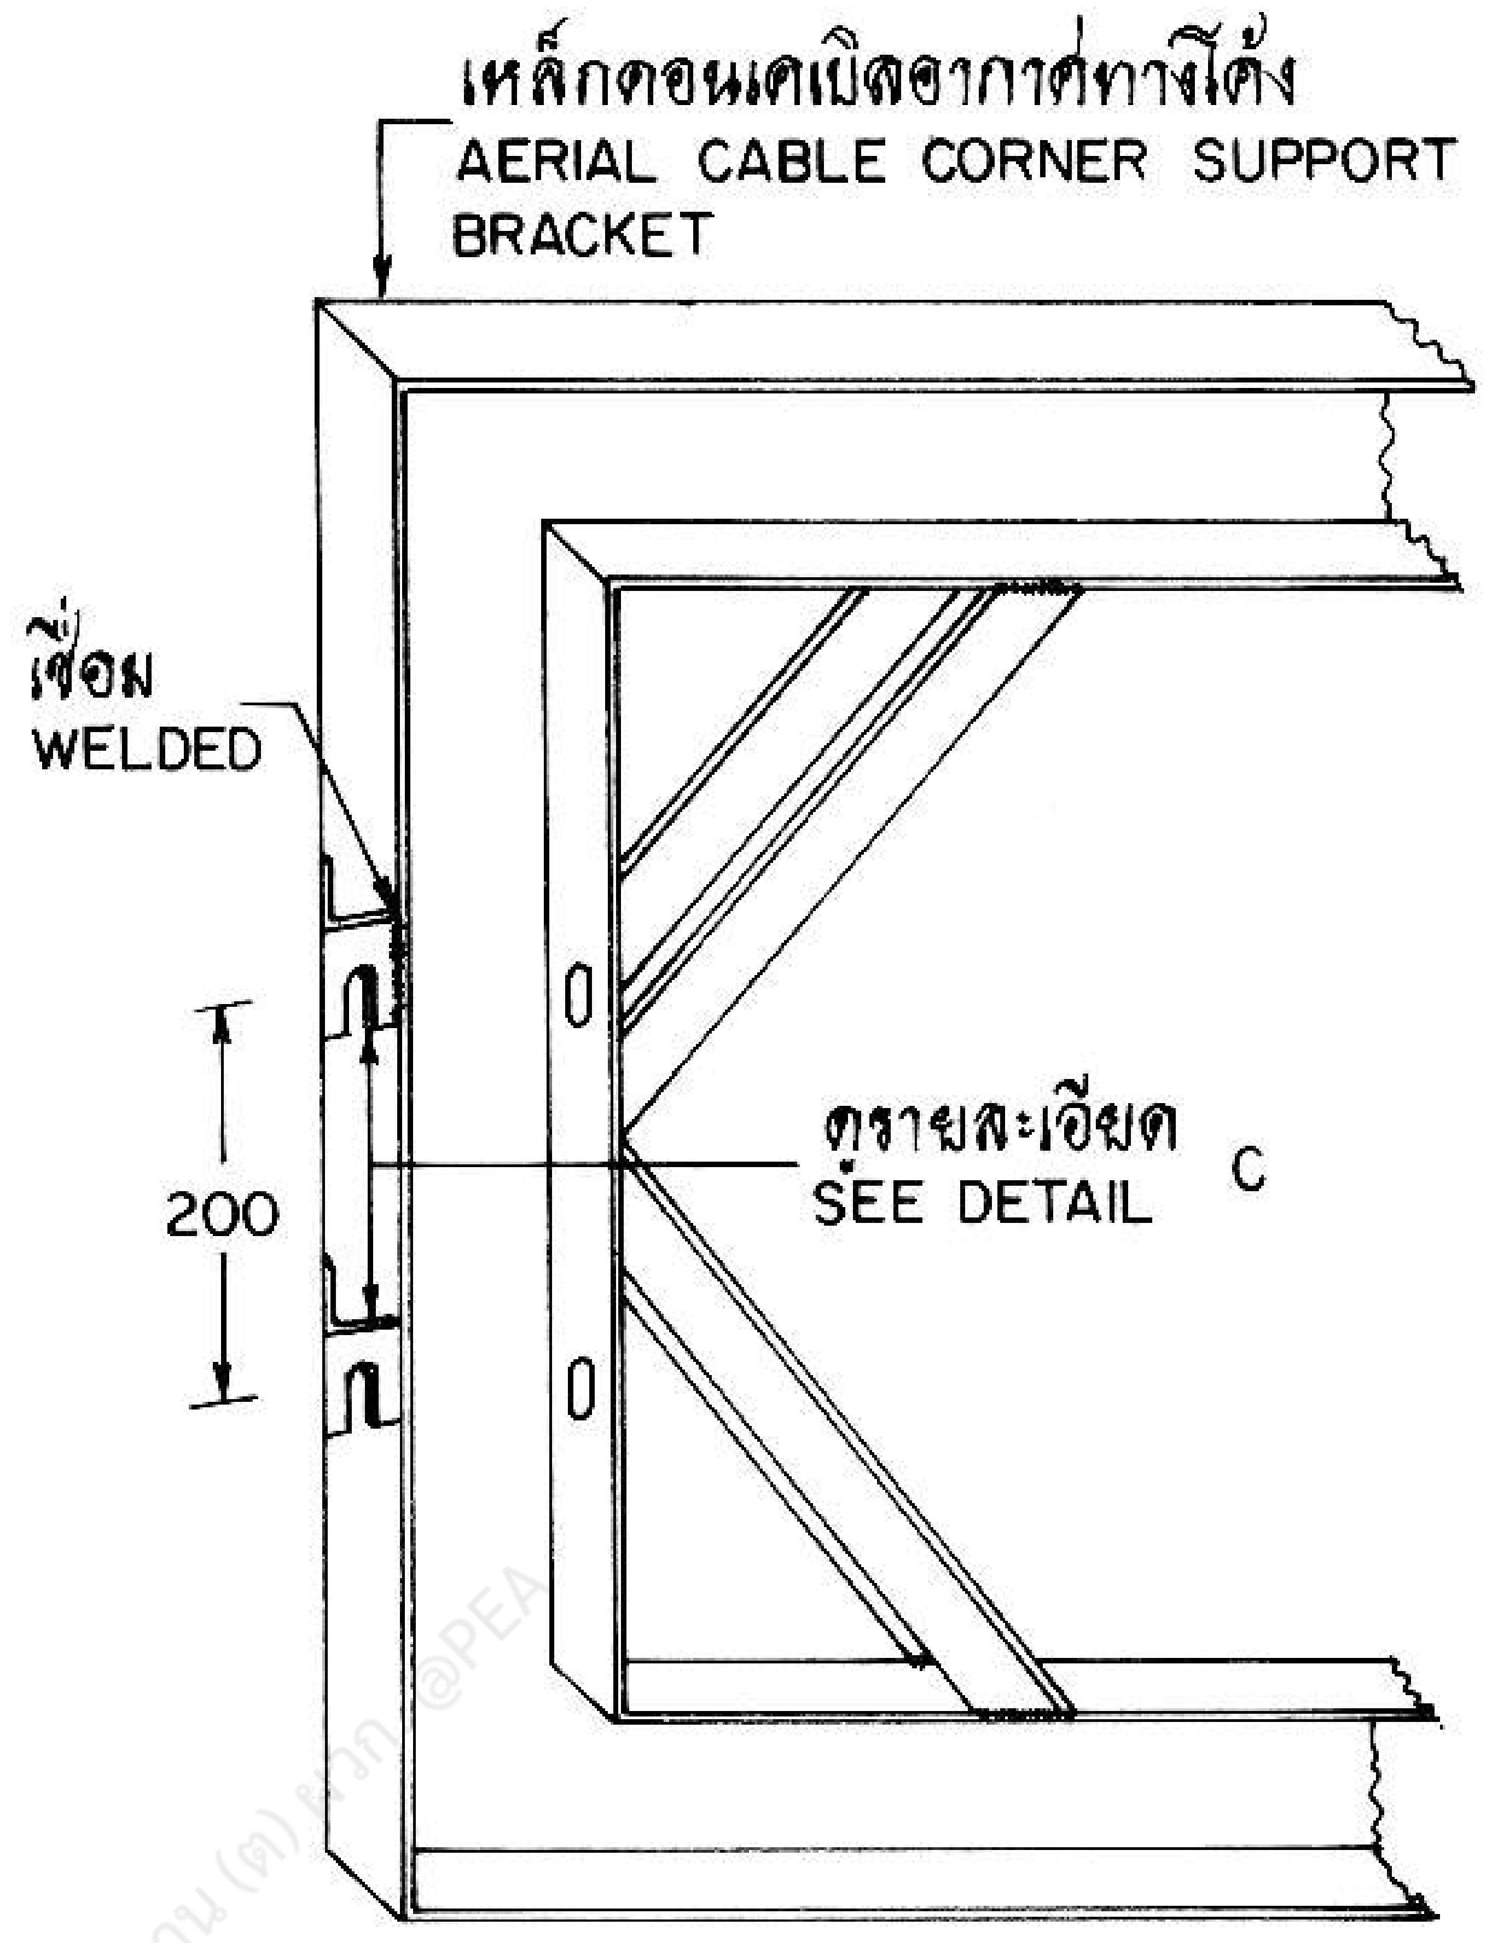

เหล็กตอนเคเบิลอากาศทางโค้ง
AERIAL CABLE CORNER SUPPORT BRACKET
เชื่อม
WELDED
200
ดูรายละเอียด
SEE DETAIL C

รายละเอียด
DETAIL **B**

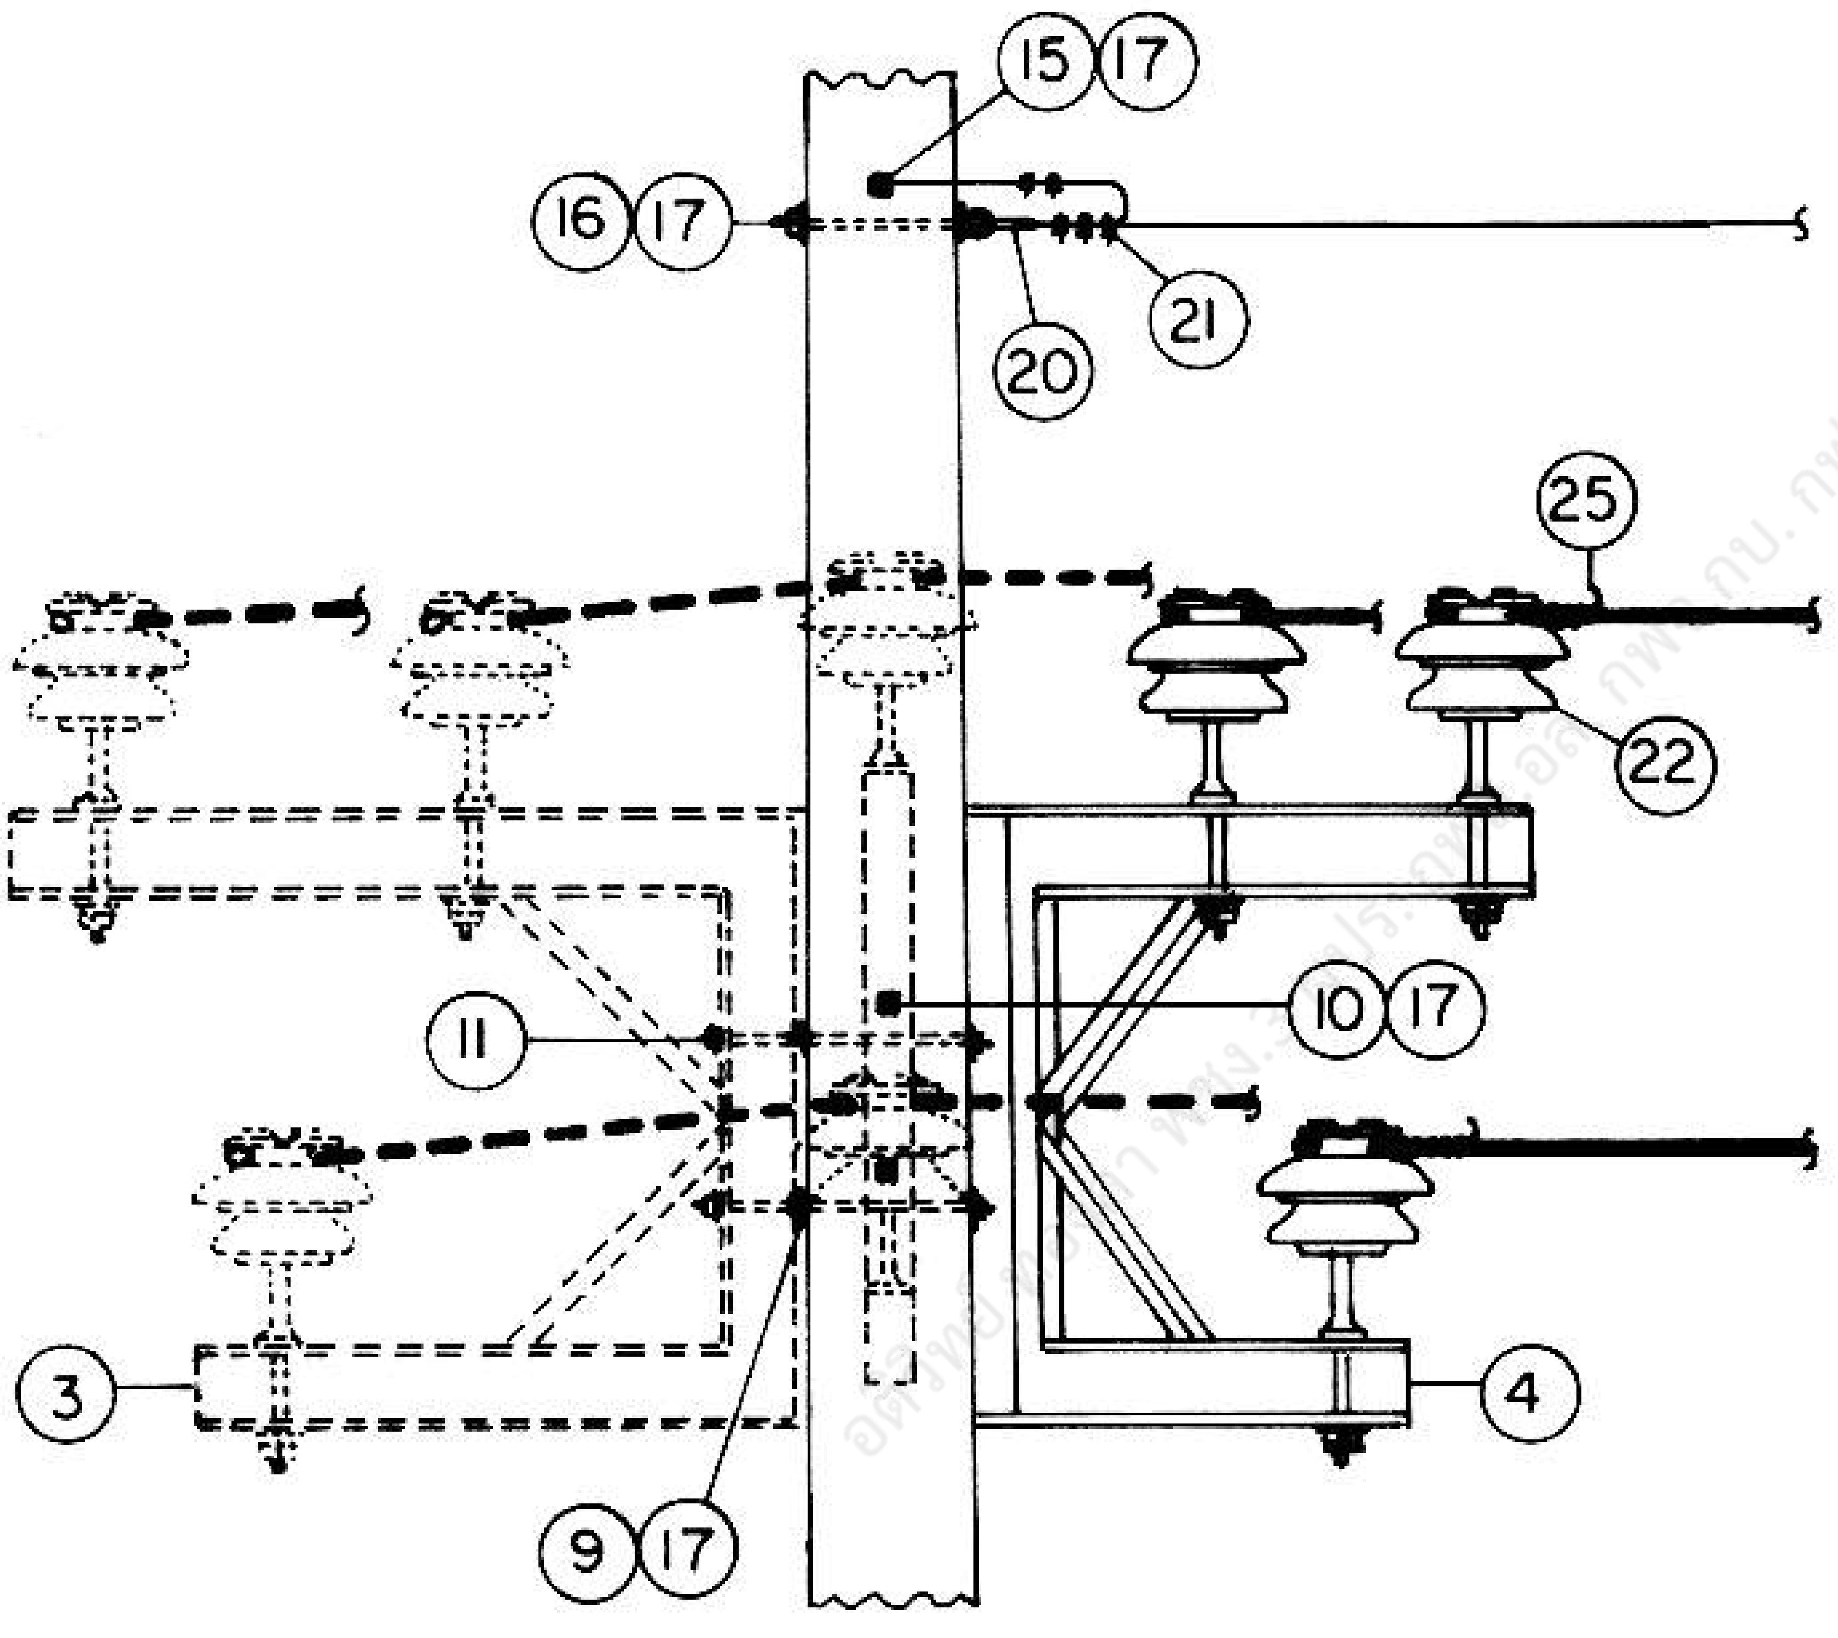

⑮⑰
⑯⑰
⑳
㉑
㉕
㉒
⑪
⑩⑰
③
④
⑨⑰

รายละเอียด
DETAIL **A**

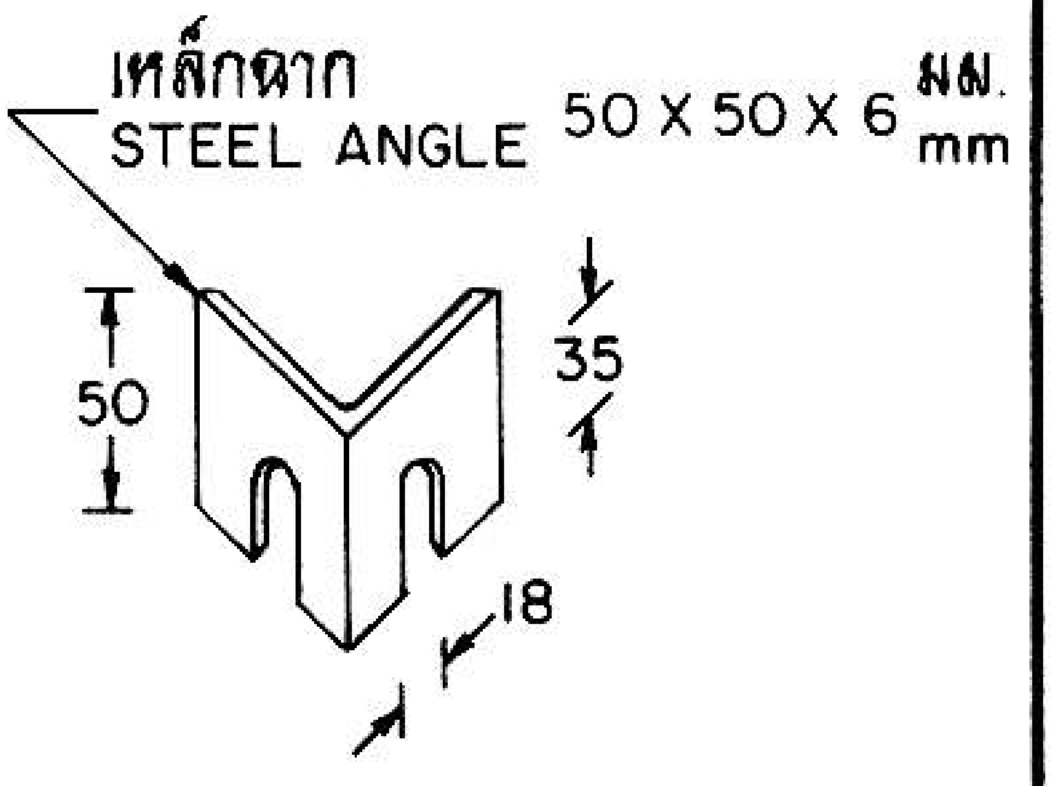

เหล็กฉาก
STEEL ANGLE 50 X 50 X 6 มม. mm
50
35
18

รายละเอียด
DETAIL **C**

กองวิศวกรรมไฟฟ้าและเครื่องกล ฝ่ายวิศวกรรม	**การไฟฟ้าส่วนภูมิภาค**	ใช้แทนแบบ ถูกแทนโดยแบบ
ผู้เขียน ผู้สำรวจ วิศวกร หัวหน้าแผนก ผู้อำนวยการกอง ผู้อำนวยการฝ่าย	ผู้ว่าการ 29 [illegible] 35 โครงสร้างเสาต้นทางโค้ง ระบบ 33 kV, มุม 60°- 90° 3 - 4 วงจร	เขียนเสร็จวันที่ 13 ต.ค. 35 แก้แบบวันที่ มิติเป็น มิลลิเมตร มาตราส่วน
รองผู้ว่าการฝ่ายเทคนิค	33 kV ANGLE STRUCTURE, LINE ANGLE 60°- 90° 3 - 4 CIRCUIT	แบบเลขที่ SA4-015/35012 แผ่นที่ 2 จากจำนวน 6 แผ่น

[illegible] ต.ค. 2535

การประกอบเลขที่
ASSEMBLY NO. **3239**

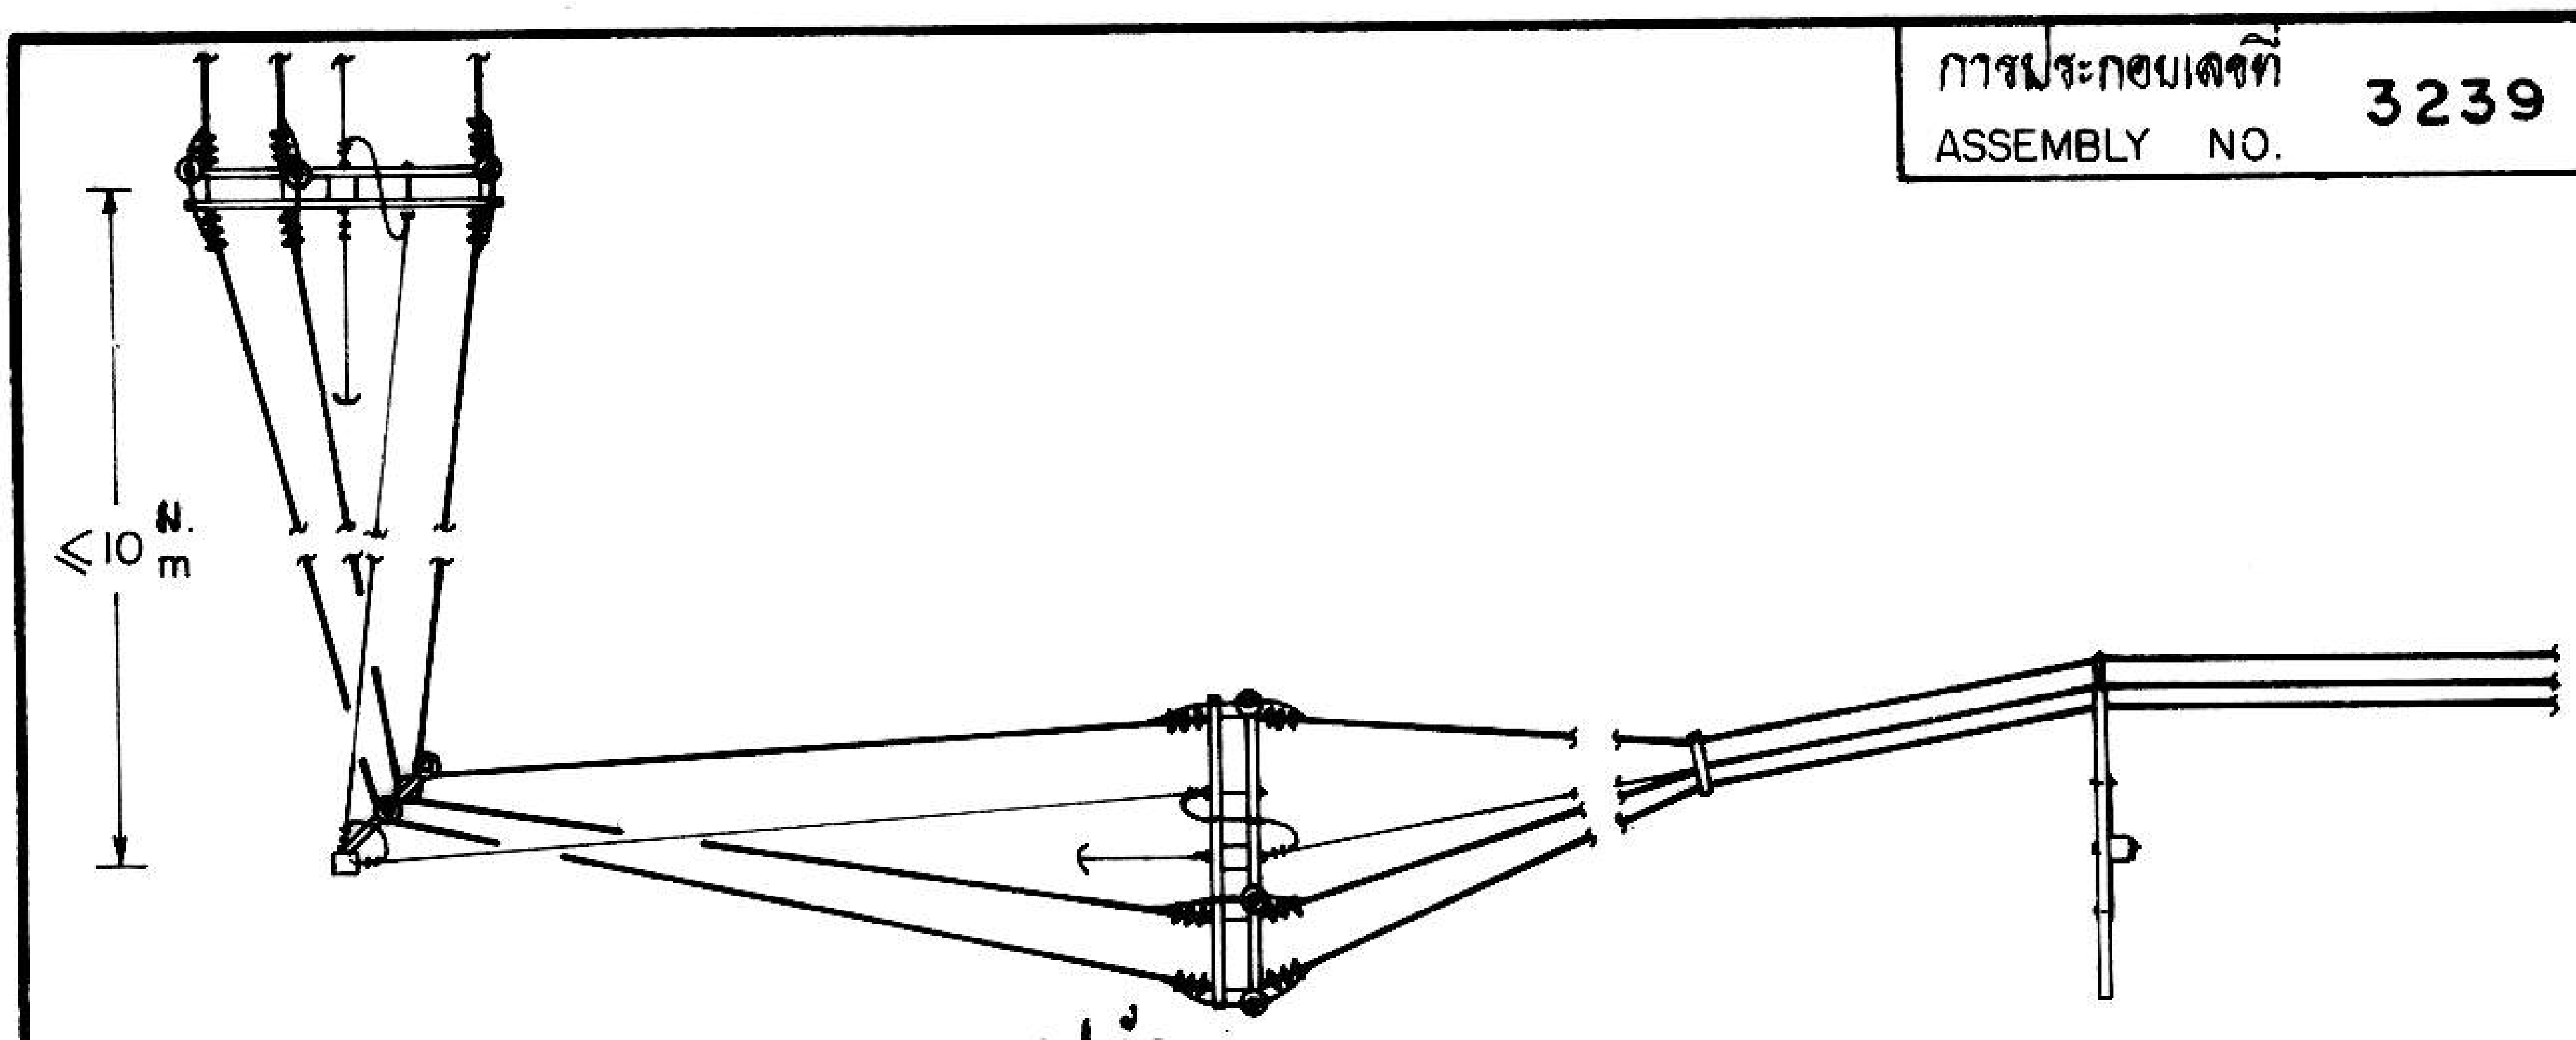

รูปตัด
SECTION A – A

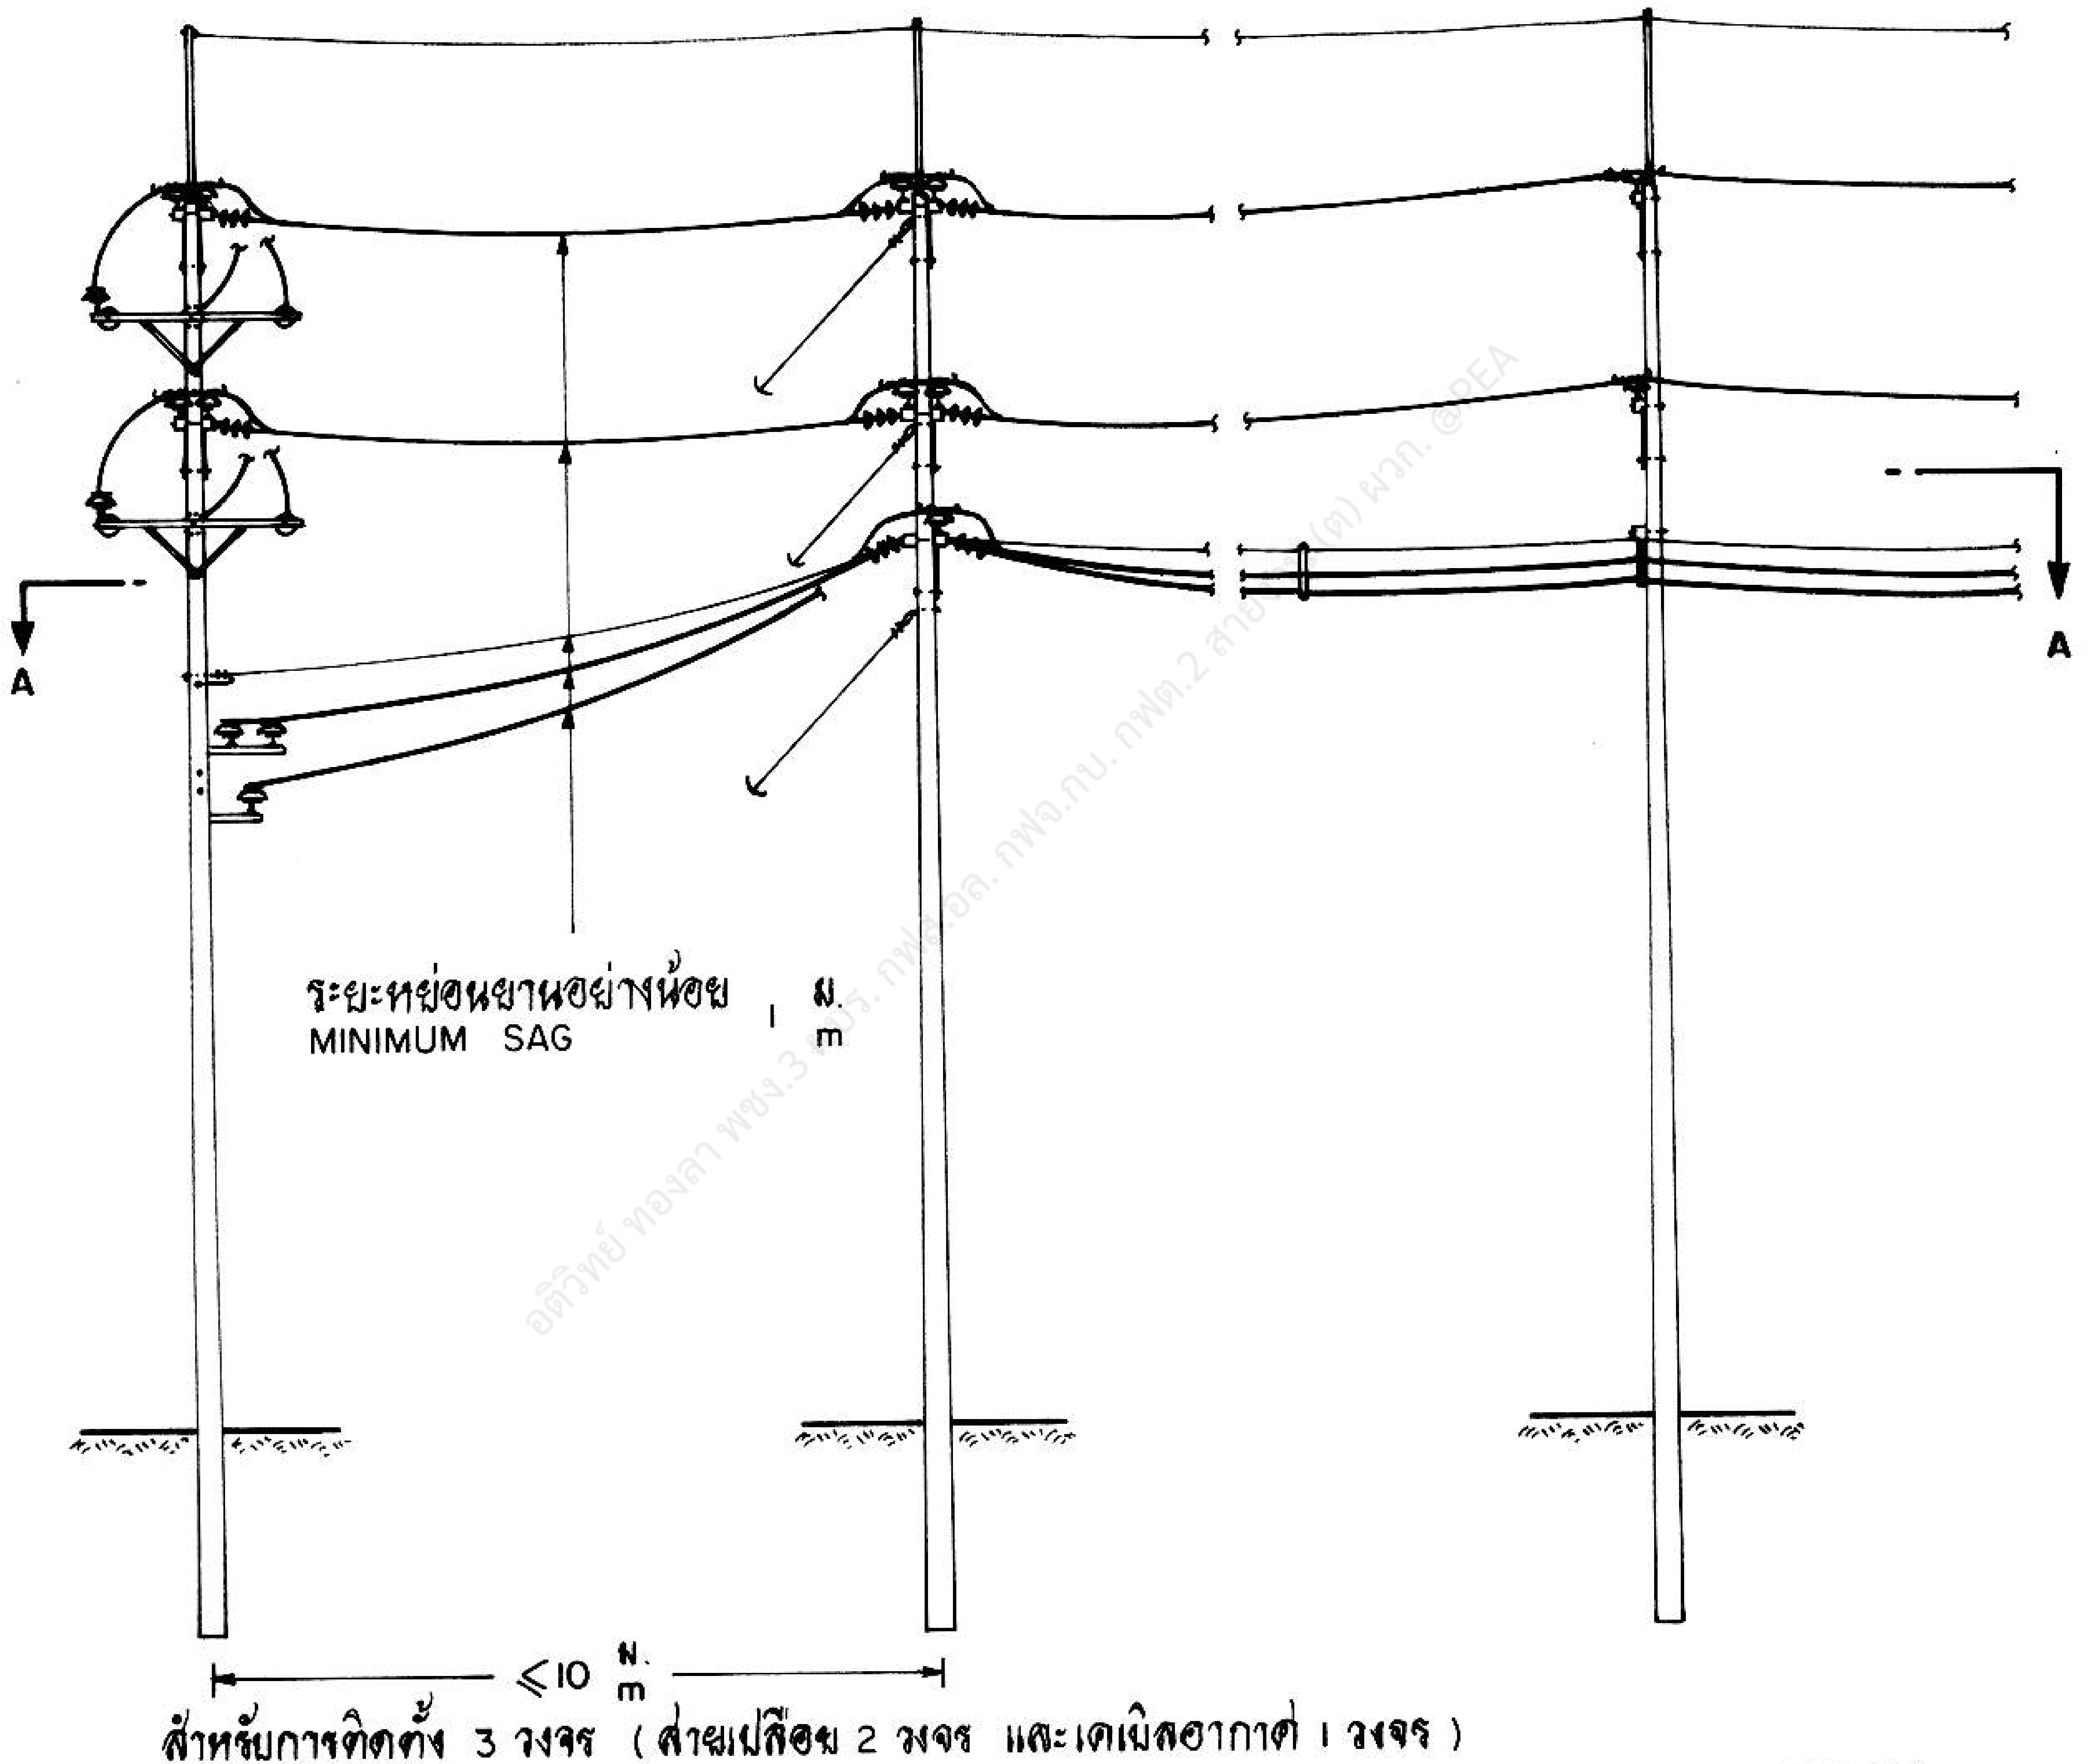

สำหรับการติดตั้ง 3 วงจร (สายเปลือย 2 วงจร และเคเบิลอากาศ 1 วงจร)
FOR 3-CIRCUIT INSTALLATION (2-CIRCUIT BARE CONDUCTOR AND 1-CIRCUIT AERIAL CABLE)

อดิวิทย์ ทองลา พชง.3 ฝบร. กฟส.อล. กฟจ.กบ. กฟต.2 สายงาน(ต) ผวก. @PEA

กองวิศวกรรมไฟฟ้าและเครื่องกล
ฝ่ายวิศวกรรม

ผู้เขียน
ผู้สำรวจ
วิศวกร
หัวหน้าแผนก
ผู้อำนวยการกอง
ผู้อำนวยการฝ่าย

รองผู้ว่าการฝ่ายเทคนิค

การไฟฟ้าส่วนภูมิภาค

ผู่ว่าการ 29 ต.ค. 35

โครงสร้างเสาต้นทางโค้ง ระบบ 33 kV, มุม 60° - 90°
3 - 4 วงจร

33 kV ANGLE STRUCTURE, LINE ANGLE 60° - 90°
3 - 4 CIRCUIT

ใช้แทนแบบ
ถูกแทนโดยแบบ
เขียนเสร็จวันที่ 13 ต.ค. 35
แก้แบบวันที่
ผลิตเป็น
มาตราส่วน 1 : 125

แบบเลขที่ SA4-015/35012
แผ่นที่ 3 ของจำนวน 6 แผ่น

2 6 ต.ค. 2535

การประกอบเลขที่
ASSEMBLY NO. **3239**

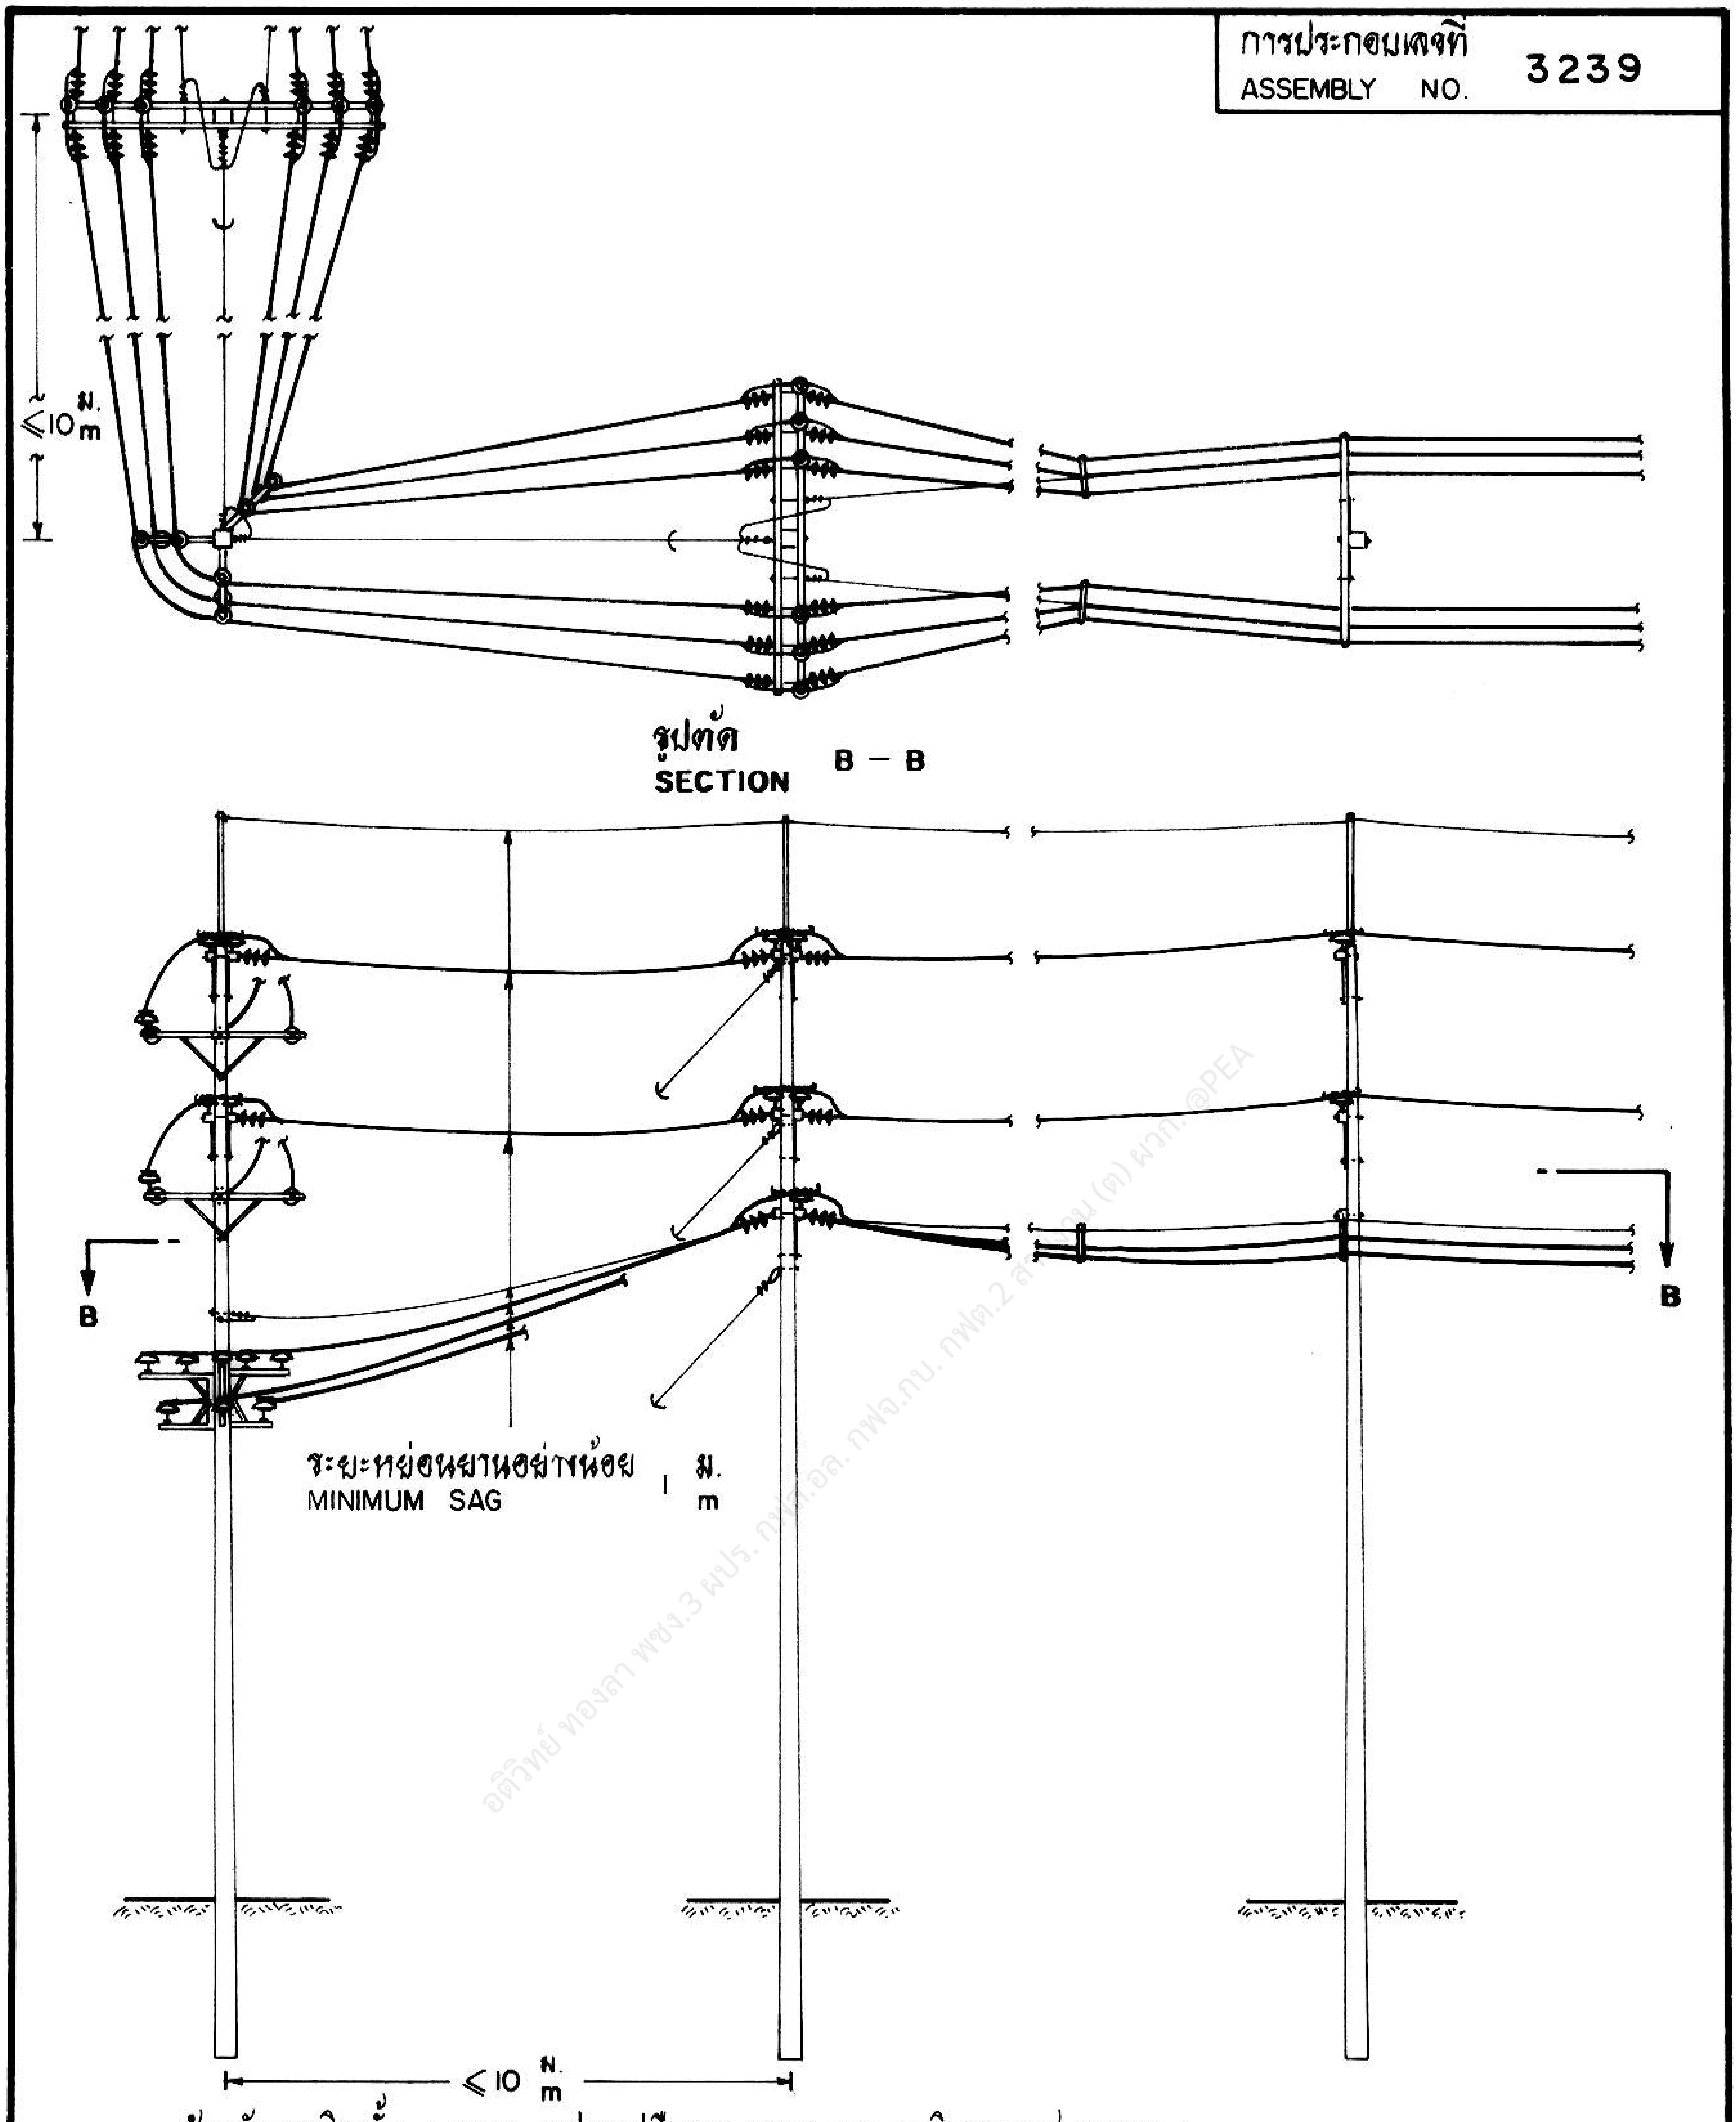
≤10 ม. m
รูปตัด SECTION B – B
B
B
ระยะหย่อนยานอย่างน้อย 1 ม.
MINIMUM SAG 1 m
≤10 ม. m

สำหรับการติดตั้ง 4 วงจร (สายเปลือย 2 วงจร และเคเบิลอากาศ 2 วงจร)
FOR 4-CIRCUIT INSTALLATION (2-CIRCUIT BARE CONDUCTOR AND 2-CIRCUIT AERIAL CABLE)

กองวิศวกรรมไฟฟ้าและเครื่องกล
ฝ่ายวิศวกรรม

การไฟฟ้าส่วนภูมิภาค

ผู้เขียน
ผู้สำรวจ
วิศวกร
หัวหน้าแผนก
ผู้อำนวยการกอง
ผู้อำนวยการฝ่าย

ผู้ว่าการ 29 ต.ค. 35

โครงสร้างเสาต้นทางโค้ง ระบบ 33 kV, มุม 60°-90°
3 - 4 วงจร

รองผู้ว่าการฝ่ายเทคนิค

33 kV ANGLE STRUCTURE, LINE ANGLE 60°-90°
3 - 4 CIRCUIT

ใช้แทนแบบ
ถูกแทนโดยแบบ
เขียนเสร็จวันที่ 13 ต.ค. 35
แก้แบบวันที่
มิติเป็น
มาตราส่วน 1 : 125

แบบเลขที่ SA4-015/35012
แผ่นที่ 4 ของจำนวน 6 แผ่น

2 6 [illegible] 2535

อดิวิทย์ ทองลา พชง.3 ผปร. กฟส.อล. กฟจ.กบ. กฟต.2 [illegible] (ต) ผวก. @PEA

การประกอบเลขที่
ASSEMBLY NO. 3239

บัญชีวัสดุ
BILL OF MATERIAL

ลำดับที่ ITEM	รายละเอียด DESCRIPTION	จำนวน REQ'D I	จำนวน REQ'D II	วัสดุเลขที่ MAT. NO.
1	เสาคอนกรีต ขนาด 14 ม. POLE, CONCRETE, 14 m LONG	1	1	00010006 (0036)
2	คอน คอร. สปัน (สำหรับเข้าปลายสาย) ขนาด 120 X 120 X 2,500 มม. CROSSARM, SPUN, PRESTRESSED CONCRETE (FOR DEADENDING), 120 X 120 X 2,500 mm	8	8	00110004 (0196)
3	เหล็กคอนเคเบิลอากาศทางโค้ง BRACKET, FOR AERIAL CABLE CORNER SUPPORT	–	2	02440104 (5920)
4	เหล็กคอนเคเบิลอากาศทางโค้ง (ตามรายละเอียด B) BRACKET, FOR AERIAL CABLE CORNER SUPPORT (ACC. TO DETAIL B)	1	1	02440104 (5920)
5	เหล็กรูปรางน้ำรับสายล่อฟ้า ขนาด 100 X 50 X 5 มม. ยาว 2.25 ม. OVERHEAD GROUND WIRE BAYONET, CHANNEL STEEL, 100 X 50 X 5 mm, 2.25 m LONG	2	2	01000100 (6012)
6	เหล็กประกับคอน ขนาด 30 X 6 X 760 มม. BRACE, FLAT, FOR CROSSARM, 30 X 6 X 760 mm	16	16	01200001 (0120)
7	สลักเกลียว M 16 X 170 มม. BOLT, MACHINE, M 16 X 170 mm	16	16	01110201 (0221)
8	สลักเกลียว M 16 X 250 มม. BOLT, MACHINE, M 16 X 250 mm	5	5	01110203 (0223)
9	สลักเกลียว M 16 X 300 มม. BOLT, MACHINE, M 16 X 300 mm	4	2	01110204 (0224)
10	สลักเกลียว M 16 X 350 มม. BOLT, MACHINE, M 16 X 350 mm	–	2	01110205 (0225)
11	สลักเกลียว M 16 X 400 มม. BOLT, MACHINE, M 16 X 400 mm	–	2	01110206 (0226)
12	สลักเกลียวห่วงกลม M 16 X 450 มม. BOLT, DOUBLE ARMING, ROUND EYE, M 16 X 450 mm	3	3	01130001 (0247)
13	สลักเกลียวห่วงกลม M 16 X 500 มม. BOLT, DOUBLE ARMING, ROUND EYE, M 16 X 500 mm	9	9	01130002 (0248)
14	สลักเกลียวห่วงกลม M 16 X 200 มม. BOLT, ROUND EYE, M 16 X 200 mm	1	1	01140001 (0253)
15	สลักเกลียวห่วงกลม M 16 X 250 มม. BOLT, ROUND EYE, M 16 X 250 mm	2	2	01140002 (0254)
16	สลักเกลียวห่วงกลม M 16 X 300 มม. BOLT, ROUND EYE, M 16 X 300 mm	1	1	01140003 (0255)
17	แหวนสี่เหลี่ยมแบน 52 X 52 X 4.5 มม. รู Ø 18 มม. มอก. 258 WASHER, SQUARE, FLAT, 52 X 52 X 4.5 mm, HOLE Ø 18 mm, TIS 258	64	64	01180100 (0355)
18	สเตรนแคลมป์ สำหรับสายอะลูมิเนียม ขนาดตามต้องการ CLAMP, STRAIN, FOR Al CONDUCTOR ; SIZE AS REQUIRED	12	12	03110000 - 03110101 -
19	หลอดต่อสายชนิดบีบไม่รับแรงดึง สายอะลูมิเนียมขนาดตามต้องการ CONNECTOR, SPLICE, COMPRESSION TYPE, TENSIONLESS, Al ; SIZE AS REQ'D	6	6	02410001 - 5 02410007

กพล. กพอ.กบ. กพพ.2 สายงาน (ต) ผวก. @PEA

กองวิศวกรรมไฟฟ้าและเครื่องกล
ฝ่ายวิศวกรรม

ผู้เขียน
ผู้สำรวจ
วิศวกร
หัวหน้าแผนก
ผู้อำนวยการกอง
ผู้อำนวยการฝ่าย

รองผู้ว่าการฝ่ายเทคนิค

26 ต.ค. 2535

การไฟฟ้าส่วนภูมิภาค

ผู้ว่าการ 27 ตค 35

โครงสร้างเสาต้นทางโค้ง ระบบ 33 kV, มุม 60°-90°
3 – 4 วงจร

33 kV ANGLE STRUCTURE, LINE ANGLE 60°- 90°
3 - 4 CIRCUIT

ใช้แทนแบบ
ถูกแทนโดยแบบ
เขียนเสร็จวันที่ 13 ต.ค. 35
แก้แบบวันที่
มิติเป็น
มาตราส่วน

แบบเลขที่ SA4-015/35012
แผ่นที่ 5 ของจำนวน 6 แผ่น

การประกอบเลขที่ ASSEMBLY NO.	3239

บัญชีวัสดุ
BILL OF MATERIAL

ลำดับที่ ITEM	รายละเอียด DESCRIPTION	จำนวน REQ'D I	จำนวน REQ'D II	วัสดุเลขที่ MAT. NO.
20	กายทิมเบิล สำหรับสายยึดโยง 50-95 ต.มม. THIMBLE, GUY, FOR STEEL WIRE 50-95 mm^2	4	4	01210304 (0150)
21	ยูแคล้มป์ สลัก 1 ตัว M 8 CLAMP, SINGLE U-BOLT, M 8	17	17	01230000 (0165)
22	ลูกถ้วยก้านตรง 33 kV มอก. 279 แบบ ค (แบบ 56-3) พร้อมก้าน INSULATOR, PIN TYPE, 33 kV, TIS 279, TYPE C (CLASS 56-3) COMP. WITH PIN	11	17	03000002 03100001
23	ลูกถ้วยแขวน มอก. 354 แบบ ง (แบบ 52-4) INSULATOR, SUSPENSION TYPE, TIS 354, TYPE D (CLASS 52-4)	36	36	03020002 (0415)
24	ลวดอะลูมิเนียมแบน 1 X 10 มม. ความยาวตามต้องการ TAPE, ARMOUR, Al, 1 X 10 mm ; LENGTH AS REQUIRED	ม. m	ม. m	02200000 (0700)
25	ลวดอะลูมิเนียมกลม 4.0 มม. ความยาวตามต้องการ TIE WIRE, Al, 4.0 mm ; LENGTH AS REQUIRED	ม. m	ม. m	02200002 (0704)
26	ท่อเหล็ก ขนาดระบุ 20 ประเภทที่ 2 ยาว 200 มม. มอก. 227 PIPE, STEEL, SIZE 20, TYPE 2, 200 mm LONG, TIS 227	2	2	

	แบบอ้างอิง REFERENCE DRAWING	แบบเลขที่ DWG. NO.	การประกอบเลขที่ ASSEMBLY NO.
1	โครงสร้างเสาระบบจำหน่าย 33 kV, 3-4 วงจร 33 kV DISTRIBUTION POLE STRUCTURE, 3-4 CIRCUIT	IB1-015/34071	8282
2	การประกอบคอนกับเสาคอนกรีต 33 kV, 3-4 วงจร 33 kV CROSSARM ASSEMBLY ON CONCRETE POLE, 3-4 CIRCUIT	SA1-015/34024	3237
3	โครงสร้างเสาต้นเจ้าปลายสายสองข้าง ระบบ 33 kV, 3-4 วงจร 33 kV DOUBLE DEADEND STRUCTURE, 3-4 CIRCUIT	SA4-015/35011	
4	หลักเกณฑ์การใช้ลูกถ้วยแรงสูง ในบริเวณใกล้ฝั่งทะเล RECOMMENDATION FOR H.T. INSULATOR INSTALLATION, NEAR THE SEA COAST	SA1-015/24019	9502
5	การต่อสายเคเบิลอากาศแรงสูง COMPRESSION SLEEVE, FOR H.T. AERIAL CABLE	SA1-015/22020	9562
6	การต่อปลายลวดเหล็กตีเกลียว STEEL STRANDED WIRE SPLICING	SA1-015/23053 SA1-015/28010	9563 9563A

หมายเหตุ

บัญชีวัสดุ :-

สดมภ์ I : สำหรับการติดตั้ง 3 วงจร
(สายเปลือย 2 วงจร และเคเบิลอากาศ 1 วงจร)

สดมภ์ II : สำหรับการติดตั้ง 4 วงจร
(สายเปลือย 2 วงจร และเคเบิลอากาศ 2 วงจร)

NOTES

BILL OF MATERIAL :-

COLUMN I : FOR 3 CIRCUIT INSTALLATION
(2-CIRCUIT BARE CONDUCTOR AND
1-CIRCUIT AERIAL CABLE)

COLUMN II : FOR 4 CIRCUIT INSTALLATION
(2-CIRCUIT BARE CONDUCTOR AND
2-CIRCUIT AERIAL CABLE)

กองวิศวกรรมไฟฟ้าและเครื่องกล
ฝ่ายวิศวกรรม

ผู้เขียน
ผู้สำรวจ
วิศวกร
หัวหน้าแผนก
ผู้อำนวยการกอง
ผู้อำนวยการฝ่าย

รองผู้ว่าการฝ่ายเทคนิค

การไฟฟ้าส่วนภูมิภาค

ผู้ว่าการ 29 ต.ค.35

โครงสร้างเสาต้นทางโค้ง ระบบ 33 kV, มุม 60°-90° 3-4 วงจร

33 kV ANGLE STRUCTURE, LINE ANGLE 60°-90° 3-4 CIRCUIT

ใช้แทนแบบ
ถูกแทนโดยแบบ
เขียนเสร็จวันที่ 13 ต.ค. 35
แก้แบบวันที่
ผลิตเป็น
มาตราส่วน

แบบเลขที่ SA4-015/35012
แผ่นที่ 6 ของจำนวน 6 แผ่น

26 ต.ค. 2535