การประกอบเลขที่ 5264
ASSEMBLY NO. 5264

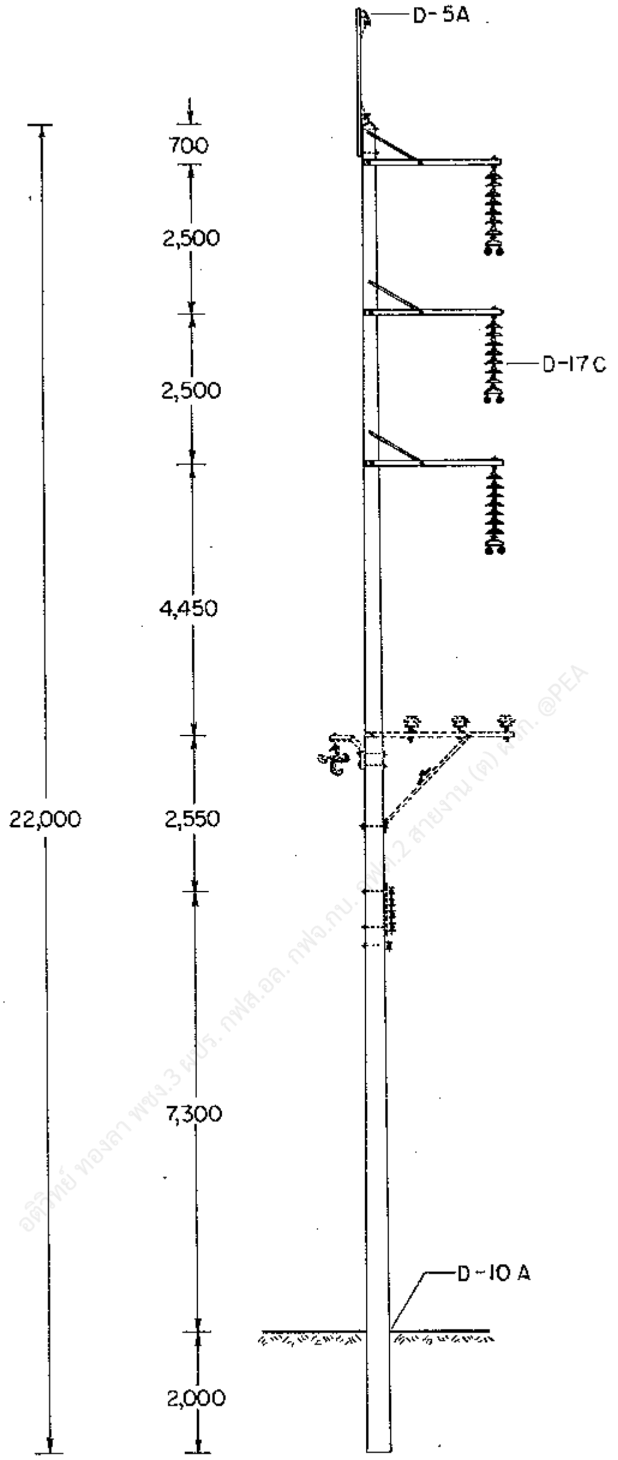

อดิศักดิ์ ทองลา พชง.3 ผปร. กฟส.อล. กฟจ.กบ. กฟต.2 สายงาน (ต) ผวก. @PEA

กองวิศวกรรมไฟฟ้าและเครื่องกล
ฝ่ายวิศวกรรม

ผู้เขียน
ผู้ตรวจ
วิศวกร
หัวหน้าแผนก
ผู้อำนวยการกอง
ผู้อำนวยการฝ่าย

รองผู้ว่าการฝ่ายเทคนิค

# การไฟฟ้าส่วนภูมิภาค

ผู้ว่าการ 11 เม.ย. 33

115 kV วงจรเดี่ยว สายไฟฟ้าคู่
เสาสำหรับทางตรง
แบบ SD - TG - 3

115 kV SINGLE CIRCUIT DOUBLE CONDUCTOR
TANGENT STRUCTURE
TYPE SD - TG - 3

ใช้แทนแบบ
ถูกแทนโดยแบบ
เขียนเสร็จวันที่ 4 ม.ค. 33
แก้แบบวันที่ 27 ก.ค. 38
มิติเป็น มิลลิเมตร
มาตราส่วน 1:125

แบบเลขที่ SAI-015/33002
แผ่นที่ 1 ของจำนวน 3 แผ่น

การประกอบเลขที่ 
ASSEMBLY NO. 5264

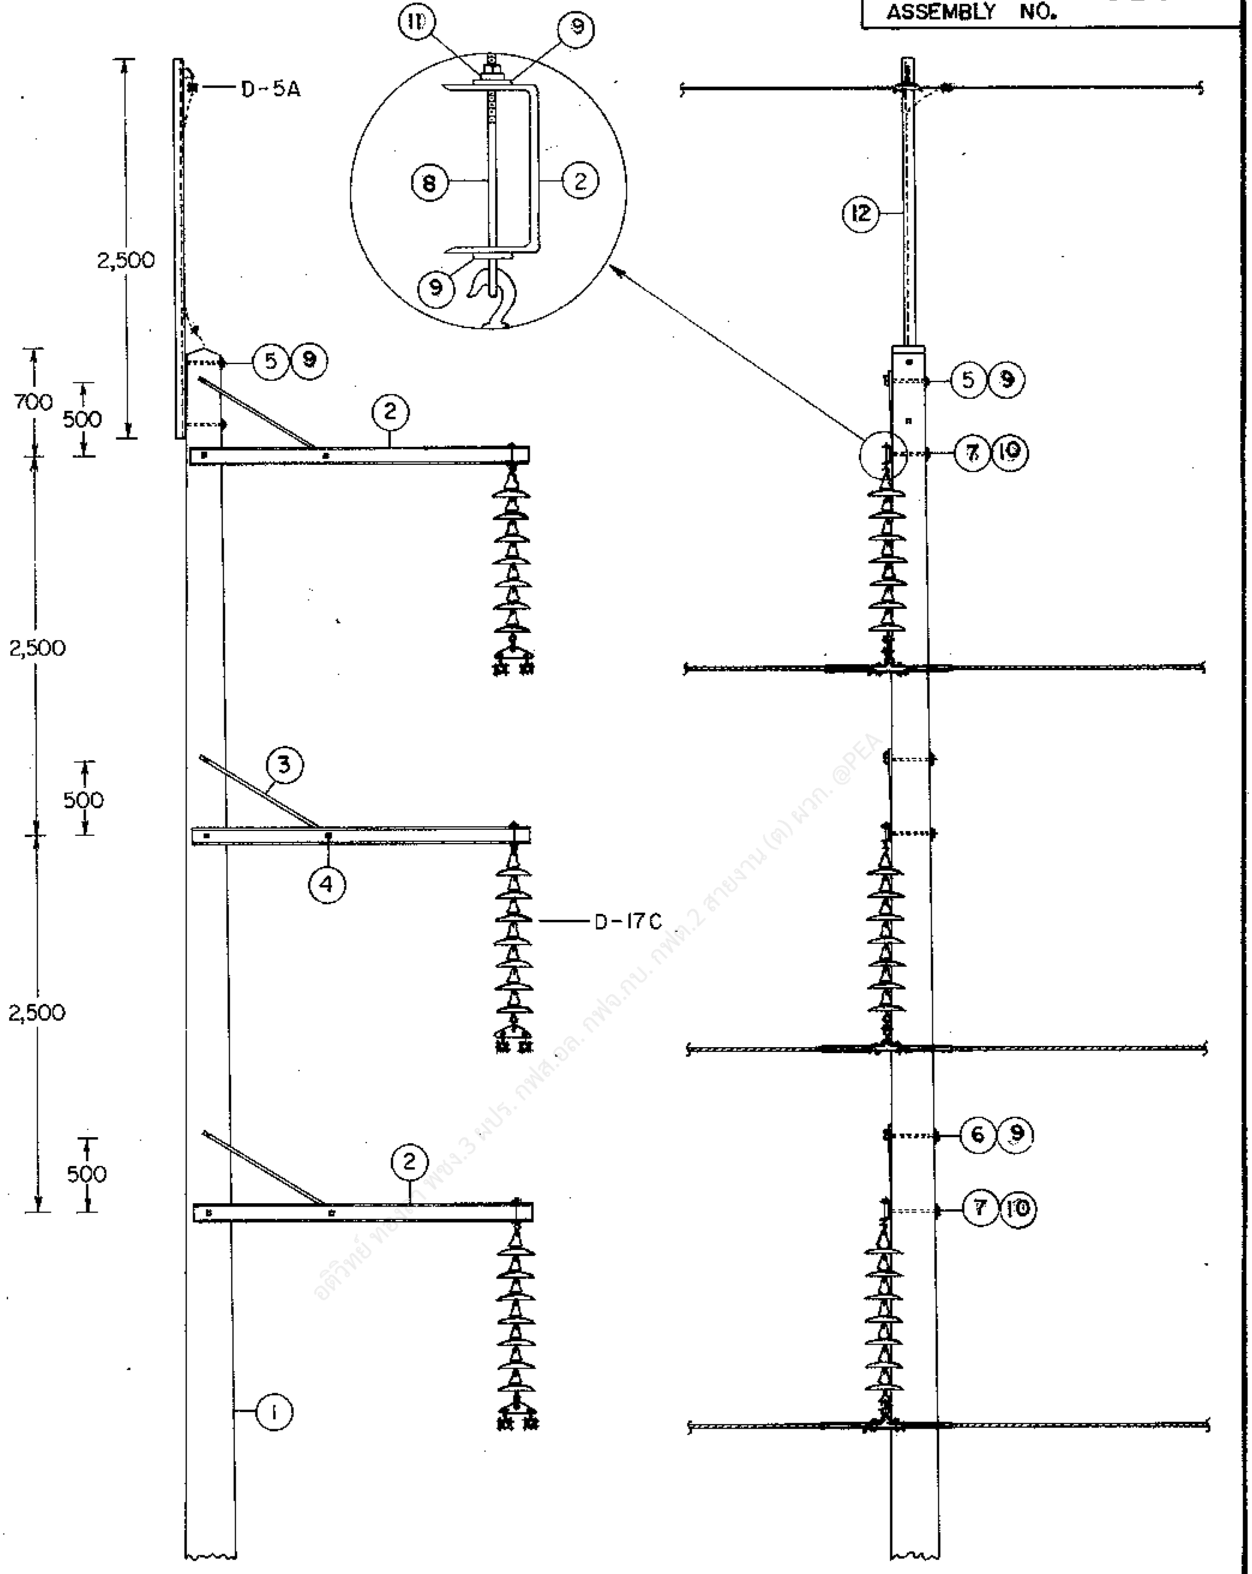

อดิวิทย์ ท[illegible] พชง.3 ผบร. กฟส.อล. กฟจ.กบ. กฟต.2 สายงาน (ต) ผวก. @PEA

กองวิศวกรรมไฟฟ้าและเครื่องกล
ฝ่ายวิศวกรรม

ผู้เขียน
ผู้สำรวจ
วิศวกร
หัวหน้าแผนก
ผู้อำนวยการกอง
ผู้อำนวยการฝ่าย

รองผู้ว่าการฝ่ายเทคนิค

## การไฟฟ้าส่วนภูมิภาค

ผู้ว่าการ 13 เม.ย. 33

115 kV วงจรเดี่ยว สายไฟฟ้าคู่
เสาสำหรับทางตรง
แบบ SD - TG - 3

115 kV SINGLE CIRCUIT DOUBLE CONDUCTOR
TANGENT STRUCTURE
TYPE SD - TG - 3

ใช้แทนแบบ
ถูกแทนโดยแบบ
เขียนเสร็จวันที่ 3 ม.ค. 33
แก้แบบวันที่ 27 ก.ค. 38
มิติเป็น มิลลิเมตร
มาตราส่วน 1 : 50

แบบเลขที่ SAI-015/33002

แผ่นที่ 2 ของจำนวน 3 แผ่น

| การประกอบเลขที่<br>ASSEMBLY NO. | 5264 |
|---|---|

## บัญชีวัสดุ
## BILL OF MATERIAL

| ลำดับที่<br>ITEM | รายละเอียด<br>DESCRIPTION | จำนวน<br>REQ'D | วัสดุเลขที่<br>MAT. NO. |
|---|---|---|---|
| 1 | เสาคอนกรีต 22 ม.<br>POLE, CONCRETE, 22 m LONG | 1 | 00010011<br>(0041) |
| 2 | คอนเหล็กแบบท้าวแขน ขนาด [ 100 X 50 X 5 มม. ยาว 2.25 ม. มอก. 116<br>STEEL ALLEY ARM, [ 100 X 50 X 5 mm, 2.25 m LONG, TIS 116 | 3 | 01000100<br>(6015) |
| 3 | เหล็กประกับคอน ขนาด 40 X 6 X 1,000 มม.<br>BRACE, FLAT FOR CROSSARM, 40 X 6 X 1,000 mm | 3 | 01200002<br>(0121) |
| 4 | สลักเกลียว M 16 X 75 มม. พร้อมแหวนกลม 2 อัน<br>BOLT, MACHINE, M 16 X 75 mm, COMPLETE WITH 2 ROUND WASHER | 3 | 01110400<br>(0236) |
| 5 | สลักเกลียว M 16 X **300** มม.<br>BOLT, MACHINE, M 16 X **300** mm, | 3 | 01110204<br>(0224) |
| 6 | สลักเกลียว M 16 X 350 มม.<br>BOLT, MACHINE, M 16 X 350 mm | 2 | 01110205<br>(0225) |
| 7 | สลักเกลียว M 20 X **350** มม.<br>BOLT, MACHINE, M 20 X **350** mm | 3 | 01110300<br>(0233) |
| 8 | สลักห่วงโอแวล M 16 X 150 มม.<br>BOLT, OVAL EYE, M 16 X 150 mm | 3 | 01150000<br>(0257) |
| 9 | แหวนสี่เหลี่ยมแบน 52 X 52 X 4.5 มม. รู Ø 18 มม. มอก. 258<br>WASHER, SQUARE, FLAT 52 X 52 X 4.5 mm, HOLE Ø 18 mm, TIS 258 | 11 | 01180100<br>(0355) |
| 10 | แหวนสี่เหลี่ยมแบน 62 X 62 X 6 มม. รู Ø 22 มม. มอก. 258<br>WASHER, SQUARE, FLAT 62 X 62 X 6 mm, HOLE Ø 22 mm, TIS 258 | 3 | 01180101<br>(0356) |
| 11 | แหวนสปริง M 16 มอก. 259<br>WASHER, LOCK, M 16, TIS 259 | 3 | 01180301<br>(0365) |
| 12 | เหล็กฉากรับสายล่อฟ้า ขนาด 65 X 65 X 6 มม. ยาว 2,500 มม. มอก. 116<br>OVERHEAD GROUND WIRE BAYONET, 65 X 65 X 6 mm, 2,500 mm LONG, TIS 116 | 1 | 01010004<br>(0135) |
|  |  |  |  |

|  | รายละเอียด<br>DESCRIPTION |  |  |
|---|---|---|---|
| D-17C | การประกอบลูกถ้วยแขวน<br>SUSPENSION INSULATOR ASSEMBLY | 3 |  |
| D-5A | การต่อสายล่อฟ้า<br>OVERHEAD GROUND WIRE CONNECTION | 1 |  |
| D-10A | ฐานรากเสา<br>POLE FOUNDATION | 1 |  |

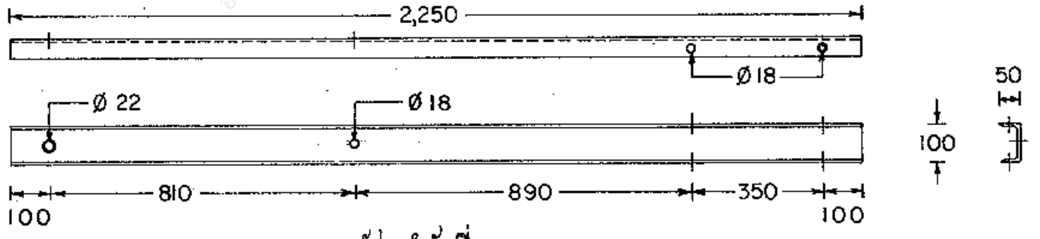

วัสดุลำดับที่
MATERIAL ITEM ②

| | | |
|---|---|---|
| กองวิศวกรรมไฟฟ้าและเครื่องกล<br>ฝ่ายวิศวกรรม | การไฟฟ้าส่วนภูมิภาค | ใช้แทนแบบ........<br>ถูกแทนโดยแบบ........ |
| ผู้เขียน........<br>ผู้สำรวจ........<br>วิศวกร........<br>หัวหน้าแผนก........<br>ผู้อำนวยการกอง........<br>ผู้อำนวยการฝ่าย........ | ผู้ว่าการ........ 11 เมย 33<br>115 kV วงจรเดี่ยว สายไฟฟ้าคู่<br>เสาสำหรับทางตรง<br>แบบ SD - TG - 3 | เขียนเสร็จวันที่ 4 พ.ค. 33<br>แก้แบบวันที่ 27 ก.ค. 38<br>มิติเป็น มิลลิเมตร<br>มาตราส่วน 1 : 20 |
| รองผู้ว่าการฝ่ายเทคนิค | 115 kV SINGLE CIRCUIT DOUBLE CONDUCTOR<br>TANGENT STRUCTURE<br>TYPE SD - TG - 3 | แบบเลขที่ SAI-015/33002<br>แผ่นที่ 3 ของจำนวน 3 แผ่น |