การประกอบเลขที่
ASSEMBLY NO. **5265**

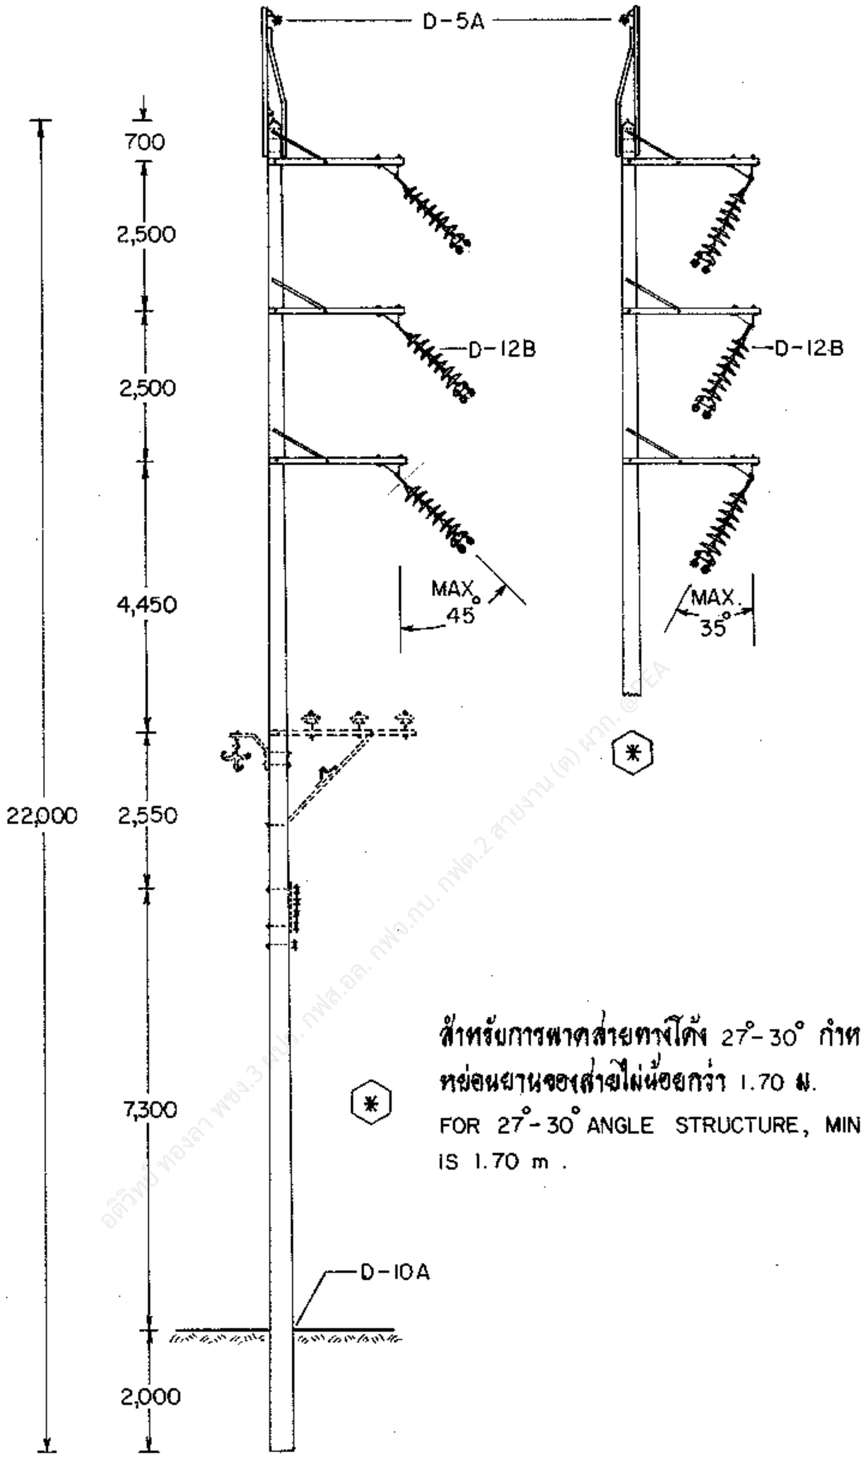

✱ สำหรับการพาดสายทางโค้ง 27°-30° กำหนดให้มีระยะหย่อนยานของสายไม่น้อยกว่า 1.70 ม.
FOR 27°-30° ANGLE STRUCTURE, MINIMUM SAG IS 1.70 m .

อติวิทย์ ทองลา พชง.3 ฝปบ. กฟส.อล. กฟจ.กบ. กฟต.2 สายงาน (ต) ผวก. @PEA

กองวิศวกรรมไฟฟ้าและเครื่องกล
ฝ่ายวิศวกรรม

ผู้เขียน
ผู้ตรวจ
วิศวกร
หัวหน้าแผนก
ผู้อำนวยการกอง
ผู้อำนวยการฝ่าย
รองผู้ว่าการฝ่ายเทคนิค

การไฟฟ้าส่วนภูมิภาค

ผู้ว่าการ 11 เม.ย. 33

115 kV วงจรเดี่ยว สายไฟฟ้าคู่
เสาสำหรับทางโค้ง
แบบ SD - SA - 2

115 kV SINGLE CIRCUIT DOUBLE CONDUCTOR
ANGLE STRUCTURE
TYPE SD - SA - 2

ใช้แทนแบบ
ถูกแทนโดยแบบ
เขียนเสร็จวันที่ 27 ก.พ. 33
แก้แบบวันที่ 27 ก.ค. 38
มิติเป็น มิลลิเมตร
มาตราส่วน 1 : 125
แบบเลขที่ SAI-015/33007
แผ่นที่ 1 ของจำนวน 3 แผ่น

5

การประกอบเลขที่
ASSEMBLY NO. **5265**

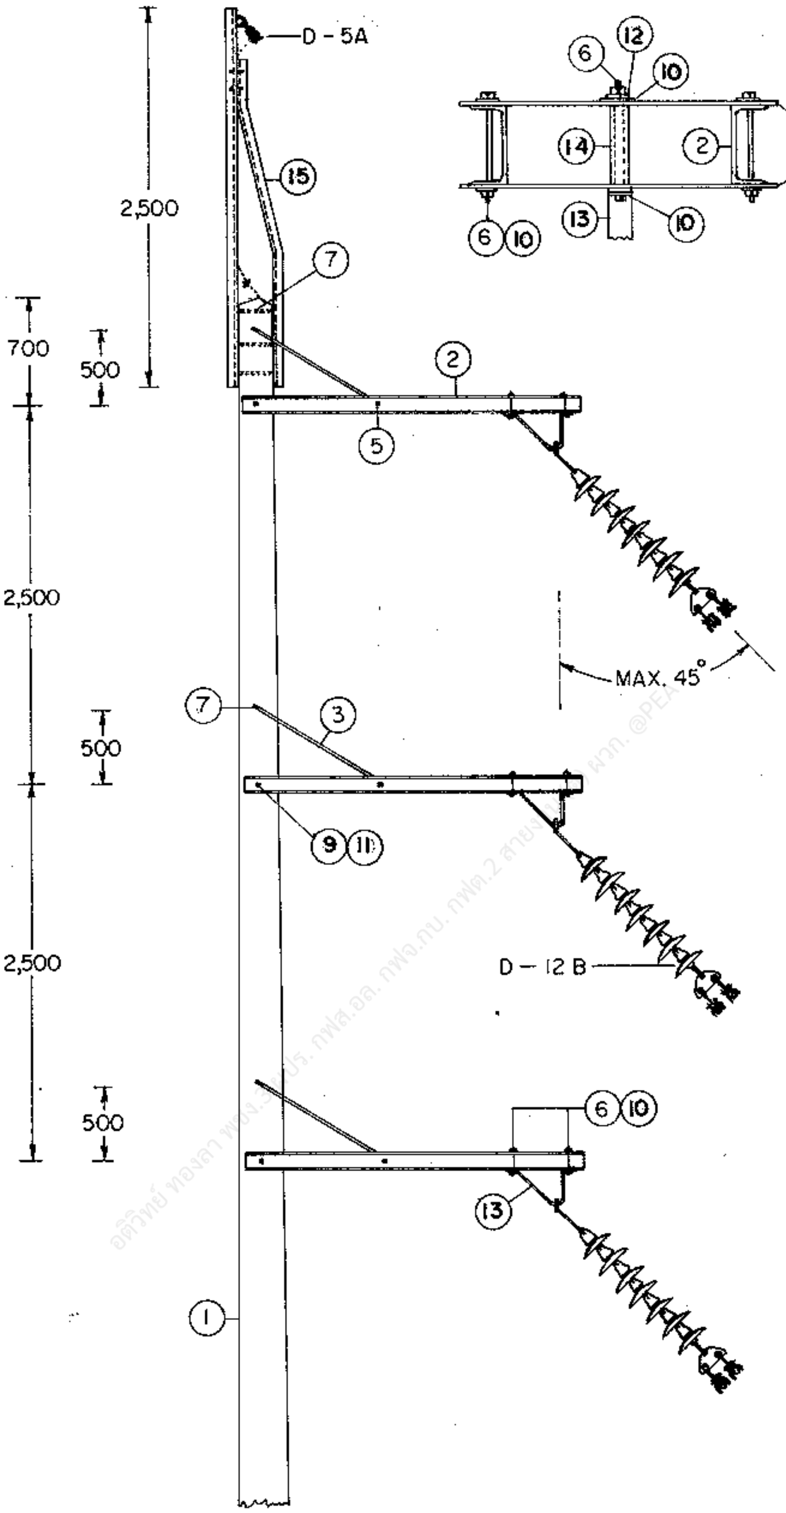

อติวิทย์ ทองลา พชง.3 ปร. กฟส.อล. กฟจ.กบ. กฟต.2 สาย ผวก. @PEA

กองวิศวกรรมไฟฟ้าและเครื่องกล
ฝ่ายวิศวกรรม

ผู้เขียน
ผู้สำรวจ
วิศวกร
หัวหน้าแผนก
ผู้อำนวยการกอง
ผู้อำนวยการฝ่าย
รองผู้ว่าการฝ่ายเทคนิค

การไฟฟ้าส่วนภูมิภาค

ผู้ว่าการ

115 kV วงจรเดี่ยว สายไฟฟ้าคู่
เสาสำหรับทางโค้ง
แบบ SD - SA - 2

115 kV SINGLE CIRCUIT DOUBLE CONDUCTOR
ANGLE STRUCTURE
TYPE SD - SA - 2

ใช้แทนแบบ
ถูกแทนที่โดยแบบ
เขียนเสร็จวันที่ 27 ก.พ.33
แก้แบบวันที่ 27 ก.ค.38
มิติเป็น มิลลิเมตร
มาตราส่วน 1 : 50
แบบเลขที่ SAI-015/33007
แผ่นที่ 2 ของจำนวน 3 แผ่น

5

การประกอบเลขที่ **5265**
ASSEMBLY NO.

บัญชีวัสดุ
BILL OF MATERIAL

ลำดับที่ ITEM	รายละเอียด DESCRIPTION	จำนวน REQ'D	วัสดุเลขที่ MAT.NO.
1	เสาคอนกรีต 22 ม. POLE, CONCRETE, 22 m LONG	1	00010011 (0041)
2	คอนเหล็กแบบท้าวแขน ขนาด ⊏ 100 X 50 X 5 มม. ยาว 2.25 ม. มอก. 116 STEEL ALLEY ARM, ⊏ 100 X 50 X 5 mm, 2.25 m LONG, TIS 116	6	01000100 (6015)
3	เหล็กประกับคอน ขนาด 40 X 6 X 1,000 มม. BRACE, FLAT FOR CROSSARM, 40 X 6 X 1,000 mm	6	01200002 (0121)
4	แผ่นเหล็ก 6 X 100 X 450 มม. PLATE, STEEL 6 X 100 X 450 mm	12	01030002 (0143)
5	สลักเกลียว M 16 X 75 มม. พร้อมแหวนกลม 2 อัน BOLT, MACHINE, M 16 X 75 mm, COMPLETE WITH 2 ROUND WASHERS	6	01110400 (0236)
6	สลักเกลียว M 16 X 170 มม. BOLT, MACHINE, M 16 X 170 mm,	18	01110201 (0221)
7	สลักเกลียว M 16 X 300 มม. BOLT, MACHINE, M 16 X 300 mm	4	01110204 (0224)
8	สลักเกลียว M 16 X 350 มม. BOLT, MACHINE, M 16 X 350 mm	2	01110205 (0225)
9	สลักเกลียว M 20 X 350 มม. BOLT, MACHINE, M 20 X 350 mm	3	01110300 (0232)
10	แหวนสี่เหลี่ยมแบน 52 X 52 X 4.5 มม. รู Ø 18 มม. มอก. 258 WASHER, SQUARE, FLAT 52 X 52 X 4.5 mm, HOLE Ø 18 mm, TIS 258	36	01180100 (0355)
11	แหวนสี่เหลี่ยมแบน 62 X 62 X 6 มม. รู Ø 22 มม. มอก. 258 WASHER, SQUARE, FLAT 62 X 62 X 6 mm, HOLE Ø 22 mm, TIS 258	6	01180101 (0356)
12	แหวนสปริง M 16 มอก. 259 WASHER, LOCK, M 16, TIS 259	6	01180301 (0365)
13	ที่แขวนลูกถ้วยทางโค้ง BRACKET, CORNER SUSPENSION	3	03140012 (0489)
14	ท่อเหล็กช่องขนาด 20 มม. หนา 2.65 มม. ยาว 100 มม. PIPE, IRON DIA. 20 mm I.D., 2.65 mm THICKNESS, 100 mm LONG	6	01050000 (0905)
15	เหล็กฉากจับสายล่อฟ้าทางโค้ง ขนาด 65 X 65 X 6 มม. ยาว 2,500 มม. มอก. 116 OVERHEAD GROUND WIRE CORNER BAYONET, 65 X 65 X 6 mm, 2,500 mm LONG, TIS 116	1	01010005 (0136)
	รายละเอียด DESCRIPTION		
D-12B	การประกอบลูกถ้วยแขวน SUSPENSION INSULATOR ASSEMBLY	3	
D-5A	การต่อสายล่อฟ้า OVERHEAD GROUND WIRE CONNECTION	1	
D-10A	ฐานรากเสา POLE FOUNDATION	1	

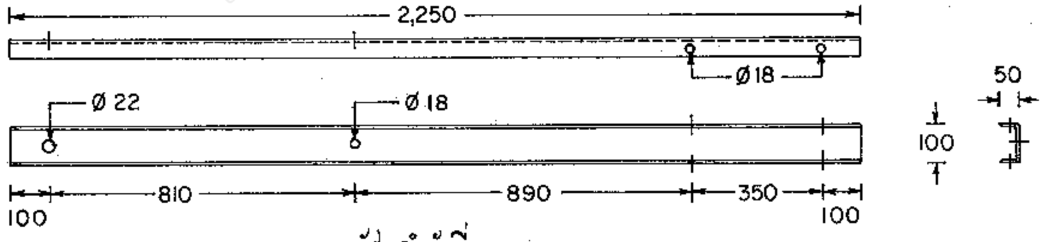

วัสดุลำดับที่
MATERIAL ITEM ②

กองวิศวกรรมไฟฟ้าและเครื่องกล ฝ่ายวิศวกรรม	**การไฟฟ้าส่วนภูมิภาค**	ใช้แทนแบบ ถูกแทนโดยแบบ เขียนเสร็จวันที่ 27 ก.พ. 33 แก้แบบวันที่ 27 ค.ต. 38 มิติเป็น มิลลิเมตร มาตราส่วน 1 : 20
ผู้เขียน ผู้สำรวจ วิศวกร หัวหน้าแผนก ผู้อำนวยการกอง ผู้อำนวยการฝ่าย	ผู้ว่าการ 1/12/33 115 kV วงจรเดี่ยว สายไฟฟ้าคู่ เสาสำหรับทางโค้ง แบบ SD - SA - 2	
รองผู้ว่าการฝ่ายเทคนิค	115 kV SINGLE CIRCUIT DOUBLE CONDUCTOR ANGLE STRUCTURE TYPE SD - SA - 2	แบบเลขที่ SAI-015/33007 แผ่นที่ 3 จากจำนวน 3 แผ่น

5