การประกอบเลขที่ 5214
ASSEMBLY NO.

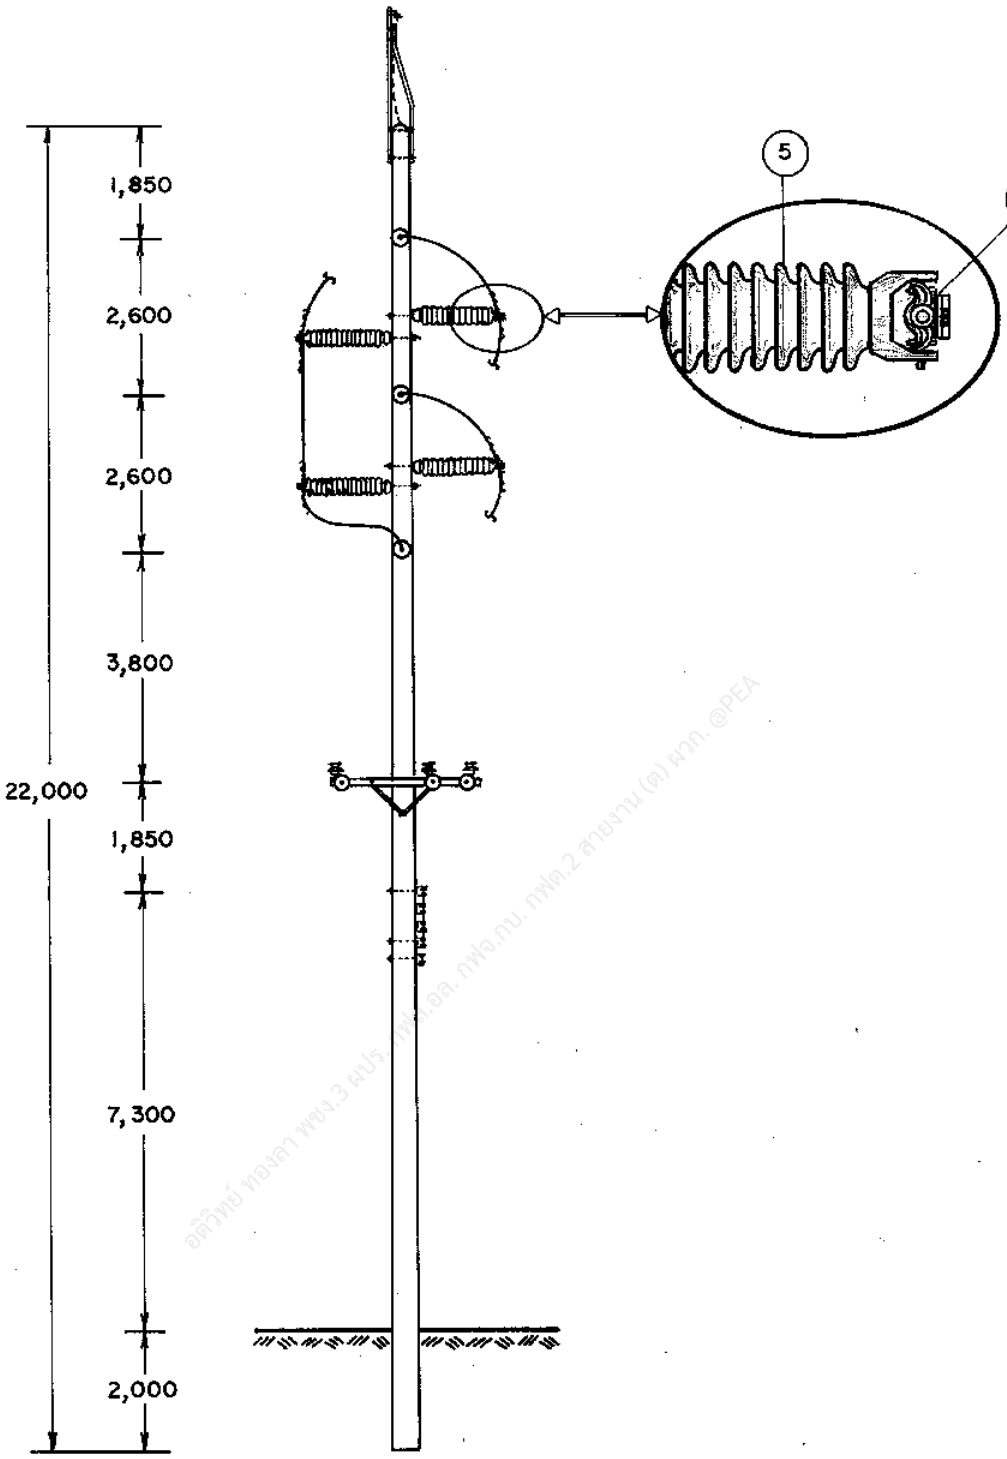

อดิวิทย์ ทองลา พชง.3 ผปร. กฟฟ.อล. กฟจ.กบ. กฟต.2 สายงาน (ต) ผวก. @PEA

กองวิศวกรรมไฟฟ้าและเครื่องกล
ฝ่ายวิศวกรรม

ผู้เขียน ____
ผู้ตรวจ ____
วิศวกร ____
หัวหน้าแผนก ____
ผู้อำนวยการกอง ____
ผู้อำนวยการฝ่าย ____

รองผู้ว่าการฝ่ายเทคนิค

การไฟฟ้าส่วนภูมิภาค

ผู้ว่าการ ____ 10 มี.ค.35

115 kV วงจรเดี่ยว สายไฟฟ้าเดี่ยว
เสาสำหรับสลับเฟสสาย
แบบ SS-TR-1

115 kV SINGLE CIRCUIT SINGLE CONDUCTOR
TRANSPOSE STRUCTURE
TYPE SS-TR-1

ใช้แทนแบบ ____
ถูกแทนโดยแบบ ____
เขียนเสร็จวันที่ 2 มี.ค.35
แก้แบบวันที่ ____
มิติเป็น มิลลิเมตร
มาตราส่วน 1 : 125
แบบเลขที่ SAI-015/35007
แผ่นที่ 1 ของจำนวน 3 แผ่น

10 มี.ค. 2535

การประกอบเลขที่
ASSEMBLY NO. 5214

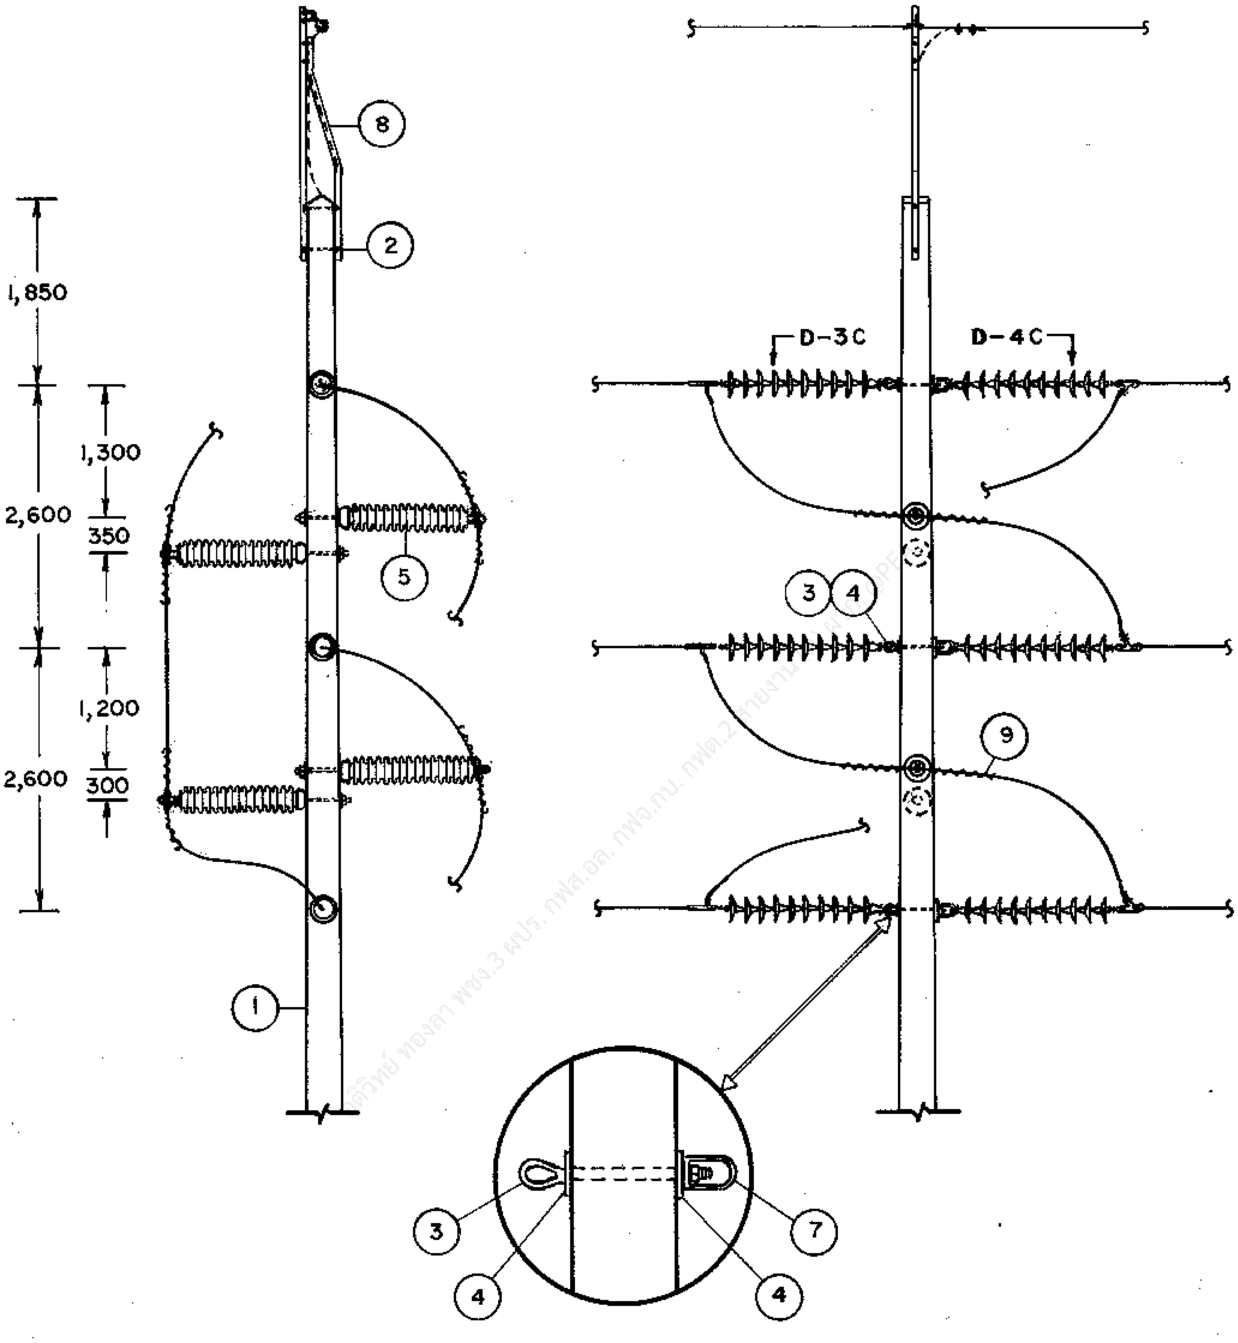
8
2
1,850
1,300
2,600
350
5
1,200
2,600
300
1
D-3C
D-4C
3
4
9
3
4
7
4

กองวิศวกรรมไฟฟ้าและเครื่องกล
ฝ่ายวิศวกรรม

ผู้เขียน ________
ผู้ตรวจ ________
วิศวกร ________
หัวหน้าแผนก ________
ผู้อำนวยการกอง ________
ผู้อำนวยการฝ่าย ________

รองผู้ว่าการฝ่ายเทคนิค

การไฟฟ้าส่วนภูมิภาค

ผู้ว่าการ ________ 10 มี.ค.35

115 kV วงจรเดี่ยว สายไฟฟ้าเดี่ยว
เสาสำหรับสลับเฟสสาย
SS-TR-1

115 kV SINGLE CIRCUIT SINGLE CONDUCTOR
TRANSPOSE STRUCTURE
TYPE SS-TR-1

ใช้แทนแบบ ________
ถูกแทนโดยแบบ ________
เขียนเสร็จวันที่ 2 มี.ค. 35
แก้แบบวันที่ ________
มิติเป็น มิลลิเมตร
มาตราส่วน 1 : 75
แบบเลขที่ SAI-015/35007
แผ่นที่ 2 ของจำนวน 3 แผ่น

10 มี.ค. 2535

การประกอบเลขที่ ASSEMBLY NO. **5214**

บัญชีวัสดุ
BILL OF MATERIAL

ลำดับที่ ITEM	รายละเอียด DESCRIPTION	จำนวน REQ'D	วัสดุเลขที่ MAT NO.
1	เสาคอนกรีต 22 ม. POLE, CONCRETE 22 m LONG	1	00010011 (0041)
2	สลักเกลียว M 16X350 มม. BOLT, MACHINE, M 16X350 mm	3	01110205 (0225)
3	สลักห่วงโอเวล M 20X350 มม. BOLT, OVAL EYE, M 20X350 mm	3	01150100 (0260)
4	แหวนสี่เหลี่ยมแบน 62X62X6 มม. รู ø 22 มม. มอก. 258 WASHER, SQUARE, FLAT, 62X62X6 mm HOLE ø 22 mm TIS 258	12	01180101 (0356)
5	ลูกถ้วย แบบโพสท์ ติดตั้งในแนวนอน ระบบ 115 kV พร้อมอุปกรณ์ประกอบยึดกับเสา (สลักเกลียว M 20X400 มม.) INSULATOR, POST TYPE, HORIZONTAL MOUNTING, 115 kV COMP. WITH ACCESSORIES FOR POLE MOUNTING (BOLT, M 20X400 mm)	4	
6	แคล้มป์จับสาย ใช้ประกอบลูกถ้วย แบบโพสท์ 115 kV CLAMP, TOP TYPE, FOR POST TYPE INSULATOR 115 kV	4	
7	อายเล็ท สำหรับสลักเกลียว M 20 EYELET FOR BOLT, M 20	3	01180002 (0346)
8	เหล็กฉากรับสายล่อฟ้า ทางโค้ง OVERHEAD GROUND WIRE CORNER BAYONET	1	01010005 (0136)
9	ปรีฟอร์มไลน์การ์ด ขนาดตามต้องการ LINE GUARD, PREFORMED SIZE REQUIRED	4	
	รายละเอียด DESCRIPTION		
D-3C	การประกอบลูกถ้วยแขวน SUSPENSION INSULATOR ASSEMBLY	3	
D-4C	การประกอบลูกถ้วยแขวน SUSPENSION INSULATOR ASSEMBLY	3	
D-5A	การต่อสายล่อฟ้า OVERHEAD GROUND WIRE CONNECTION	1	
D-10A	ฐานรากเสา POLE FOUNDATION	1	

อดิวิทย์ ทองลา [illegible] 3 ผบร. กฟส.อล. กฟจ.กบ. กฟต.2 สายงาน (ฉ) ผวก. @PEA

กองวิศวกรรมไฟฟ้าและเครื่องกล
ฝ่ายวิศวกรรม

ผู้เขียน
ผู้สำรวจ
วิศวกร
หัวหน้าแผนก
ผู้อำนวยการกอง
ผู้อำนวยการการ

รองผู้ว่าการฝ่ายเทคนิค

การไฟฟ้าส่วนภูมิภาค

ผู้จัดการ 10 มี.ค. 35

115 kV วงจรเดี่ยว สายไฟฟ้าเดี่ยว
เสาสำหรับสลับเฟสสาย
แบบ SS-TR-1

115 kV SINGLE CIRCUIT SINGLE CONDUCTOR
TRANSPOSE STRUCTURE
TYPE SS-TR-1

ใช้แทนแบบ
ถูกแทนโดยแบบ
เขียนเสร็จวันที่ 2 มี.ค. 35
แก้แบบวันที่
มิติเป็น
มาตราส่วน
แบบเลขที่ SAI-015/35007
แผ่นที่ 3 ของจำนวน 3 แผ่น

10 มี.ค. 2535