การประกอบเลขที่ ASSEMBLY NO. **5 2 8 5**

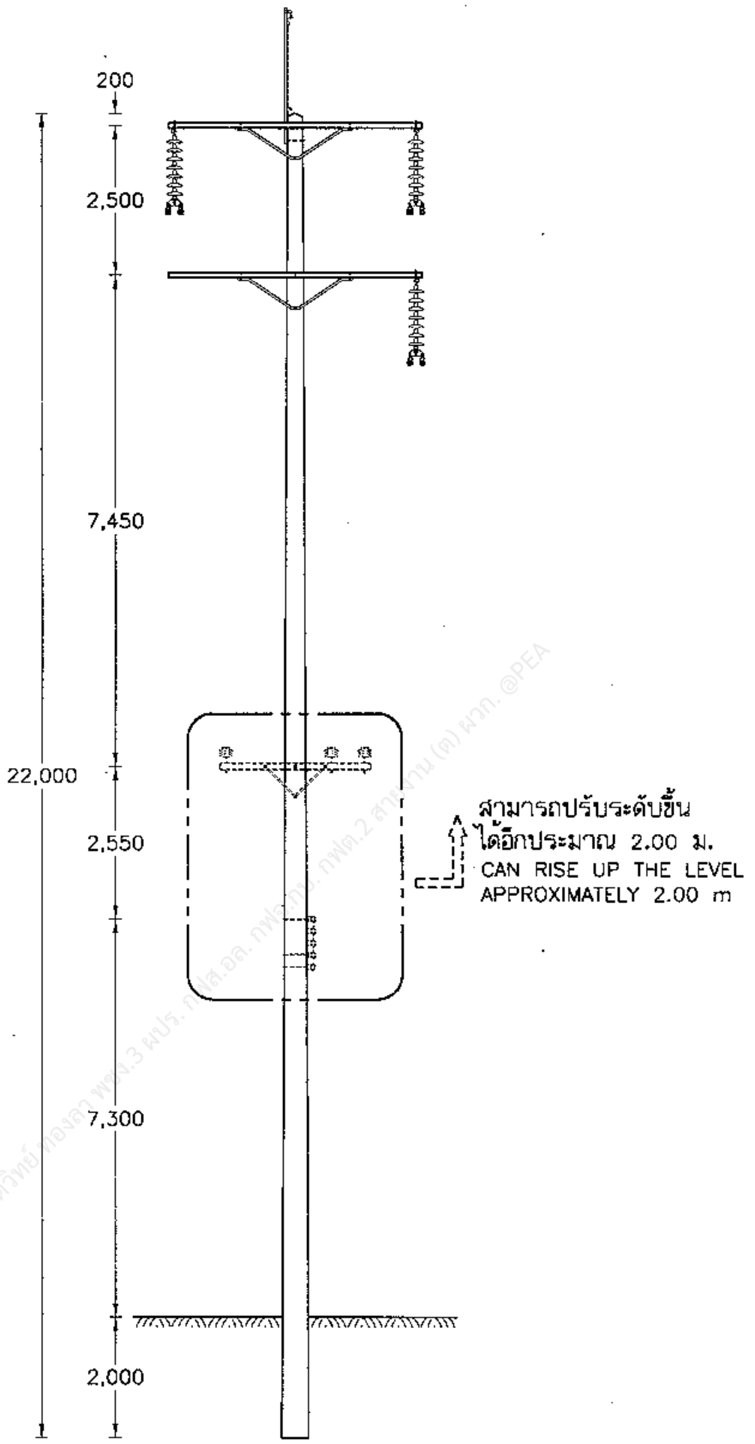

สามารถปรับระดับขึ้นได้อีกประมาณ 2.00 ม.
CAN RISE UP THE LEVEL APPROXIMATELY 2.00 m

อติวิทย์ ทองลา พชง.3 ผปร. กฟส.อล. กฟจ.กบ. กฟต.2 สายงาน (ต) ผวก. @PEA

กองวิศวกรรมไฟฟ้าและเครื่องกล
ฝ่ายวิศวกรรม

การไฟฟ้าส่วนภูมิภาค

ผู้เขียน ....
ผู้สำรวจ ....
วิศวกร ....
หัวหน้าแผนก ....
ผู้อำนวยการกอง ....
ผู้อำนวยการฝ่าย ....
รองผู้ว่าการเทคนิคและบริการ ....

ผู้ว่าการ ....

- 3 ส.ค. 2542

115 kV วงจรเดียว สายไฟฟ้าคู่
เสาสำหรับทางตรง
แบบ SD-TG-8

115 kV SINGLE CIRCUIT, DOUBLE CONDUCTOR
TANGENT STRUCTURE
TYPE SD-TG-8

ใช้แทนแบบ ....
ถูกแทนโดยแบบ ....
เขียนเสร็จวันที่ 22 ก.พ. 2542
แก้แบบวันที่ ....
มิติเป็น มิลลิเมตร
มาตราส่วน 1 : 125
แบบเลขที่ SA1-015/42008
แผ่นที่ 1 ของจำนวน 3 แผ่น

- 3 ส.ค. 2542

การประกอบเลขที่
ASSEMBLY NO. **5285**

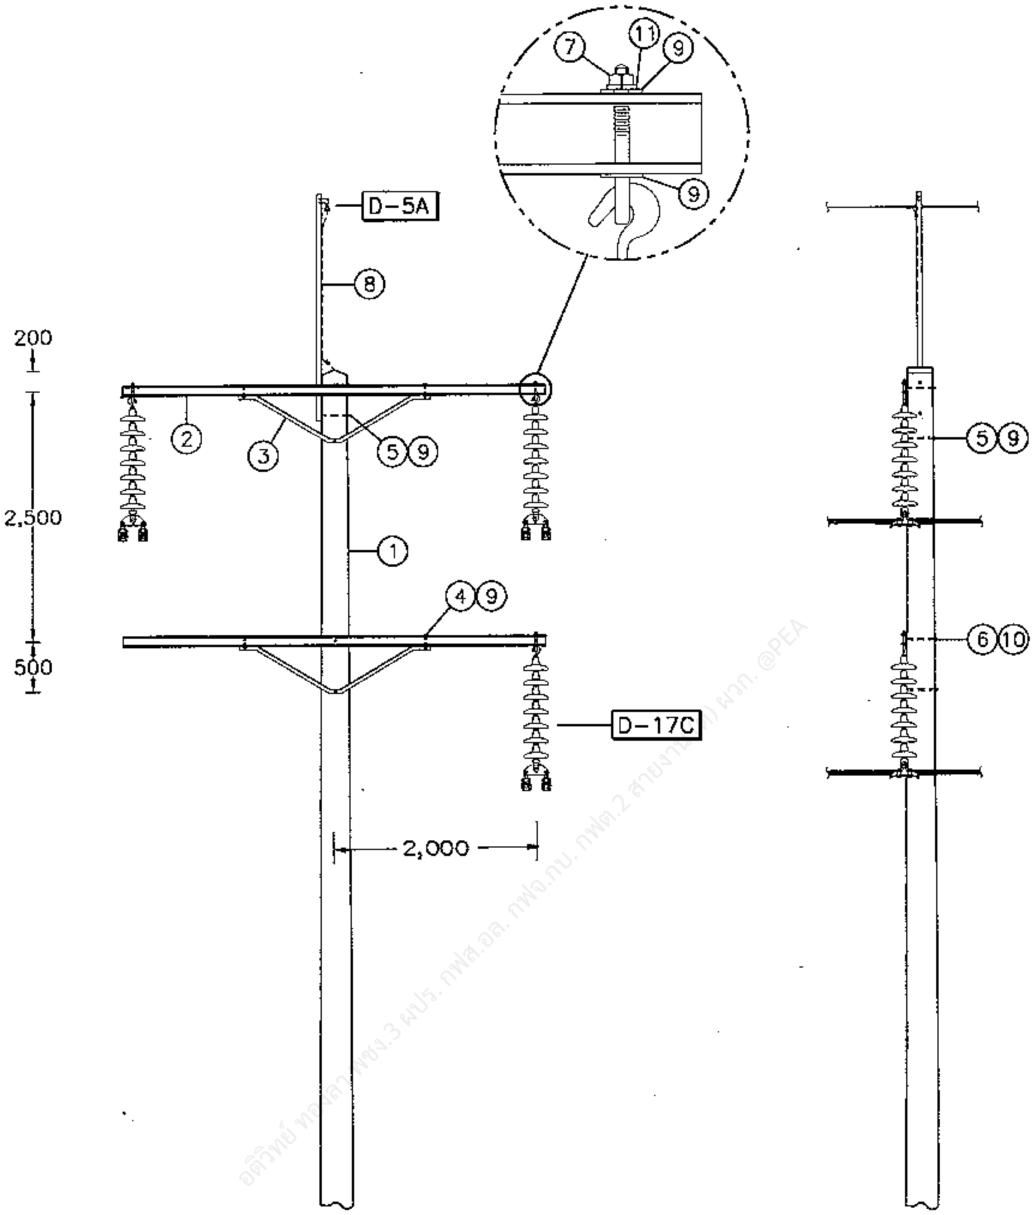

อดิวิทย์ ทองลา พชง.3 ผปร. กฟส.อล. กฟจ.กบ. กฟต.2 สายงาน[illegible] ผวก. @PEA

กองวิศวกรรมไฟฟ้าและเครื่องกล
ฝ่ายวิศวกรรม

การไฟฟ้าส่วนภูมิภาค

ใช้แทนแบบ ....
ถูกแทนโดยแบบ ....

ผู้เขียน ....
ผู้สำรวจ....................
วิศวกร.....................
หัวหน้าแผนก...............
ผู้อำนวยการกอง.............
ผู้อำนวยการฝ่าย............
รองผู้ว่าการเทคนิคและบริการ
....

ผู้ว่าการ.................................... - 3 ส.ค. 2542

115 kV วงจรเดียว สายไฟฟ้าคู่
เสาสำหรับทางตรง
แบบ SD-TG-8

115 kV SINGLE CIRCUIT, DOUBLE CONDUCTOR
TANGENT STRUCTURE
TYPE SD-TG-8

เขียนเสร็จวันที่ 22 ก.พ. 2542
แก้แบบวันที่ ....
มิติเป็น มิลลิเมตร
มาตราส่วน 1 : 75
แบบเลขที่ SA1-015/42008
แผ่นที่ 2 ของจำนวน 3 แผ่น

- 3 ส.ค. 2542

การประกอบเลขที่ ASSEMBLY NO. **5285**

บัญชีวัสดุ
BILL OF MATERIAL

ลำดับที่ ITEM	รายละเอียด DESCRIPTION	จำนวน REQ'D	วัสดุเลขที่ MAT. NO.
1	เสาคอนกรีต 22 ม. POLE, CONCRETE 22 m LONG	1	00010011
2	คอนสายแบบเหล็กรูปรางน้ำ 100x50x5 มม. ยาว 4.20 ม. มอก. 116 CROSSARM, STEEL, CHANNEL 100x50x5 mm, 4.20 m LONG TIS 116	2	01000103
3	เหล็กฉากรับคอนสายขนาด 50x50x6 มม. ช่วงกว้าง 1,800 มม. ดรอพ 450 มม. BRACE, ANGLE STEEL, 50X50X6 mm, 1,800 mm WIDE 450 mm DROP	2	00120007
4	สลักเกลียว M 16x130 มม. BOLT, MACHINE M 16x130 mm	4	01110200
5	สลักเกลียว M 16x350 มม. BOLT, MACHINE M 16x350 mm	5	01110206
6	สลักเกลียว M 20x400 มม. BOLT, MACHINE M 20x400 mm	2	01110301
7	สลักห่วงโอแวล M 16x150 มม. BOLT, OVAL EYE M 16x150 mm	3	01150000
8	เหล็กฉากรับสายล่อฟ้าทางตรง ยาว 2.50 ม. OVERHEAD GROUND WIRE BAYONET 2.50 m LONG	1	01010004
9	แหวนสี่เหลี่ยมแบน 52x52x4.5 มม. รู ø18 มม. มอก. 258 WASHER, SQUARE FLAT 52x52x4.5 mm HOLE ø18 mm TIS 258	14	01180100
10	แหวนสี่เหลี่ยมแบน 62x62x6 มม. รู ø22 มม. มอก. 258 WASHER, SQUARE FLAT 62x62x6 mm HOLE ø22 mm TIS 258	2	01180101
11	แหวนสปริง M 16 มอก. 259 WASHER, LOCK M 16 TIS 259	3	01180301

รายละเอียด
DETAIL

D-17C	การประกอบลูกถ้วยแขวน SUSPENSION INSULATOR ASSEMBLY	3	
D-5A	การต่อสายล่อฟ้า OVERHEAD GROUND WIRE CONNECTION	1	
* D-10A	ฐานรากเสา POLE FOUNDATION	1	

* สามารถเปลี่ยนได้ตามความเหมาะสม
CAN BE CHANGEDTO BE SUITABLE

กองวิศวกรรมไฟฟ้าและเครื่องกล
ฝ่ายวิศวกรรม

การไฟฟ้าส่วนภูมิภาค

ใช้แทนแบบ ....
ถูกแทนโดยแบบ ....

ผู้เขียน ....
ผู้สำรวจ ....
วิศวกร ....
หัวหน้าแผนก ....
ผู้อำนวยการกอง ....
ผู้อำนวยการฝ่าย ....

ผู้ว่าการ ....

3 ส.ค. 2542

เขียนเสร็จวันที่ 22 ก.พ. 2542
แก้แบบวันที่ ....
มิติเป็น ....
มาตราส่วน ....

115 kV วงจรเดียว สายไฟฟ้าคู่
เสาสำหรับทางตรง
แบบ SD-TG-8

รองผู้ว่าการเทคนิคและบริการ
....

115 kV SINGLE CIRCUIT, DOUBLE CONDUCTOR
TANGENT STRUCTURE
TYPE SD-TG-8

แบบเลขที่ SA1-015/42008
แผ่นที่ 3 ของจำนวน 3 แผ่น

- 3 ส.ค. 2542

อดิวิทย์ ทองลา พฟง.3 ผปร. กฟส.อล. กฟจ.กบ. กฟต.2 สายงาน (ต) [illegible] @PEA