

การประกอบเลขที่ ASSEMBLY NO.	0557

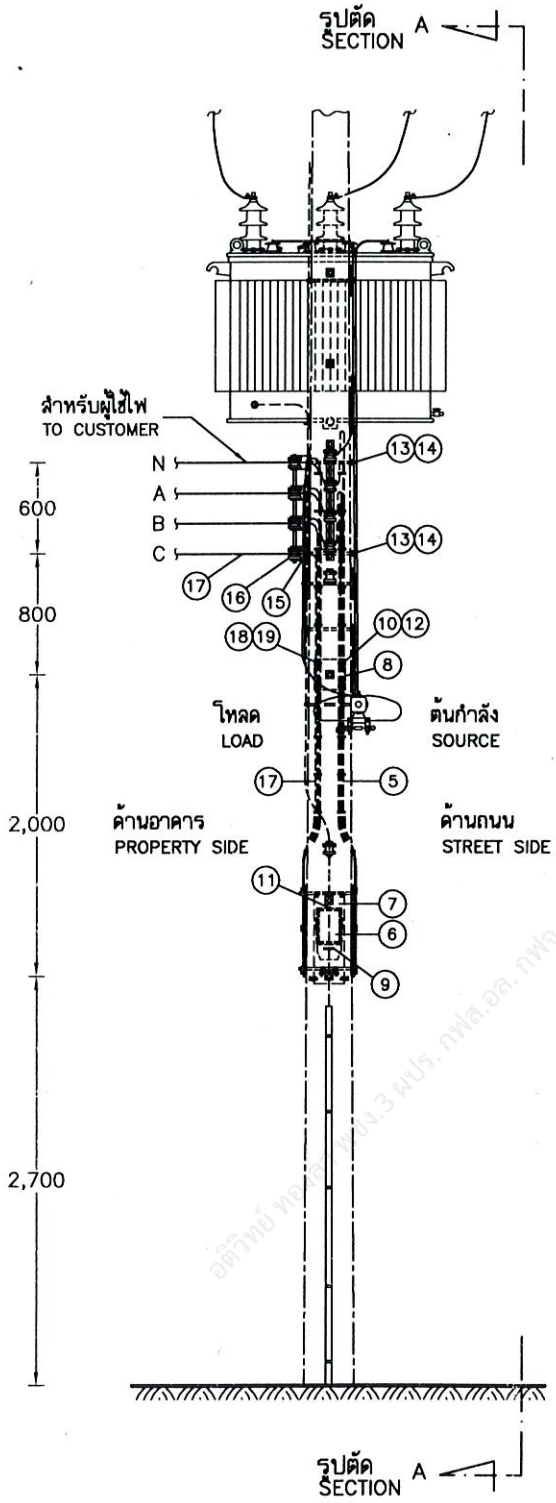

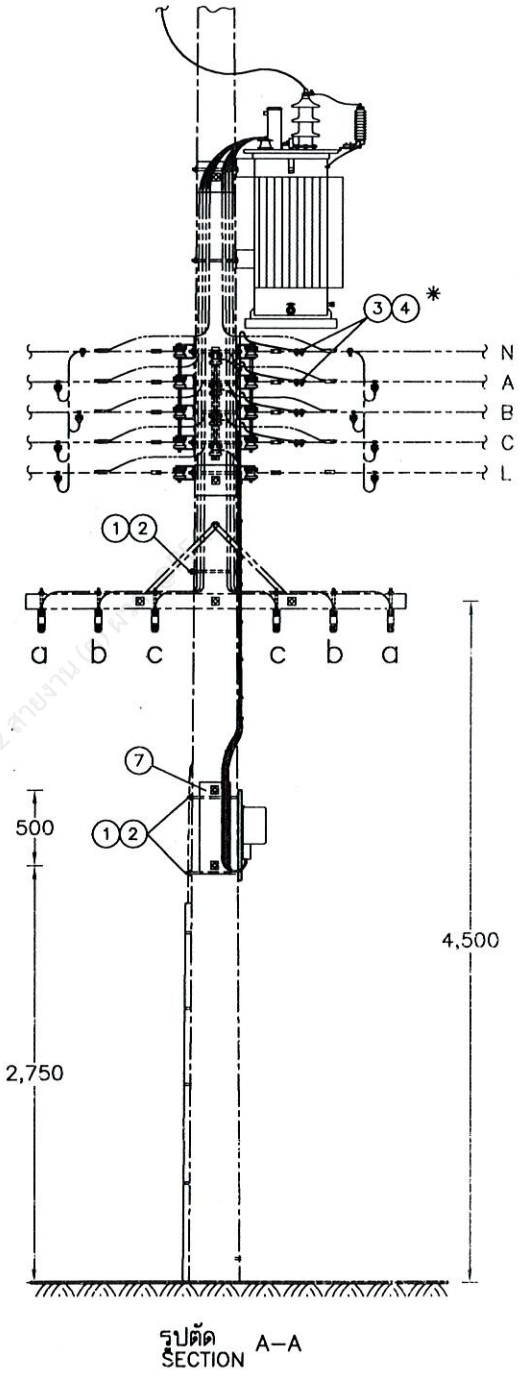

กองวิศวกรรมระบบไฟฟ้า ฝ่ายวิศวกรรม	การไฟฟ้าส่วนภูมิภาค	ใช้แทนแบบ ..... ถูกแทนโดยแบบ .....
ผู้เขียน Supphakit Boonreung ผู้สำรวจ ..... วิศวกร Supphakit Boonreung หัวหน้าแผนก อนุวัตร ผู้อำนวยการกอง ..... ผู้อำนวยการฝ่าย	ผู้ว่าการ ..... 13 ธ.ค. 2564 (แทน) การติดตั้งอิเล็กทรอนิกส์มิเตอร์พร้อมระบบสื่อสารไร้สาย 3 เฟส 230/400 โวลต์ ขนาด 5 (100) แอมแปร บนเสาต้นติดตั้งหม้อแปลง แขวนบนเสาเดี่ยว	เขียนเสร็จวันที่ 26 พ.ย. 2564 แก้แบบวันที่ ..... มิติเป็น มิลลิเมตร มาตราส่วน 1 : 50
รองผู้ว่าการสายงานวิศวกรรม	5(100) A, 3–PHASE, 230/400 V ELECTRONIC METER WITH WIRELESS COMMUNICATION INSTALLATION ON SINGLE POLE WITH TRANSFORMER	แบบเลขที่ SA4–015/64022 แผ่นที่ 1 ของจำนวน 4 แผ่น

การประกอบเลขที่ ASSEMBLY NO. 0557

บัญชีวัสดุ BILL OF MATERIAL


ลำดับที่ ITEM		รายละเอียด DESCRIPTION	จำนวน REQ'D	วัสดุเลขที่ MAT. NO.
		บัญชีวัสดุในส่วนที่ กฟภ. ลงทุน BILL OF MATERIAL FOR PEA		
1		สลักเกลียว M 16 x 300 มม. สำหรับเสาคอนกรีต 12.00 ม. BOLT, MACHINE, M 16 x 300 mm FOR 12.00 m CONCRETE POLE	5	1010110204
		สลักเกลียว M 16 x 350 มม. สำหรับเสาคอนกรีต 12.20, 14.00 ม. BOLT, MACHINE, M 16 x 350 mm FOR 12.20, 14.00 m CONCRETE POLE		1010110205
		สลักเกลียว M 16 x 400 มม. สำหรับเสาคอนกรีต 14.30, 16.00 ม. BOLT, MACHINE, M 16 x 400 mm FOR 14.30, 16.00 m CONCRETE POLE		1010110206
2		แหวนสี่เหลี่ยมแบน 52x52x4.5 มม. รู ø 18 มม. มอก. 258 WASHER, SQUARE, FLAT 52x52x4.5 mm HOLE ø18 mm TIS 258	10	1010180100
3		คอนเนคเตอร์ชนิดบีบ แบบ H ขนาดตามต้องการ CONNECTOR, COMPRESSION, H TYPE ; SIZE AS REQUIRED	4	1020320002-6
4		PVC เทป กว้าง 19 มม. (ใช้ความยาว 2 ม. ต่อ 1 จุด) มอก. 386 PVC TAPE, 19 mm WIDE (2 m LONG PER POINT) TIS 386	ม. m	1020180001 or 1020180002
5	a	สายทองแดง ขนาด 10 ตร.มม. หรือ อะลูมิเนียม 25 ตร.มม. หุ้มฉนวน PVC 600 โวลต์ หรือ 750 โวลต์ สำหรับขนาดโหลดสูงสุดไม่เกิน 36 แอมแปร์ CABLE, Cu, 10 mm^2 or Al, 25 mm^2 , PVC INSULATOR, 600 V or 750 V FOR MAXIMUM LOAD NOT MORE THAN 36 A	22 ม. m	1020070000 1020080608 or 1020080551
	b	สายทองแดง ขนาด 35 ตร.มม. หรือ อะลูมิเนียม 50 ตร.มม. หุ้มฉนวน PVC 600 โวลต์ หรือ 750 โวลต์ สำหรับขนาดโหลดสูงสุดไม่เกิน 80 แอมแปร์ CABLE, Cu, 35 mm^2 or Al, 50 mm^2 , PVC INSULATOR, 600 V or 750 V FOR MAXIMUM LOAD NOT MORE THAN 80 A		1020070002 1020080609 or 1020080552
6		อิเล็กทรอนิกส์มิเตอร์พร้อมระบบสื่อสารไร้สาย 3 เฟส 230/400 โวลต์ 5 (100) แอมป์ 3-PHASE, 230/400 V, 5 (100) A, ELECTRONIC METER WITH WIRELESS COMMUNICATION	1	1060050111
7		แป้นรองรับมิเตอร์ ตกแต่งผิวเรียบร้อยแล้ว ขนาด 60x20x2 ซม. METER PLATE, SURFACE FINISHED, 60x20x2 cm	3	1060100001
8		แป้นสำหรับยึดสาย เข้า และออกจากมิเตอร์ ตกแต่งผิวเรียบร้อยแล้ว ขนาด 20x20x2 ซม. CABLE PLATE, SURFACE FINISHED, 20x20x2 cm	1	1060100000
9		หมายเลขผู้ใช้ไฟ NUMBER OF CUSTOMER	1	-
10		เข็มขัดรัดสาย (ทำด้วยลวดอะลูมิเนียมแบน 1x10 มม.) ช่วงระยะ 25 ซม. CABLE STRAP (MADE OF ARMOUR TAPE 1x10 mm) AT 25 cm INTERVALS	4 ม. m	1020200000
11		ตะปูเกลียวชุบโครเมี่ยม ขนาด 15-20 มม. SCREW, CHROME PLATED, SIZE 15-20 mm	3	
12		ตะปูหัวกลมแบน ยาว 15-20 มม., ø1 มม. มอก.113 NAIL, ROUND MILD STEEL WIRE, 15-20 mm LONG, ø 1 mm TIS 113	20	

กองวิศวกรรมระบบไฟฟ้า ฝ่ายวิศวกรรม	การไฟฟ้าส่วนภูมิภาค	ใช้แทนแบบ ..... ถูกแทนโดยแบบ .....
ผู้เขียน Supphakit Boonreung ผู้สำรวจ ..... วิศวกร Supphakit Boonreung หัวหน้าแผนก อนุวัตร ผู้อำนวยการกอง ..... ผู้อำนวยการฝ่าย	ผู้ว่าการ ..... 13 ธ.ค. 2564 (แทน)	เขียนเสร็จวันที่ 26 พ.ย. 2564 แก้แบบวันที่ ..... มิติเป็น ..... มาตราส่วน .....
รองผู้ว่าการสายงานวิศวกรรม	การติดตั้งอิเล็กทรอนิกส์มิเตอร์พร้อมระบบสื่อสารไร้สาย 3 เฟส 230/400 โวลต์ ขนาด 5 (100) แอมแปร์ บนเสาต้นติดตั้งหม้อแปลง แขวนบนเสาเดี่ยว 5(100) A, 3-PHASE, 230/400 V ELECTRONIC METER WITH WIRELESS COMMUNICATION INSTALLATION ON SINGLE POLE WITH TRANSFORMER	แบบเลขที่ SA4-015/64022 แผ่นที่ 2 ของจำนวน 4 แผ่น

การประกอบเลขที่ ASSEMBLY NO.	0557

บัญชีวัสดุ
BILL OF MATERIAL

ลำดับที่ ITEM		รายละเอียด DESCRIPTION	จำนวน REQ'D	วัสดุเลขที่ MAT. NO.
		บัญชีวัสดุในส่วนของผู้ใช้ไฟ BILL OF MATERIAL FOR CUSTOMER		
13		สลักเกลียว M 16 x 250 มม. สำหรับเสาคอนกรีต 12.00 ม. BOLT, MACHINE, M 16 x 250 mm FOR 12.00 m CONCRETE POLE	2	1010110203
		สลักเกลียว M 16 x 300 มม. สำหรับเสาคอนกรีต 12.20. 14.00 ม. BOLT, MACHINE, M 16 x 300 mm FOR 12.20, 14.00 m CONCRETE POLE		1010110204
		สลักเกลียว M 16 x 350 มม. สำหรับเสาคอนกรีต 14.30, 16.00 ม. BOLT, MACHINE, M 16 x 350 mm FOR 14.30, 16.00 m CONCRETE POLE		1010110205
14		แหวนสี่เหลี่ยมแบน 52x52x4.5 มม. รู ø 18 มม. มอก. 258 WASHER, SQUARE, FLAT 52x52x4.5 mm HOLE ø18 mm TIS 258	2	1010180100
15		แร็ค 4x200 มม. แบบหลังยื่น RACK, SECONDARY, MEDIUM PRESSED STEEL, 4x200 mm, EXTENDED RACK	1	1030130002
16		ลูกรอกแรงต่ำ มอก.227 แบบ ข (แบบ 53-2) INSULATOR, SPOOL TYPE, L.T., TIS 227 TYPE B (CLASS 53-2)	4	1030030000
17	a	สายทองแดง ขนาด 10 ตร.มม. หรือ อะลูมิเนียม 25 ตร.มม. หุ้มฉนวน PVC 750 โวลต์ สำหรับขนาดโหลดสูงสุดไม่เกิน 36 แอมแปร์ CABLE, Cu, 10 mm^2 or Al, 25 mm^2 , PVC INSULATOR, 750 V FOR MAXIMUM LOAD NOT MORE THAN 36 A	ม. m	–
	b	สายทองแดง ขนาด 35 ตร.มม. หรือ อะลูมิเนียม 50 ตร.มม. หุ้มฉนวน PVC 750 โวลต์ สำหรับขนาดโหลดสูงสุดไม่เกิน 80 แอมแปร์ CABLE, Cu, 35 mm^2 or Al, 50 mm^2 , PVC INSULATOR, 750 V FOR MAXIMUM LOAD NOT MORE THAN 80 A		–
18		เข็มขัดรัดสาย (ทำด้วยลวดอะลูมิเนียมแบน 1x10 มม.) ช่วงระยะ 25 ซม. CABLE STRAP (MADE OF ARMOUR TAPE 1x10 mm) AT 25 cm INTERVALS	4 ม. m	1020200000
19		ตะปูหัวกลมแบน ยาว 15-20 มม., ø1 มม. มอก.113 NAIL, ROUND MILD STEEL WIRE, 15-20 mm LONG, ø 1 mm TIS 113	20	

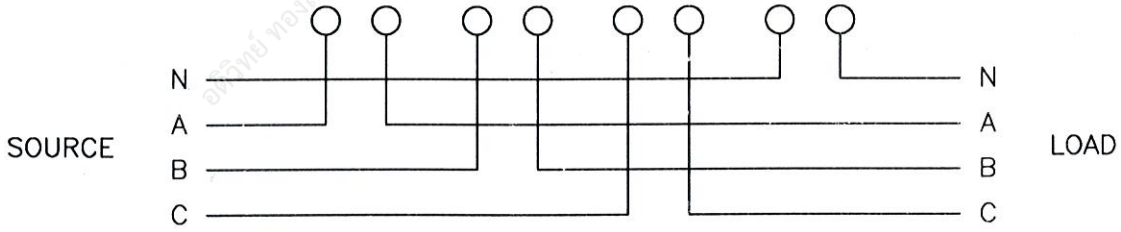

ไดอะแกรมแสดงการต่ออิเล็กทรอนิกส์มิเตอร์พร้อมระบบสื่อสารไร้สาย 3 เฟส 230/400 โวลต์
CONNECTION DIAGRAM FOR 3-PHASE 230/400 V ELECTRONIC METER WITH WIRELESS COMMUNICATION INSTALLATION

กองวิศวกรรมระบบไฟฟ้า ฝ่ายวิศวกรรม	การไฟฟ้าส่วนภูมิภาค	ใช้แทนแบบ ..... ถูกแทนโดยแบบ .....
ผู้เขียน Supphakit Boonreung ผู้สำรวจ ..... วิศวกร Supphakit Boonreung หัวหน้าแผนก อนุวัตร ผู้อำนวยการกอง ..... ผู้อำนวยการฝ่าย 21 ต.ค. 64	ผู้ว่าการ ..... 13 ธ.ค. 2564 (แทน) การติดตั้งอิเล็กทรอนิกส์มิเตอร์พร้อมระบบสื่อสารไร้สาย 3 เฟส 230/400 โวลต์ ขนาด 5 (100) แอมแปร์ บนเสาต้นติดตั้งหม้อแปลง แขวนบนเสาเดี่ยว	เขียนเสร็จวันที่ 26 พ.ย. 2564 แก้แบบวันที่ ..... มิติเป็น ..... มาตราส่วน .....
รองผู้ว่าการสายงานวิศวกรรม –	5(100) A, 3-PHASE, 230/400 V ELECTRONIC METER WITH WIRELESS COMMUNICATION INSTALLATION ON SINGLE POLE WITH TRANSFORMER	แบบเลขที่ SA4-015/64022 แผ่นที่ 3 ของจำนวน 4 แผ่น

การประกอบเลขที่ ASSEMBLY NO.	0557

ข้อแนะนำในการจัดทำเข็มขัดรัดสายด้วยอะลูมิเนียมแบน 1x10 มม.

สายเข้าหรือออกจากมิเตอร์ ใช้ลวดอะลูมิเนียมแบน 1x10 มม. ยาว 15 ซม. ต่อหนึ่งจุด ทุกช่วงระยะ 25 ซม.

หมายเหตุ

* สามารถใช้ INSULATION PIERCING CONNECTOR (IPC) วัสดุเลขที่ 1020360000 ทดแทนวัสดุลำดับที่ ③ และ ④ ได้

	แบบอ้างอิง REFERENCE DRAWING	แบบเลขที่ DWG. No.	การประกอบเลขที่ ASSEMBLY No.
1	หลักเกณฑ์การกำหนดจุดติดตั้งมิเตอร์ และวิธีการเดินสายจากมิเตอร์ถึงตัวอาคาร STANDARD FOR kW-h METERS INSTALLATION AND THE METHOD TO CONNECT CONDUCTOR FROM METER TO CUSTOMER'S BUILDING	SA4-015/61011	0526
2	การเดินสายไฟฟ้า จากเสาต้นติดตั้งมิเตอร์ถึงตัวอาคารของผู้ใช้ไฟ CABLE CONNECTION FROM METER ON THE POLE TO CUSTOMER'S BUILDING	SA4-015/61010	0542
3	การเข้าปลายสายแรงต่ำด้วยลวดอะลูมิเนียมกลม L.T. DEAD-ENDING WITH ALUMINIUM TIE WIRE	SA1-015/21006	9529
4	คอนเนคเตอร์ชนิดบีบ แบบ H สำหรับใช้งานในระบบจำหน่ายแรงต่ำ COMPRESSION CONNECTOR, H-TYPE USE IN L.T. DISTRIBUTION SYSTEM	SA1-015/26021	9530
5	การติดตั้งอุปกรณ์ต่อแยกสายแรงต่ำแบบทุ่มฉนวน ในระบบจำหน่ายแรงต่ำ INSULATION PIERCING CONNECTOR (IPC) INSTALLATION FOR LOW VOLTAGE DISTRIBUTION SYSTEM	SA4-015/62004	9531
6	การติดตั้งอิเล็กทรอนิกส์มิเตอร์พร้อมระบบสื่อสารไร้สาย 1 เฟส 230 โวลต์ และ 3 เฟส 230/400 โวลต์ ขนาด 5(100) แอมแปร์ บนแป้นรองรับมิเตอร์ 5(100) A, 1 PHASE, 230 V AND 3-PHASE, 230/400 V ELECTRONIC METER WITH WIRELESS COMMUNICATION INSTALLATION ON METER PLATE	SA4-015/64024	0532 A

กองวิศวกรรมระบบไฟฟ้า ฝ่ายวิศวกรรม	การไฟฟ้าส่วนภูมิภาค	ใช้แทนแบบ ..... ถูกแทนโดยแบบ .....
ผู้เขียน Supphakit Boonreung ผู้สำรวจ ..... วิศวกร Supphakit Boonreung หัวหน้าแผนก อนุวัตร ผู้อำนวยการกอง ..... ผู้อำนวยการฝ่าย	ผู้ว่าการ ..... 13 ธ.ค. 2564 (แทน) การติดตั้งอิเล็กทรอนิกส์มิเตอร์พร้อมระบบสื่อสารไร้สาย 3 เฟส 230/400 โวลต์ ขนาด 5 (100) แอมแปร์ บนเสาต้นติดตั้งหม้อแปลง แขวนบนเสาเดี่ยว	เขียนเสร็จวันที่ 26 พ.ย. 2564 แก้แบบวันที่ ..... มิติเป็น ..... มาตราส่วน .....
รองผู้ว่าการสายงานวิศวกรรม	5(100) A, 3-PHASE, 230/400 V ELECTRONIC METER WITH WIRELESS COMMUNICATION INSTALLATION ON SINGLE POLE WITH TRANSFORMER	แบบเลขที่ SA4-015/64022 แผ่นที่ 4 ของจำนวน 4 แผ่น