

กางประกอบเลขที่ 3811
ASSEMBLY NO.

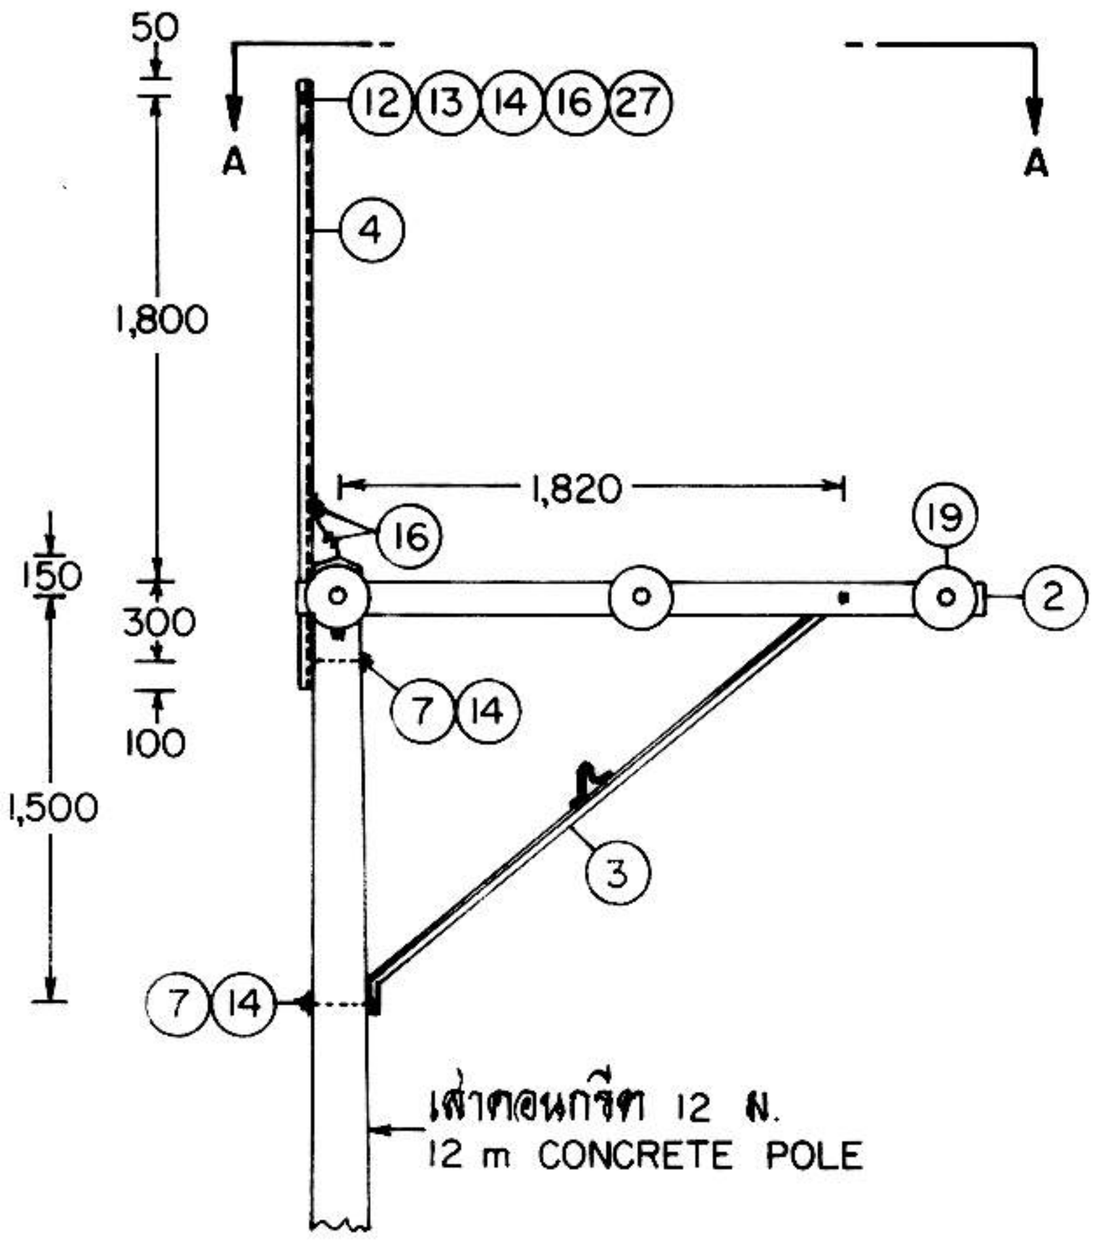


DEA – 1

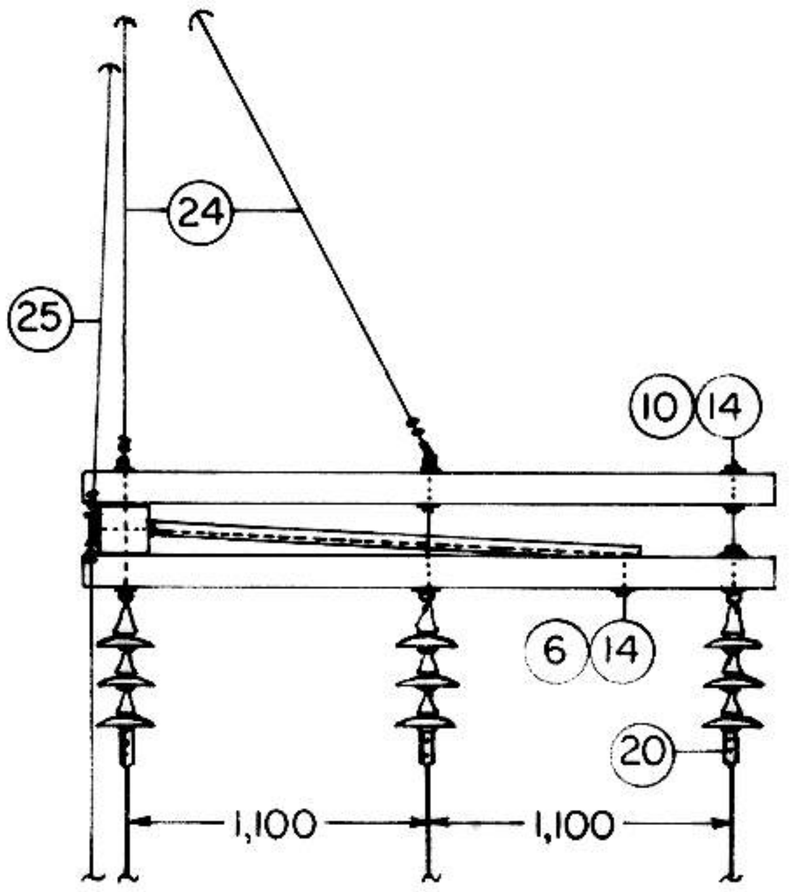

ช่วงรับแรงดึง
TENSION SPAN

รูปตัด
SECTION A – A

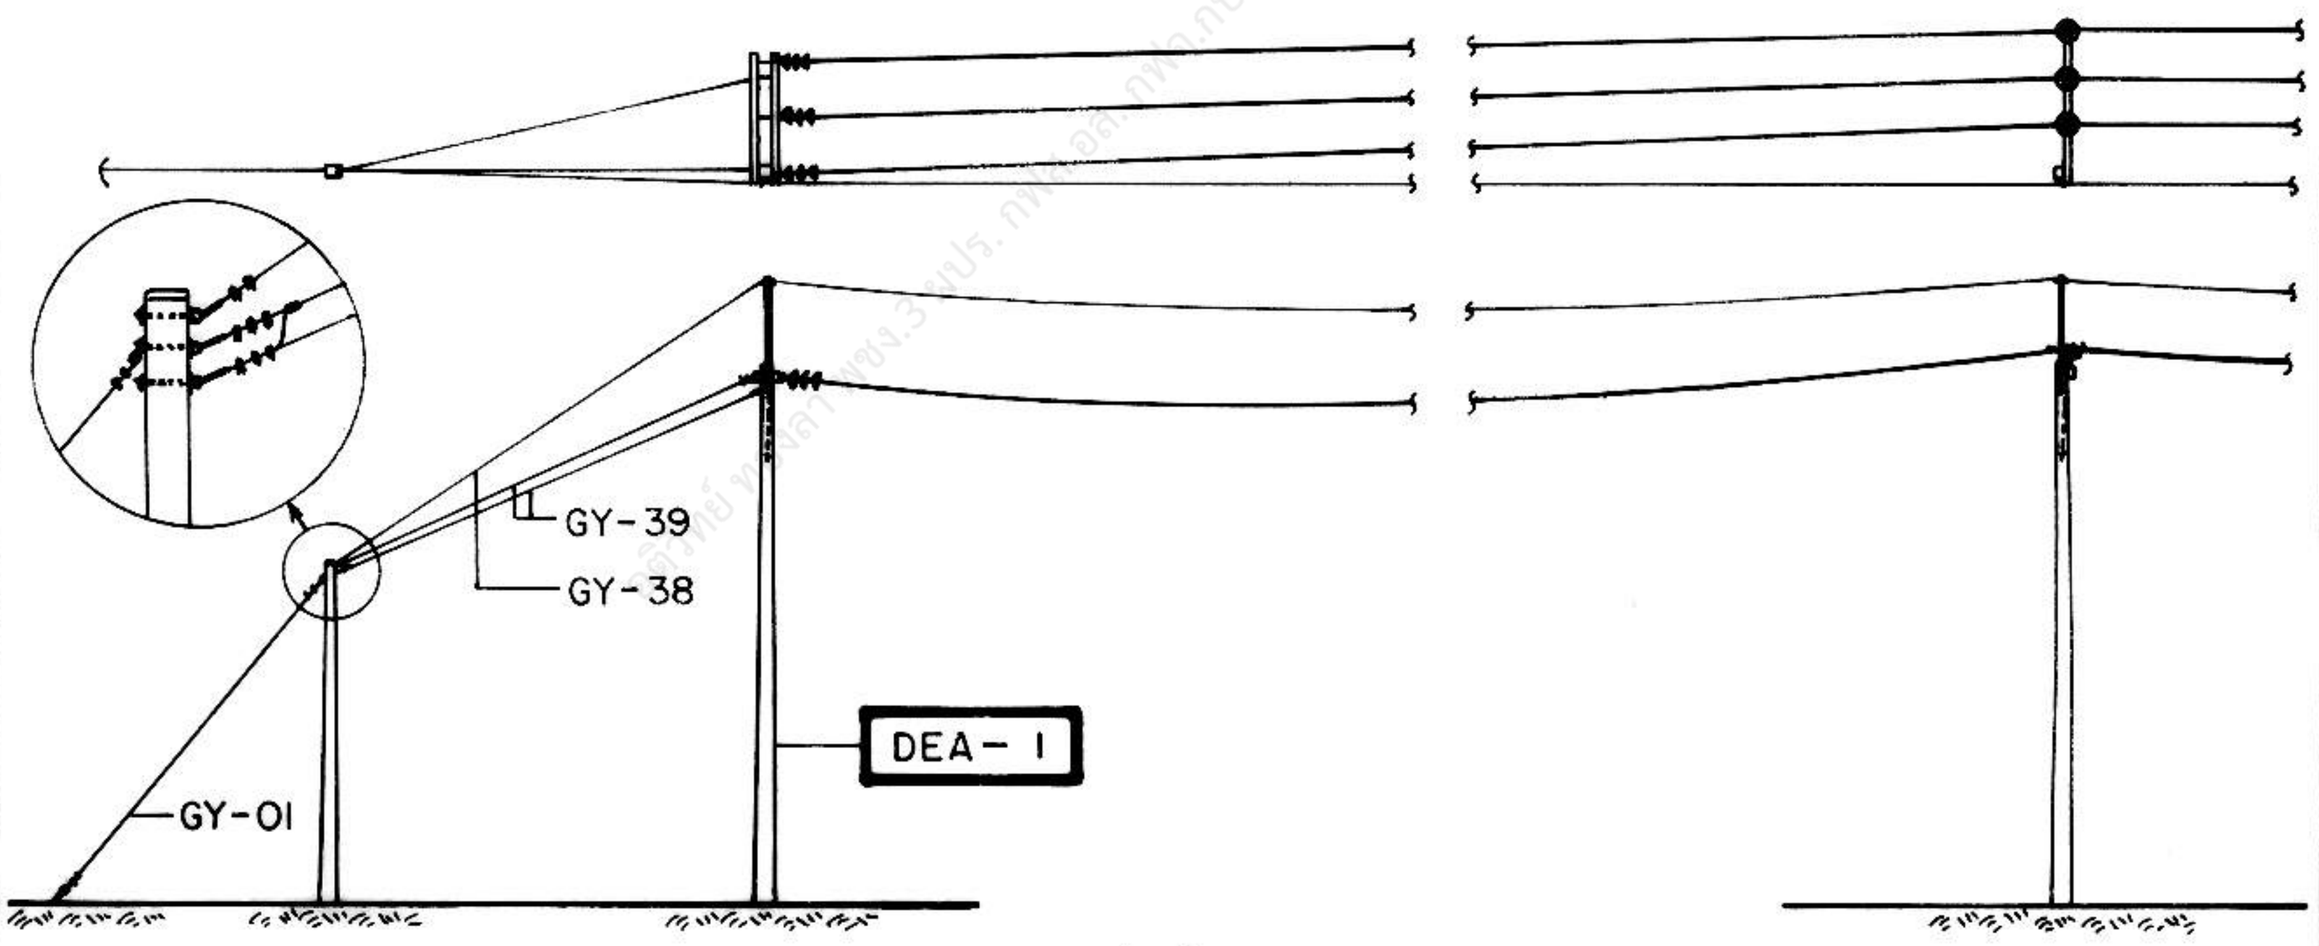

~ 5-8 ม./m — ช่วงรับแรงดึง TENSION SPAN ≤ 50 ม./m

กองวิศวกรรมไฟฟ้าและเครื่องกล ฝ่ายวิศวกรรม	การไฟฟ้าส่วนภูมิภาค	ใช้แทนแบบ ถูกแทนโดยแบบ เขียนเสร็จวันที่ 6 มี.ค. 35 แก้แบบวันที่ มิติเป็น มิลลิเมตร มาตราส่วน 1 : 50, 1 : 125
ผู้เขียน ผู้สำรวจ วิศวกร สมพร หัวหน้าแผนก ผู้อำนวยการกอง ผู้อำนวยการฝ่าย	ผู้ว่าการ 27 เม.ย. 2535 การติดตั้งอุปกรณ์ที่เสาเข้าปลายสายแบบท้าวแขน (กรณีใช้ดอนดอนกรีต) ระบบ 33 kV	
รองผู้ว่าการฝ่ายเทคนิค 21 เม.ย. 2535	DEADEND CONSTRUCTION ON ALLEY ARM (CONCRETE CROSSARM) 33 kV SYSTEM	แบบเลขที่ SAI-015/35009 แผ่นที่ 1 จากจำนวน 6 แผ่น

การประกอบเลขที่ ASSEMBLY NO. 3811

ช่วงไม่รับแรงดึง
SLACK SPAN

ช่วงรับแรงดึง
TENSION SPAN

1,220

850

500

ดูหมายเหตุ
SEE NOTE

BAS – 3

DAS – 2

ดูหมายเหตุ
SEE NOTE

100 ± 50

1,600

150 100 300

1,000

1,500

50 ± 100

1,600

100 150 300

1,500

ห้ามจึงพาดสายให้มีระยะหย่อนยานเกิน 1.00 ม.
MAX. STRINGING SAG OF COND. SHALL NOT EXCEED 1.00 m .

เสาคอนกรีต 12 ม.
12 m CONCRETE POLE

วงจรประธาน
MAIN CIRCUIT

วงจรย่อย
LATERAL CIRCUIT

กองวิศวกรรมไฟฟ้าและเครื่องกล
ฝ่ายวิศวกรรม

ผู้เขียน ...
ผู้สำรวจ
วิศวกร ...
หัวหน้าแผนก ...
ผู้อำนวยการกอง ...
ผู้อำนวยการฝ่าย ...

ของผู้ว่าการฝ่ายเทคนิค
21 เม.ย. 2535

การไฟฟ้าส่วนภูมิภาค

ผู้ว่าการ ... 22 เมย 2535


การติดตั้งอุปกรณ์ที่เสาเข้าปลายสายแบบท้าวแขน
(กรณีใช้คอนคอนกรีต)
ระบบ 33 kV

DEADEND CONSTRUCTION ON ALLEY ARM
(CONCRETE CROSSARM)
33 kV SYSTEM

ใช้แทนแบบ
ถูกแทนโดยแบบ
เขียนเสร็จวันที่ 6 มี.ค. 35
แก้แบบวันที่
มิติเป็น มิลลิเมตร
มาตราส่วน 1 : 50

แบบเลขที่ SAI-015/35009
แผ่นที่ 2 ของสำนวน 6 แผ่น

การประกอบเสาที่ 3811
ASSEMBLY NO.

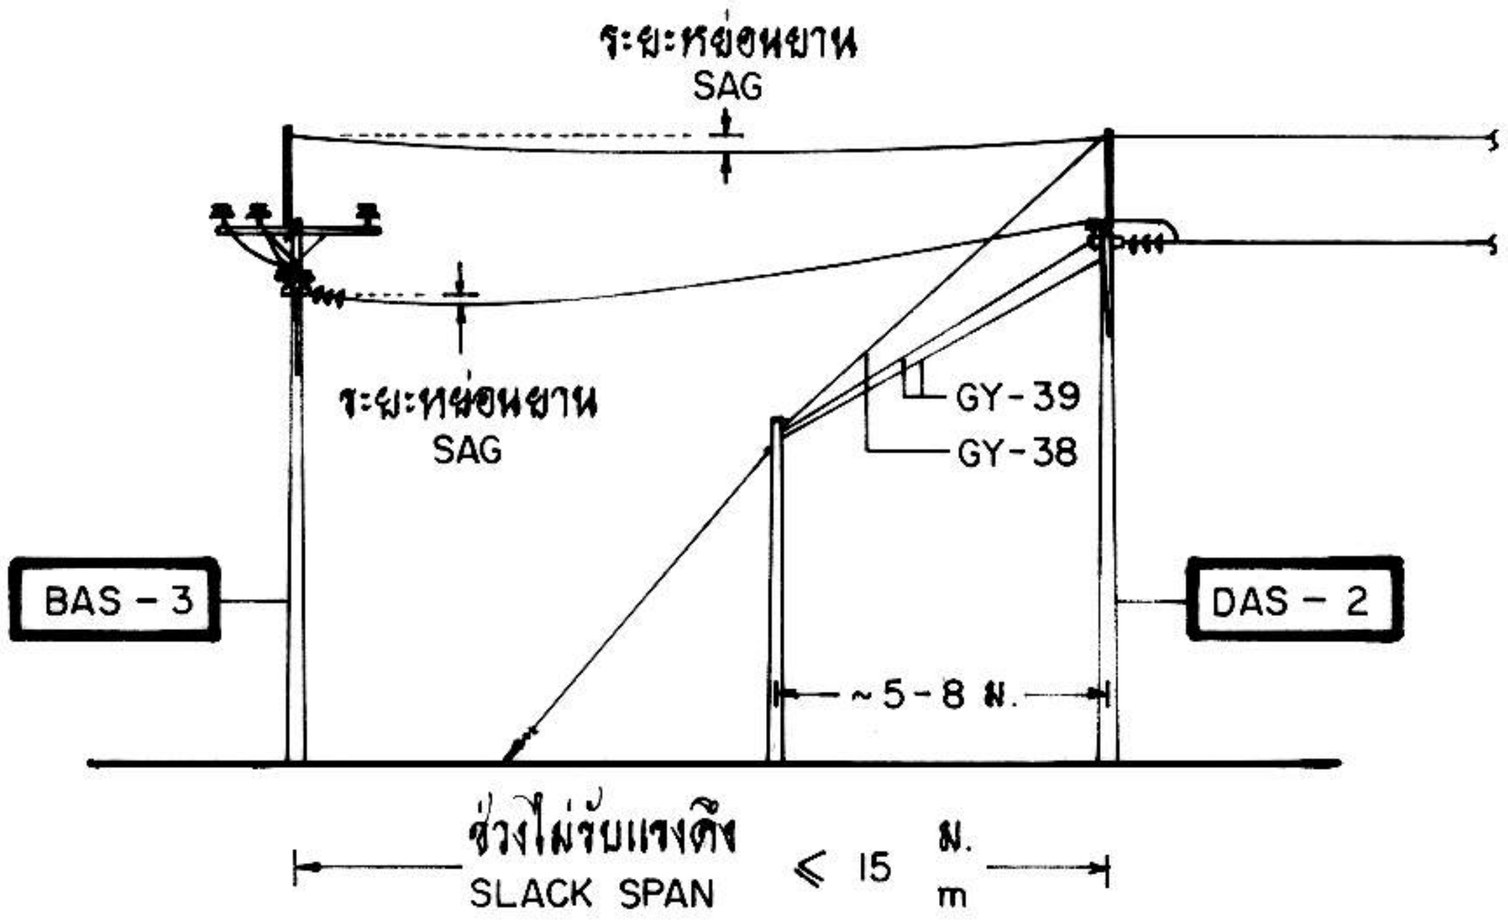

ข้อกำหนดการใช้งาน (BAS-3, DAS-2)

1. ระยะห่างช่วงเสาไม่รับแรงดึงสูงสุด : 15 ม.
2. ระยะห่างเสาในวงจรประธาน ต้องไม่เกิน 50 ม.
3. ขนาดสายของวงจรย่อย :
   สายอะลูมิเนียมเปลือย 95 - 185 ต.มม.
4. ให้ขึงพาดสายช่วงไม่รับแรงดึง มีระยะหย่อนยาน ดังนี้ :

RECOMMENDATIONS (BAS-3, DAS-2)

1. MAXIMUM SLACK SPAN LATERAL LENGTH : 15 m .
2. THE SPAN IN MAIN LINE SHALL NOT BE EXCEEDED 50 m .
3. CONDUCTOR SIZE OF LATERAL CIRCUIT :
   BARE AI CONDUCTOR 95 - 185 mm^2
4. SAG OF CONDUCTOR FOR RULING OF SLACK SPAN :

ระยะห่างเสา SPAN LENGTH	ม. m	≤ 10	> 10 — 15
ระยะหย่อนยานของสาย SAG OF CONDUCTORS	ม. m	0.50 — 0.60	0.70 — 0.80


กองวิศวกรรมไฟฟ้าและเครื่องกล ฝ่ายวิศวกรรม	**การไฟฟ้าส่วนภูมิภาค**	ใช้แทนแบบ ถูกแทนโดยแบบ
ผู้เขียน ผู้สำรวจ วิศวกร หัวหน้าแผนก ผู้อำนวยการกอง ผู้อำนวยการฝ่าย	ผู้ว่าการ 22 เมษ. 2535	เขียนเสร็จวันที่ 6 มี.ค. 35 แก้แบบวันที่ มิติเป็น มาตราส่วน
ของผู้ว่าการฝ่ายเทคนิค	การติดตั้งอุปกรณ์ที่เสาเข้าปลายสายแบบท้าวแขน (กรณีใช้คอนกรีต) ระบบ 33 kV	
	DEADEND CONSTRUCTION ON ALLEY ARM (CONCRETE CROSSARM) 33 kV SYSTEM	แบบเลขที่ SAI-015/35009 แผ่นที่ 3 ของจำนวน 6 แผ่น

21 เม.ย. 2535

การประกอบเลขที่ ASSEMBLY NO.	38N


5. ในกรณีที่ไม่สามารถทำการยึดโยงเสาแยกต้นแรกได้ ให้ติดตั้งในลักษณะตามแผนข้างล่างได้

5. IN CASE OF FIRST LATERAL LINE POLE CAN NOT BE GUYED, INSTALLATION AS FIGURE BELOW MAY BE APPLIED .

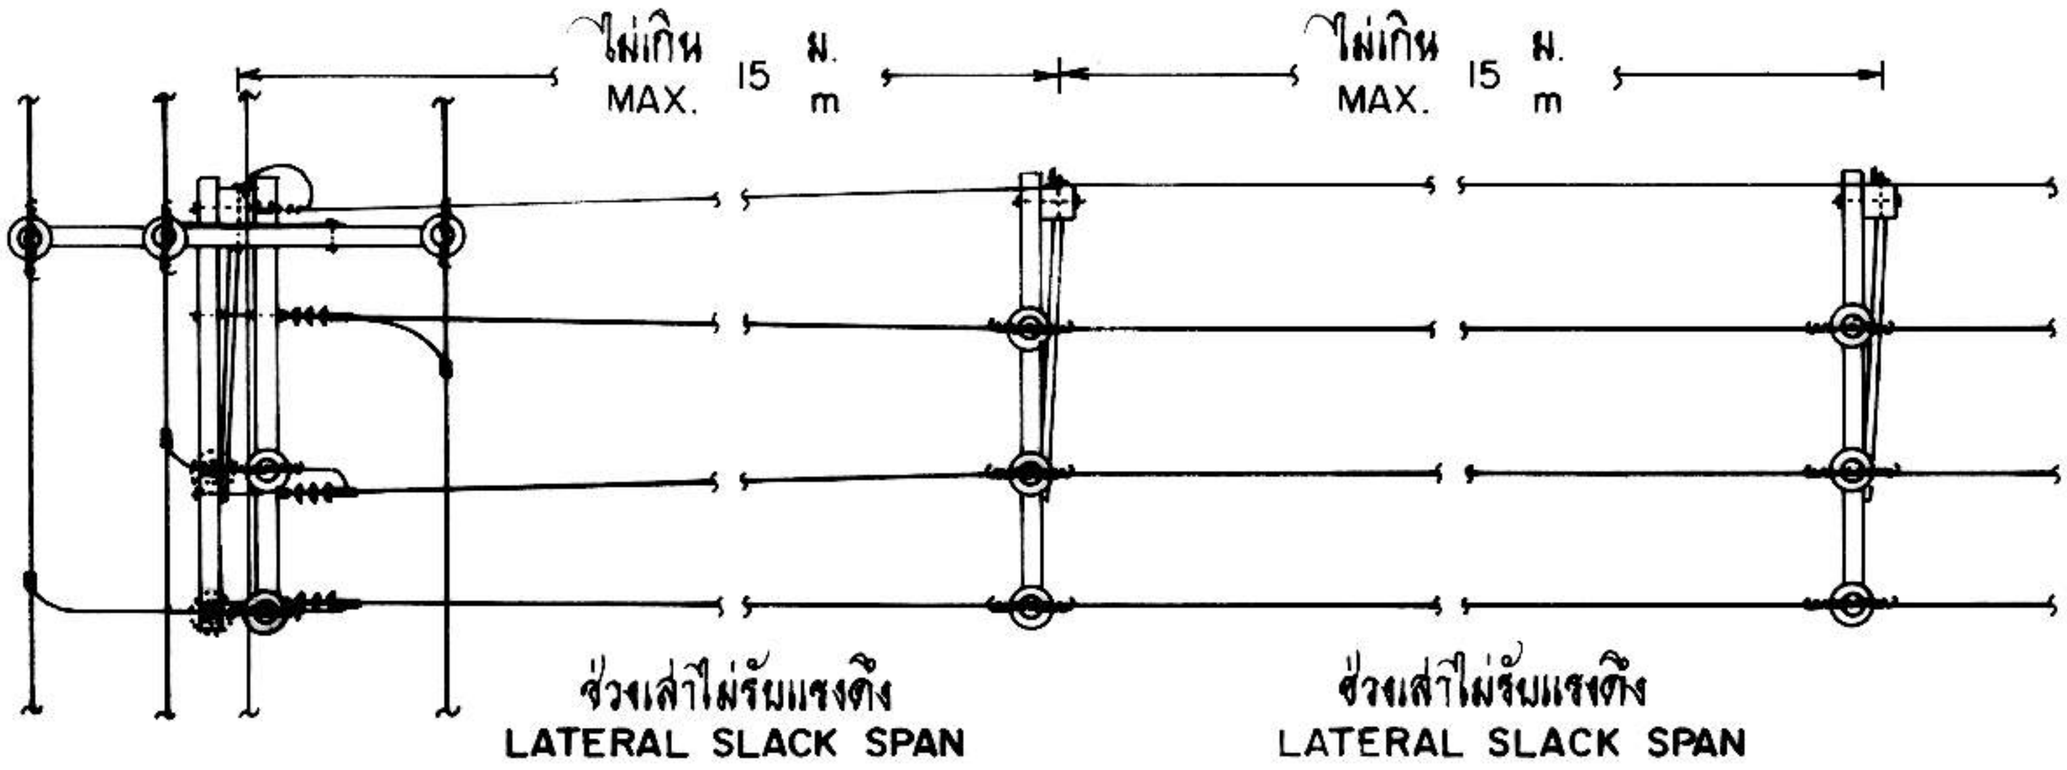

6. ถ้าขนาดสายไฟฟ้าของวงจรย่อยไม่เกิน 50 ต.มม. ระยะห่างระหว่างช่วงเสาไม่รับแรงดึงของวงจรย่อย สามารถเพิ่มเป็น 20 ม. ได้

6. LATERAL SLACK SPAN LENGTH CAN BE EXPANDED TO 20 m, IF CONDUCTOR SIZE OF LATERAL LINES ARE NOT LARGER THAN 50 mm^2.

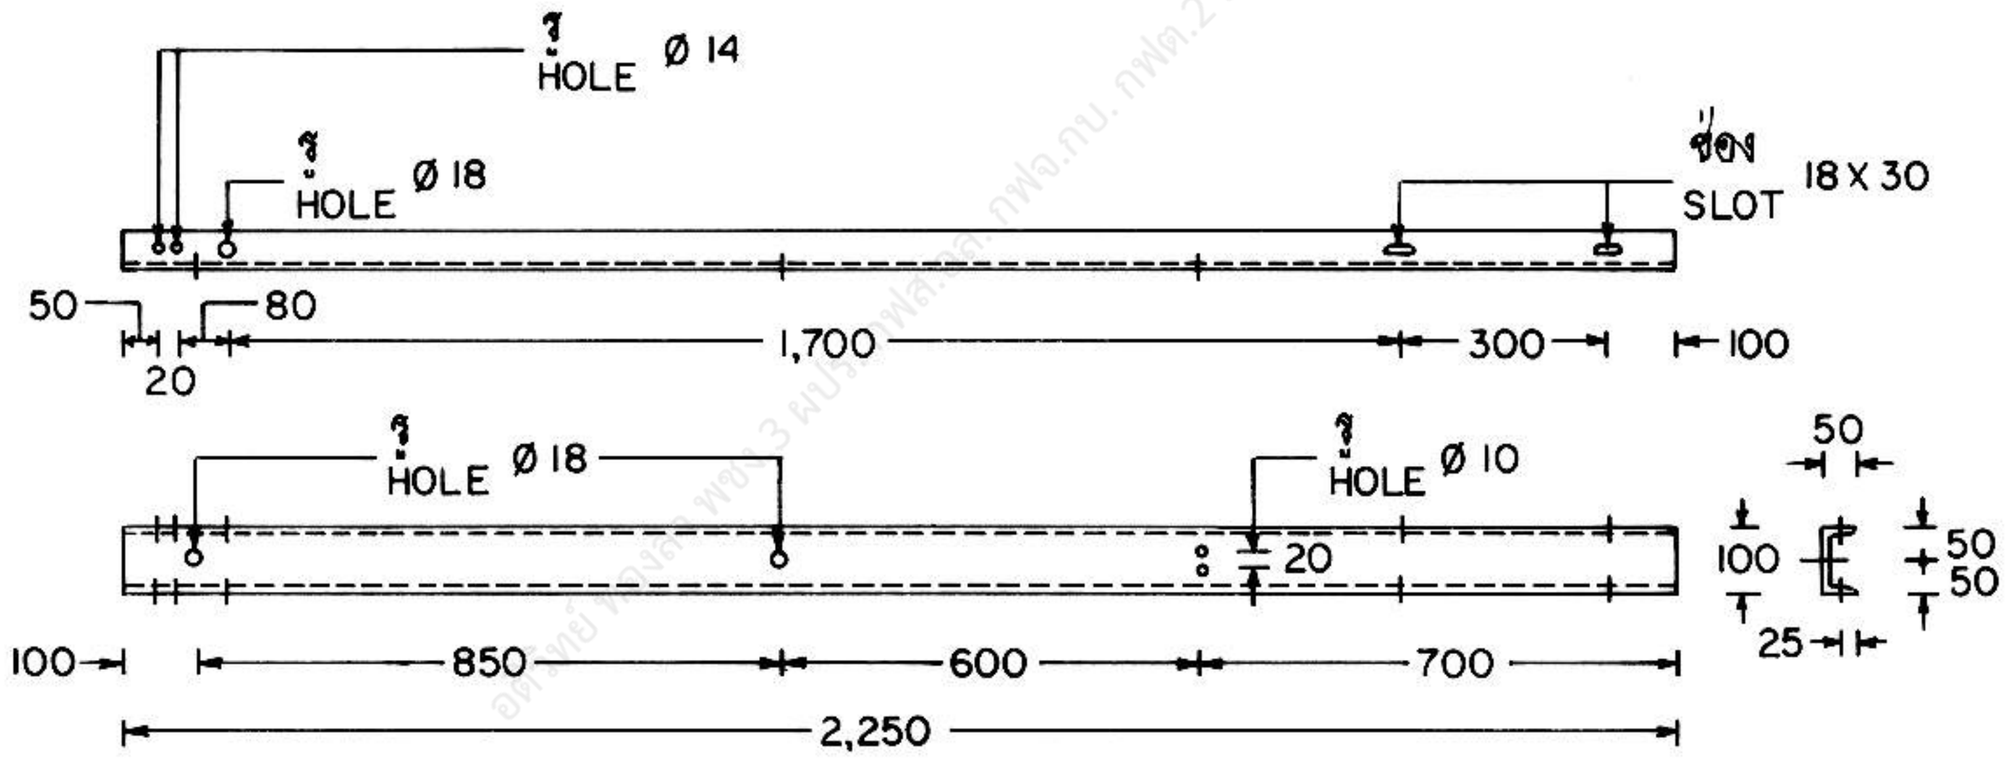

เหล็กรูปรางน้ำชนิดรีดร้อน ขนาด 100 X 50 X 5 มม. ยาว 2.25 ม. มอก. 116 (อาจทำจากวัสดุเลขที่ 6012 ได้)
STEEL, CHANNEL, 100 X 50 X 5 mm, 2.25 m LONG, TIS 116 (MAY BE MADE FROM MAT. NO. 6012)

วัสดุลำดับที่ MATERIAL ITEM (5)

กองวิศวกรรมไฟฟ้าและเครื่องกล ฝ่ายวิศวกรรม	**การไฟฟ้าส่วนภูมิภาค**	ใช้แทนแผน ..... ถูกแทนโดยแผน ..... เขียนเสร็จวันที่ 6 มี.ค. 35 แก้แผนวันที่ ..... มิติเป็น มิลลิเมตร มาตราส่วน 1 : 20
ผู้เขียน ..... ผู้สำรวจ ..... วิศวกร สิทธา ..... หัวหน้าแผนก ..... ผู้อำนวยการกอง ..... ผู้อำนวยการฝ่าย	ผู้ว่าการ ..... 17 เมย 7535	
ของผู้ว่าการฝ่ายเทคนิค	การติดตั้งอุปกรณ์ที่เสาเข้าปลายสายแยมท้าวแขน (กรณีใช้คอนกรีต) ระบบ 33 kV	
	DEADEND CONSTRUCTION ON ALLEY ARM (CONCRETE CROSSARM) 33 kV SYSTEM	แผนเลขที่ SAI-015/35009 แผ่นที่ 4 ของจำนวน 6 แผ่น

21 เม.ย. 2535

* หรือใช้ลูกถ้วยก้านตรง (วัสดุเลขที่ 0409) พร้อมก้านแบบฟ้อก (วัสดุเลขที่ 0423) จำนวน 3 ชุด เพื่อแก้ปัญหาเนื่องจากนก

การประกอบเลขที่ ASSEMBLY NO. **3811**

บัญชีวัสดุ
BILL OF MATERIAL

ลำดับที่ ITEM	รายละเอียด DESCRIPTION	จำนวน REQ'D DEA 1	BAS 3	DAS 2	วัสดุเลขที่ MAT. NO.
1	คอน คอร. สปัน ขนาด 120 X 120 X 3,000 มม. CROSSARM, SPUN, PRESTRESSED CONCRETE, 120 X 120 X 3,000 mm	–	2	–	00110002
2	คอน คอร. สปัน (สำหรับเข้าปลายสาย) ขนาด 120 X 120 X 2,500 มม. CROSSARM, SPUN, PRESTRESSED CONCRETE (FOR DEADENDING), 120 X 120 X 2,500 mm	2	–	2	00110004
3	เหล็กประกับคอนแบบท้าวแขน ขนาด 50 X 50 X 5 มม. ยาว 2,350 มม. BRACE, ALLEY ARM, 50 X 50 X 5 mm, 2,350 mm LONG	1	1	1	01200005
4	เหล็กรูปรางน้ำรับสายล่อฟ้า ต้นเข้าปลายสาย ขนาด 100 X 50 X 5 มม. ยาว 2.25 ม. OVERHEAD GROUND WIRE DEADEND BAYONET, CHANNEL STEEL, 100 X 50 X 5 mm, 2.25 m LONG	1	–	1	01000100
5	เหล็กรูปรางน้ำ ขนาด 100 X 50 X 5 มม. ยาว 2.25 ม. มอก. 116 เจาะรูตามแบบแผ่นที่ 4 STEEL, CHANNEL, 100 X 50 X 5 mm, 2.25 m LONG, TIS 116, PUNCH HOLE AS DWG. ON SHEET NO. 4	–	1	–	—
6	สลักเกลียว M 16 X 170 มม. BOLT, MACHINE, M 16 X 170 mm	1	–	1	01110201
7	สลักเกลียว M 16 X 250 มม. BOLT, MACHINE, M 16 X 250 mm	3	1	3	01110203
8	สลักเกลียว M 16 X 350 มม. BOLT, MACHINE, M 16 X 350 mm	–	2	–	01110205
9	สลักเกลียว M 16 X 500 มม. BOLT, MACHINE, M 16 X 500 mm	–	1	–	01110208
10	สลักเกลียวห่วงกลม M 16 X 450 มม. BOLT, DOUBLE ARMING, ROUND EYE, M 16 X 450 mm	3	–	3	01130001
11	สลักเกลียวห่วงกลม M 16 X 500 มม. BOLT, DOUBLE ARMING, ROUND EYE, M 16 X 500 mm	–	3	–	01130002
12	สลักห่วงกลม M 16 X 200 มม. BOLT, ROUND EYE, M 16 X 200 mm	1	1	1	01140001
13	นัทรูปห่วง M 16, DIN 582 NUT, EYE, M 16, DIN 582	1	–	1	01180001
14	แหวนสี่เหลี่ยมแบน 52 X 52 X 4.5 มม. รู Ø 18 มม. มอก. 258 WASHER, SQUARE, FLAT, 52 X 52 X 4.5 mm, HOLE Ø 18 mm, TIS 258	16	18	16	01180100
15	แหวนสี่เหลี่ยมโค้ง 60 X 60 X 5 มม. รู Ø 22 มม. WASHER, SQUARE, CURVED, 60 X 60 X 5 mm, HOLE Ø 22 mm	–	2 (4)	3 (6)	01180201
16	ยูแคล้มป์ สลัก 1 ท้าว M 8 CLAMP, SINGLE U-BOLT, M 8	4	6	8	01230000
17	ลวดเหล็กกลม เส้นผ่านศูนย์กลาง 4 มม. มอก. 71 (น้ำหนักประมาณ 0.1 กก. / ม.) WIRE, STEEL, SOLID, DIA 4 mm, TIS 71 (WEIGHT 0.1 kg/m)	–	4.5 น.ม. (6)	3.5 น.ม. (6)	01100000
18	ลูกถ้วยก้านตรง 33 kV มอก. 279 แบบ ค (แบบ 56-3) พร้อมก้าน INSULATOR, PIN TYPE, 33 kV, TIS 279, TYPE C (CLASS 56-3); COMP. WITH PIN	–	2 (4)	3 (6)*	03000002 03100001

กองวิศวกรรมไฟฟ้าและเครื่องกล
ฝ่ายวิศวกรรม

ผู้เขียน ...
ผู้สำรวจ
วิศวกร ...
หัวหน้าแผนก ...
ผู้อำนวยการกอง ...
ผู้อำนวยการฝ่าย ...

ของผู้ว่าการฝ่ายเทคนิค

การไฟฟ้าส่วนภูมิภาค

ผู้ว่าการ ... 22 เม.ย. 2535

การติดตั้งอุปกรณ์ที่เสาเข้าปลายสายแบบท้าวแขน
(กรณีใช้คอนคอนกรีต)
ระบบ 33 kV

DEADEND CONSTRUCTION ON ALLEY ARM
(CONCRETE CROSSARM)
33 kV SYSTEM

ใช้แทนแผ่น .....
ถูกแทนโดยแผ่น .....
เขียนแล้วเสร็จวันที่ 6 มี.ค. 35
แก้แผ่นวันที่ .....
มิติเป็น .....
มาตราส่วน .....

แผ่นเลขที่ SAI-015/35009
แผ่นที่ 5 ของจำนวน 6 แผ่น

21 เม.ย. 2535

การประกอบเลขที่ ASSEMBLY NO. 3811

บัญชีวัสดุ
BILL OF MATERIAL

ลำดับที่ ITEM	รายละเอียด DESCRIPTION	จำนวน REQ'D DEA 1	BAS 3	DAS 2	วัสดุเลขที่ MAT. NO.
19	ลูกถ้วยแขวน มอก. 354 แบบ ง (แบบ 52-4) INSULATOR, SUSPENSION TYPE, TIS 354, TYPE D (CLASS 52-4)	9	9	9	03020002
20	สเตรนเคล้มป์ สำหรับสายอะลูมิเนียม ขนาด 95-185 ต.มม. CLAMP, STRAIN, FOR Al CONDUCTOR, 95-185 mm^2	3	3	3	03110001-4
21	ลวดอะลูมิเนียมแบน 1 X 10 มม. ความยาวตามต้องการ TAPE, ARMOUR, Al, 1 X 10 mm ; LENGTH AS REQUIRED	–	กก. kg	กก. kg	02200000
22	ลวดอะลูมิเนียมกลม Ø 4 มม. ความยาวตามต้องการ TIE, WIRE, Al, Ø 4 mm ; LENGTH AS REQUIRED	–	กก. kg	กก. kg	02200002
23	พี.จี. คอนเนคเตอร์ ส่ลัก 3 ตัว สำหรับสายอะลูมิเนียม ขนาด 70-185 ต.มม. CONNECTOR, PARALLEL GROOVE, TRIPLE BOLT, FOR Al CONDUCTOR, 70-185 mm^2	–	6	–	02300103
24	สายยึดโยง แบบ GY-39 (เพิ่มส่ลักห่วงแบบธรรมดา 45° M 16 X 250 มม. (วัสดุเลขที่ 0161) จำนวน 1 ชุด) GUY ASSEMBLY, GY-39 (ADD ONE SET OF M 16 X 250 mm, 45° SINGLE STRAND EYE BOLT (MAT. NO. 0161))	1	–	1	
25	สายยึดโยงแบบ GY-38 (ตัดส่ลักห่วงกลม M 16 X 250-300 มม. (วัสดุเลขที่ 0254-0255) ออก) GUY ASSEMBLY GY-38 (OMITED M 16 X 250-300 mm, ROUND EYE BOLT (MAT. NO. 0254-0255))	1	–	–	
26	สายยึดโยงแบบ GY-38 (เปลี่ยนส่ลักห่วงกลม M 16 X 250-300 มม. (วัสดุเลขที่ 0254-0255) เป็น M 16 X 200 มม. (วัสดุเลขที่ 0253)) GUY ASSEMBLY GY-38 (CHANGE M 16 X 250-300 mm, ROUND EYE BOLT (MAT. NO. 0254-0255) TO M 16 X 200 mm (MAT. NO. 0253))	–	–	1	
27	กาลทิมเบิล สำหรับสายยึดโยง 50-95 ต.มม. THIMBLE, GUY, FOR STEEL WIRE 50-95 mm^2	1	1	2	01210304
28	กราวด์วายร์แคล้มป์ แบบ J 1152 GROUND WIRE CLAMP, J 1152	–	1	–	01230205

หมายเหตุ จำนวนวัสดุในวงเล็บ ใช้สำหรับการแก้ปัญหากระแสไฟฟ้าขัดข้องเนื่องจากนก (ถ้าต้องการ)

NOTE THE QUANTITY OF MATERIAL REQUIRED IN BRACKET, USE FOR AVOIDANCE THE OUTAGE DUE TO BIRD (IF REQUIRED)

DEA – 1 = DEADEND, ALLEY ARM, TYPE 1

BAS – 3 = BUCKARM, ALLEY ARM, SLACK SPAN, TYPE 3

DAS – 2 = DEADEND, ALLEY ARM, SLACK SPAN, TYPE 2

กองวิศวกรรมไฟฟ้าและเครื่องกล
ฝ่ายวิศวกรรม

ผู้เขียน ...
ผู้สำรวจ ...
วิศวกร สัมพร
หัวหน้าแผนก ...
ผู้อำนวยการกอง สวน
ผู้อำนวยการฝ่าย ...

ของผู้ว่าการฝ่ายเทคนิค
...
21 มิ.ย. 2535

การไฟฟ้าส่วนภูมิภาค

ผู้ว่าการ ... 22 มิ.ย. 2535

การติดตั้งอุปกรณ์ที่เสาเข้าปลายสายแบบท้ายแขน
(กรณีใช้คอนคอนกรีต)
ระบบ 33 kV

DEADEND CONSTRUCTION ON ALLEY ARM
(CONCRETE CROSSARM)
33 kV SYSTEM

ใช้แทนแบบ ...
ถูกแทนโดยแบบ ...
เขียนเสร็จวันที่ 6 มี.ค. 35
แก้แบบวันที่ ...
มิติเป็น ...
มาตราส่วน ...

แบบเลขที่ SAI-015/35009
แผ่นที่ 6 ของจำนวน 6 แผ่น