การประกอบเลขที่ 2323
ASSEMBLY NO. 3909

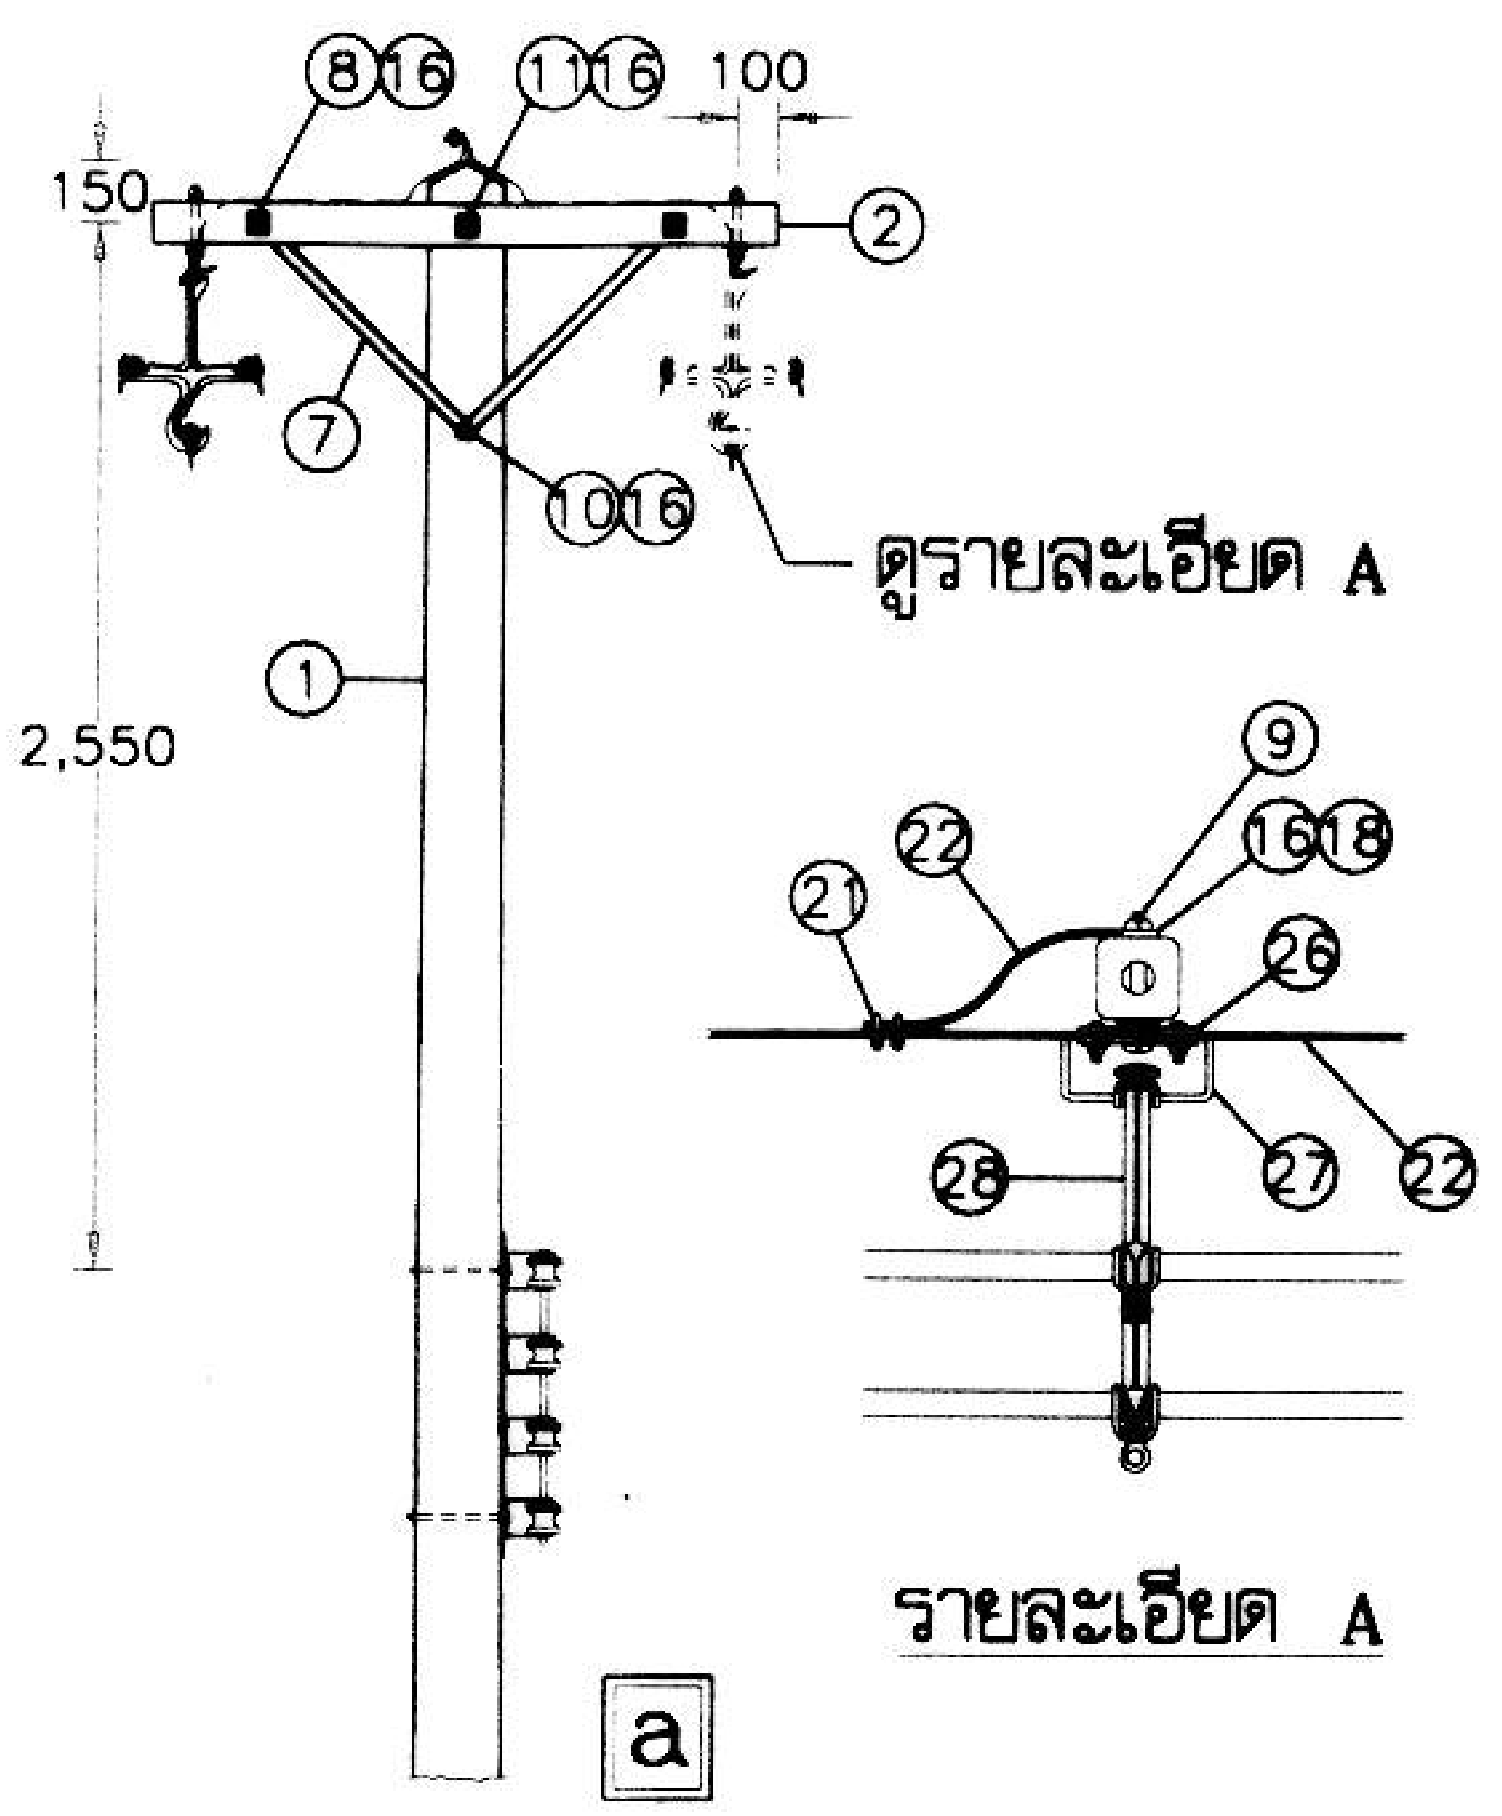

รายละเอียด A

a

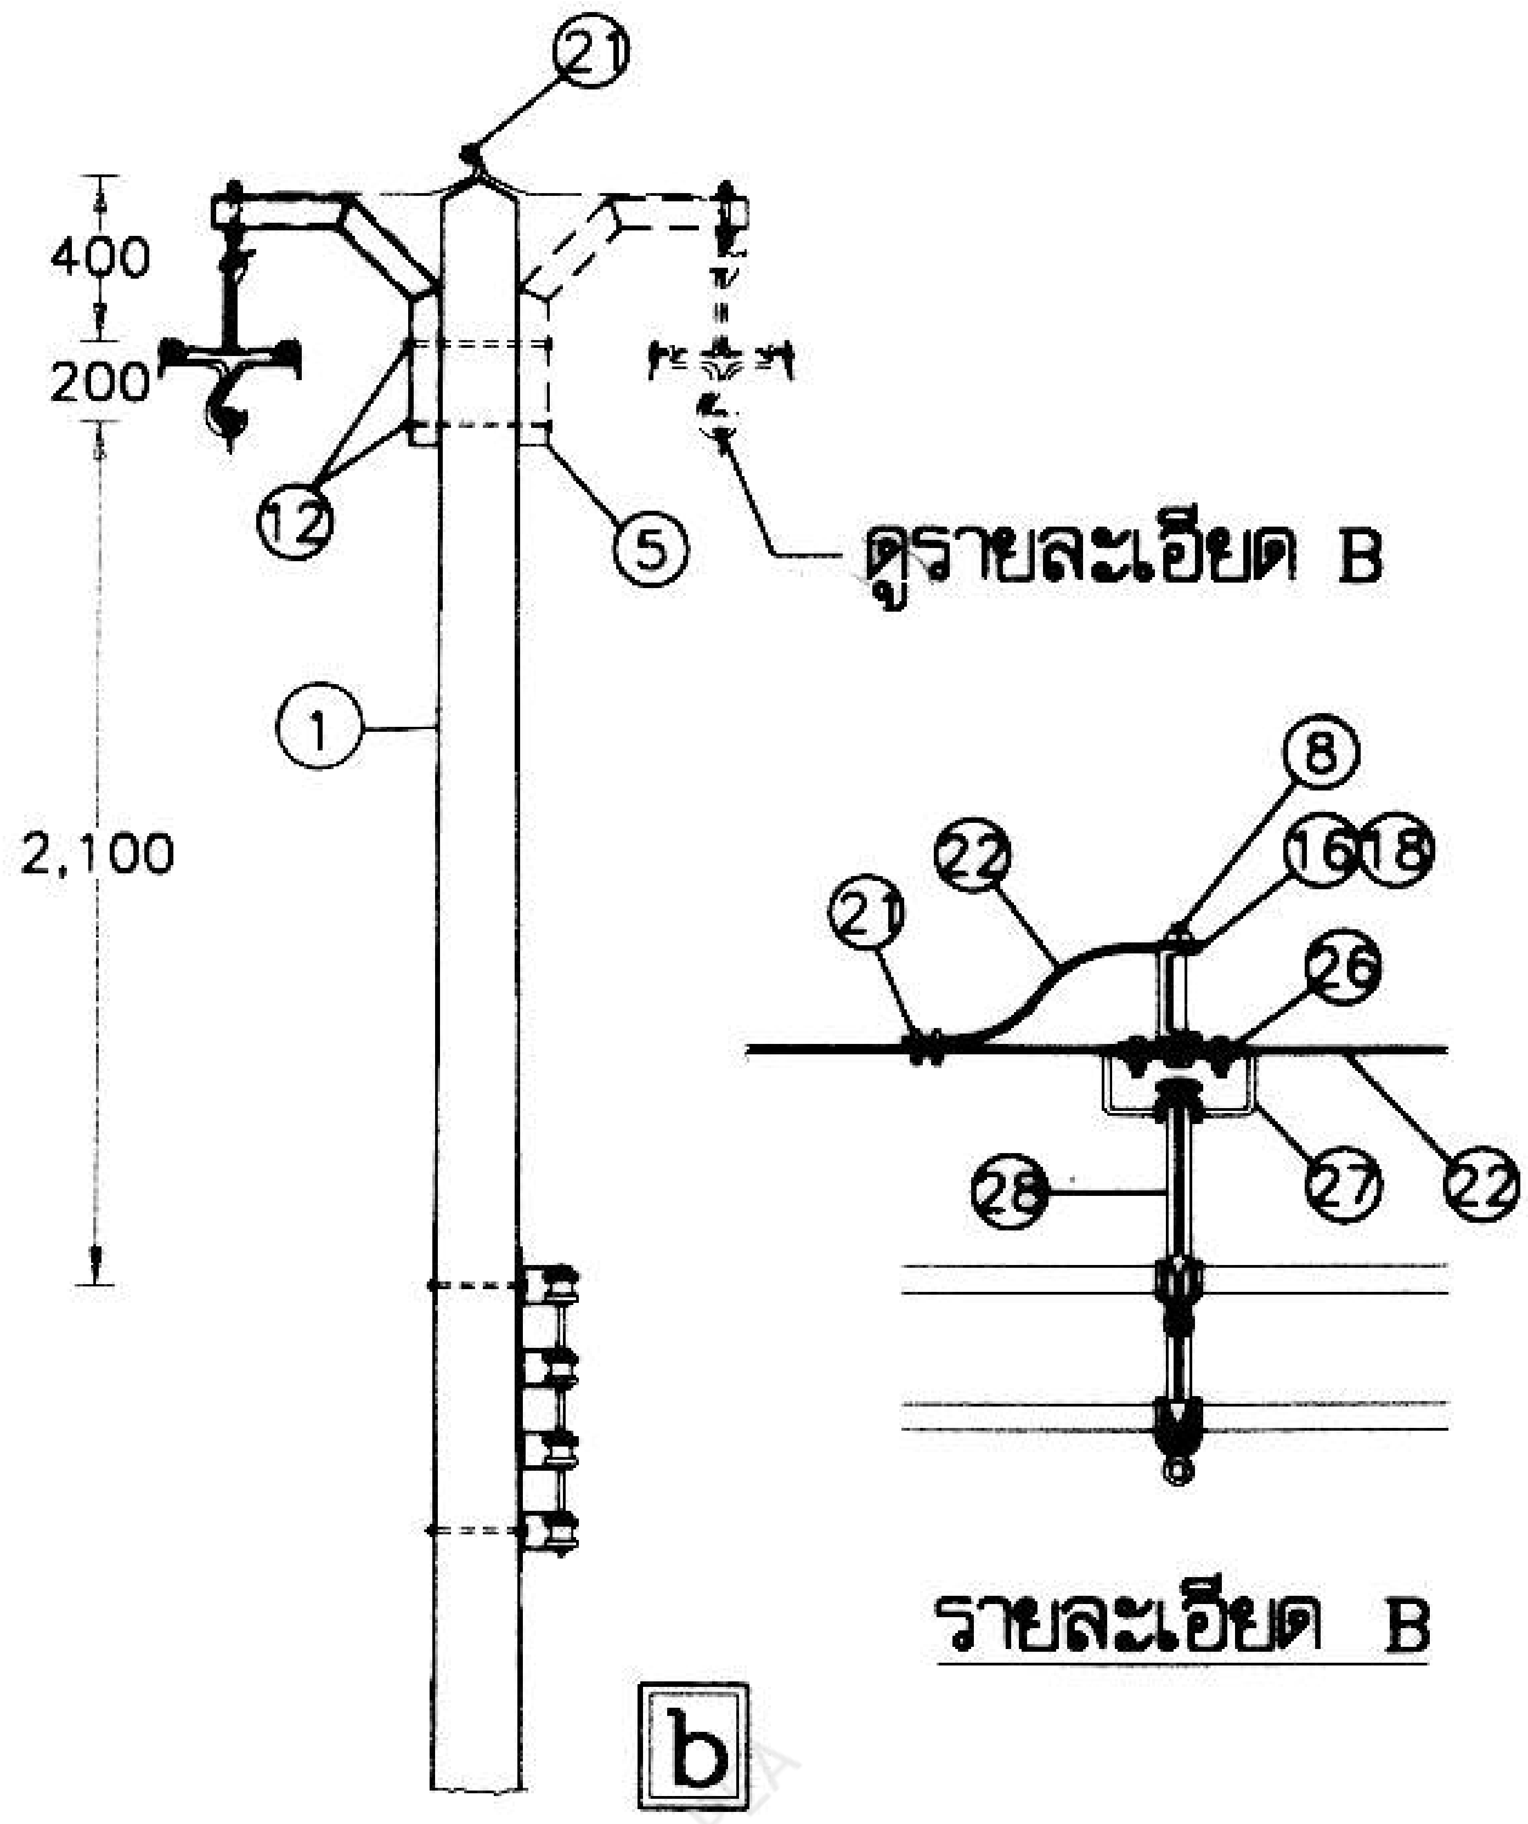

รายละเอียด B

b

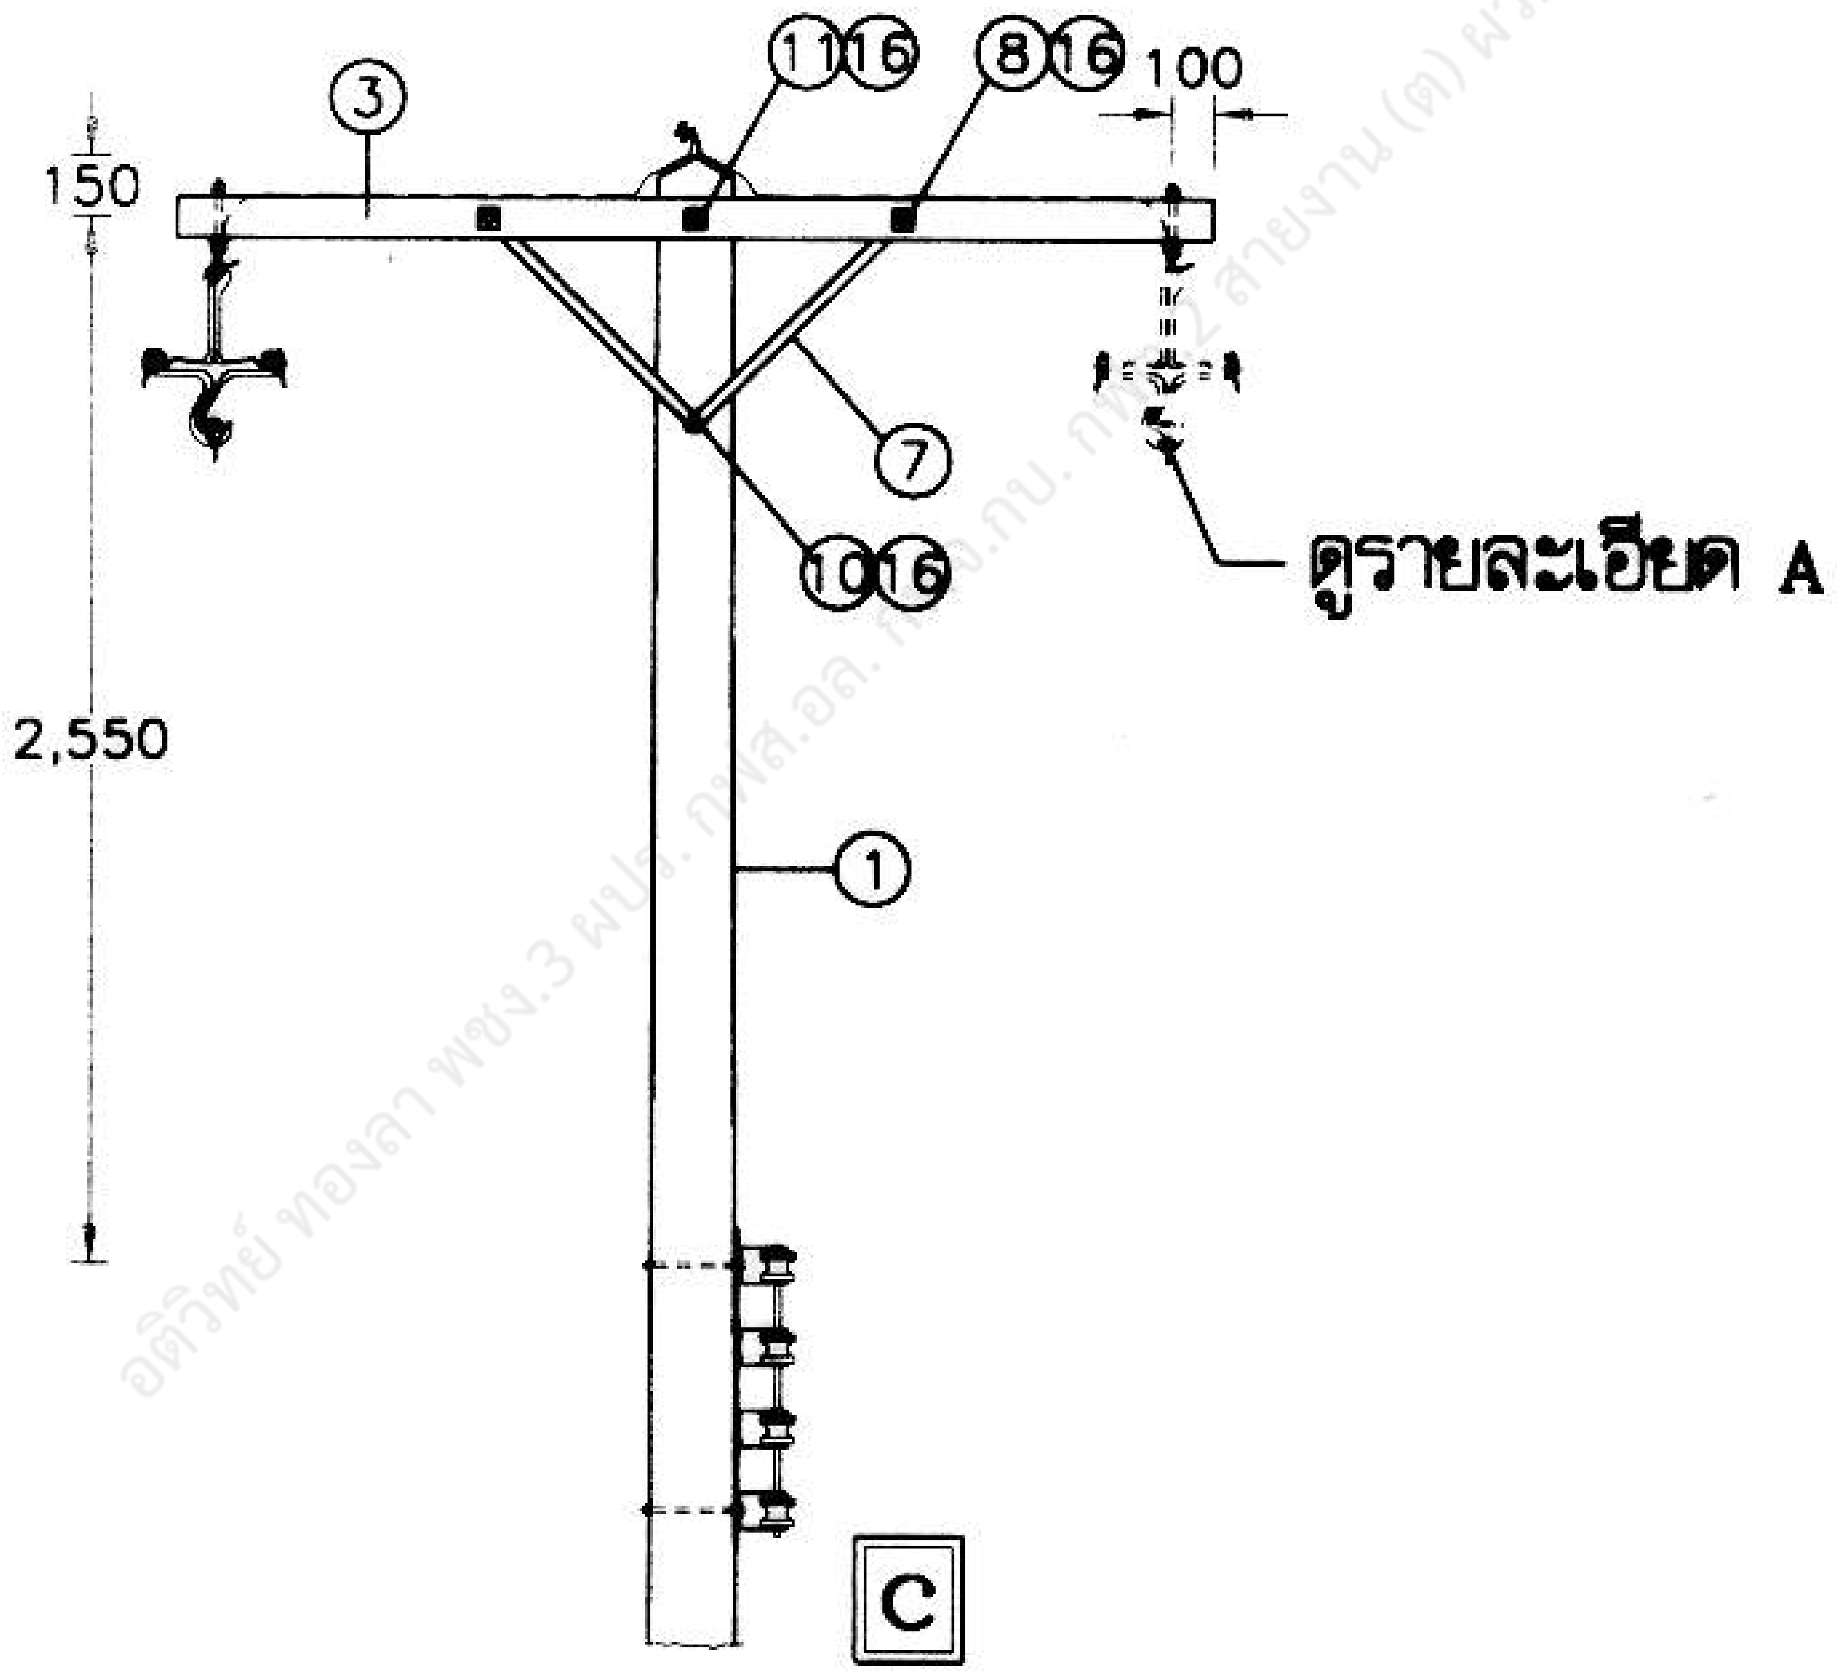

c

I สำหรับทางตรง 0°-5°
FOR TANGENT STRUCTURE 0°-5°

กองวิศวกรรมไฟฟ้าและเครื่องกล
ฝ่ายวิศวกรรม

การไฟฟ้าส่วนภูมิภาค

ใช้แทนแบบ...............
ถูกแทนโดยแบบ...........

ผู้เขียน Supphakit Boonmung
ผู้สำรวจ.................
วิศวกร.................
หัวหน้าแผนก.................
ผู้อำนวยการกอง.................
ผู้อำนวยการฝ่าย.................

ผู้ว่าการ.................

เขียนเสร็จวันที่ 2 ธ.ค. 2540
แก้แบบวันที่ ....

การติดตั้งเคเบิลอากาศ ระบบ 22-33 kV 1-2 วงจร
(กับเสา คอร. ขนาด 12.20 เมตร)

มิติเป็น มิลลิเมตร
มาตราส่วน 1 : 50

รองผู้ว่าการเทคนิคและบริการ
....

22-33 kV AERIAL CABLE INSTALLATION, 1-2 CIRCUIT
(FOR CONCRETE POLE 12.20 m)

แบบเลขที่ SA4-015/40018
แผ่นที่ 1 ของจำนวน 7 แผ่น

การประกอบเลขที่ ASSEMBLY NO.	2323 3909

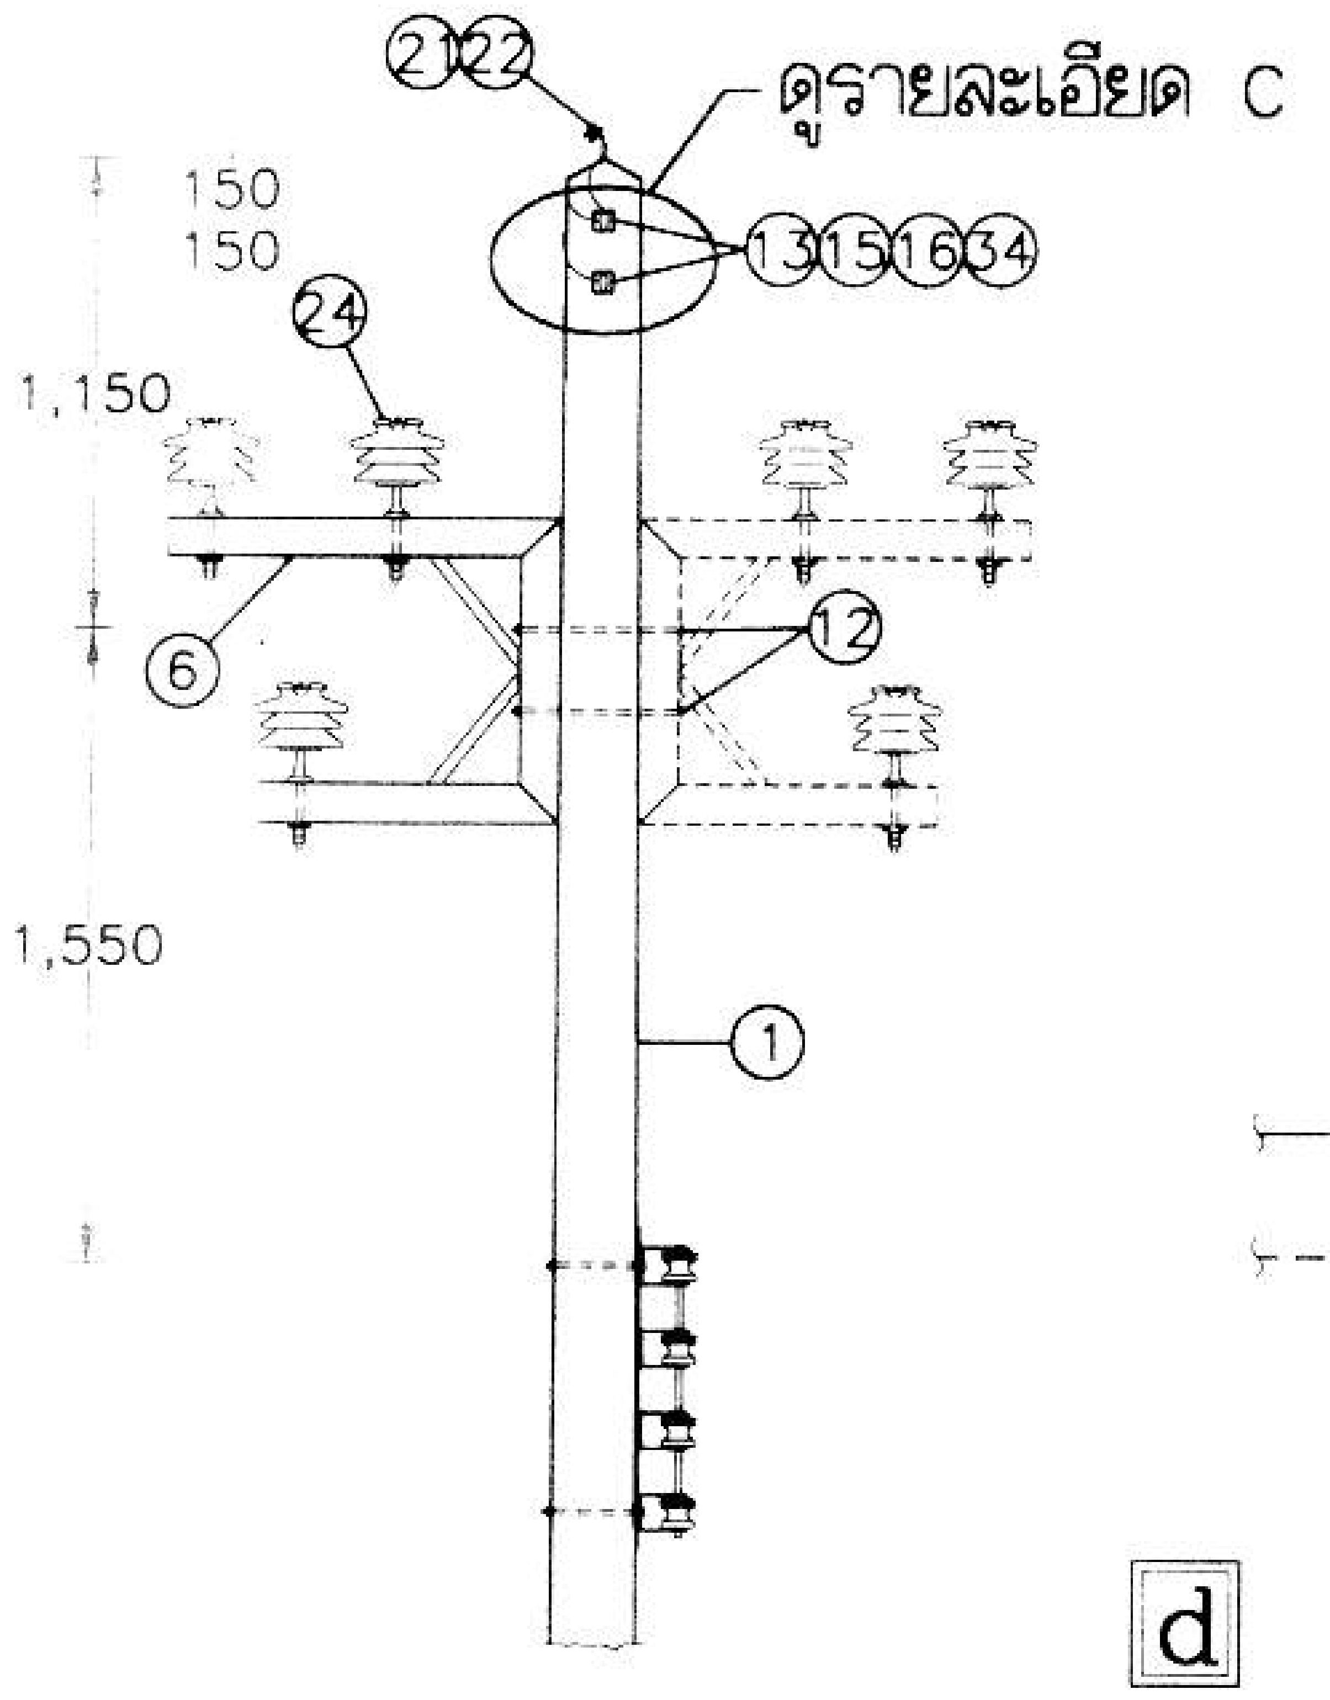

d

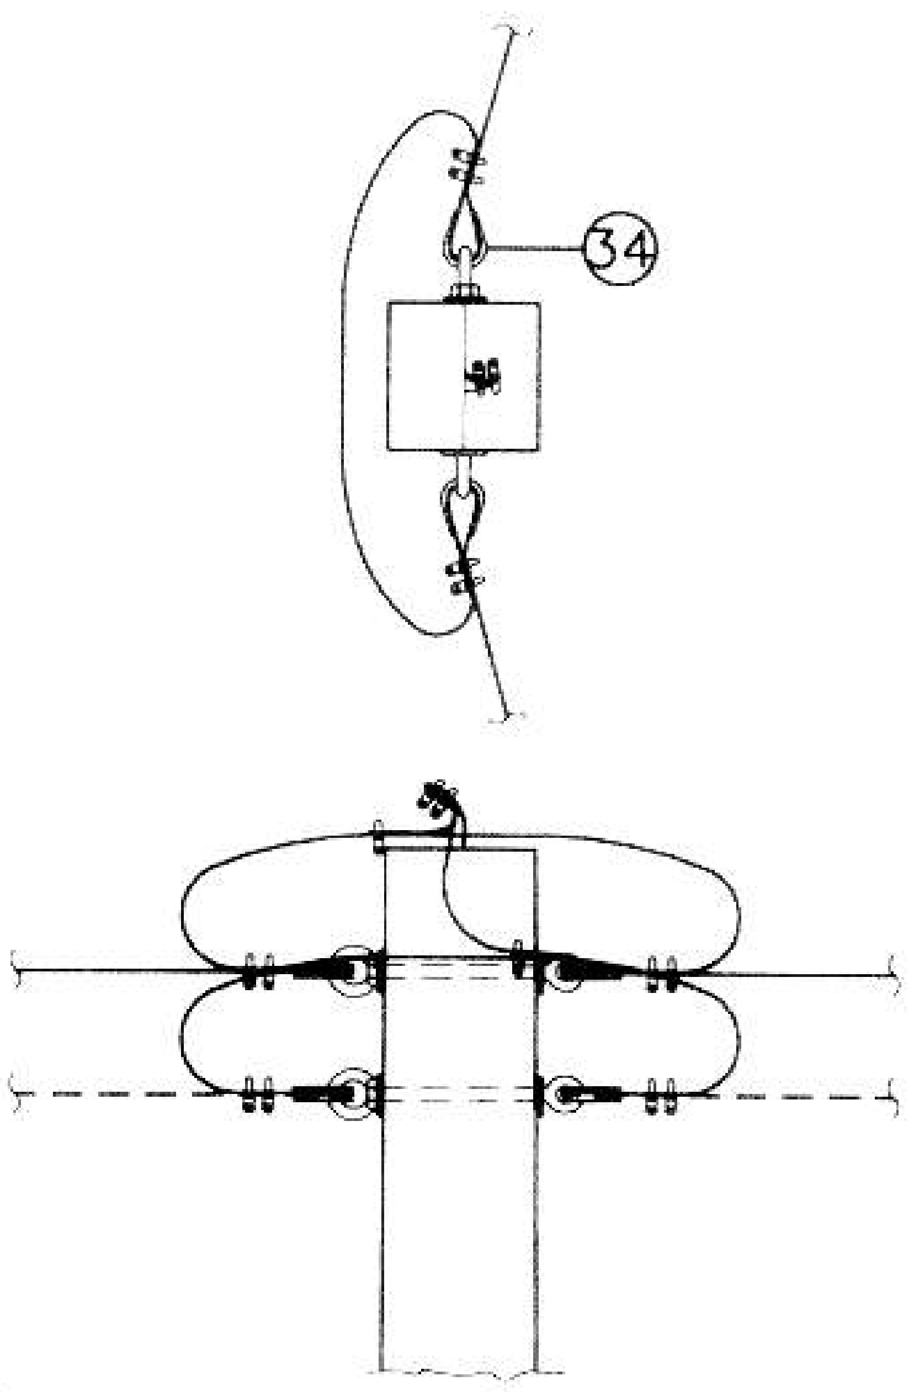

รายละเอียด C

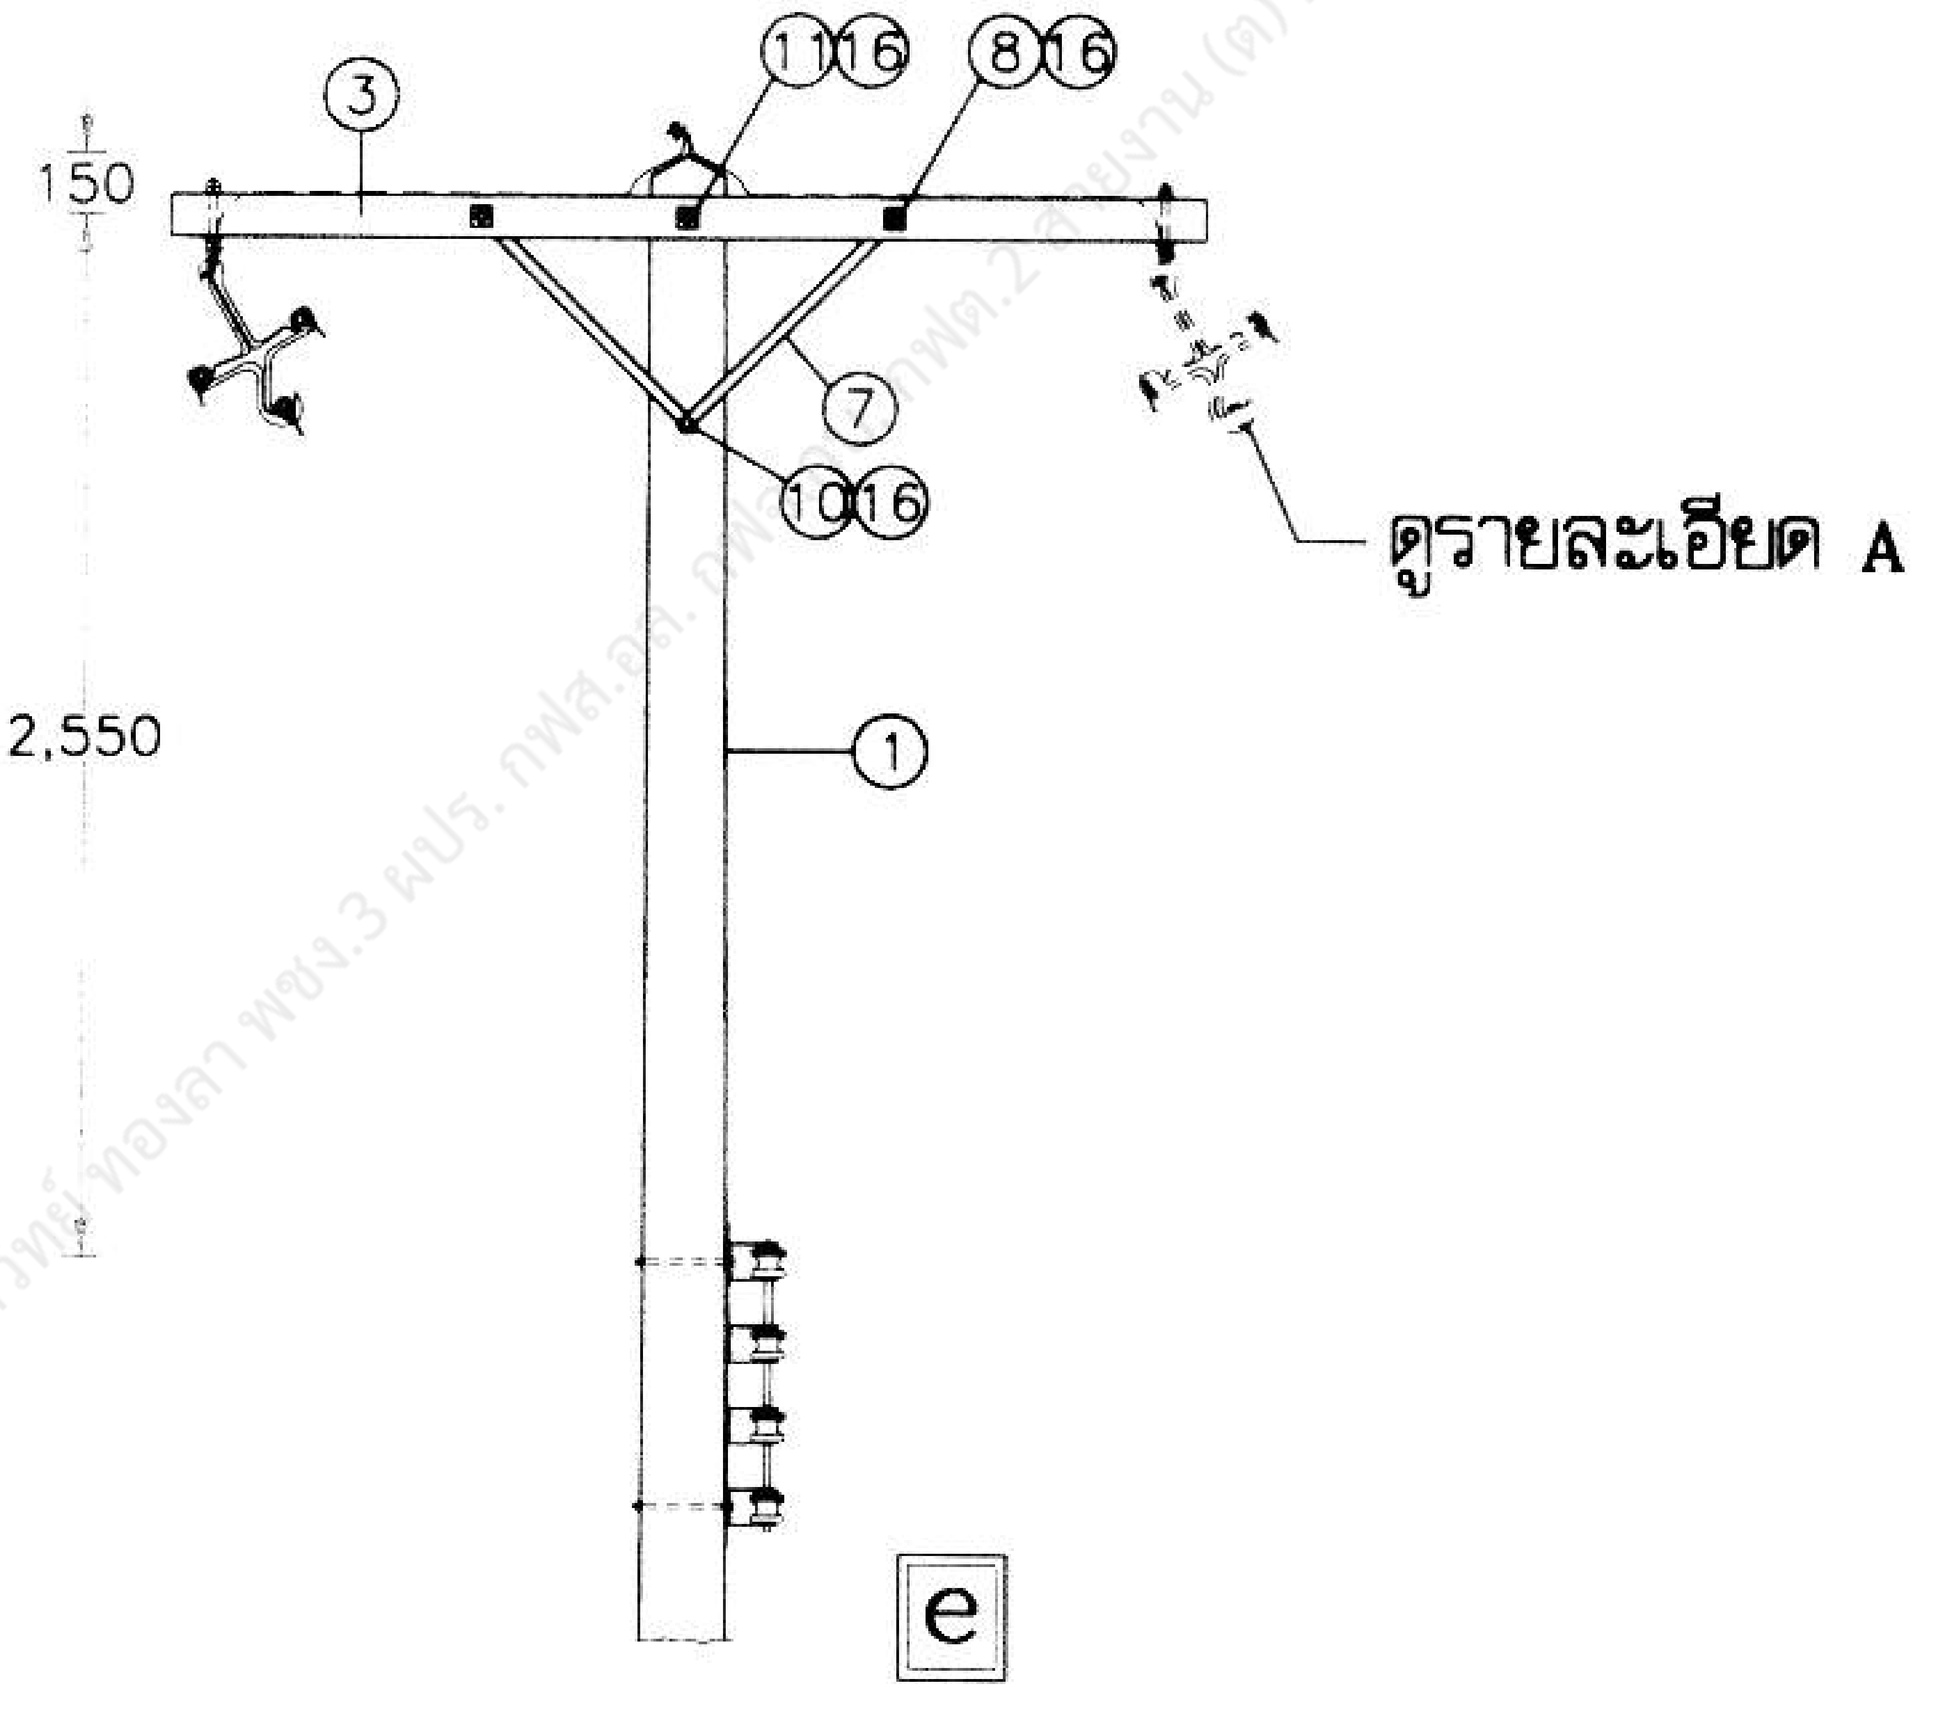

อติวิทย์ ทองลา พชง.3 ผปร. กฟส.ลล. กฟต.2 สายงาน (ต) ผวก. @PEA

II สำหรับทางโค้ง 5°–30°
FOR ANGLE STRUCTURE 5°–30°

กองวิศวกรรมไฟฟ้าและเครื่องกล ฝ่ายวิศวกรรม	การไฟฟ้าส่วนภูมิภาค	ใช้แทนแบบ................ ถูกแทนโดยแบบ............
ผู้เขียน Supphakit Bamrung ผู้สำรวจ................ วิศวกร................ หัวหน้าแผนก................ ผู้อำนวยการกอง................ ผู้อำนวยการฝ่าย................	ผู้ว่าการ .... การติดตั้งเคเบิลอากาศ ระบบ 22–33 kV 1–2 วงจร (กับเสา คอร. ขนาด 12.20 เมตร)	เขียนเสร็จวันที่ 2 ธ.ค. 2540 แก้แบบวันที่ .... มิติเป็น มิลลิเมตร มาตราส่วน 1 : 50
รองผู้ว่าการเทคนิคและบริการ	22–33 kV AERIAL CABLE INSTALLATION, 1–2 CIRCUIT (FOR CONCRETE POLE 12.20 m)	แบบเลขที่ SA4–015/40018 แผ่นที่ 2 ของจำนวน 7 แผ่น

การประกอบเลขที่ 2323
ASSEMBLY NO. 3909

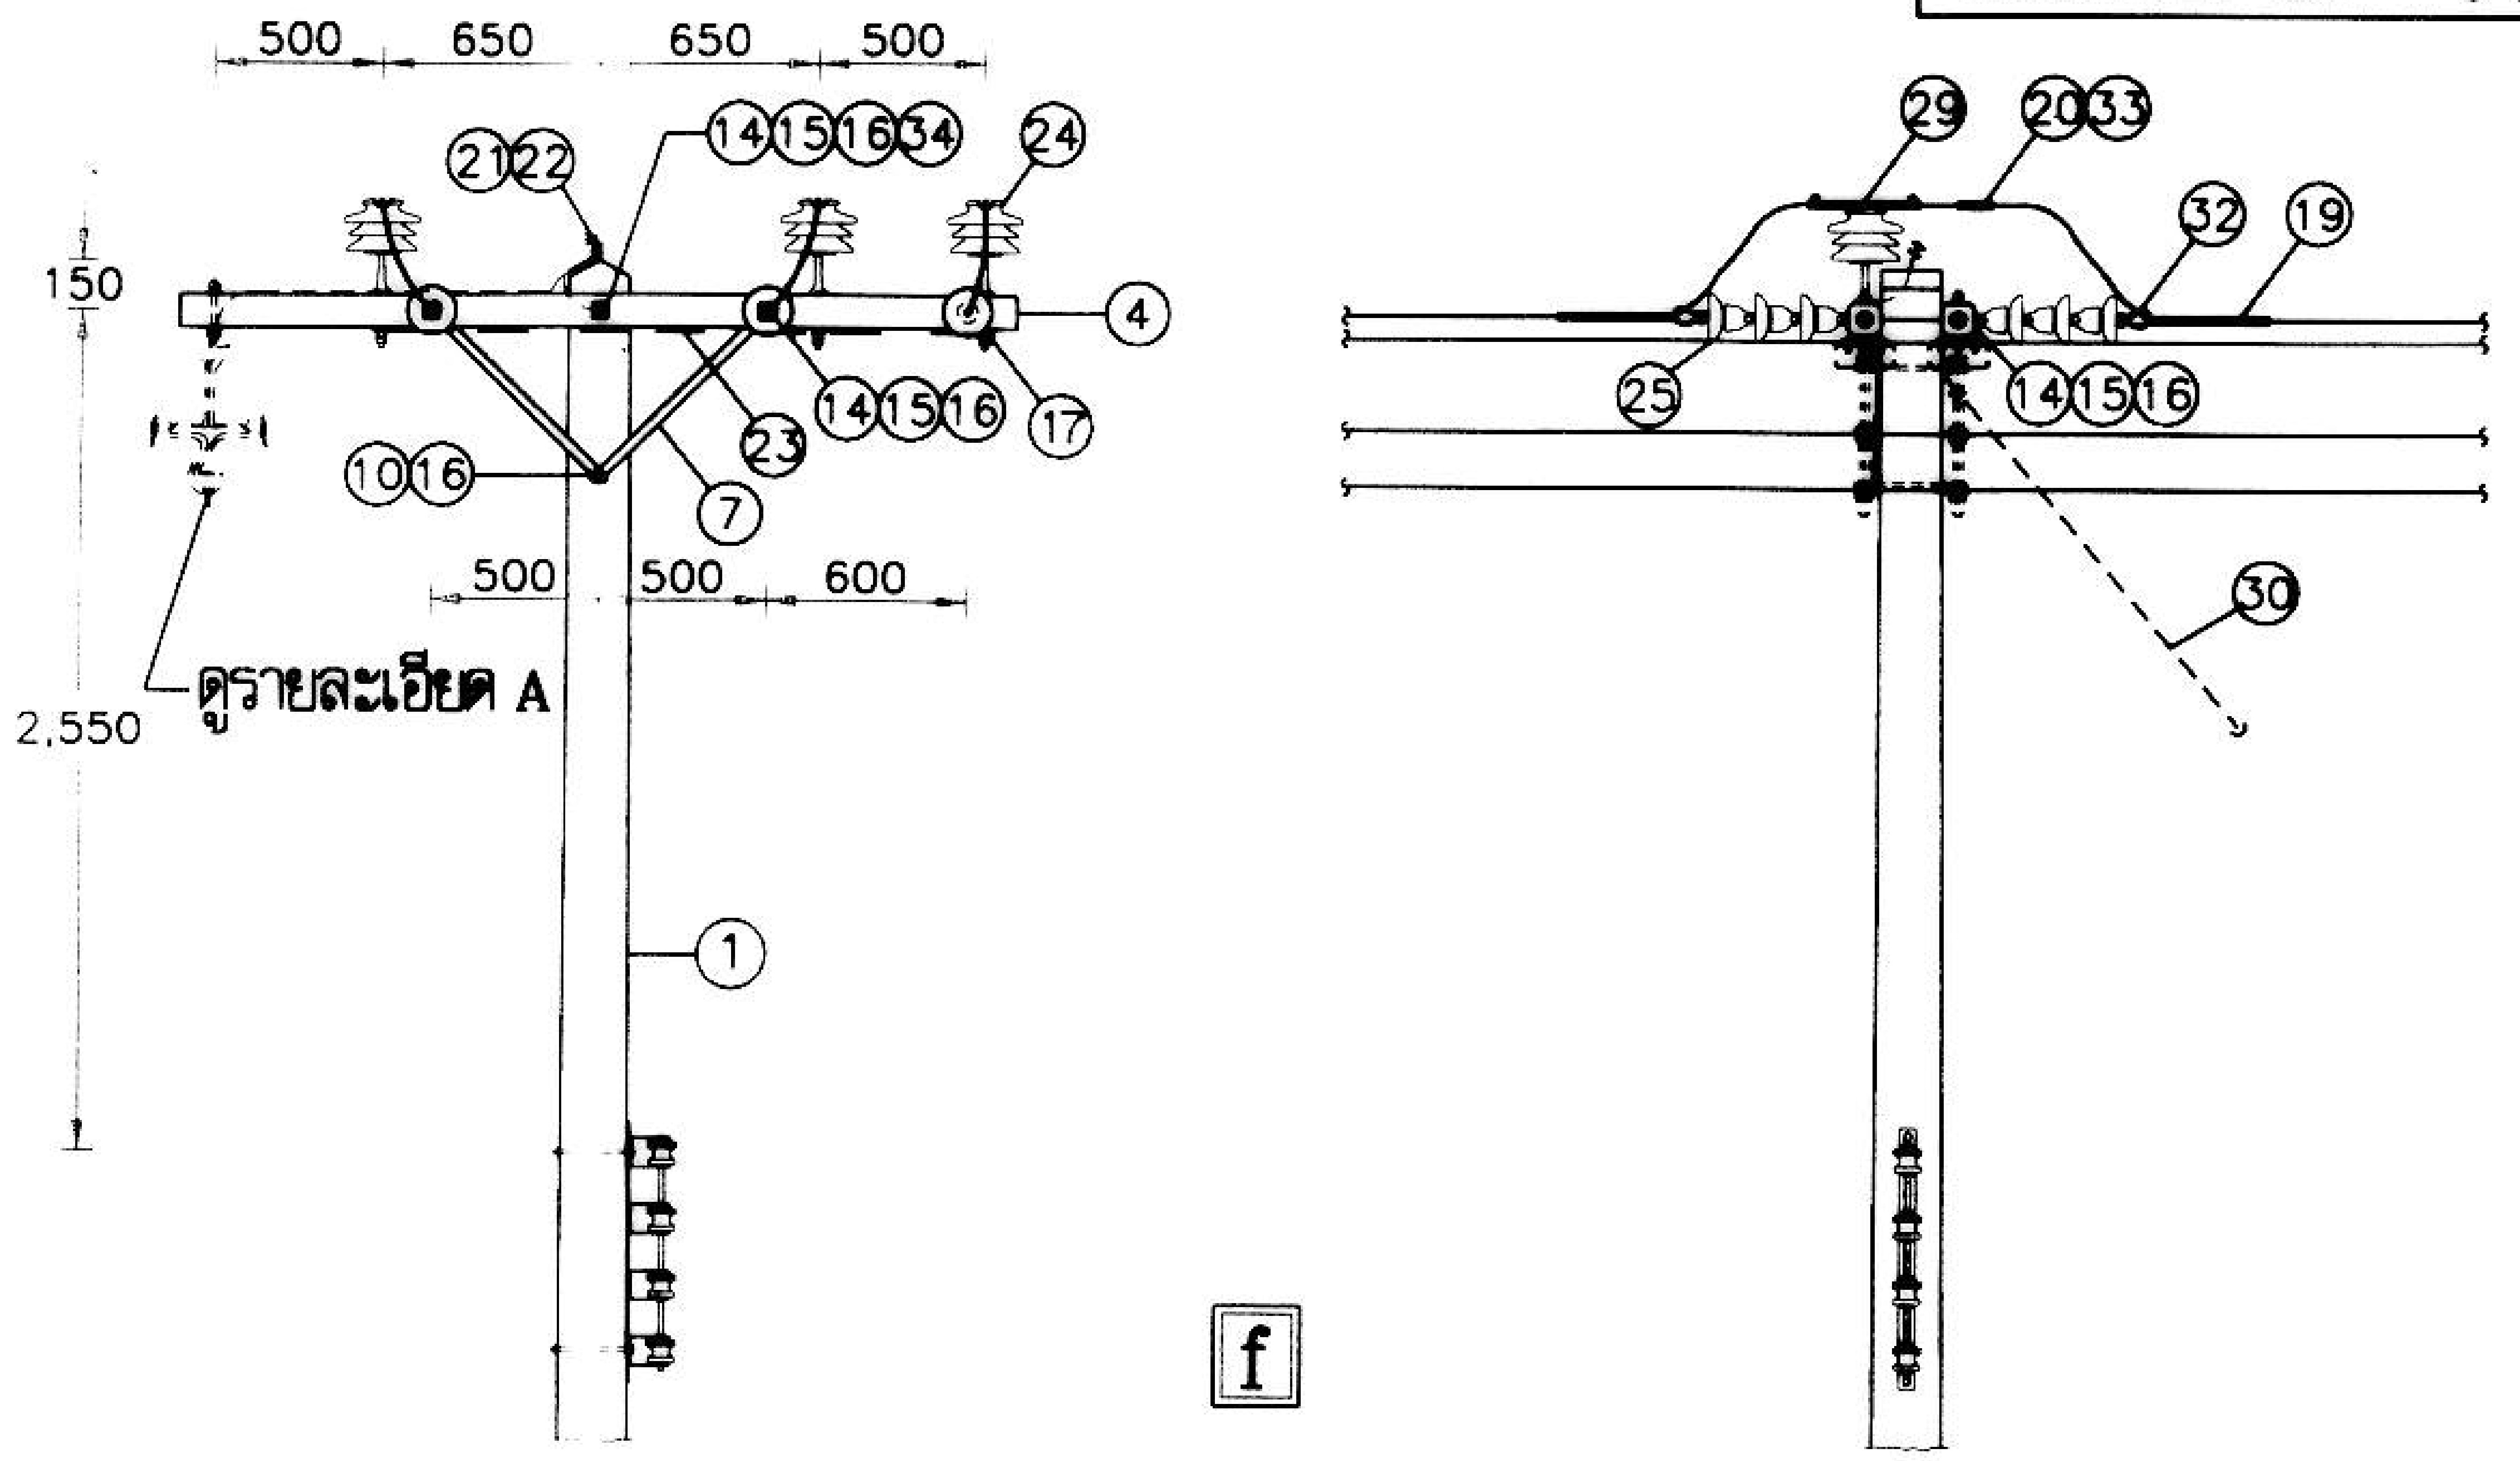

f

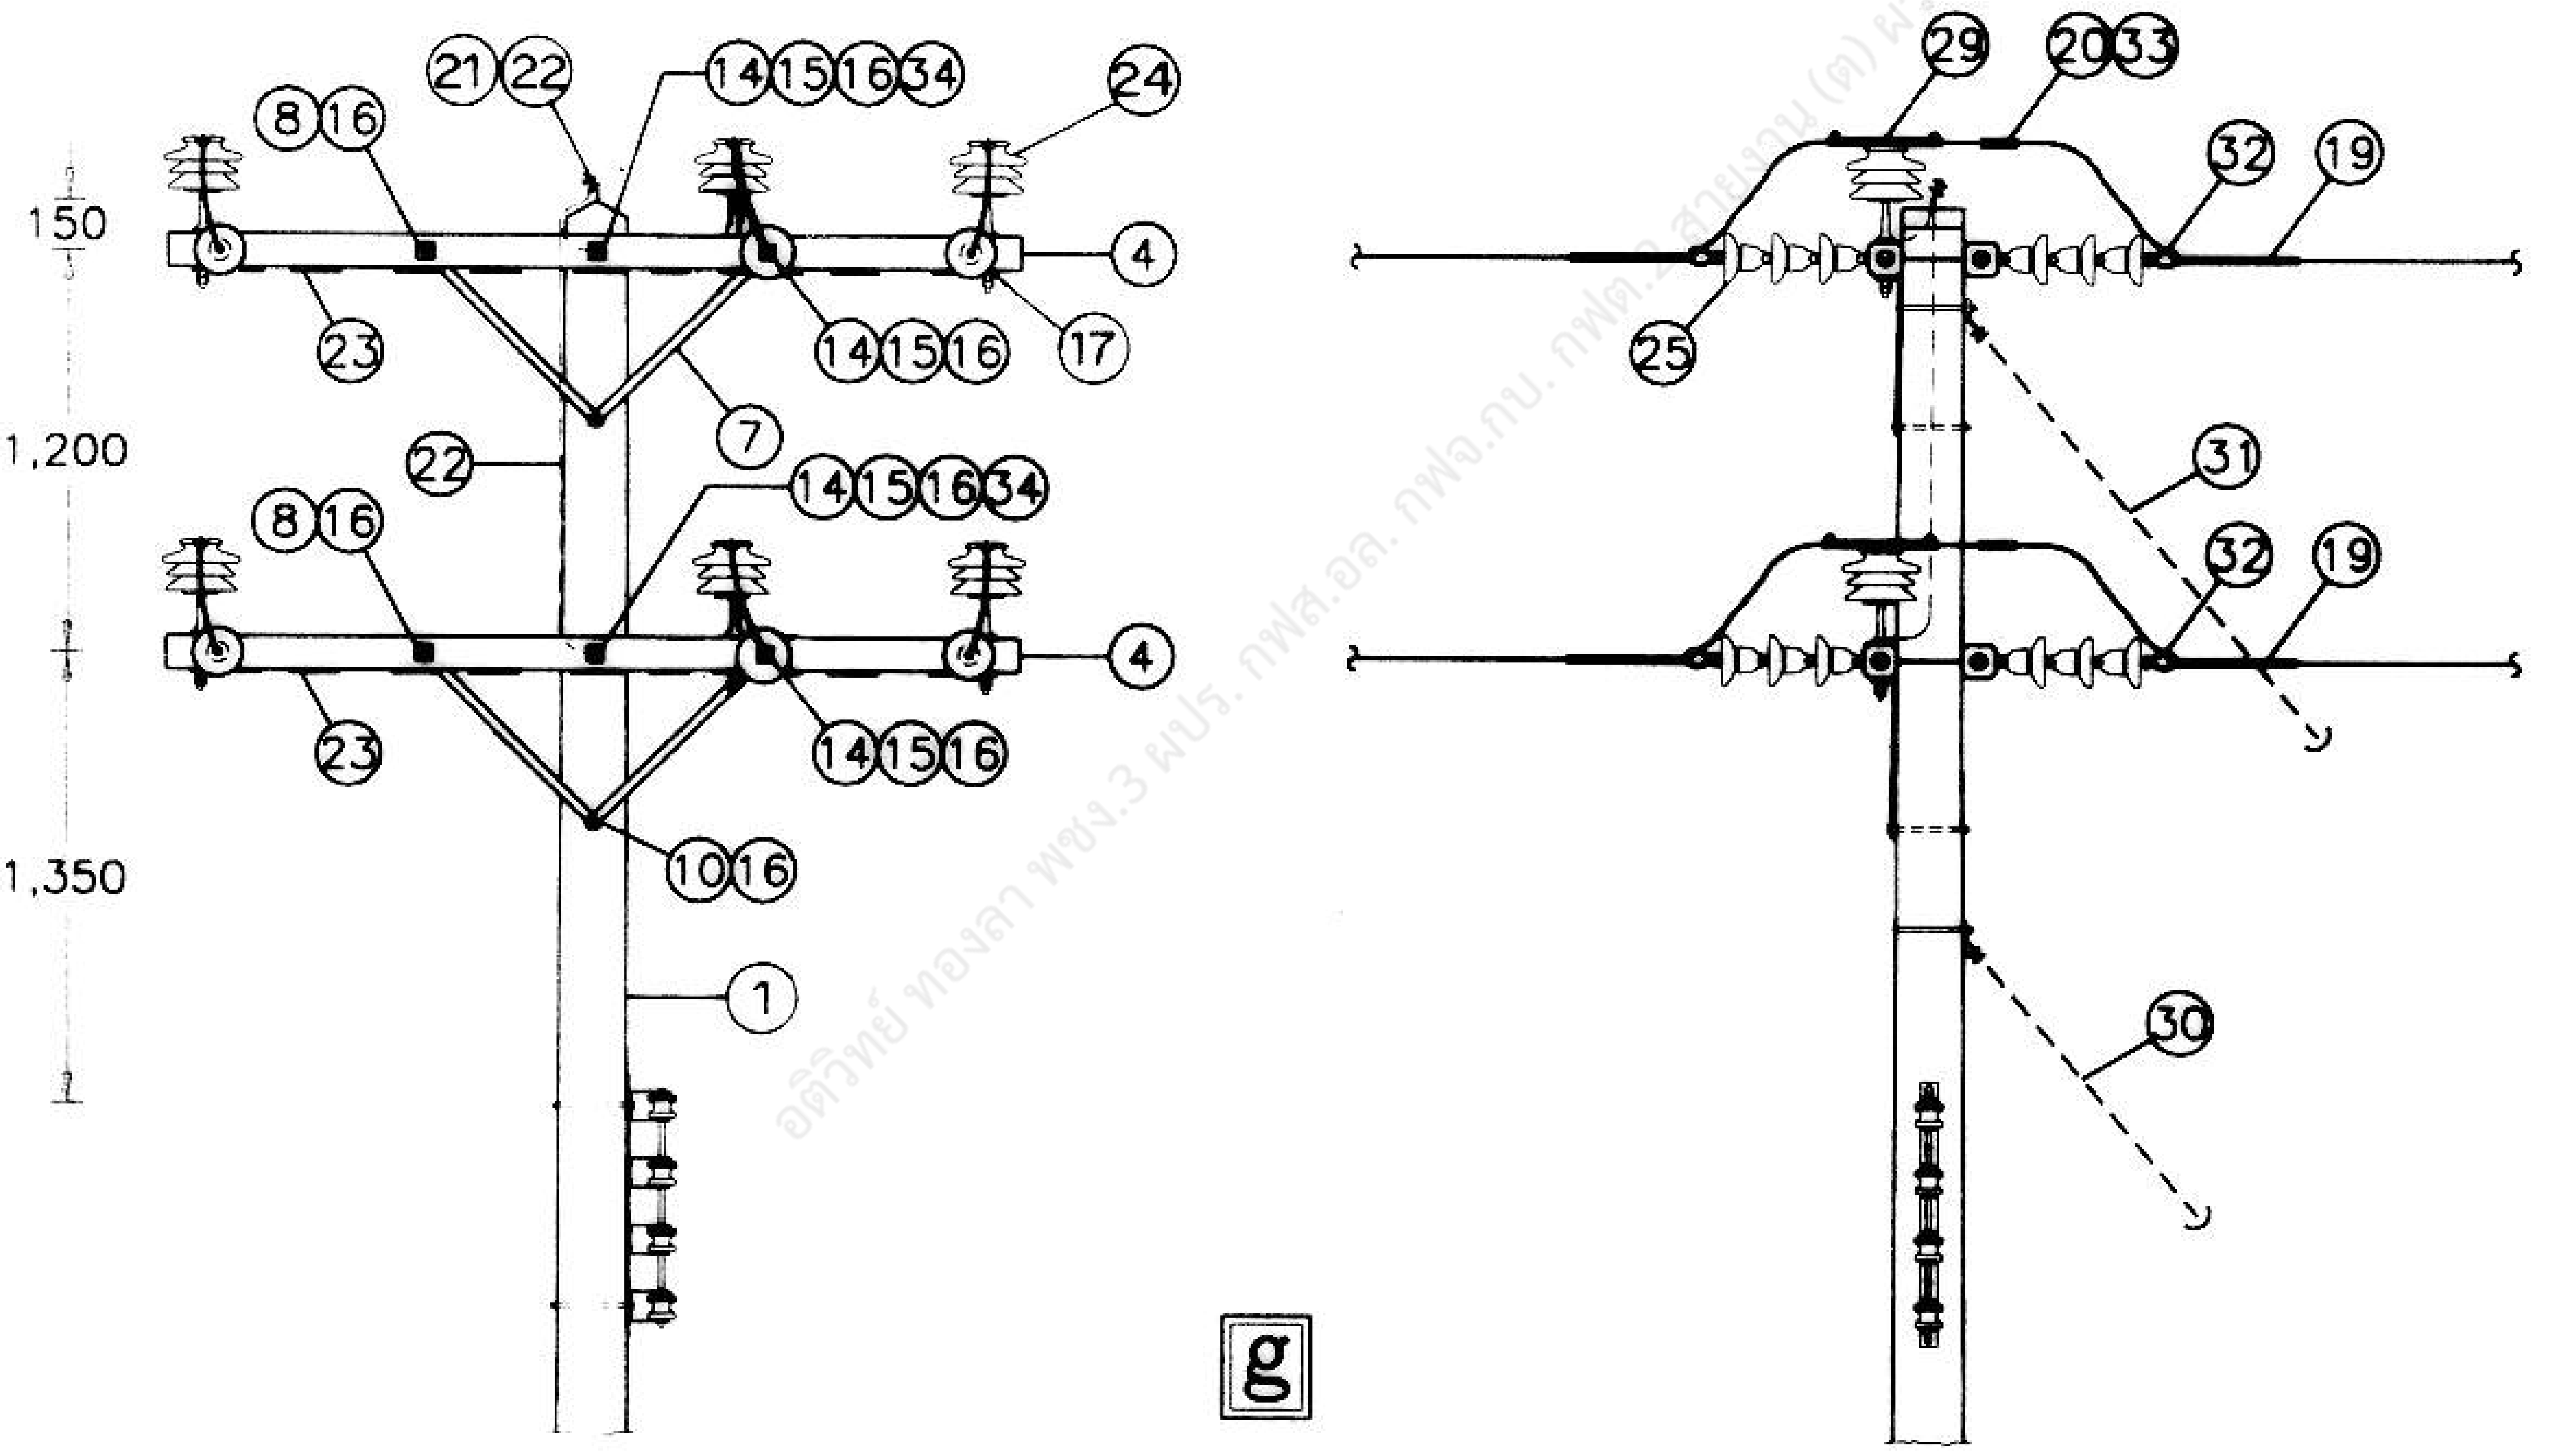

g

III สำหรับเข้าปลายสายสองข้าง
FOR DOUBLE DEADEND

อดิวิทย์ ทองลา พชง.3 ผปร. กฟส.อล. กฟจ.กบ. กฟต.2 สายงาน (ต) ผวก. @PEA

กองวิศวกรรมไฟฟ้าและเครื่องกล
ฝ่ายวิศวกรรม

ผู้เขียน Suppakit Boonrung
ผู้สำรวจ..................
วิศวกร..................
หัวหน้าแผนก..................
ผู้อำนวยการกอง..................
ผู้อำนวยการฝ่าย..................

รองผู้ว่าการเทคนิคและบริการ
....

การไฟฟ้าส่วนภูมิภาค

ผู้ว่าการ..................

การติดตั้งเคเบิลอากาศ ระบบ 22-33 kV 1-2 วงจร
(กับเสา คอร. ขนาด 12.20 เมตร)

22-33 kV AERIAL CABLE INSTALLATION, 1-2 CIRCUIT
(FOR CONCRETE POLE 12.20 m)

ใช้แทนแบบ..................
ถูกแทนโดยแบบ..................
เขียนเสร็จวันที่ 2 ธ.ค. 2540
แก้แบบวันที่..................
มิติเป็น มิลลิเมตร
มาตราส่วน 1 : 50
แบบเลขที่ SA4-015/40018
แผ่นที่ 3 ของจำนวน 7 แผ่น

การประกอบเลขที่ 2323
ASSEMBLY NO. 3909

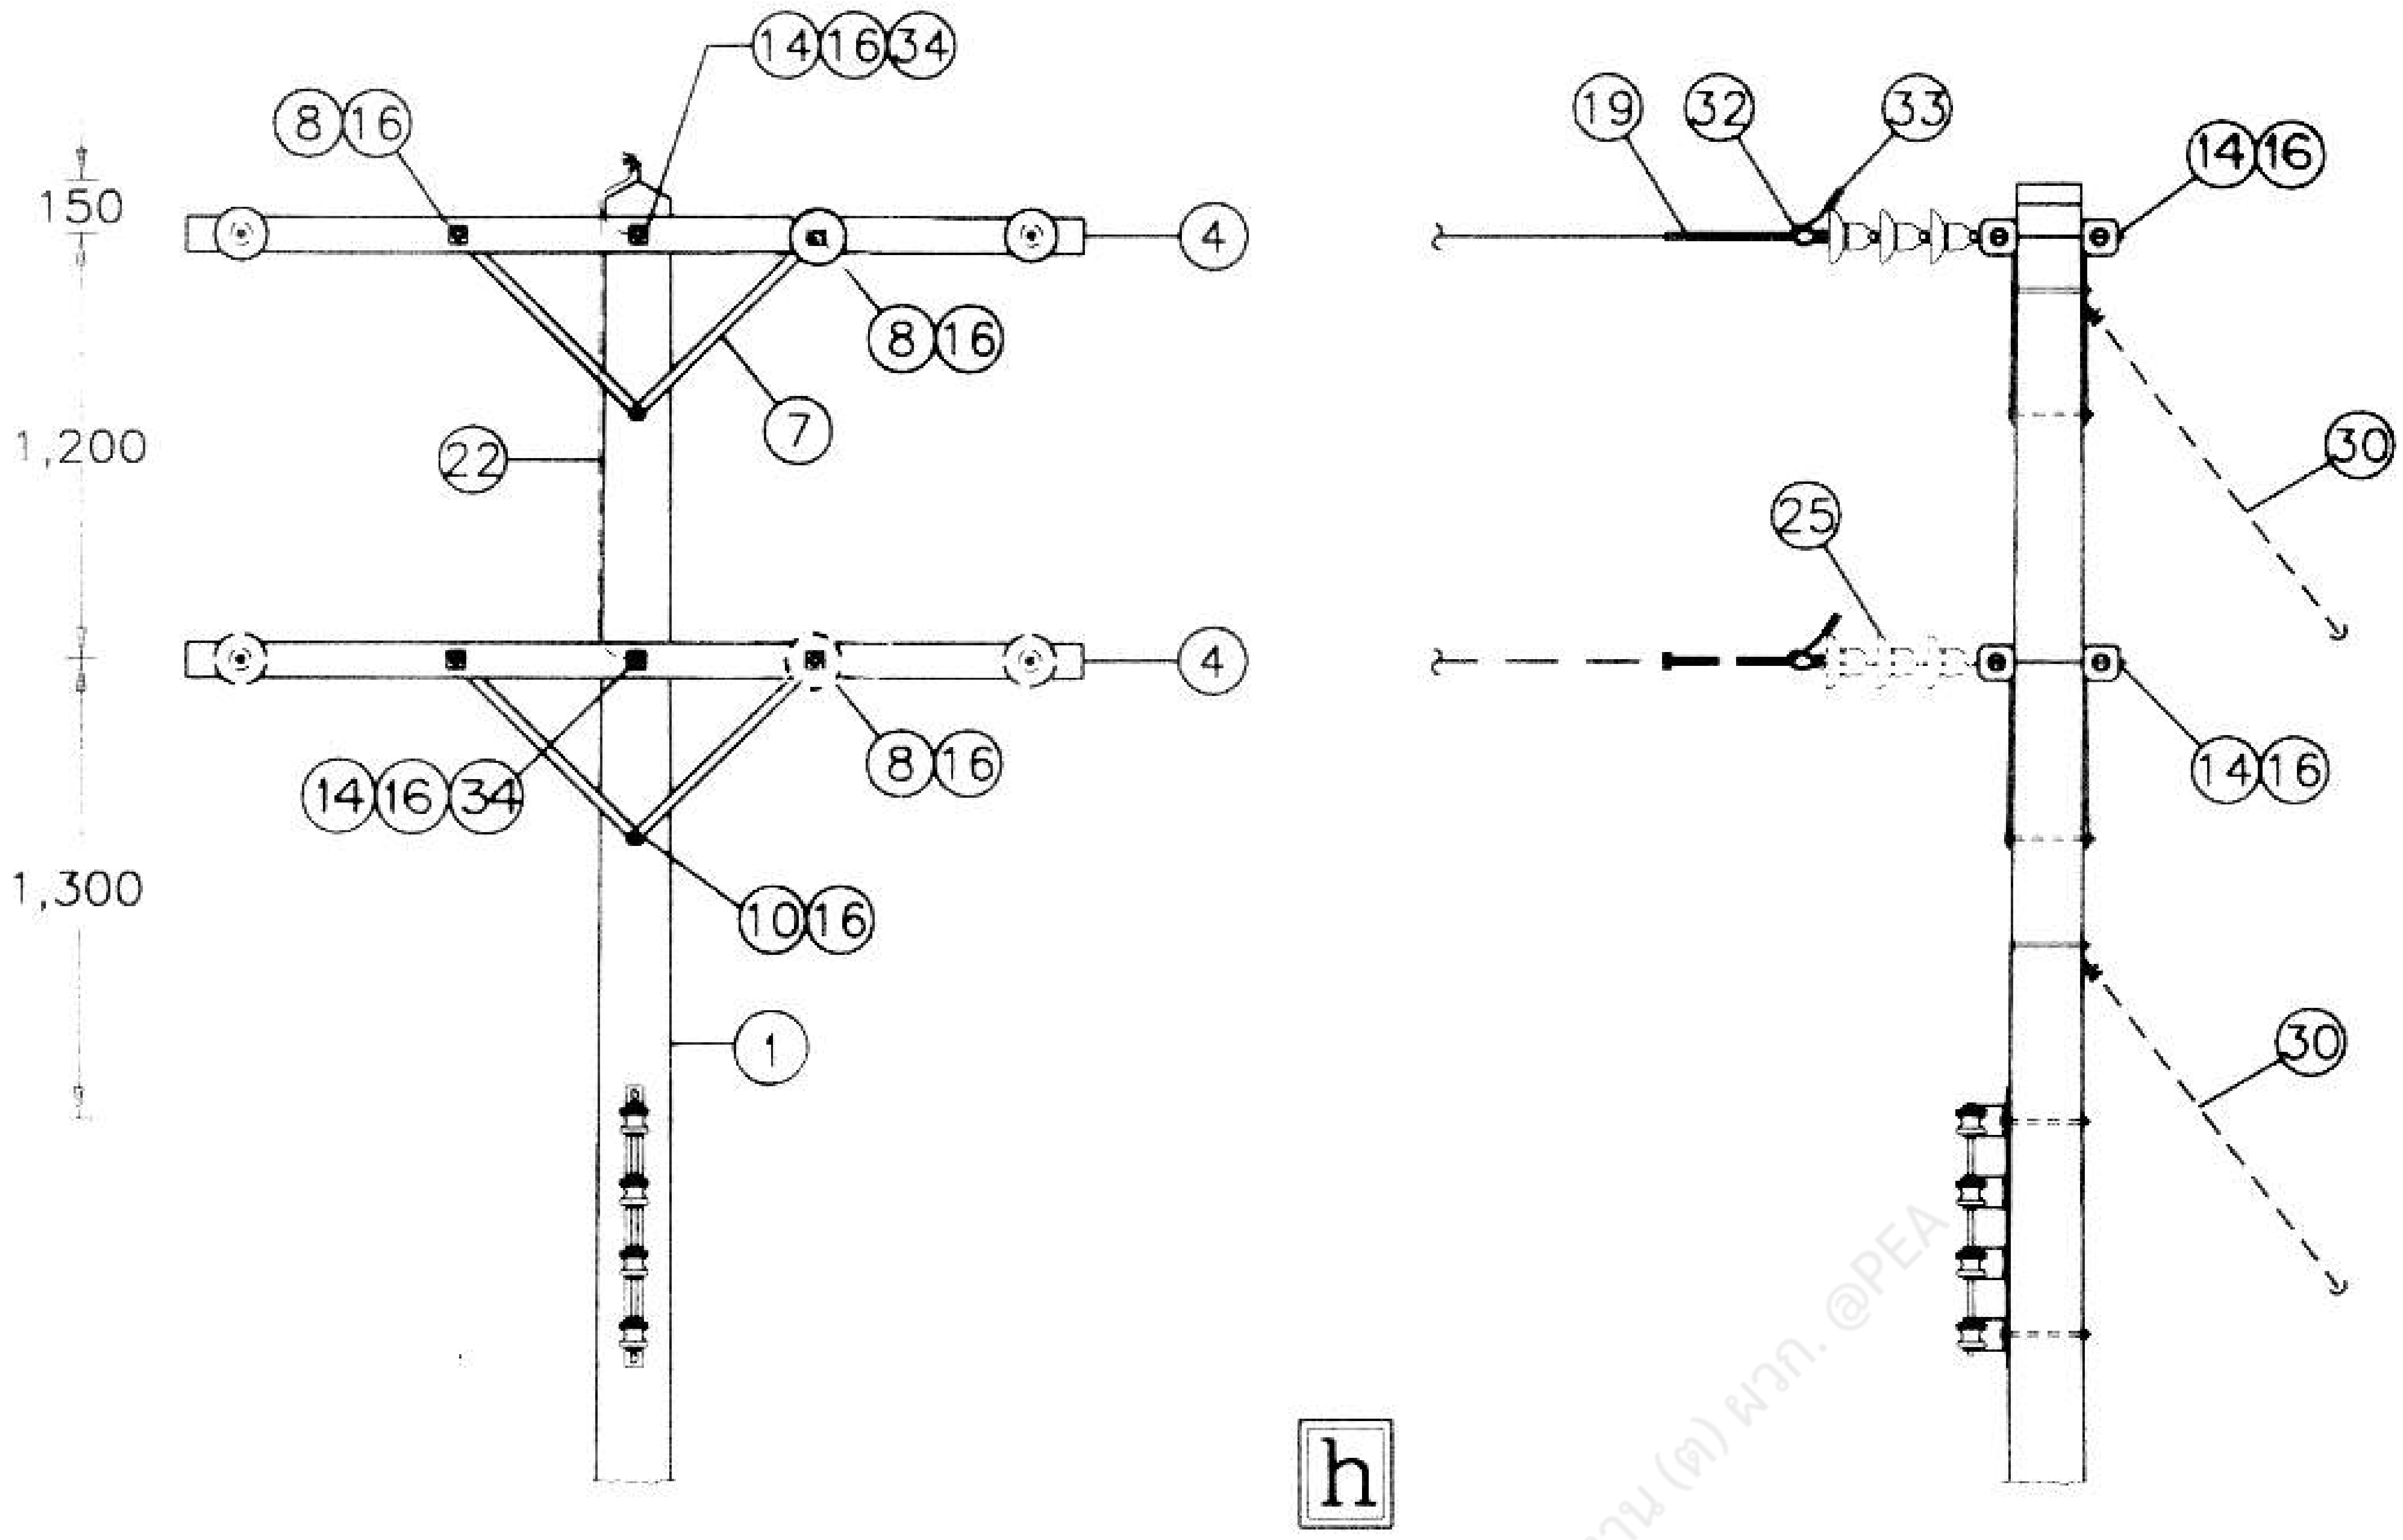

h

IV สำหรับเข้าปลายสายต้นสุดท้าย
FOR DEADEND

อดิวิทย์ ทองลา พชง.3 ผปร. กฟส.อล. กฟจ.กบ. สายงาน (ต) ผวก. @PEA

กองวิศวกรรมไฟฟ้าและเครื่องกล
ฝ่ายวิศวกรรม

การไฟฟ้าส่วนภูมิภาค

ใช้แทนแบบ................
ถูกแทนโดยแบบ...........

ผู้เขียน.....................
ผู้สำรวจ.....................
วิศวกร.....................
หัวหน้าแผนก.....................
ผู้อำนวยการกอง.....................
ผู้อำนวยการฝ่าย.....................

ผู้ว่าการ.....................

เขียนเสร็จวันที่ 2 ธ.ค. 2540
แก้แบบวันที่ ....

การติดตั้งเคเบิลอากาศ ระบบ 22–33 kV 1–2 วงจร
(กับเสา คอร. ขนาด 12.20 เมตร)

มิติเป็น มิลลิเมตร
มาตราส่วน 1 : 50

รองผู้ว่าการเทคนิคและบริการ
....

22–33 kV AERIAL CABLE INSTALLATION, 1–2 CIRCUIT
(FOR CONCRETE POLE 12.20 m)

แบบเลขที่ SA4–015/40018
แผ่นที่ 4 ของจำนวน 7 แผ่น

การประกอบเลขที่ 2323
ASSEMBLY NO. 3909

บัญชีวัสดุ
BILL OF MATERIAL

ลำดับที่ ITEM	รายละเอียด DESCRIPTION	จำนวน REQ'D								วัสดุเลขที่ MAT. NO.
		a	b	c	d	e	f	g	h	
1	เสาคอนกรีต 12.20 เมตร POLE, CONCRETE, 12.20 m LONG	1	1	1	1	1	1	1	1	00010012
2	คอน คอนกรีตอัดแรง ขนาด 100x100x1,500 มม. CROSSARM, PRESTRESSED CONCRETE, 100x100x1,500 mm	1	–	–	–	–	–	–	–	00110000
3	คอน คอนกรีตอัดแรง สปัน ขนาด 100x100x2,500 มม. CROSSARM, PRESTRESSED CONCRETE, 100x100x2,500 mm	–	–	1	–	1	–	–	1	00110001
4	คอน คอนกรีตอัดแรง สปัน (สำหรับเข้าปลายสาย) ขนาด 120x120x2,500 มม. CROSSARM, SPUN, PRESTRESSED CONCRETE (FOR DEADENDING), 120x120x2,500 mm	–	–	–	–	–	2	4	4	00110004
5	เหล็กคอนเคเบิลอากาศทางตรง BRACKET, FOR AERIAL CABLE TANGENT SUPPORT	–	2	–	–	–	–	–	–	01200002
6	เหล็กคอนเคเบิลอากาศทางโค้ง BRACKET, FOR AERIAL CABLE CORNER SUPPORT	–	–	–	2	–	–	–	–	02440104
7	เหล็กประกับคอน ขนาด 30x6x760 มม. BRACE, FLAT, FOR CROSSARM, 30x6x760 mm	2	–	2	–	2	2	4	8	01200001
8	สลักเกลียว M 16x130 มม. BOLT, MACHINE, M 16x130 mm	2	2	2	–	2	–	2	4	01110200
9	สลักเกลียว M 16x170 มม. BOLT, MACHINE, M 16x170 mm	2	–	2	–	2	2	–	–	01110201
10	สลักเกลียว M 16x250 มม. BOLT, MACHINE, M 16x250 mm	1	–	1	–	1	1	2	2	01110203
11	สลักเกลียว M 16x300 มม. BOLT, MACHINE, M 16x300 mm	1	–	1	–	1	–	–	–	01110204
12	สลักเกลียว M 16x450 มม. BOLT, MACHINE, M 16x450 mm	–	2	–	2	–	–	–	–	01110207
13	สลักห่วงกลม M 16x200 มม. BOLT, ROUND EYE, M 16x200 mm	–	–	–	2	–	–	–	–	01140001
14	สลักเกลียวห่วงกลม M 16x500 มม. BOLT, DOUBLE ARMING, ROUND EYE, M 16x500 mm	–	–	–	–	–	4	8	8	01130002
15	นัทรูปห่วง M 16 DIN 582 NUT, EYE, M 16 DIN 582	–	–	–	2	–	4	8	–	01180001
16	แหวนสี่เหลี่ยมแบน 52x52x4.5 มม. รู ø 18 มม. มอก. 258 WASHER, SQUARE, FLAT , 52x52x4.5 mm, HOLE ø 18 mm, TIS 258	11	6	11	4	11	21	32	30	01180100
17	แหวนสี่เหลี่ยมโค้ง 60x60x5 มม. รู ø 22 มม. WASHER, SQUARE, CURVED, 60x60x5 mm, HOLE ø 22 mm	–	–	–	–	–	3	6	–	01180201
18	แหวนรองแบบสปริง ขนาดระบุ 16 มม. มอก. 259 WASHER, LOCK, SPRING, SIZE 16 mm, TIS 259	2	2	2	–	2	2	–	2	01180300
19	ปรีฟอร์มเข้าปลายสาย สำหรับเคเบิลอะลูมิเนียมอากาศ 22-33 kV ขนาดตามต้องการ PREFORMED DEADEND, FOR 22-33 kV, AERIAL CABLE ; SIDE AS REQUIRED	–	–	–	–	–	6	12	6	02260000-4 02260100-4
20	หลอดต่อสายชนิดบีบไม่รับแรงดึง สายอะลูมิเนียม ขนาดตามต้องการ CONNECTOR, SPLICE, COMPRESSION TYPE, TENSIONLESS, Al ; SIZE AS REQUIRED	–	–	–	–	–	3	6	–	02410001-7

อภิรักษ์ ทองลา พชง. ผบปร. กฟส.อล. กฟจ.กบ. กฟต.2 สายงาน (พ) ผสอ. @PEA

กองวิศวกรรมไฟฟ้าและเครื่องกล
ฝ่ายวิศวกรรม

การไฟฟ้าส่วนภูมิภาค

ใช้แทนแบบ..................
ถูกแทนโดยแบบ..............

ผู้เขียน Supphakit Boonwong
ผู้สำรวจ..................
วิศวกร..................
หัวหน้าแผนก..................
ผู้อำนวยการกอง..................
ผู้อำนวยการฝ่าย..................

ผู้ว่าการ..................

เขียนเสร็จวันที่ 2 ธ.ค. 2540
แก้แบบวันที่..................

การติดตั้งเคเบิลอากาศ ระบบ 22-33 kV 1-2 วงจร
(กับเสา คอร. ขนาด 12.20 เมตร)

มิติเป็น มิลลิเมตร
มาตราส่วน..................

รองผู้ว่าการเทคนิคและบริการ
....

22-33 kV AERIAL CABLE INSTALLATION, 1-2 CIRCUIT
(FOR CONCRETE POLE 12.20 m)

แบบเลขที่ SA4-015/40018
แผ่นที่ 5 ของจำนวน 7 แผ่น

การประกอบเลขที่ 2323
ASSEMBLY NO. 3909

บัญชีวัสดุ
BILL OF MATERIAL

ลำดับที่ ITEM	รายละเอียด DESCRIPTION	จำนวน REQ'D a	b	c	d	e	f	g	h	วัสดุเลขที่ MAT. NO.
21	ยูแคล้มป์ สลัก 1 ตัว M 8 CLAMP, SINGLE U-BOLT, M 8	6	6	6	12	6	10	14	6	01230000
22	ลวดเหล็กตีเกลียว 50 ต.มม. มอก. 404 ความยาวตามต้องการ WIRE, STEEL STRANDED 50 mm ,^{2} TIS 404 ; LENGTH AS REQUIRED	ม m	ม m	ม m	ม m	ม m	ม m	ม m	ม m	01100004
23	ลวดเหล็กกลม เส้นผ่านศูนย์กลาง 4 มม. มอก. 71 (น้ำหนักประมาณ 0.1 กก./ม.) WIRE, STEEL, SOLID, DIA. 4 mm, TIS 71 (WEIGHT 0.1 kg/m)	–	–	–	–	–	ม 4 m	ม 8 m	–	01100000
24*	ลูกถ้วยก้านตรง มอก. 279 แบบ ข หรือ แบบ ค (แบบ 56-2 หรือ 56-3) พร้อมก้าน INSULATOR, PIN TYPE, TIS 279, TYPE B OR C (CLASS 56-2 OR 56-3) ; COMPLETE WITH PIN	–	–	–	6	–	3	6	–	03000001 or 03000002 03100000 or 03100001
25	ลูกถ้วยแขวน มอก. 354 แบบ ก หรือ แบบ ง (แบบ 52-1 หรือ 52-4) INSULATOR, SUSPENSION TYPE, TIS 354, TYPE A OR D (CLASS 52-1 OR 52-4)	–	–	–	–	–	18	36	18	03020000 or 03020002
26	แคล้มป์แขวนเคเบิล หรือกายแคล้มป์ สลัก 3 ตัว CLAMP, CABLE SUSPENSION, OR CLAMP, GUY TRIPLE BOLT	2	2	2	–	2	2	–	–	02440100 or 02440102
27	ที่จับเคเบิลสเปเซอร์ หรือห่วงแขวนเคเบิลสเปเซอร์ CLEVIS, FLAT STEEL, FOR CABLE SPACER ; OR LINK, CABLE SPACER	2	2	2	–	2	2	–	–	02440101 or 02440103
28	เคเบิลสเปเซอร์ ชนิดอะลูมินา 22-33 kV พร้อมห่วงรัด SPACER, CABLE, ALUMINA, 22-33 kV ; WITH SNAP TIES	2	2	2	–	2	2	–	–	02440001 – 02440003
29	ลวดอะลูมิเนียมกลม 4.0 มม. ความยาวตามต้องการ TIE, WIRE AI, 4.0 mm ; LENGTH AS REQUIRED	–	–	–	ม m	–	ม m	ม m	–	02200002
30	สายยึดโยง GY-21 หรือ GY-32 GUY ASSEMBLY, GY-21 OR GY-32	–	–	–	–	–	1	1	2	
31	สายยึดโยง GY-22 หรือ GY-32 GUY ASSEMBLY, GY-22 OR GY-32	–	–	–	–	–	–	1	–	
32	ทิมเบิลเคลวิส สำหรับปรีฟอร์มเข้าปลายสาย CLEVIS, THIMBLE, FOR PREFORMED DEADEND	–	–	–	–	–	6	12	6	03140011
33	เทปพันเคเบิลอากาศแรงสูง ขนาด 3/4" x 30' ELECTRICAL SPLICING TAPE, FOR H.T. AERIAL CABLE SIZE 3/4"x30'	–	–	–	–	–	ม้วน roll	ม้วน roll	–	02180003
34	กายทิมเบิ้ล สำหรับสายยึดโยง 50-95 ต.มม. THIMBLE, GUY, FOR STEEL WIRE 50-95 mm^2	–	–	–	4	–	2	4	2	01210304

* สามารถเลือกใช้ลูกถ้วยประเภทอื่นได้ เช่น ลูกถ้วยไลน์โพสท์ไทพ์ ลูกถ้วยพินโพสท์ไทพ์ เป็นต้น

CAN BE USE THE OTHER TYPE INSULATOR AS LINE POST TYPE INSULATOR, PIN POST TYPE INSULATOR etc.

กองวิศวกรรมไฟฟ้าและเครื่องกล
ฝ่ายวิศวกรรม

การไฟฟ้าส่วนภูมิภาค

ผู้เขียน Suppalit Boonruang
ผู้สำรวจ ....
วิศวกร ....
หัวหน้าแผนก ....
ผู้อำนวยการกอง ....
ผู้อำนวยการฝ่าย ....

ผู้ว่าการ ....

รองผู้ว่าการเทคนิคและบริการ
....

การติดตั้งเคเบิลอากาศ ระบบ 22-33 kV 1-2 วงจร
(กับเสา คอร. ขนาด 12.20 เมตร)

22-33 kV AERIAL CABLE INSTALLATION, 1-2 CIRCUIT
(FOR CONCRETE POLE 12.20 m)

ใช้แทนแบบ..................
ถูกแทนโดยแบบ..................
เขียนเสร็จวันที่ 2 ธ.ค. 2540
แก้แบบวันที่ ....
มิติเป็น มิลลิเมตร
มาตราส่วน..................

แบบเลขที่ SA4-015/40018
แผ่นที่ 6 ของจำนวน 7 แผ่น

การประกอบเลขที่ ASSEMBLY NO.	2323 3909

	แบบอ้างอิง REFERENCE DRAWING	แบบเลขที่ DWG. NO.	การประกอบเลขที่ ASSEMBLY NO.
1	โครงสร้างเสาระบบจำหน่าย 22–33 kV, 1–2 วงจร สำหรับแขวนเคเบิลอากาศ 22–33 kV DISTRIBUTION POLE STRUCTURE, 1–2 CIRCUIT FOR AERIAL CABLE STRINGING	IB2–015/40009	8253
2	การติดตั้งเคเบิลอากาศ ระบบ 22–33 kV 22–33 kV AERIAL CABLE INSTALLATION	S02–015/19162 SA1–015/34028 S02–015/16021 SA1–015/23077 SA1–015/23080	2301 2301 A 2302 3901 3904
3	การประกอบปรีฟอร์มเข้าปลายสายสำหรับเคเบิลอากาศ PREFORMED DEAD END ASSEMBLY FOR AERIAL CABLE	SA1–015/22016	9556
4	การต่อสายเคเบิลอากาศแรงสูง COMPRESSION SLEEVE, FOR H.T. AERIAL CABLE	SA1–015/22020	9562
5	การต่อปลายสายลวดเหล็กตีเกลียว STEEL STRANDED WIRE SPLICING	SA1–015/23053 SA1–015/28010	9563 9563 A
6	การประกอบสายลงดิน วิธียึดลวดเหล็ก GROUND LEAD ASSEMBLY	S02–015/19166 SA1–015/31012	9703 9703 A

หมายเหตุ : ข้อกำหนดการใช้งาน ระยะห่างระหว่างช่วงเสา และระยะหย่อนยานของสายที่มุมเบี่ยงแบนต่างๆ ดูรายละเอียดจากแบบเลขที่ IB2–015/40009 (การประกอบเลขที่ 8253)

NOTE : THE RECOMMENDATION OF SPAN LENGTH AND SAG OF CONDUCTOR AT ANY LINE DEFLECTION ANGLE, SEE DETAIL IN DRAWING No. IB2–015/40009 (ASSEMBLY No. 8253).

อดิวิทย์ ทองลา พชง.3 ผปร. กฟส.อล. กฟจ.กบ. กฟต.2 สายงาน ผวก. @PEA

กองวิศวกรรมไฟฟ้าและเครื่องกล ฝ่ายวิศวกรรม	การไฟฟ้าส่วนภูมิภาค	ใช้แทนแบบ............ ถูกแทนโดยแบบ............
ผู้เขียน ผู้สำรวจ............ วิศวกร............ หัวหน้าแผนก............ ผู้อำนวยการกอง............ ผู้อำนวยการฝ่าย............	ผู้ว่าการ............	เขียนเสร็จวันที่ 2 ธ.ค. 2540 แก้แบบวันที่ ....
	การติดตั้งเคเบิลอากาศ ระบบ 22–33 kV 1–2 วงจร (กับเสา คอร. ขนาด 12.20 เมตร)	วัดเป็น มิลลิเมตร มาตราส่วน............
รองผู้ว่าการเทคนิคและบริการ	22–33 kV AERIAL CABLE INSTALLATION, 1–2 CIRCUIT (FOR CONCRETE POLE 12.20 m)	แบบเลขที่ SA4–015/40018 แผ่นที่ 7 ของจำนวน 7 แผ่น