การประกอบเลขที่ ASSEMBLY NO. 3236

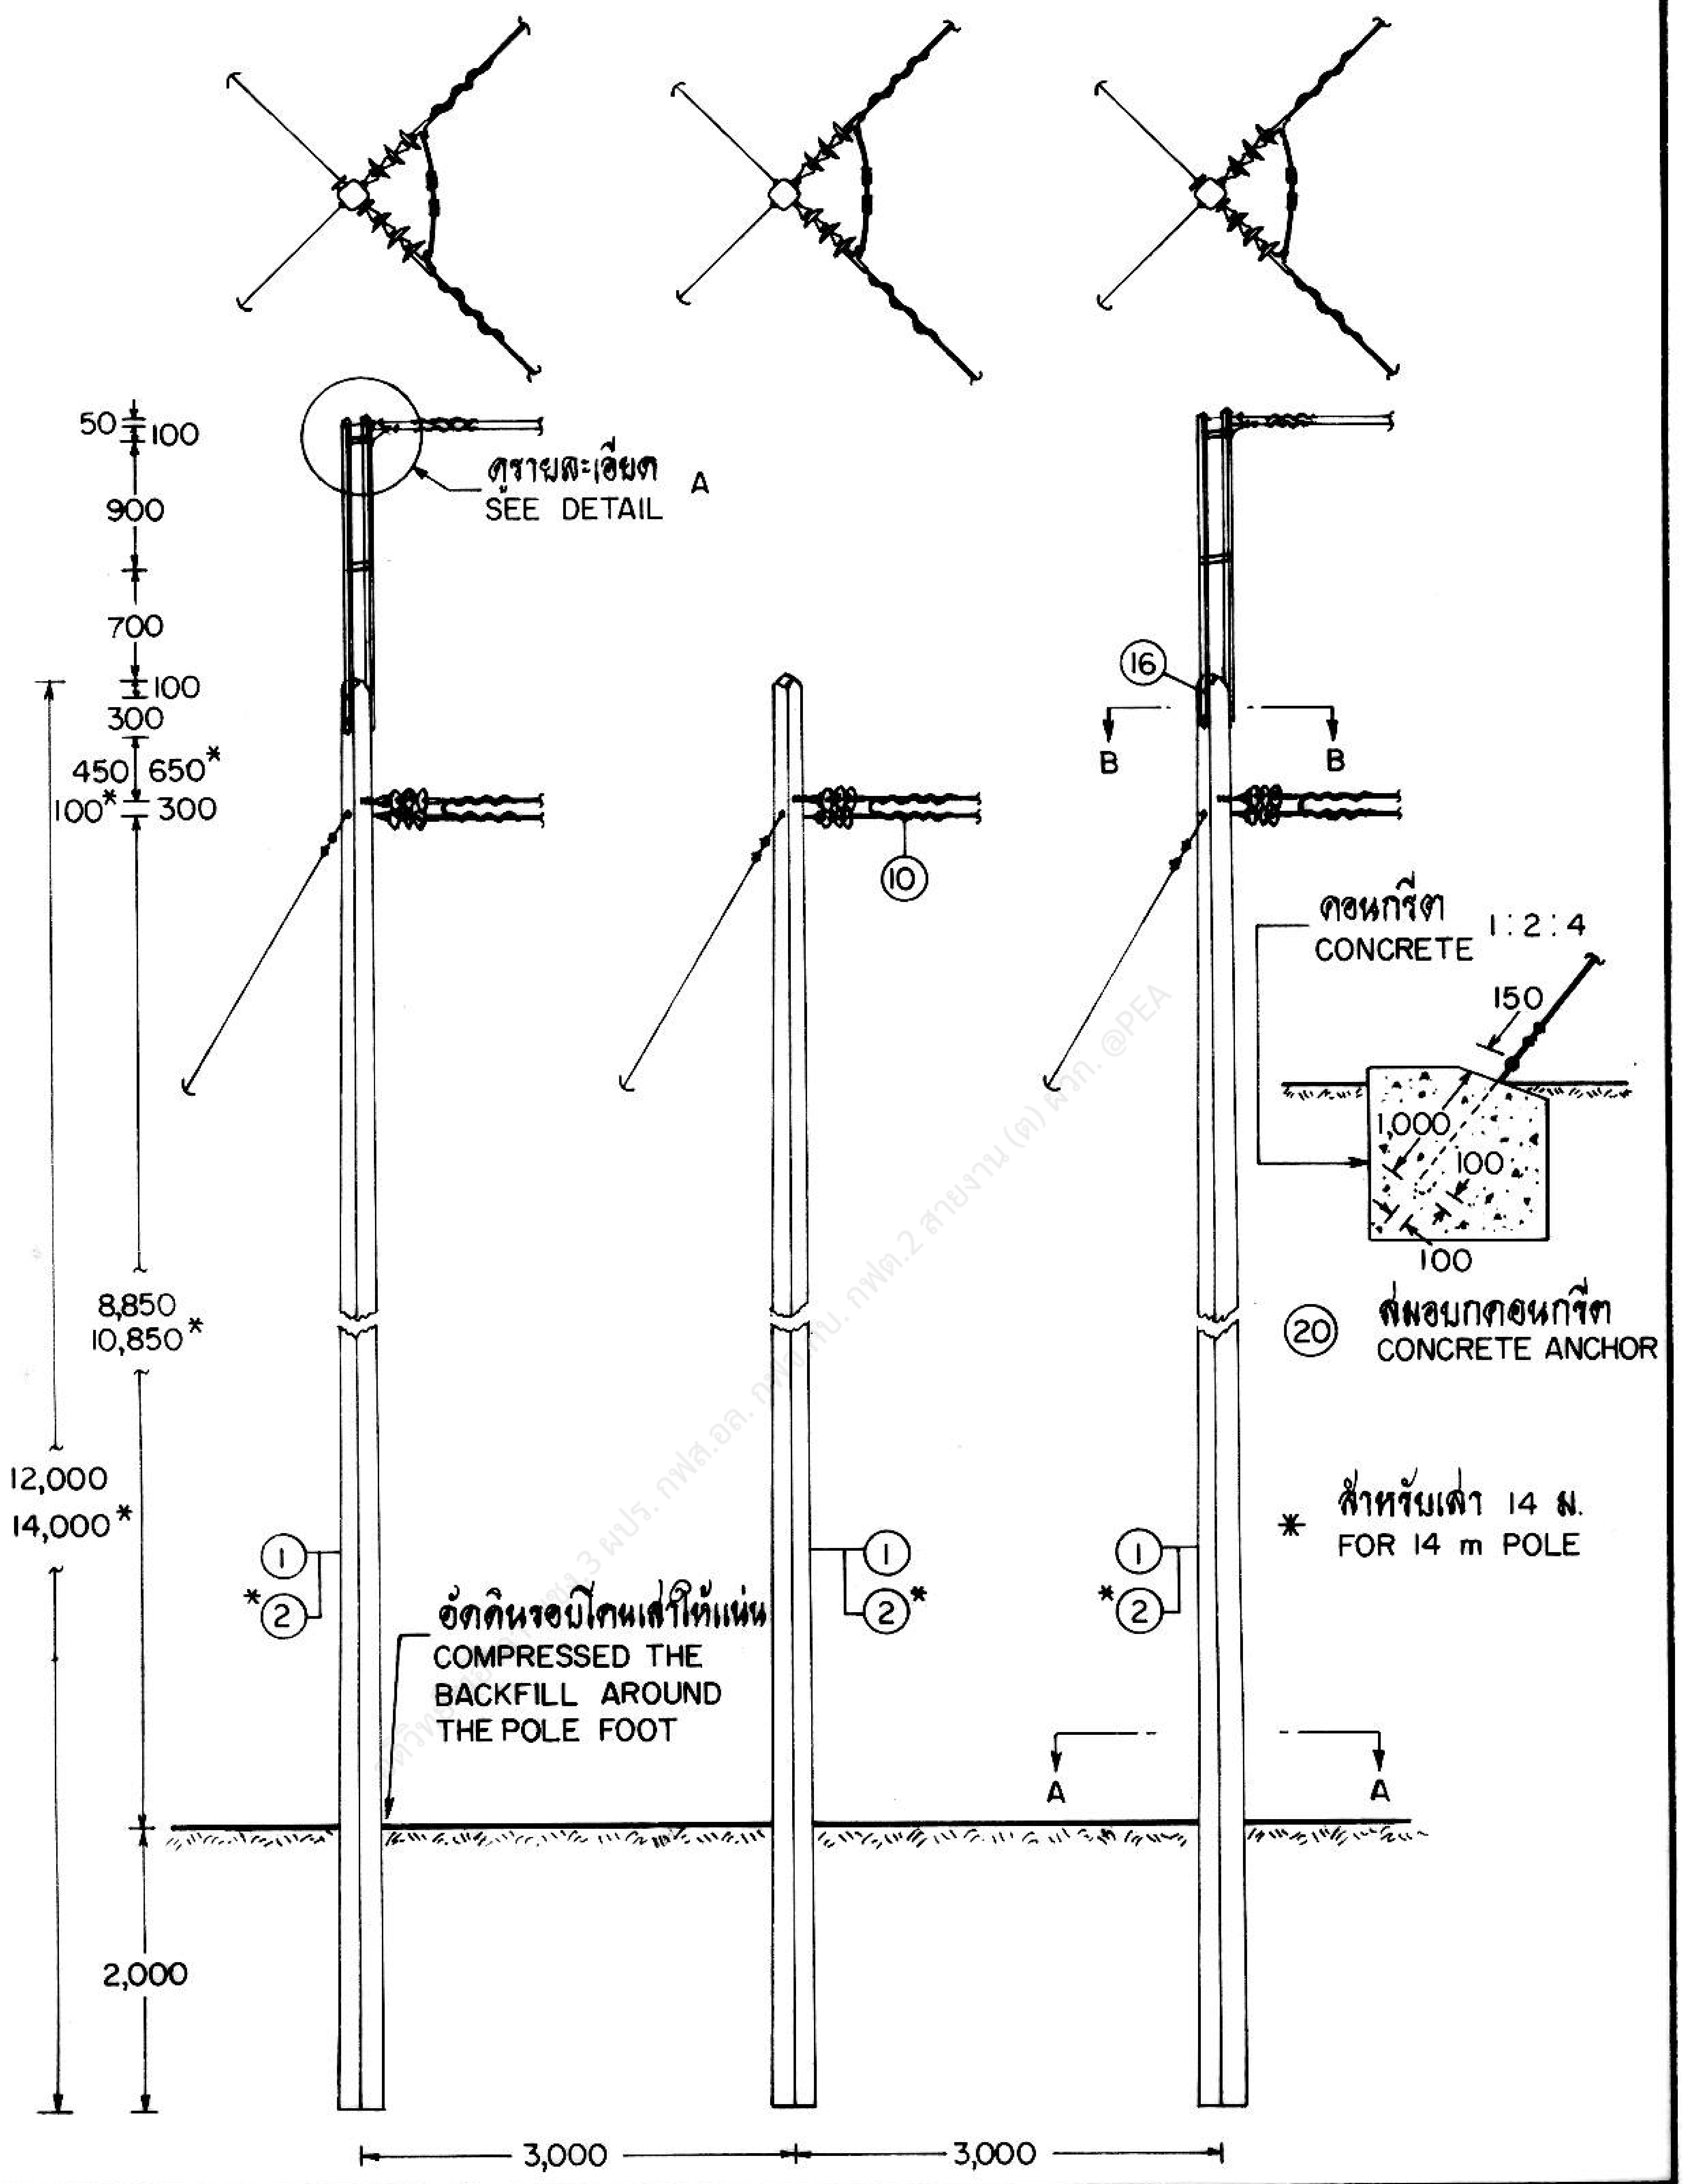

กองวิศวกรรมไฟฟ้าและเครื่องกล
ฝ่ายวิศวกรรม

ผู้เขียน
ผู้สำรวจ
วิศวกร
หัวหน้าแผนก
ผู้อำนวยการกอง
ผู้อำนวยการฝ่าย

รองผู้ว่าการฝ่ายเทคนิค

การไฟฟ้าส่วนภูมิภาค

ผู้ว่าการ 30 ก.ย. 34

โครงสร้างเสาสำหรับสายไฟฟ้า 3 เฟส 33 kV
ช่วงเสา 120 - 200 ม.
มุม >60°-90°

3-PHASE, 33 kV LINE STRUCTURE
SPAN 120 - 200 m
LINE ANGLE >60°-90°

ใช้แทนแบบ
ถูกแทนโดยแบบ
เขียนเสร็จวันที่ 22 ส.ค. 34
แก้แบบวันที่
มิติเป็น มิลลิเมตร
มาตราส่วน 1 : 75

แบบเลขที่ SAI-015/34022
แผ่นที่ 1 ของจำนวน 4 แผ่น

26 ก.ย. 2534 (แทน)

การประกอบเลขที่
ASSEMBLY NO. **3236**

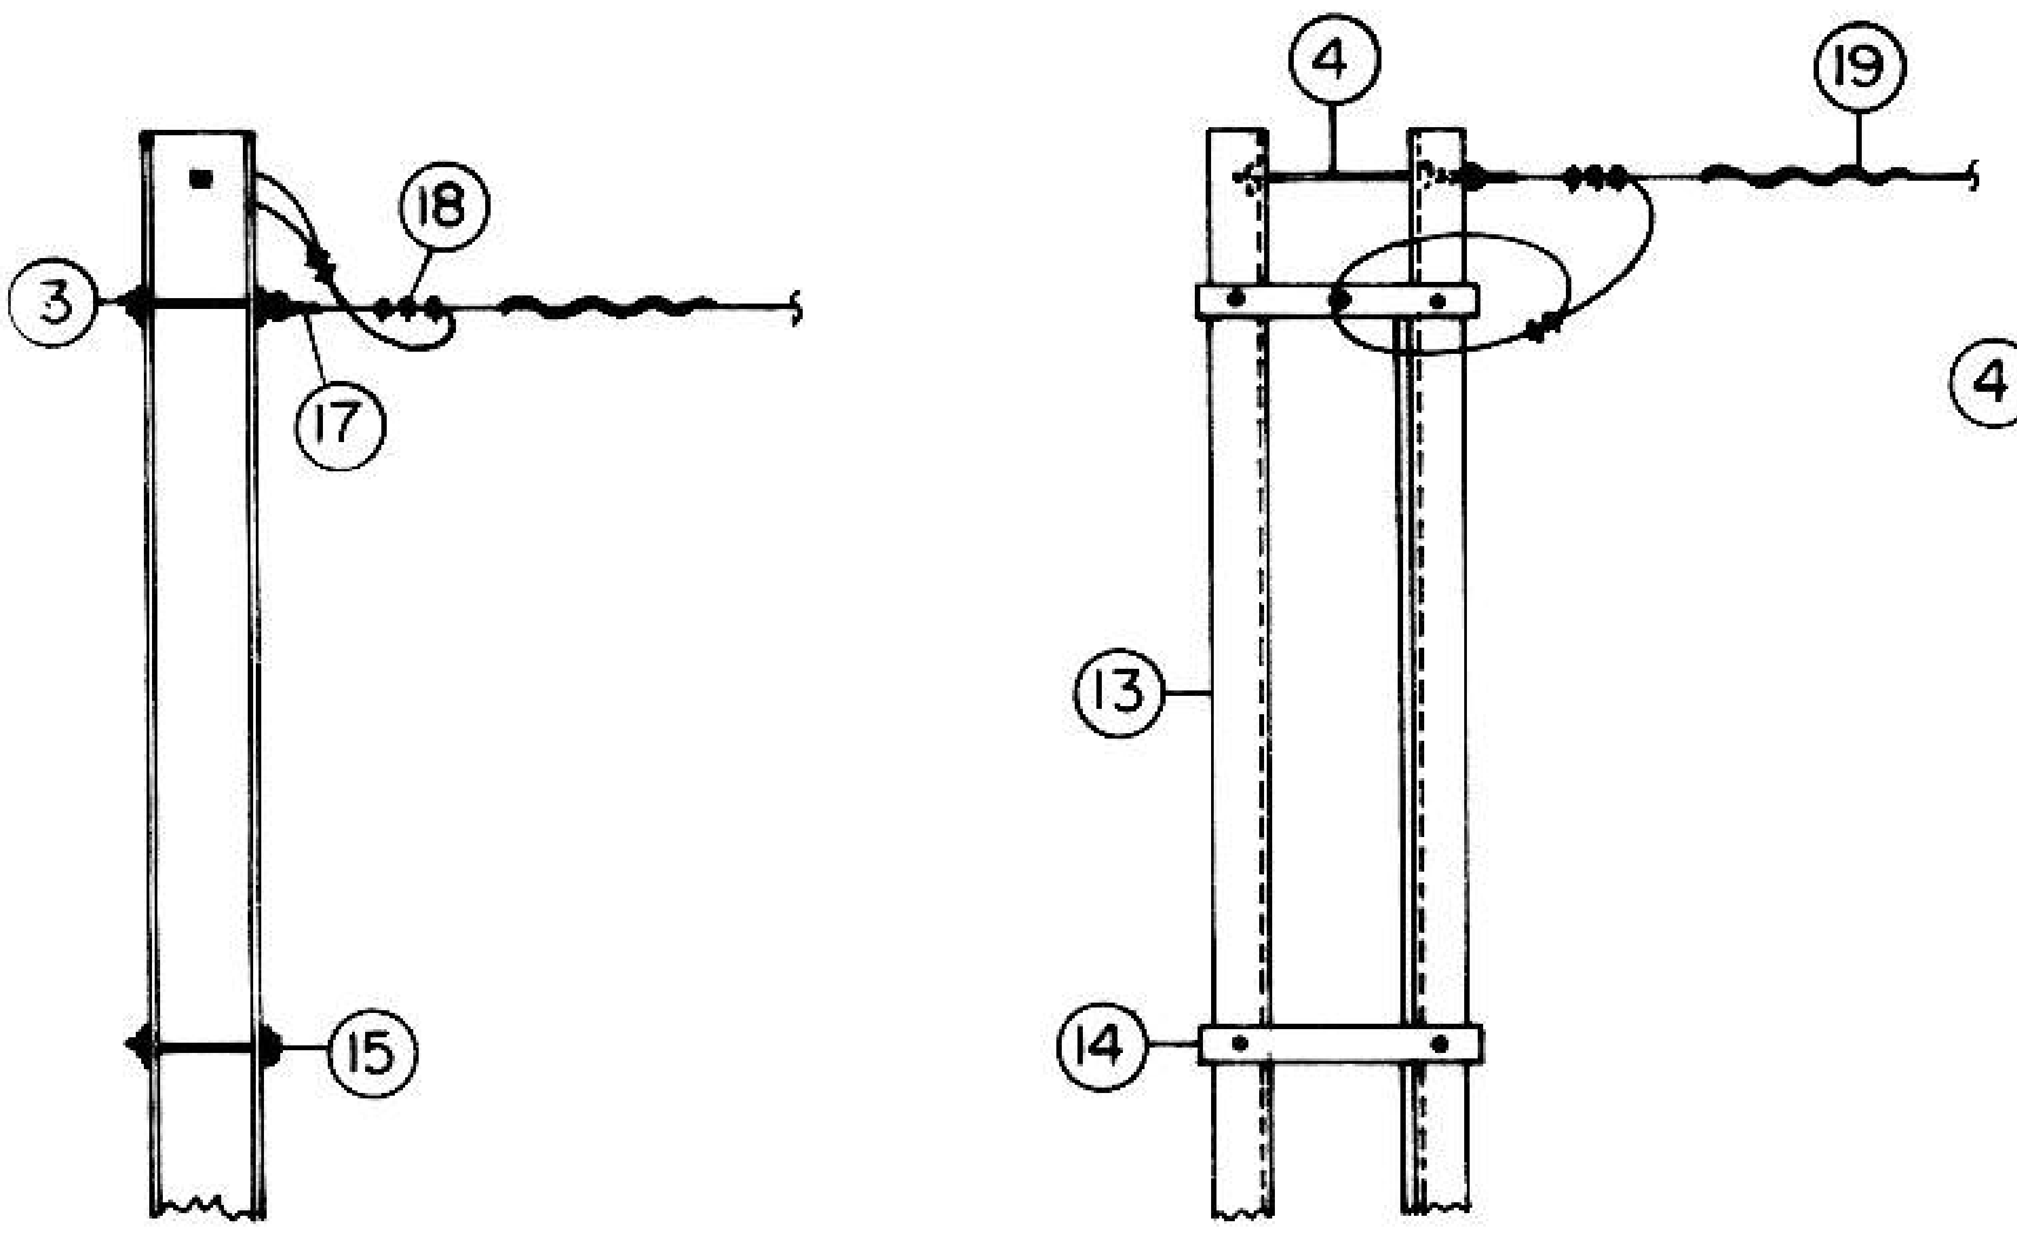

รายละเอียด
DETAIL A

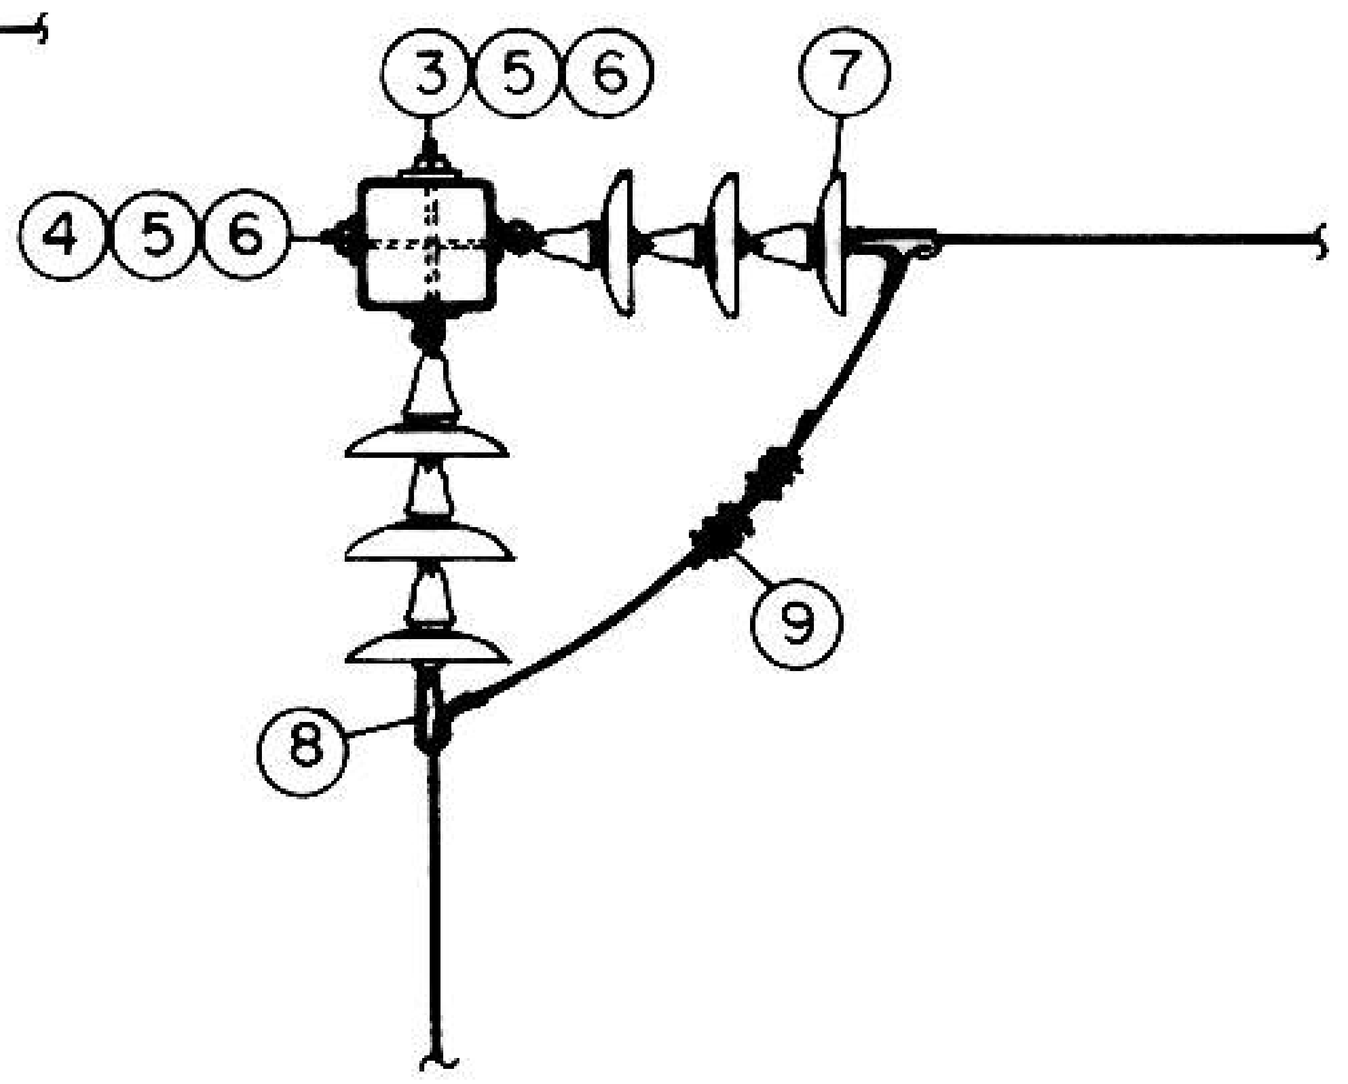

รูปตัด
SECTION B - B

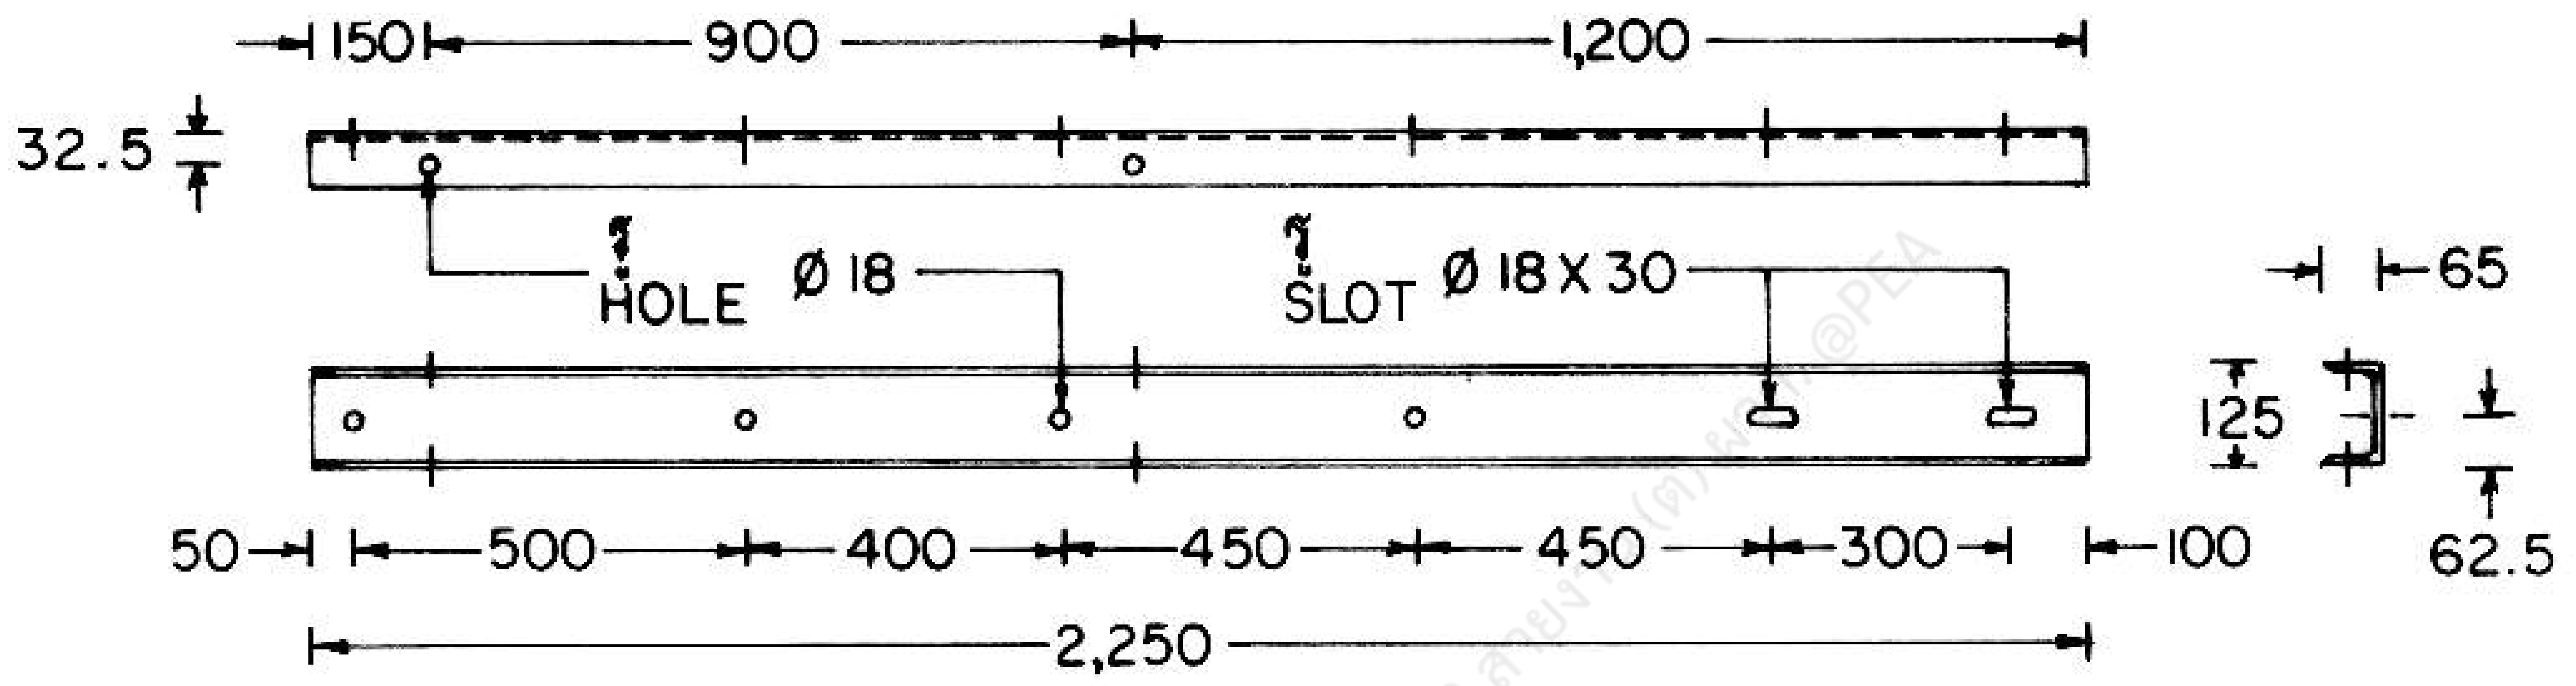

⑬ เหล็กรูปรางน้ำ ขนาด 125 X 65 X 6 มม. ยาว 2.25 ม. มอก. 116
STEEL, CHANNEL, 125 X 65 X 6 mm, 2.25 m LONG, TIS 116

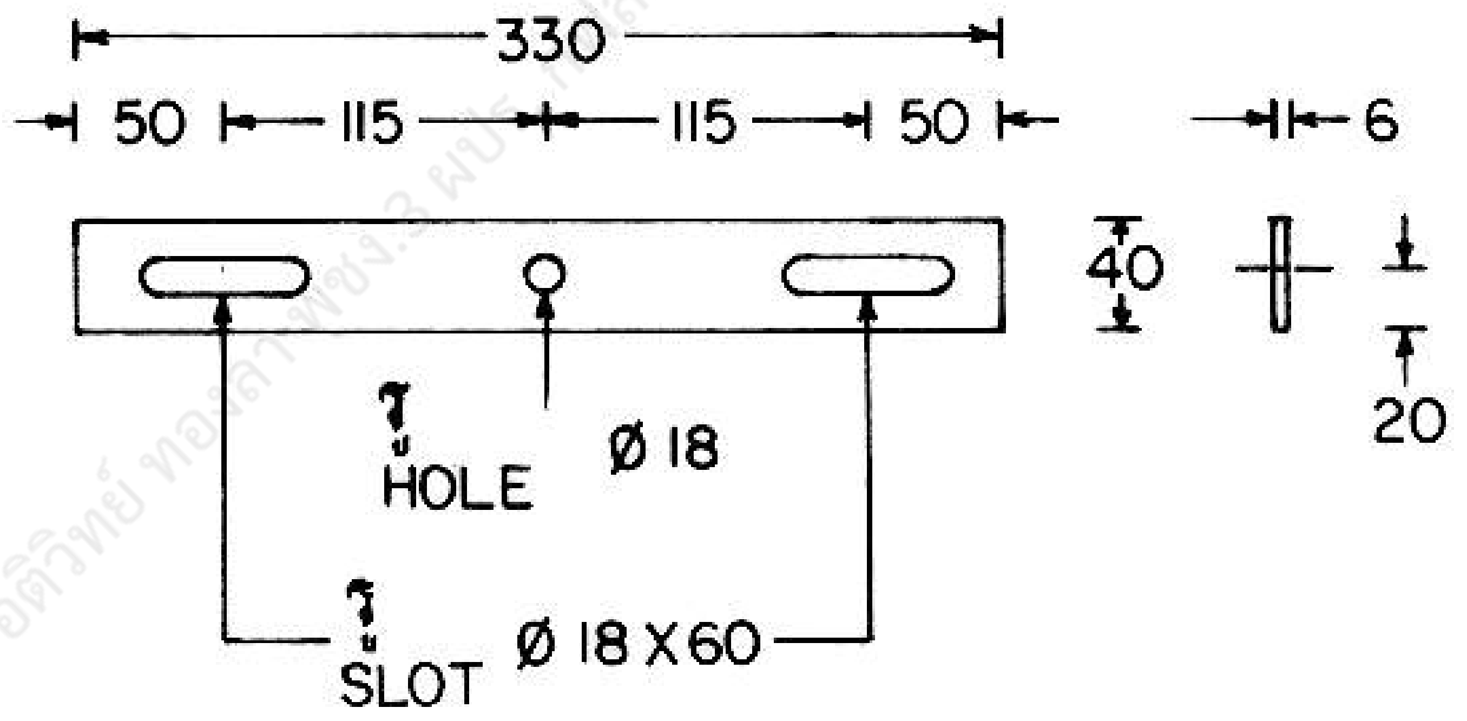

⑭ เหล็กแผ่น 40 X 6 มม. ยาว 330 มม. (อาจทำจากวัสดุเลขที่ 01200002 ได้)
STEEL, PLATE, 40 X 6 mm, 330 mm LONG (MAY BE MADE FROM MAT. NO. 01200002)

กองวิศวกรรมไฟฟ้าและเครื่องกล
ฝ่ายวิศวกรรม

ผู้เขียน
ผู้สำรวจ
วิศวกร สมพร
หัวหน้าแผนก
ผู้อำนวยการกอง
ผู้อำนวยการฝ่าย

รองผู้ว่าการฝ่ายเทคนิค

การไฟฟ้าส่วนภูมิภาค

ผู้ว่าการ 30 ก.ย.34

โครงสร้างเสาสำหรับสายไฟฟ้า 3 เฟส 33 kV
ช่วงเสา 120-200 ม.
มุม >60°-90°

3-PHASE, 33 kV LINE STRUCTURE
SPAN 120 - 200 m
LINE ANGLE >60°-90°

ใช้แทนแบบ
ถูกแทนโดยแบบ
เขียนเสร็จวันที่ 22 ส.ค.34
แก้แบบวันที่
มิติเป็น มิลลิเมตร
มาตราส่วน

แบบเลขที่ SAI-015/34022
แผ่นที่ 2 ของจำนวน 4 แผ่น

26 ก.ย. 2534

การประกอบเลขที่
ASSEMBLY NO. **3236**

บัญชีวัสดุ
BILL OF MATERIAL

ลำดับที่ ITEM	รายละเอียด DESCRIPTION	จำนวน REQ' D I	 II	วัสดุเลขที่ MAT. NO.
1	เสาคอนกรีต 12 ม. POLE, CONCRETE, 12 m LONG	3	–	00010003 (0033)
2	เสาคอนกรีต 14 ม. POLE, CONCRETE, 14 m LONG	–	3	00010005 (0035)
3	สลักเกลียวห่วงกลม M 16 X 250 มม. BOLT, ROUND EYE, M 16 X 250 mm	5	5	01140002 (0254)
4	สลักเกลียวห่วงกลม M 16 X 300 มม. BOLT, ROUND EYE, M 16 X 300 mm	5	5	01140003 (0255)
5	แหวนสี่เหลี่ยมแบน 52 X 52 X 4.5 มม. รู ø 18 มม. มอก. 258 WASHER, SQUARE, FLAT, 52 X 52 X 4.5 mm, HOLE ø 18 mm, TIS 258	12	12	01180100 (0355)
6	แหวนสปริง M 16 มอก. 259 WASHER, LOCK, M 16, TIS 259	6	6	01180301 (0365)
7	ลูกถ้วยแขวน มอก. 354 แบบ ง (แบบ 52-4) INSULATOR, SUSPENSION TYPE, TIS 354, TYPE D (CLASS 52-4)	18	18	03020002 (0415)
8	สเตรนแคล้มป์ สำหรับสายอะลูมิเนียมแกนเหล็ก CLAMP, STRAIN, FOR ACSR	6	6	01110207 - 03110005
9	พี.จี. คอนเน็คเตอร์ 3 สลัก CONNECTOR, PARALLEL GROOVE, TRIPLE BOLT	6	6	02300103 - 02300104
10	ไวเบรชั่นแดมเปอร์ แบบสไปแรล สำหรับสายอะลูมิเนียมเปลือย, สายอะลูมิเนียมแกนเหล็ก และ สายอะลูมิเนียมเจือ VIBRATION DAMPER, SPIRAL, FOR Al, ACSR, AND Al - ALLOY CONDUCTOR	6	6	02200101 - 02200103
11	การยึดโยง GY-32 (ลวดเหล็กตีเกลียว 95 ต.มม.) GUY, GY-32 (STEEL STRANDED WIRE 95 mm^2)	6	6	—
12	คอนกรีต 1 : 3 : 5 CONCRETE 1 : 3 : 5	13 ม.³ 13 m^3	13 ม.³ 13 m^3	—
13	เหล็กรูปรางน้ำ ขนาด 125 X 65 X 6 มม. ยาว 2.25 ม. มอก. 116 เจาะรูตามแบบแผ่นที่ 2 STEEL, CHANNEL, 125 X 65 X 6 mm, 2.25 m LONG; PUNCH HOLE AS DWG. ON SHEET NO. 2	4	4	—
14	เหล็กแผ่น ขนาด 40 X 6 มม. ยาว 330 มม. เจาะรูตามแบบแผ่นที่ 2 STEEL, PLATE, 40 X 6 mm, 330 mm LONG; PUNCH HOLE AS DWG. ON SHEET NO. 2	8	8	—
15	สลักเกลียว M 16 X 170 มม. BOLT, MACHINE, M 16 X 170 mm	8	8	01110201 (0221)
16	สลักเกลียว M 16 X 250 มม. BOLT, MACHINE, M 16 X 250 mm	4	4	01110203 (0223)
17	กายทิมเบิลสำหรับสายยึดโยง 50-95 ต.มม. THIMBLE, GUY, FOR STEEL WIRE 50-95 mm^2	4	4	01210304 (0150)
18	ยูแคล้มป์ สลัก 1 ตัว M 8 CLAMP, SINGLE U-BOLT, M 8	20	20	01230000 (0165)
19	ไวเบรชั่นแดมเปอร์ แบบสไปแรล สำหรับลวดเหล็กตีเกลียว 25 ต.มม. VIBRATION DAMPER, SPIRAL, FOR 25 mm^2 STEEL STRANDED WIRE	4	4	02200100 (0903)

กองวิศวกรรมไฟฟ้าและเครื่องกล
ฝ่ายวิศวกรรม

ผู้เขียน
ผู้สำรวจ
วิศวกร
หัวหน้าแผนก
ผู้อำนวยการกอง
ผู้อำนวยการฝ่าย

รองผู้ว่าการฝ่ายเทคนิค

การไฟฟ้าส่วนภูมิภาค

ผู้ว่าการ 30 ก.ย. 34

โครงสร้างเสาสำหรับสายไฟฟ้า 3 เฟส 33 kV
ช่วงเสา 120 - 200 ม.
มุม >60°-90°

3-PHASE, 33 kV LINE STRUCTURE
SPAN 120 - 200 m
LINE ANGLE >60°-90°

ใช้แทนแบบ
ถูกแทนโดยแบบ
เขียนเสร็จวันที่ 22 ส.ค. 34
แก้แบบวันที่
มิติเป็น
มาตราส่วน

แบบเลขที่ SAI-015/34022
แผ่นที่ 3 ของจำนวน 4 แผ่น

26 ก.ย. 2534

การประกอบเลขที่
ASSEMBLY NO. 3236

บัญชีวัสดุ
BILL OF MATERIAL

ลำดับที่ ITEM	รายละเอียด DESCRIPTION	จำนวน REQ'D I	 II	วัสดุเลขที่ MAT. NO
20	สมอบกคอนกรีต 1,250 X 1,250 X 1,250 มม. (คอนกรีต 1 : 2 : 4) ANCHOR, CONCRETE, 1,250 X 1,250 X 1,250 mm (CONCRETE 1 : 2 : 4)	6	6	—

ข้อกำหนด
REGULATIONS

ชนิดและขนาดของสายไฟฟ้า ต.มม. TYPE AND SIZE OF CONDUCTOR mm^2	ระยะระหว่างเสาสูงสุด ม. MAXIMUM SPAN LENGTH m	ระยะหย่อนยานต่ำสุดของสายไฟฟ้าทุกเส้น ม. MINIMUM SAG OF ALL CONDUCTORS m
ACSR 95/15	200	3.00
ACSR 120/20		4.00
ACSR 185/30		6.00
AA 95		3.00
AA 120		3.00
AA 185		4.00

หมายเหตุ

1. จำนวนในบัญชีวัสดุ :
   สดมภ์ I สำหรับเสาคอนกรีต 12 ม.
   สดมภ์ II สำหรับเสาคอนกรีต 14 ม.
2. ACSR หมายถึงสายอะลูมิเนียมแกนเหล็ก

   AA หมายถึงสายอะลูมิเนียมเจือ
3. เสาต้นที่ปักอยู่ในบริเวณที่เป็นดินอ่อน (ดินเหนียว, ดินเลน) หรือดินแข็งปานกลาง (ดินปนทราย) ให้เทคอนกรีตหุ้มโคนเสา ลึก 2.00 ม. จากระดับผิวดิน ขนาดหน้าตัด 1.50 X 1.50 ม.

NOTES

1. REQ'D IN BILL OF MATERIAL :
   COLUMN I , FOR 12 m CONCRETE POLE.
   COLUMN II , FOR 14 m CONCRETE POLE.
2. ACSR IS ALUMINIUM CONDUCTOR STEEL REINFORCED.

   AA IS ALL ALUMINIUM ALLOY CONDUCTOR.
3. THE POLE FOOT SHALL BE COVERED WITH CONCRETE 2.00 m DEPTH, CROSS-SECTION 1.50 X 1.50 m, IF IT IS SET IN POOR SOIL (MARCHY SOIL, OR CLAY) OR NORMAL SOIL (SANDY CLAY).

กองวิศวกรรมไฟฟ้าและเครื่องกล ฝ่ายวิศวกรรม	การไฟฟ้าส่วนภูมิภาค	ใช้แทนแบบ ถูกแทนโดยแบบ เขียนเสร็จวันที่ 22 ส.ค. 34 แก้แบบวันที่ ผลิตเป็น มาตราส่วน
ผู้เขียน ผู้สำรวจ วิศวกร หัวหน้าแผนก ผู้อำนวยการกอง ผู้อำนวยการฝ่าย	ผู้ว่าการ 30ก.ค.34 โครงสร้างเสาสำหรับสายไฟฟ้า 3 เฟส 33 kV ช่วงเสา 120-200 ม. มุม >60°-90°	
รองผู้ว่าการฝ่ายเทคนิค	3-PHASE, 33 kV LINE STRUCTURE SPAN 120 - 200 m LINE ANGLE >60°-90°	แบบเลขที่ SAI-015/34022 แผ่นที่ 4 ของจำนวน 4 แผ่น

อดีตพนักงาน พชง.3 ผปร. กฟส.อสล. กฟจ.กบ. กฟต.2 สายงาน (ต) ผวก. @PEA