

การประกอบเลขที่ ASSEMBLY NO. 3307

I การประกอบคอนไม้ WOOD CROSSARM ASSEMBLY

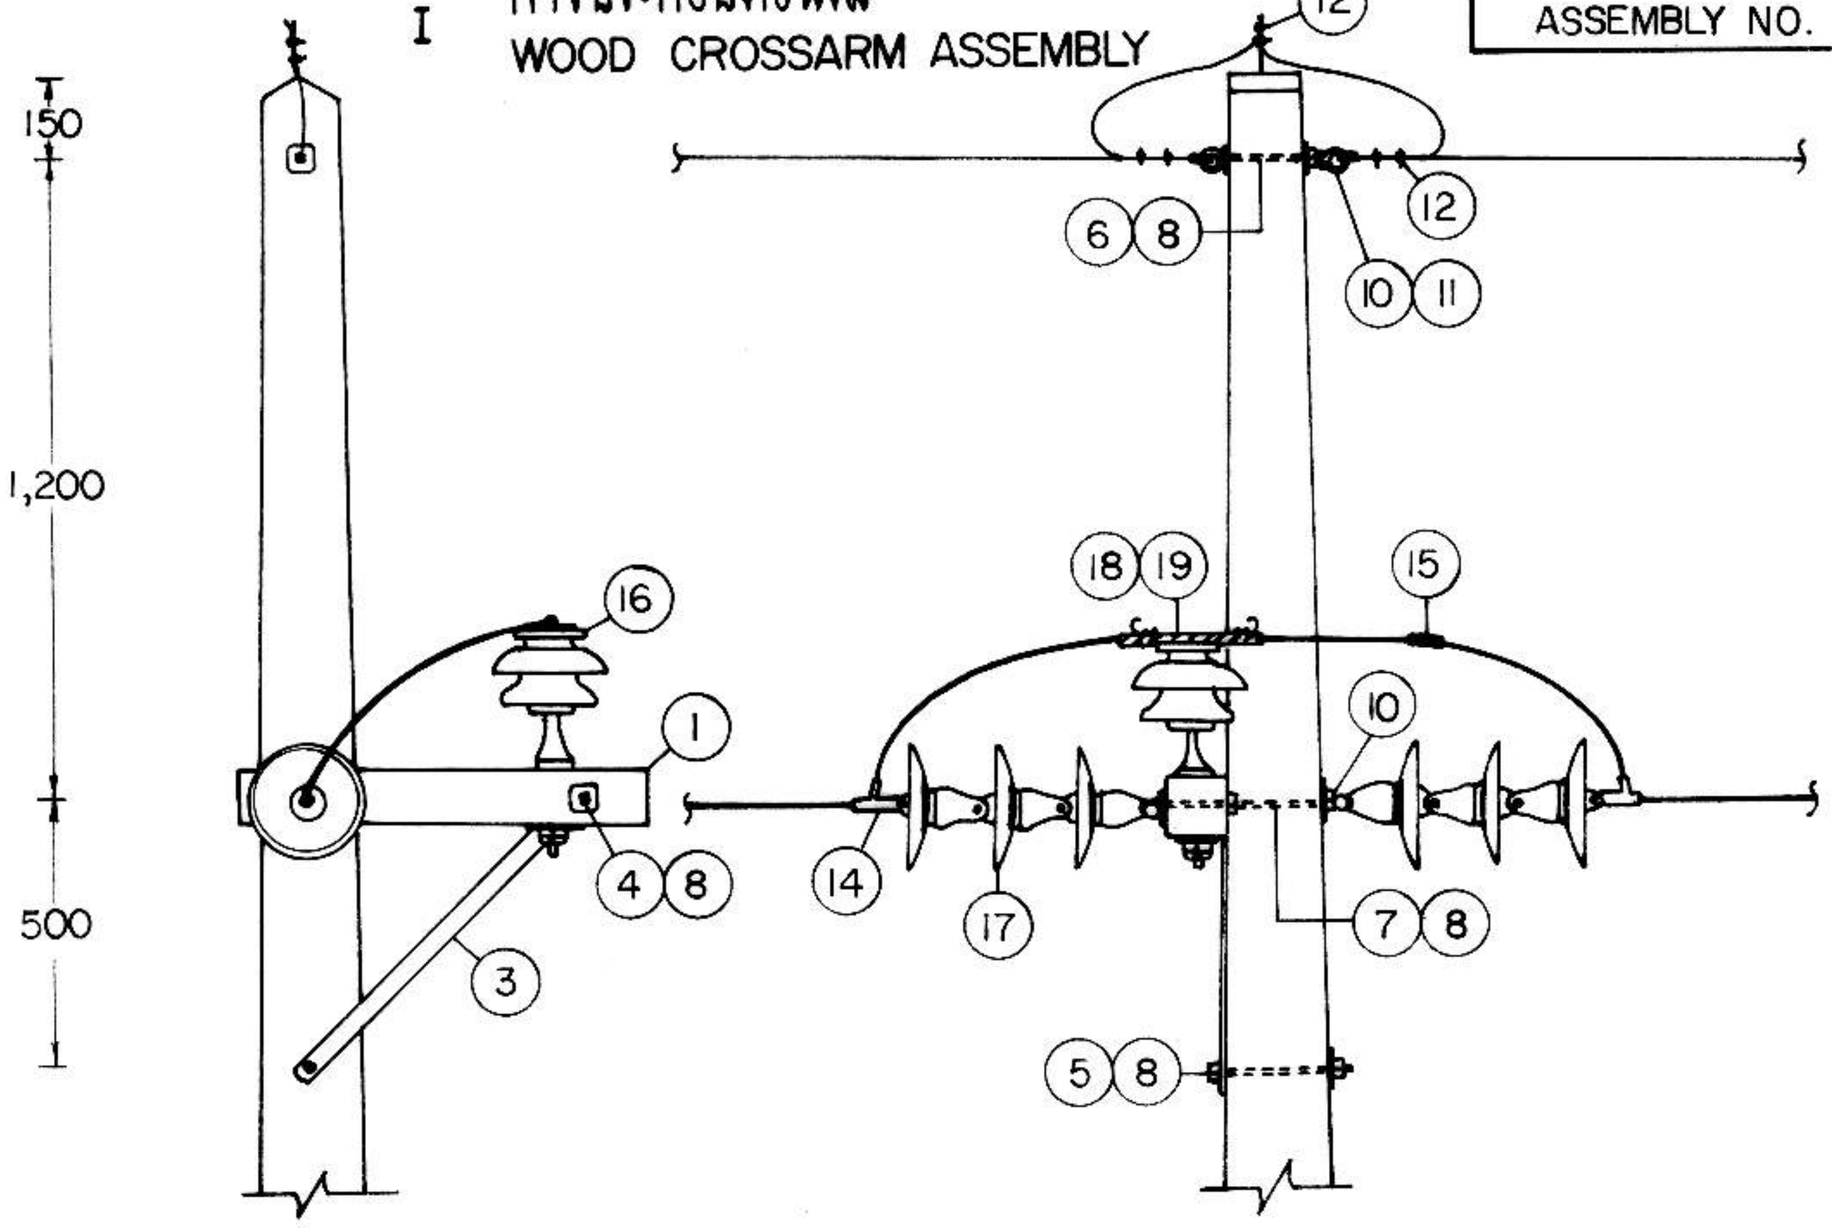

II การประกอบคอนเหล็ก STEEL CROSSARM ASSEMBLY

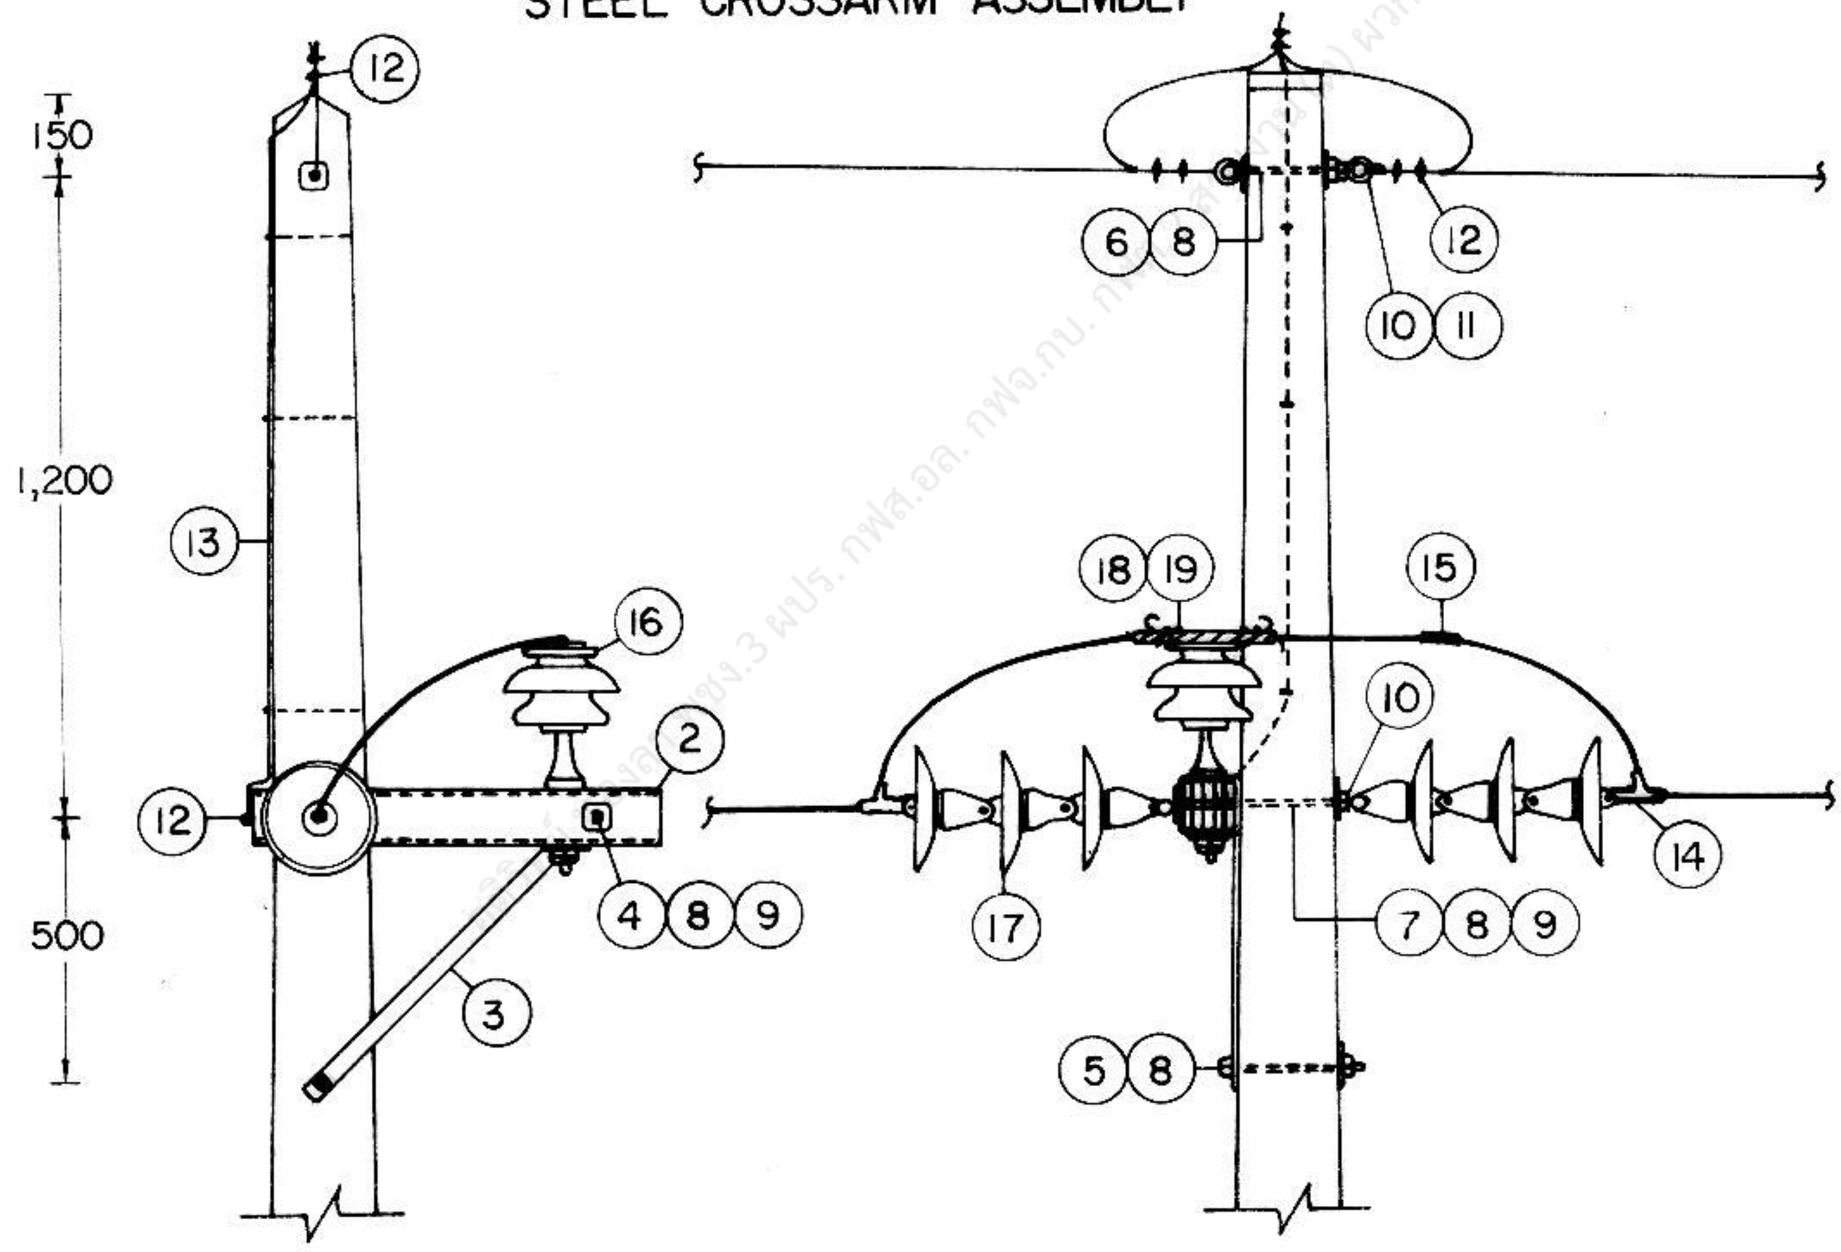

สำหรับใช้ก่อสร้างในที่ที่มีโหลดน้อย และไม่มีการปรับปรุงเป็นระบบ 3 เฟส 33 kV ในอนาคตอันใกล้

FOR LIGHT LOAD SITE CONSTRUCTION AND SHALL NOT BE REVAMPED TO 3-PHASE 33 kV SYSTEM IN THE NEAR FUTURE

กองวิศวกรรมไฟฟ้าและเครื่องกล ฝ่ายวิศวกรรม	**การไฟฟ้าส่วนภูมิภาค**	ใช้แทนแบบ ถูกแทนโดยแบบ
ผู้เขียน ผู้สำรวจ วิศวกร หัวหน้าแผนก หัวหน้ากอง ผู้อำนวยการฝ่าย	ผู้ว่าการ	เขียนเสร็จวันที่ 19 ม.ค. 21 แก้แบบวันที่ มิติเป็น MM. มาตราส่วน 1 : 25
รองผู้ว่าการฝ่ายเทคนิค	การติดตั้งอุปกรณ์เข้าปลายสายส่งข้างกับเสาคอนกรีต 12 ม. ระบบ 1 เฟส 19 kV DOUBLE DEADEND ASSEMBLY ON 12 m CONCRETE POLE 1-PHASE 19 kV SYSTEM	แบบเลขที่ SAI-015/21079 แผ่นที่ 1 ของจำนวน 2 แผ่น

การประกอบเลขที่ ASSEMBLY NO. 3307

บัญชีวัสดุ
BILL OF MATERIAL

ลำดับที่ ITEM	รายละเอียด DESCRIPTION	จำนวน REQ'D I	จำนวน REQ'D II	วัสดุเลขที่ MAT. NO.
1	ไม้คอนสาย 100 X 100 X 750 มม. CROSSARM, WOOD 100 X 100 X 750 mm	1	-	00110001 (0103)
2	คอนเหล็กกลวง สี่เหลี่ยมจัตุรัส 100 X 100 X 2.3 มม. ยาว 750 มม. CROSSARM, STEEL, SQUARE TUBING, 100 X 100 X 2.3 mm, 750 mm LONG	-	1	00120000 (0115)
3	เหล็กประกับไม้คอน 30 X 6 X 760 มม. BRACE, FLAT, FOR CROSSARM 30 X 6 X 760 mm	1	1	01200001 (0120)
4	สลักเกลียว M 16 X 130 มม. BOLT, MACHINE, M 16 X 130 mm	1	1	01110200 (0220)
5	สลักเกลียว M 16 X 200 มม. BOLT, MACHINE, M 16 X 200 mm	1	1	01110202 (0222)
6	สลักห่วงกลม M 16 X 200 มม. BOLT, ROUND EYE, M 16 X 200 mm	1	1	01140001 (0253)
7	สลักห่วงกลม M 16 X 300 มม. BOLT, ROUND EYE, M 16 X 300 mm	1	1	01140003 (0255)
8	แหวนสี่เหลี่ยมแบน 52 X 52 X 4.5 มม. รู Ø 18 มม. มอก. 258 WASHER, SQUARE, FLAT 52 X 52 X 4.5 mm HOLE Ø 18 mm TIS 258	4	4	01180100 (0355)
9	แหวนสปริง M 16 มอก. 259 WASHER, LOCK M 16 TIS 259	-	2	01180301 (0365)
10	นัทรูปห่วง M 16 DIN 582 NUT, EYE M 16 DIN 582	2	2	01180001 (0345)
11	กายทิมเบิ้ลสำหรับสายยึดโยง 50-95 ต.มม. THIMBLE, GUY, FOR STEEL WIRE 50-95 mm^2	2	2	01210304 (0150)
12	ยูแคล้มป์ สลัก 1 ตัว M 8 (ไวร์ โร้ป คลิ๊ป) CLAMP, SINGLE U-BOLT M 8 (WIRE ROPE CLIP)	6	7	01230000 (0165)
13	ลวดเหล็กตีเกลียว 25 ต.มม. มอก. 404 STEEL STRANDED WIRE 25 mm^2 TIS 404	-	2.50 ม. m	01100002 (0181)
14	สเตรนแคล้มป์ สำหรับสายอะลูมิเนียม 35-95 ต.มม. อะลูมิเนียมแกนเหล็ก 35-50 ต.มม. CLAMP, STRAIN FOR Al 35-95 mm^2, ACSR 35-50 mm^2	2	2	03110000 03110001
15	ทลอดต่อสายชนิดบีบไม่รับแรงดึง สายอะลูมิเนียม 35-95 ต.มม อะลูมิเนียมแกนเหล็ก 35-50 ต.มม CONNECTOR, SPLICE, COMPRESSION TYPE, TENSIONLESS Al 35-95 mm^2 ACSR 35-50 mm^2	1	1	02410001 02410004
16	ลูกถ้วยก้านตรง 33 kV มอก. 279 แบบ ค (แบบ 56-3) พร้อมก้าน INSULATOR, PIN TYPE, 33 kV TIS 279 TYPE C (CLASS 56-3) COMP. WITH PIN	1	1	03000001 03100000
17	ลูกถ้วยแขวน มอก. 354 แบบ ง (แบบ 52-4) INSULATOR, SUSPENSION TYPE, TIS 354 TYPE D (CLASS 52-4)	6	6	03020002 (0415)
18	ลวดอะลูมิเนียมแบน ขนาด 1 X 10 มม. ความยาวตามต้องการ TAPE, ARMOUR, Al 1 X 10 mm LENGTH AS REQUIRED			02200000 (0700)
19	ลวดอะลูมิเนียมกลม ขนาด Ø 4 มม. ความยาวตามต้องการ TIE WIRE, Al Ø 4 mm LENGTH AS REQUIRED			02200002 (0704)

หมายเหตุ ในกรณีขาดแคลนทลอดต่อสาย อนุโลมให้ใช้ พี.จี. คอนเนคเตอร์ 2 อันแทนได้

NOTE IN CASE OF LACKING TENSIONLESS SPLICE CONNECTOR, PERMIT TO USE 2 P.G. CONNECTORS.

กองวิศวกรรมไฟฟ้าและเครื่องกล ฝ่ายวิศวกรรม	การไฟฟ้าส่วนภูมิภาค	ใช้แทนแบบ ถูกแทนโดยแบบ
ผู้เขียน ผู้สำรวจ วิศวกร หัวหน้าแผนก หัวหน้ากอง ผู้อำนวยการฝ่าย	ผู้ว่าการ การติดตั้งอุปกรณ์เจ้าปลายสายสองข้างกันเสาคอนกรีต 12 ม. ระบบ 1 เฟส 19 kV	เขียนเสร็จวันที่ 19 มิ.ย. 21 แก้แบบวันที่ มิติเป็น มาตราส่วน
รองผู้ว่าการฝ่ายเทคนิค	21 DOUBLE DEADEND ASSEMBLY ON 12 m CONCRETE POLE 1-PHASE 19 kV SYSTEM	แบบเลขที่ SAI-015/21079 แผ่นที่ 2 ของจำนวน 2 แผ่น