
การประกอบเลขที่
ASSEMBLY NO. 5 2 0 9 A

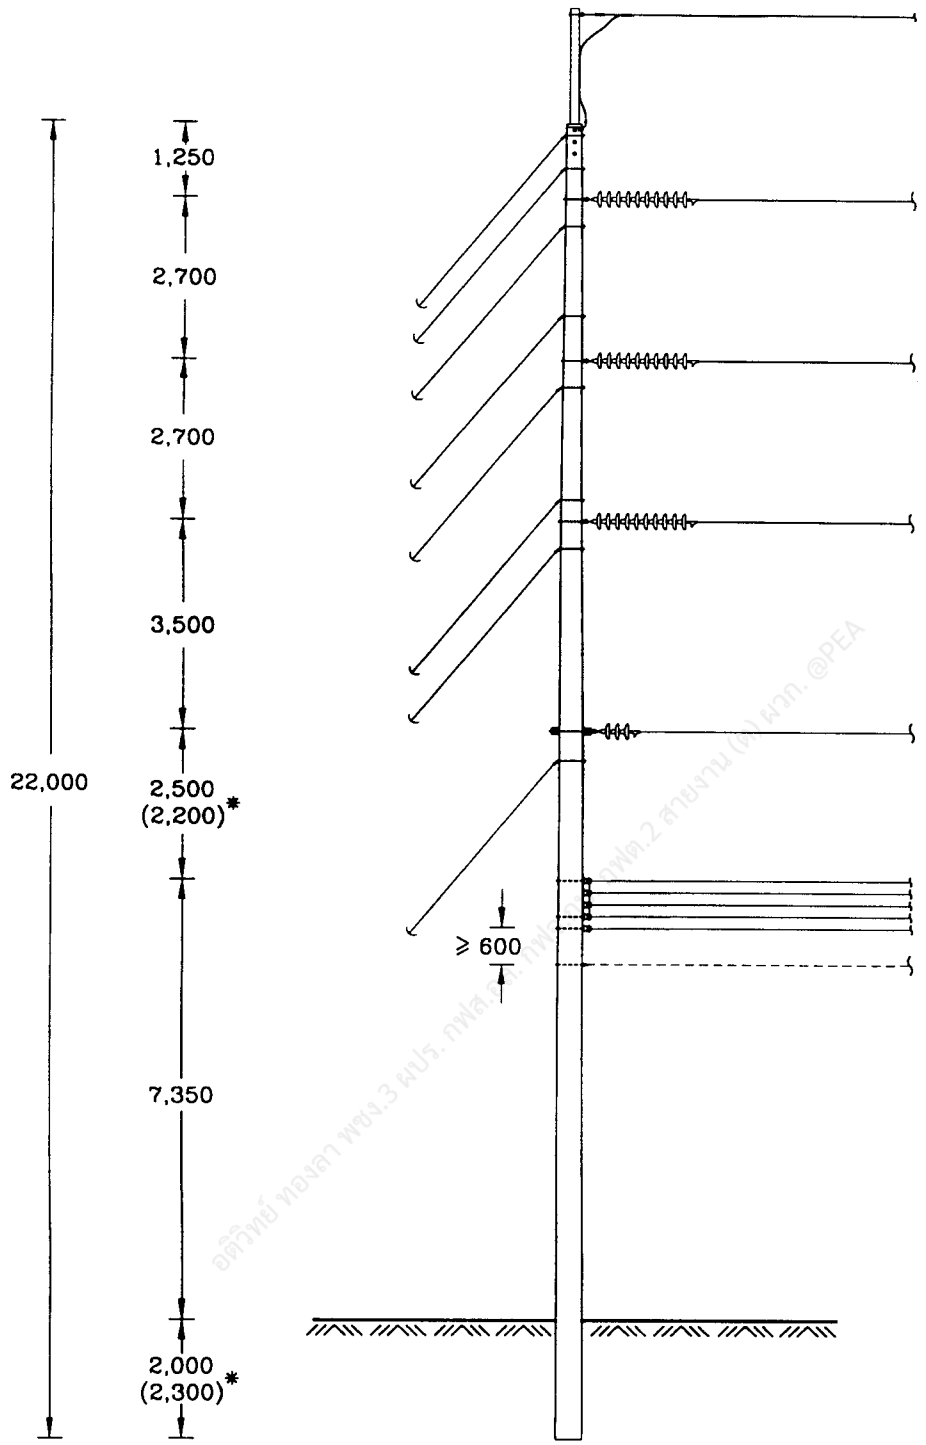


* ดูหมายเหตุ SEE NOTE 1

กองมาตรฐานระบบไฟฟ้า ฝ่ายมาตรฐานและความปลอดภัย	การไฟฟ้าส่วนภูมิภาค	ใช้แทนแบบ ..... ถูกแทนโดยแบบ .....
ผู้เขียน ...สมชาย..... ผู้สำรวจ ..... วิศวกร ..... หัวหน้าแผนก ..... ผู้อำนวยการกอง ..... ผู้อำนวยการฝ่าย	ผู้ว่าการ ..... 115 kV วงจรเดี่ยว สายไฟฟ้าเดี่ยว เสาเดี่ยว (ชนิดมีกราวด์เพลทในเสา) สำหรับเข้าปลายสาย แบบ SS-DE-1	เขียนเสร็จวันที่ 2 มิ.ย. 2547 แก้แบบวันที่ ..... มิติเป็น มิลลิเมตร มาตราส่วน 1:125
รองผู้ว่าการฝ่ายวางแผนและพัฒนาระบบไฟฟ้า	115 kV SINGLE CIRCUIT SINGLE CONDUCTOR SINGLE POLE (WITH GROUND PLATE IN POLE), DEADEND STRUCTURE TYPE SS-DE-1	แบบเลขที่ SA1-015/47006 แผ่นที่ 1 ของจำนวน 3 แผ่น

26 ก.ค. 2547

อดิวิทย์ ทองดา พงง.3 ศปร. กฟส.สามพราน กฟฟ.2 สายงาน (ก) ผวก. @PEA

การประกอบเลขที่ ASSEMBLY NO. 5 2 0 9 A

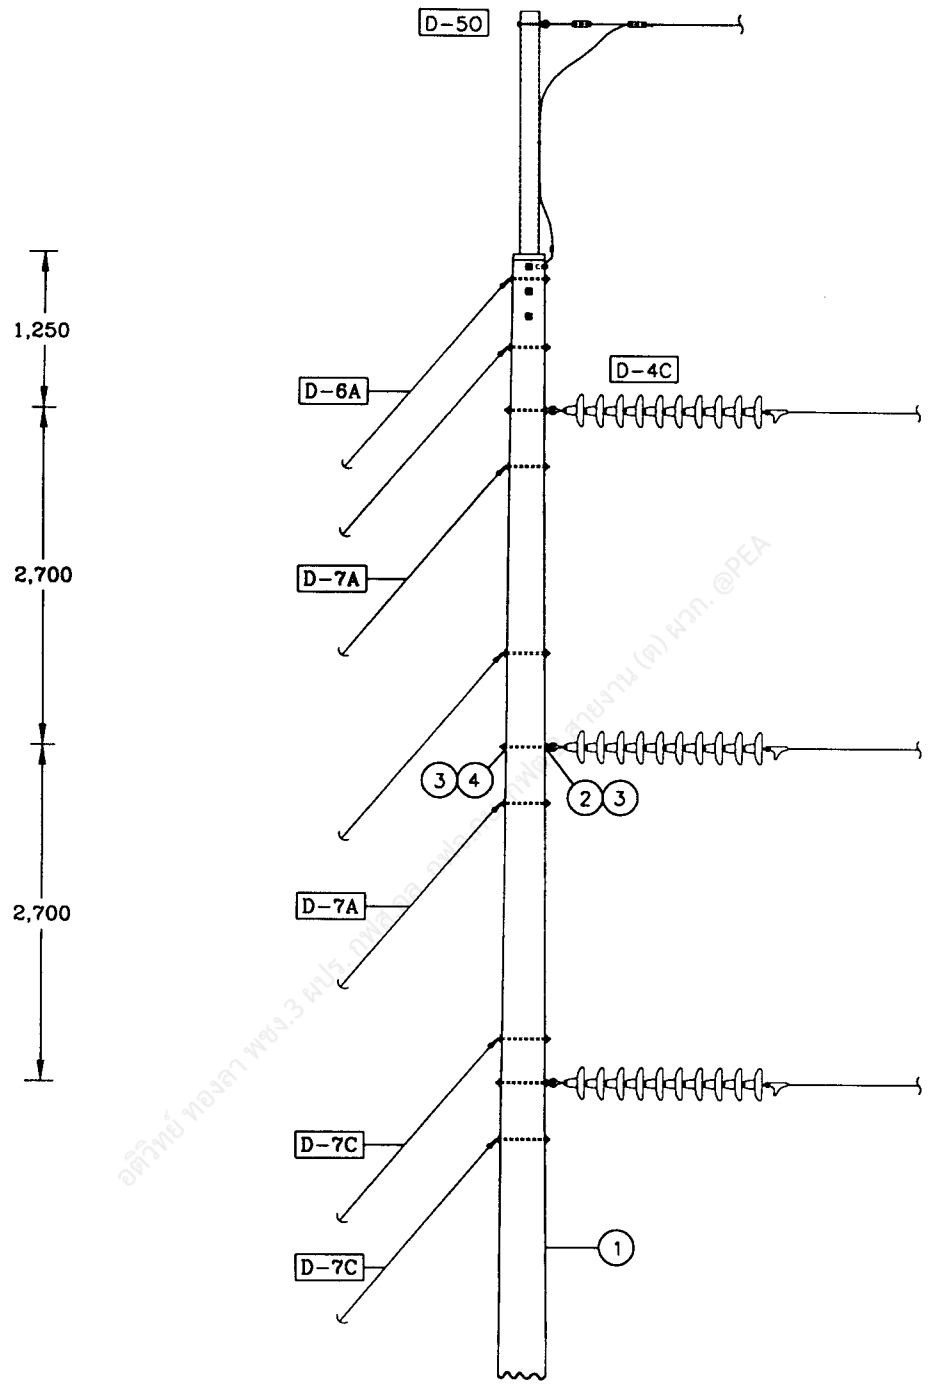

กองมาตรฐานระบบไฟฟ้า ฝ่ายมาตรฐานและความปลอดภัย	การไฟฟ้าส่วนภูมิภาค	ใช้แทนแบบ ..... ถูกแทนโดยแบบ .....
ผู้เขียน ...สมชาย..... ผู้สำรวจ ..... วิศวกร..... หัวหน้าแผนก..... ผู้อำนวยการกอง..... ผู้อำนวยการฝ่าย.....	ผู้ว่าการ.....	เขียนเสร็จวันที่ 2 มิ.ย. 2547 แก้แบบวันที่ ..... มิติเป็น มิลลิเมตร มาตราส่วน 1:60
รองผู้ว่าการฝ่ายวางแผนและพัฒนาระบบไฟฟ้า	115 kV วงจรเดี่ยว สายไฟฟ้าเสา 26 ก.ค. 2547 เสาเดี่ยว (ชนิดมีกราวด์เพลทในเสา) สำหรับเชาปลายสาย แบบ SS-DE-1 115 kV SINGLE CIRCUIT SINGLE CONDUCTOR SINGLE POLE (WITH GROUND PLATE IN POLE), DEADEND STRUCTURE TYPE SS-DE-1	แบบเลขที่ SA1-015/47006 แผ่นที่ 2 ของจำนวน 3 แผ่น

26 ก.ค. 2547

การประกอบเลขที่ ASSEMBLY NO. 5209A

บัญชีวัสดุ
BILL OF MATERIAL

ลำดับที่ ITEM	รายละเอียด DESCRIPTION	จำนวน REQ,D	วัสดุเลขที่ MAT. NO.
1	เสา คอร. ยาว 22.00 ม. ชนิดมีกราวด์เพลทในเสา POLE, CONCRETE, 22.00 m LONG, WITH GROUND PLATE IN POLE	1	00010015
2	สลักห่วงโอแวล M 20x350 มม. BOLT, OVAL EYE, M 20x350 mm	3	01150100
3	แหวนสี่เหลี่ยมแบน 62x62x6 มม. รู ø22 มม. มอก.258 WASHER, SQUARE, FLAT, 62x62x6 mm, HOLE ø22 mm, TIS 258	6	01180101
4	แหวนสปริง M 20 มอก. 259 WASHER, LOCK, M 20, TIS 259	3	01180302

รายละเอียด
DETAIL

D-4C	การประกอบลูกถ้วยแขวน SUSPENSION INSULATOR ASSEMBLY	3	
D-5O	การประกอบสายล่อฟ้า OVERHEAD GROUND WIRE ASSEMBLY	1	
D-6A	การประกอบสายยึดโยงลวดเหล็กดีเกลียว 50 ต.มม. STEEL STRANDED WIRE 50 mm^2 GUY ASSEMBLY	1	
D-7A	การประกอบสายยึดโยงลวดเหล็กดีเกลียว 95 ต.มม. STEEL STRANDED WIRE 95 mm^2 GUY ASSEMBLY	4	
D-7C	การประกอบสายยึดโยงลวดเหล็กดีเกลียว 95 ต.มม. STEEL STRANDED WIRE 95 mm^2 GUY ASSEMBLY	2	
D-9A	สมอบกคอนกรีต CONCRETE ANCHOR	1	
D-10A	ฐานรากเสา POLE FOUNDATION	1	
D-25	การต่อลงดิน GROUNDING	1	

หมายเหตุ

1.* กรณีก่อสร้างในพื้นที่เขตทางหลวง ให้ใช้ค่าในวงเล็บ โดยดูรายละเอียดเพิ่มเติมในแบบเลขที่ SA1-015/43012 (การประกอบเลขที่ 5687)
2. ขนาดของสายสื่อสารโทรคมนาคม ให้ดูแบบเลขที่ SA4-015/42018 (การประกอบเลขที่ 8754)

NOTES

1.* IN CASE OF CONSTRUCTION IN HIGHWAY AREA, USE A VALUE IN THE PARENTHESIS. FOR ADDITIONAL DETAIL, SEE DWG NO. SA1-015/43012 (ASSEMBLY NO. 5687) .
2. SIZE OF THE TELECOMMUNICATION CABLE, SEE DRAWING NO. SA4-015/42018 (ASSEMBLY NO. 8754) .

กองมาตรฐานระบบไฟฟ้า ฝ่ายมาตรฐานและความปลอดภัย	การไฟฟ้าส่วนภูมิภาค	ใช้แทนแบบ ..... ถูกแทนโดยแบบ .....
ผู้เขียน ...สมชาย..... ผู้สำรวจ ..... วิศวกร ..... หัวหน้าแผนก ..... ผู้อำนวยการกอง ..... ผู้อำนวยการฝ่าย	ผู้ว่าการ ..... 26 ก.ค. 2547 115 kV วงจรเดี่ยว สายไฟฟ้าเดี่ยว เสาเดี่ยว (ชนิดมีกราวด์เพลทในเสา) สำหรับเชาปลายสาย แบบ SS-DE-1	เขียนเสร็จวันที่ 2 มิ.ย. 2547 แก้แบบวันที่ ..... มิติเป็น ..... มาตราส่วน .....
รองผู้ว่าการฝ่ายวางแผนและพัฒนาระบบไฟฟ้า	115 kV SINGLE CIRCUIT SINGLE CONDUCTOR SINGLE POLE (WITH GROUND PLATE IN POLE), DEADEND STRUCTURE TYPE SS-DE-1	แบบเลขที่ SA1-015/47006 แผ่นที่ 3 ของจำนวน 3 แผ่น

26 ก.ค. 2547