การประกอบเลขที่ ASSEMBLY NO. 0536

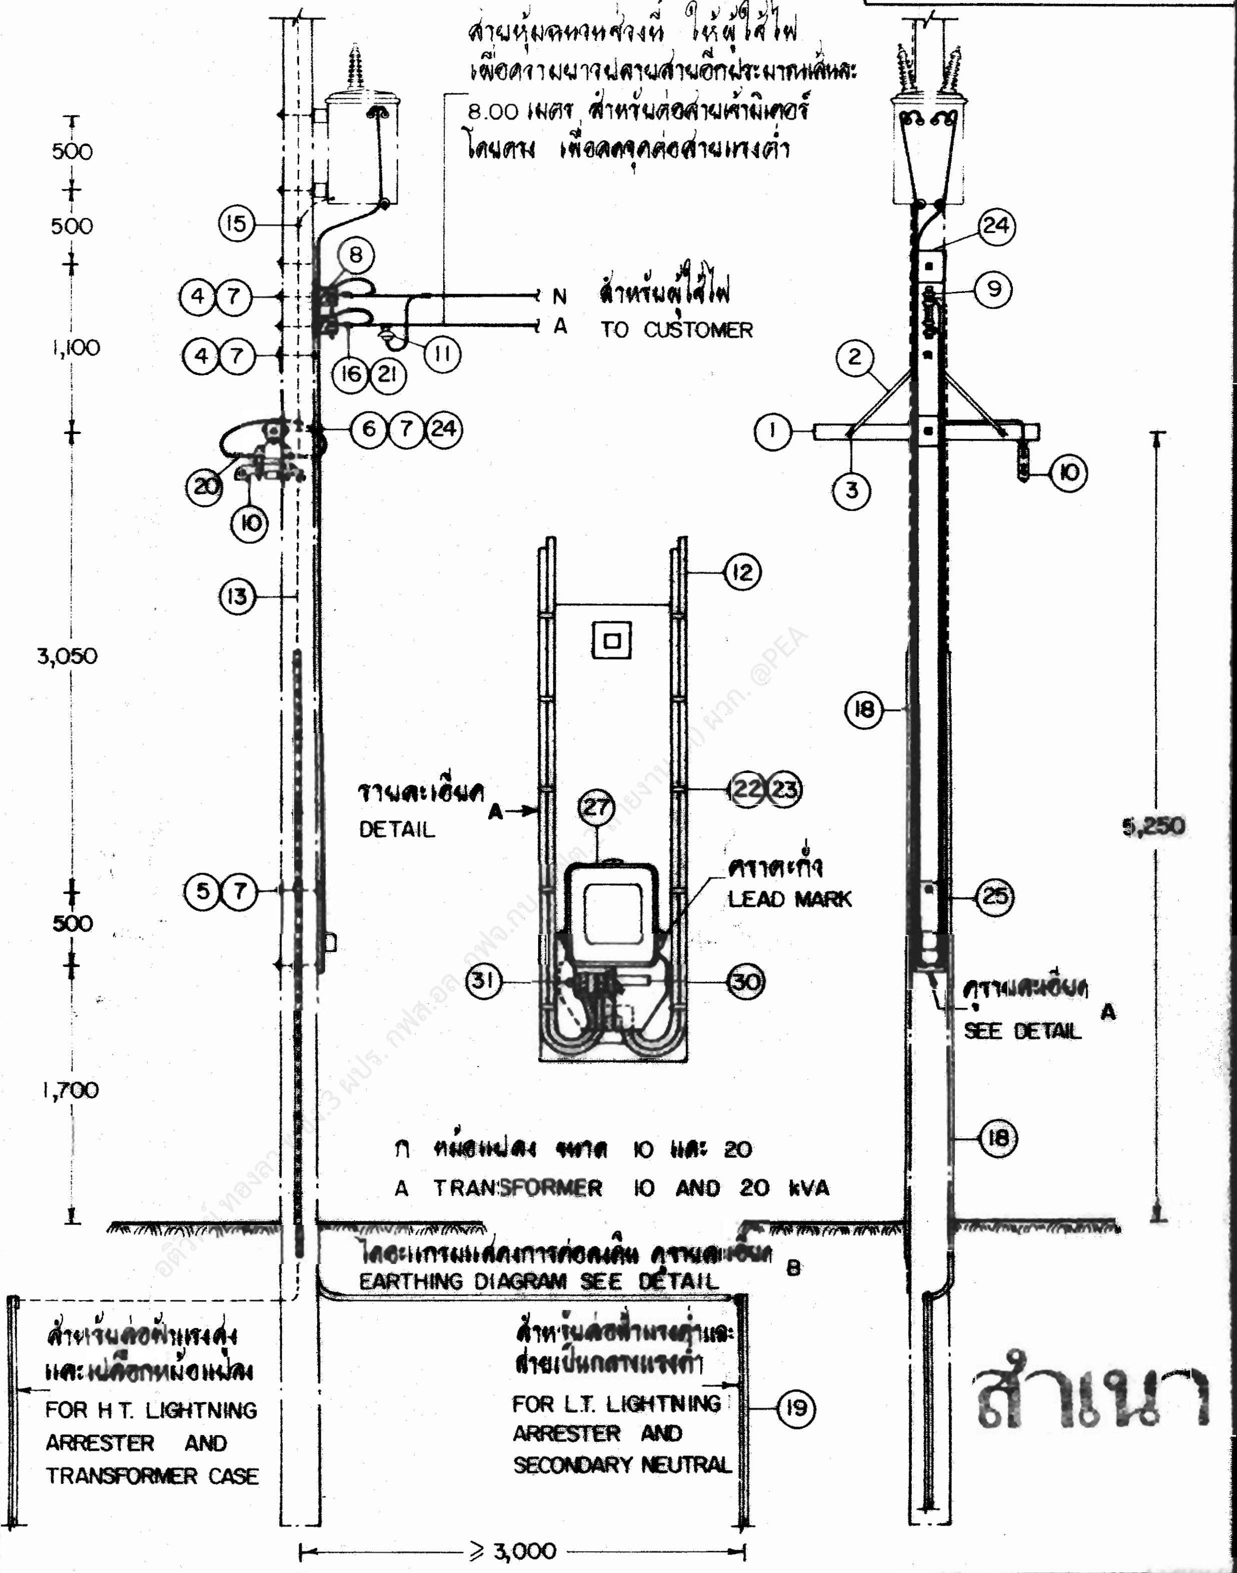
สายหุ้มฉนวนช่วงนี้ ให้ผู้ใช้ไฟเผื่อความยาวปลายสายอีกประมาณเส้นละ 8.00 เมตร สำหรับต่อสายเข้ามิเตอร์โดยตรง เพื่อลดจุดต่อสายแรงต่ำ
500
500
1,100
3,050
500
1,700
5,250
N
A
สำหรับผู้ใช้ไฟ
TO CUSTOMER
15
8
4 7
4 7
11
16 21
6 7 24
20
10
13
5 7
24
9
2
1
3
10
12
22 23
27
18
25
31
30
18
19
รายละเอียด A DETAIL
ตราตะกั่ว LEAD MARK
ดูรายละเอียด A SEE DETAIL
ก หม้อแปลง ขนาด 10 และ 20
A TRANSFORMER 10 AND 20 kVA
ไดอะแกรมแสดงการต่อลงดิน ดูรายละเอียด B
EARTHING DIAGRAM SEE DETAIL B
สำหรับต่อล่อฟ้าแรงสูง และเปลือกหม้อแปลง
FOR H.T. LIGHTNING ARRESTER AND TRANSFORMER CASE
สำหรับต่อล่อฟ้าแรงต่ำและสายเป็นกลางแรงต่ำ
FOR L.T. LIGHTNING ARRESTER AND SECONDARY NEUTRAL
≥ 3,000

สำเนา

กองวิศวกรรมไฟฟ้าและเครื่องกล
ฝ่ายวิศวกรรม

ผู้เขียน
ผู้ลอก
ผู้ตรวจ
หัวหน้าแผนก
ผู้อำนวยการกอง
ผู้อำนวยการฝ่าย

รองผู้ว่าการฝ่ายเทคนิค

การไฟฟ้าส่วนภูมิภาค

ผู้ว่าการ .... 30 ธ.ค. 28

การติดตั้งมิเตอร์แรงต่ำ สำหรับหม้อแปลง 1 เฟส ของผู้ใช้ไฟเฉพาะราย

L.T. kWh-METER INSTALLATION FOR CUSTOMER'S 1-Ø TRANSFORMER

ใช้แทนแบบ ....
ถูกแทนโดยแบบ ....
เขียนเสร็จวันที่ 6 ก.พ. 28
แก้แบบครั้งที่ ....
มิติเป็น มิลลิเมตร
มาตราส่วน 1:50
แบบเลขที่ SAI-015/28004
แผ่นที่ 1 จากจำนวน 6 แผ่น

การประกอบเลขที่
ASSEMBLY NO. 0536

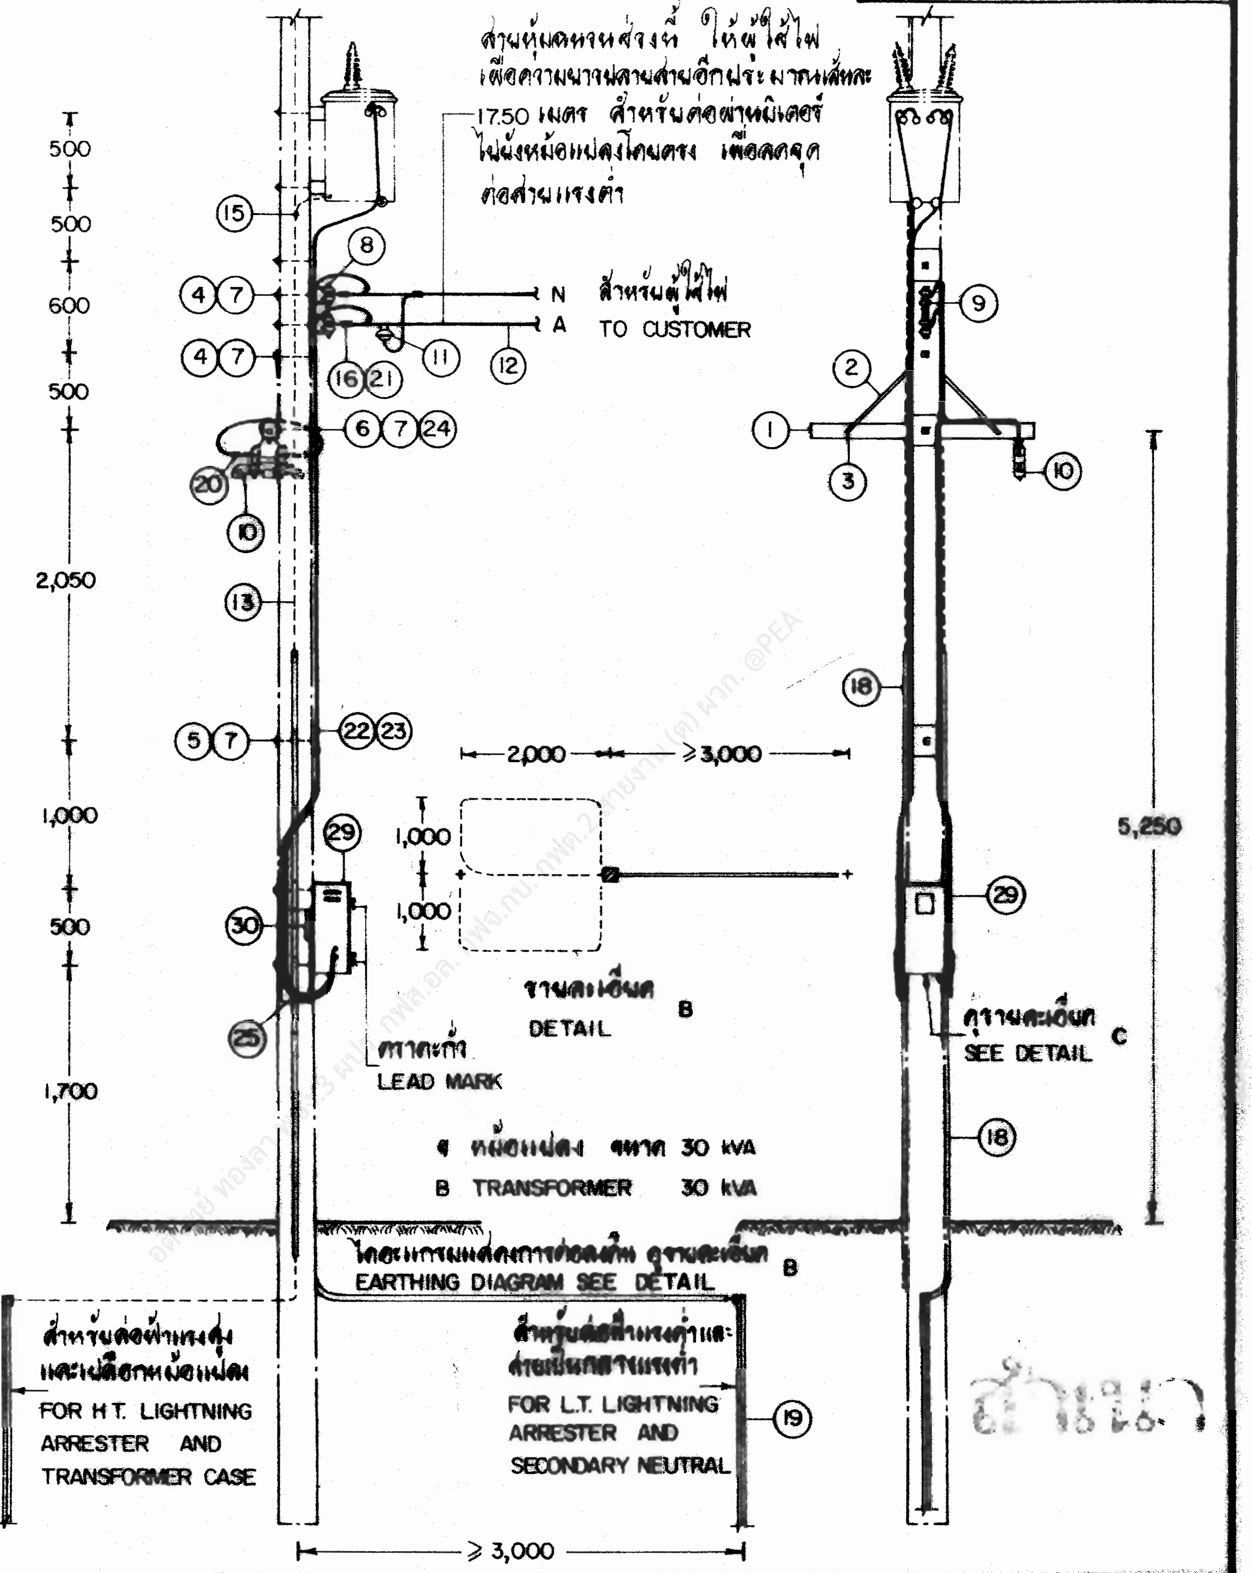

สำเนา

กองวิศวกรรมไฟฟ้าและเครื่องกล
ฝ่ายวิศวกรรม

ผู้เขียน
ผู้ตรวจ
วิศวกร
หัวหน้าแผนก
ผู้อำนวยการกอง
ผู้อำนวยการฝ่าย

รองผู้ว่าการฝ่ายเทคนิค

การไฟฟ้าส่วนภูมิภาค

ผู้ว่าการ .... 30 ส.ค. 28

การติดตั้งมิเตอร์แรงต่ำ
สำหรับหม้อแปลง 1 เฟส ของผู้ใช้ไฟเฉพาะราย

L.T. kWh-METER INSTALLATION
FOR CUSTOMER'S 1-Ø TRANSFORMER

ใช้แทนแบบ ....
ถูกแทนโดยแบบ ....
เขียนเสร็จวันที่ 6 ก.พ. 28
แก้แบบวันที่ ....
มิติเป็น มิลลิเมตร
มาตราส่วน 1:50

แบบเลขที่ SAI-015/28004
แผ่นที่ 2 ของจำนวน 6 แผ่น

การประกอบเลขที่ ASSEMBLY NO. 0536

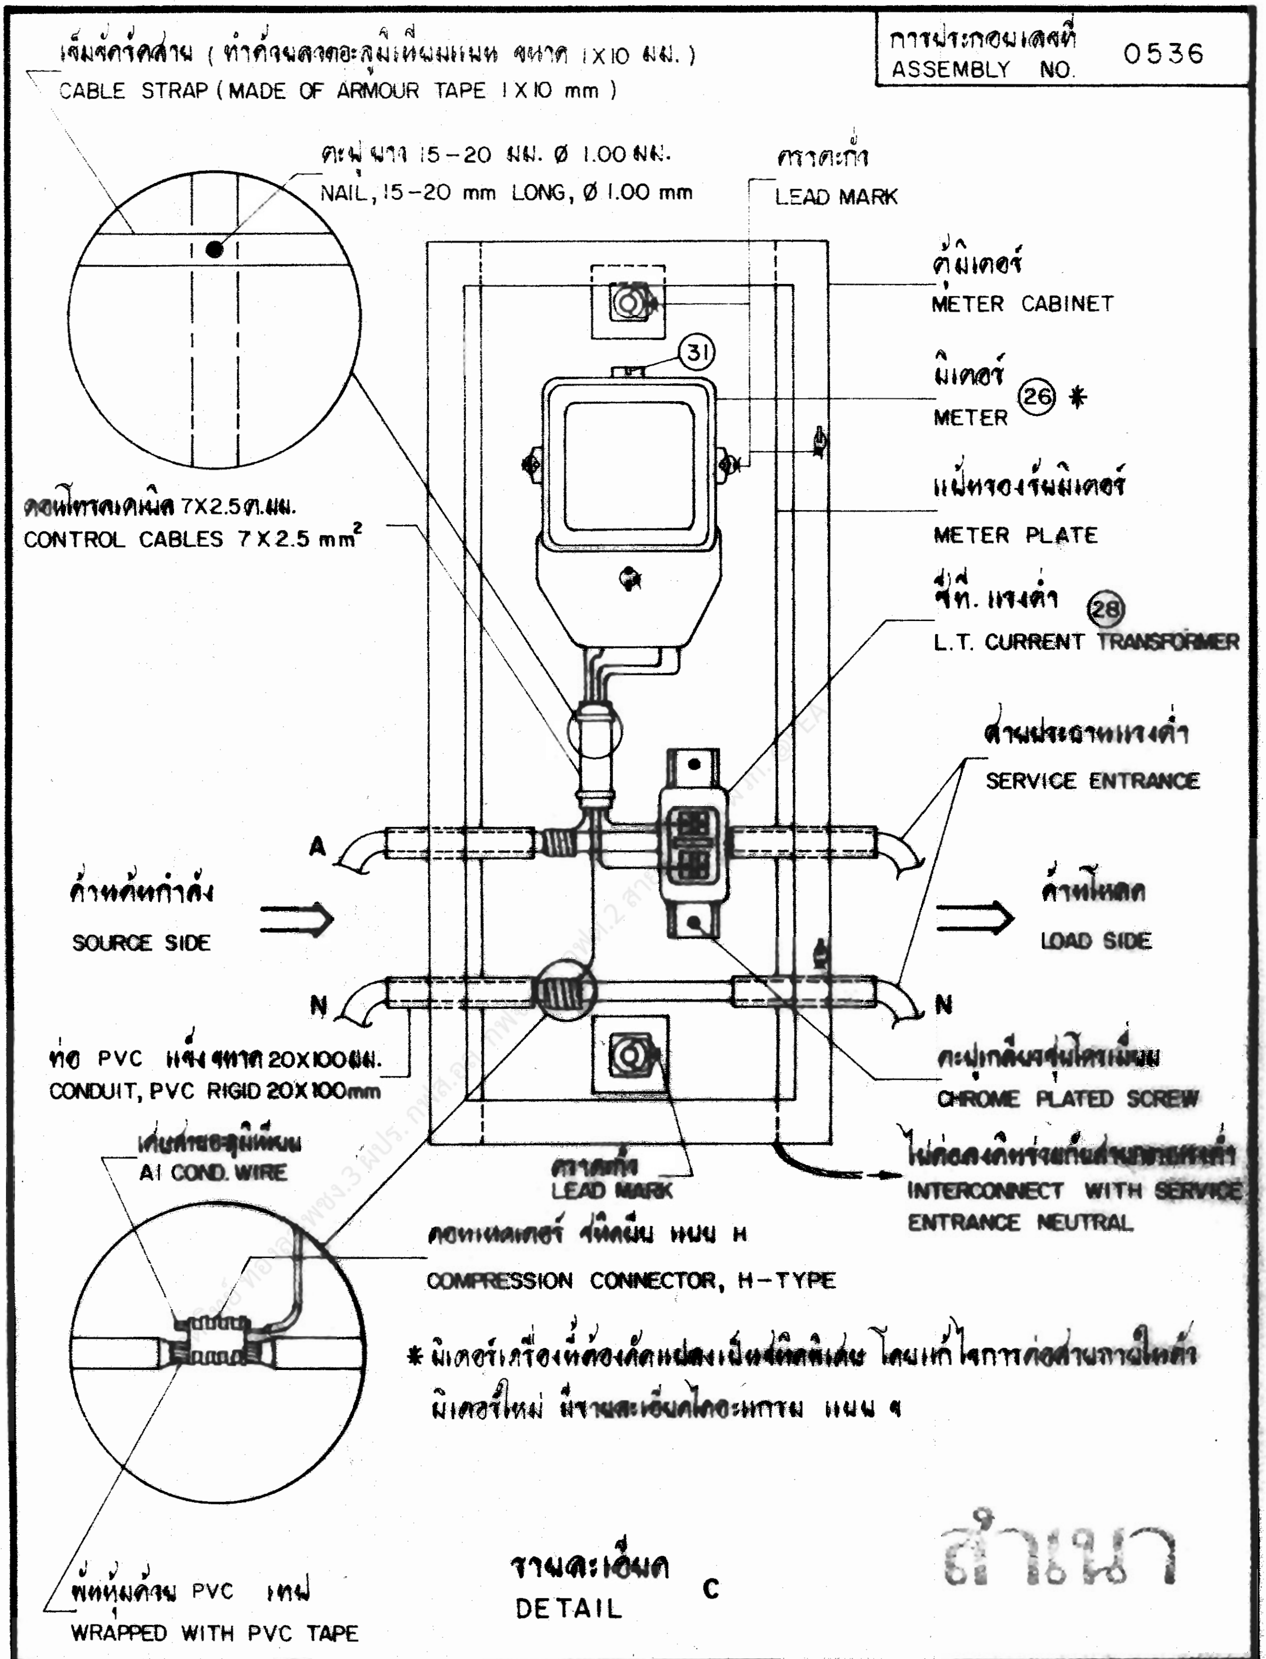

* มิเตอร์เครื่องที่ต้องติดแผงเป็นชนิดพิเศษ โดยแก้ไขการต่อสายภายในตัว มิเตอร์ใหม่ มีรายละเอียดไดอะแกรม แบบ ๆ

สำเนา

กองวิศวกรรมไฟฟ้าและเครื่องกล ฝ่ายวิศวกรรม	**การไฟฟ้าส่วนภูมิภาค**	ใช้แทนแบบ .... ถูกแทนที่โดยแบบ ....
ผู้เขียน .... ผู้สำรวจ .... วิศวกร .... หัวหน้าแผนก .... ผู้อำนวยการกอง .... ผู้อำนวยการฝ่าย	ผู้ว่าการ .... 30 ต.ค. 28	เขียนเสร็จวันที่ 6 ก.ค. 28 แก้แบบวันที่ .... มิติเป็น มิลลิเมตร มาตราส่วน 1:5
	การติดตั้งมิเตอร์แรงต่ำ สำหรับหม้อแปลง 1 เฟส ของผู้ใช้ไฟเฉพาะราย	
รองผู้ว่าการฝ่ายเทคนิค	L.T. kWh-METER INSTALLATION FOR CUSTOMER'S 1-Ø TRANSFORMER	แบบเลขที่ SAI-015/28004 แผ่นที่ 3 ของจำนวน 6 แผ่น

2528

การประกอบเลขที่
ASSEMBLY NO. 0536

ขนาดของมิเตอร์ และสายไฟฟ้าระบบ 230 โวลต์ 1 เฟส 2 สาย ที่ใช้กับหม้อแปลง 1 เฟส ของผู้ใช้ไฟเฉพาะราย

RATINGS OF L.T. kWh-METER AND SIZES OF PVC INSULATED CONDUCTOR, 230 V SYSTEM 1-PHASE 2-WIRE ; FOR 1-PHASE CUSTOMER'S TRANSFORMER

ขนาดของหม้อแปลง (kVA) TRANSFORMER CAPACITY (kVA)	กระแส (แอมป์) CURRENT (AMP)	ขนาดมิเตอร์ (แอมป์) METER RATINGS (AMP)	ขนาดสายไฟหุ้มฉนวน PVC 1 แกน (ต.มม.) SIZE OF SINGLE CORE PVC INSULATED CONDUCTOR (mm²)	
			สายอะลูมิเนียม ALUMINIUM CONDUCTOR	สายทองแดง COPPER CONDUCTOR
10	43.5	30 (60) 15(45)	35	16
20	87	50 (100) 30(100)	50	25
30	130.4	5(15) ร่วมกับ C.T. 150/5 5(15)	95	50

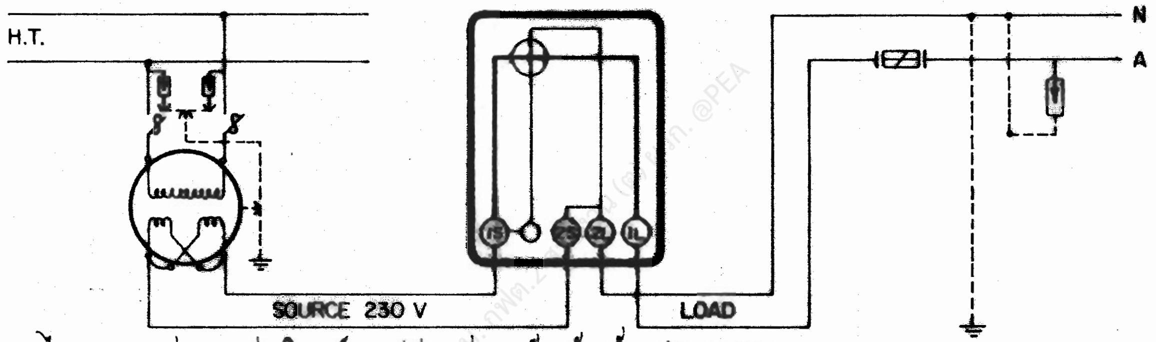

ก ไดอะแกรมแสดงการต่อมิเตอร์ 1 เฟส 2 สาย สำหรับหม้อแปลง ขนาด 10 และ 20 kVA
A CONNECTION DIAGRAM OF THE 1-PHASE 2-WIRE kWh-METER FOR 10 AND 20 kVA TRANSFORMERS

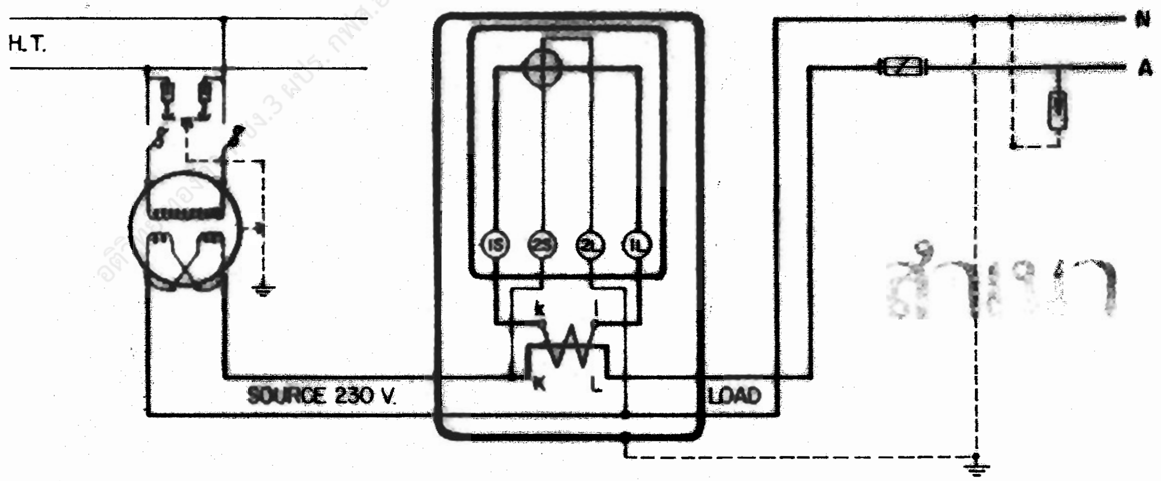

สำเนา

ข ไดอะแกรมแสดงการต่อมิเตอร์ 1 เฟส 2 สาย พร้อม ซี.ที. แรงต่ำ สำหรับหม้อแปลง ขนาด 30 kVA
B CONNECTION DIAGRAM OF THE 1-PHASE 2-WIRE kWh-METER FOR 30 kVA TRANSFORMER

กองวิศวกรรมไฟฟ้าและเครื่องกล
ฝ่ายวิศวกรรม

ผู้เขียน
ผู้ตรวจ
วิศวกร
หัวหน้าแผนก
ผู้อำนวยการกอง
ผู้อำนวยการฝ่าย
รองผู้ว่าการฝ่ายเทคนิค

การไฟฟ้าส่วนภูมิภาค

ผู้ว่าการ 30 ธ.ค. 28

การติดตั้งมิเตอร์แรงต่ำ
สำหรับหม้อแปลง 1 เฟส ของผู้ใช้ไฟเฉพาะราย

L.T. kWh-METER INSTALLATION
FOR CUSTOMER'S 1-Ø TRANSFORMER

ใช้แทนแบบ
ถูกแทนโดยแบบ
เขียนเสร็จวันที่ 6 ก.พ. 28
แก้แบบวันที่ 8 ก.ค. 31
มิติเป็น
มาตราส่วน

แบบเลขที่ SAI-015/28004
แผ่นที่ 4 จากจำนวน 6 แผ่น

การประกอบเลขที่ ASSEMBLY NO.	0536

บัญชีพัสดุ
BILL OF MATERIAL

ลำดับที่ ITEM	รายละเอียด DESCRIPTION	จำนวน REQ'D ก/A	 ข/B	รหัสเลขที่ MAT.NO.
1	คอน คอร. ขนาด 100 X 100 X 1,500 มม. CROSSARM, PRESTRESSED, CONCRETE 100 X 100 X 1,500 mm	1	1	00110000
2	เหล็กประกับคอน ขนาด 30 X 6 X 760 มม. BRACE, FLAT, FOR CROSSARM 30 X 6 X 760 mm	2	2	01200001
3	สลักเกลียว M 16 X 130 มม. BOLT, MACHINE, M 16 X 130 mm	2	2	01110200
4	สลักเกลียว M 16 X 250 มม. BOLT, MACHINE, M 16 X 250 mm	4	4	01110203
5	สลักเกลียว M 16 X 300 มม. BOLT, MACHINE, M 16 X 300 mm	2	3	01110204
6	สลักเกลียว M 16 X 350 มม. BOLT, MACHINE, M 16 X 350 mm	1	2	01110205
7	แหวนสี่เหลี่ยมแบน 52 X 52 X 4.5 มม. รู Ø 18 มม. มอก. 285 WASHER, SQUARE, FLAT 52 X 52 X 4.5 mm HOLE Ø 18 mm TIS 285	13	18	01180100
8	แร็ค 2 X 200 มม. (2 X 8") แบบหลังเผิน RACK, SECONDARY, MEDIUM PRESSED STEEL 2 X 200 mm (2 X 8") EXT. BACK	1	1	03130000
9	ลูกถ้วยแรงต่ำ มอก. 227 แบบ ข (แบบ 53-2) INSULATOR, SPOOL TYPE L.T. TIS 227 TYPE B (CLASS 53-2)	2	2	03030000
10	ฟิวส์สวิตช์แรงต่ำ 1 X 400 แอมป์ 500 โวลต์ L.T. FUSE SWITCHES 1 X 400 A 500 V	1	1	04020100
11	ล่อฟ้า 250 - 500 โวลต์ 2.5 - 5.0 กิโลแอมป์ LIGHTNING ARRESTER 250-500 V 2.5-5.0 kA	1	1	04000300
12	สายอะลูมิเนียมหุ้มฉนวน PVC มอก. 293 ขนาด และความยาวตามต้องการ CABLE, Al STRAND, PVC - INSULATED, TIS 293 SIZE AND LENGTH AS REQUIRED	ม. m	ม. m	02070001-4
13	ลวดเหล็กตีเกลียว 50/7 ต.มม. มอก. 404 WIRE, STEEL STRANDED 50/7 mm², TIS 404	ม. m	ม. m	01100004
14	ลวดอะลูมิเนียมกลม 4 มม. ความยาวตามต้องการ TIE WIRE, Al 4 mm LENGTH AS REQUIRED			02200002
15	ยูแคล้มป์ สลัก 1 ตัว M 8 (ไวร์ โรป คลิป) CLAMP, SINGLE U-BOLT M 8 (WIRE ROPE CLIP)	1	2	01230000
16	คอนเนคเตอร์ เข้าปลายสาย ขนาดตามต้องการ CONNECTOR, DEADEND, SIZE AS REQUIRED	2	2	02310000-2
17	คอนเนคเตอร์ อัดแน่น แบบ H สำหรับสายอะลูมิเนียม ขนาดตามต้องการ CONNECTOR, COMPRESSION, H-TYPE, FOR Al CONDUCTOR SIZE AS REQUIRED	1	3	02210000-2
18	ท่อ PVC แข็ง ขนาด 20X4,000 มม. พร้อมอุปกรณ์ยึด ตามแบบเลขที่ S02-015/19128 CONDUIT, PVC RIGID 20X4,000 mm COMP. WITH FIXING ACCESS. DWG. NO. S02-015/19128	3	3	08040002
19	หลักดิน 60 X 60 X 5 มม. ยาว 2 ม. ROD, GROUND 60 X 60 X 5 mm 2 m LONG	2	2	01220002
20	หางปลาเจาะรูตามมาตรฐาน NEMA สำหรับสายอะลูมิเนียม ขนาดตามต้องการ CABLE LUG, NEMA HOLE, COMPRESSION TYPE, Al SIZE AS REQUIRED	2	2	02420101-4

กองวิศวกรรมไฟฟ้าและเครื่องกล
ฝ่ายวิศวกรรม

ผู้เขียน
ผู้สำรวจ
วิศวกร
หัวหน้าแผนก
ผู้อำนวยการกอง
ผู้อำนวยการฝ่าย

รองผู้ว่าการฝ่ายเทคนิค

การไฟฟ้าส่วนภูมิภาค

ผู้ว่าการ 30 ส.ค. 28

การติดตั้งมิเตอร์แรงต่ำ
สำหรับหม้อแปลง 1 เฟส ของผู้ใช้ไฟเฉพาะราย

L.T. kWh-METER INSTALLATION
FOR CUSTOMER'S 1-Ø TRANSFORMER

ใช้แทนแบบ
ถูกแทนโดยแบบ
เขียนเสร็จวันที่ 6 ก.พ. 28
แก้แบบวันที่
มิติเป็น
มาตราส่วน

แบบเลขที่ SAI-015/28004
แผ่นที่ 5 จำนวน 6 แผ่น

การประกอบเลขที่ ASSEMBLY NO. 0536

บัญชีวัสดุ
BILL OF MATERIAL

ลำดับที่ ITEM	รายละเอียด DESCRIPTION	จำนวน REQ'D ก/A	ข/B	รหัสพัสดุ MAT.NO.
21	PVC เทป กว้าง 19 มม. (ใช้ความยาว 2 ม. ต่อ 1 จุด) มอก. 386 PVC TAPE, 19 mm WIDE (2 m LONG PER POINT) TIS 386			02180001 or 02180002
22	ตะปูหัวกลมแบน ยาว 20 มม. Ø 1.00 มม. มอก. 113 NAIL, ROUND MILD STEEL WIRE, 20 mm LONG, Ø 1.00 mm TIS 113	12	16	—
23	เข็มขัดรัดสาย (ทำด้วยแถบอะลูมิเนียมแบน 1 X 10 มม.) CABLE STRAP (MADE OF ARMOUR TAPE 1 X 10 mm)			02200000
24	แผ่นไม้รองรับมิเตอร์ ขนาด 20 X 20 X 2 ซ.ม. METER PLATE, SIZE 20 X 20 X 2 Cm.	2	3	—
25	แผ่นไม้รองรับมิเตอร์ ขนาด 20 X 60 X 2 ซ.ม. METER PLATE, SIZE 20 X 60 X 2 Cm	1	3	—
26	วัตต์อาวร์มิเตอร์ 1 เฟส 2 สาย 220 โวลต์ ขนาด 5 แอมป์ (ตัวแปลงเป็นชนิดพิเศษ) METER, WATTHOUR, SINGLE-PHASE, 2-WIRES, 220 V, RATING 5 A (SPECIAL TYPE)	–	1	06000001
27	วัตต์อาวร์มิเตอร์ 1 เฟส 2 สาย 220 โวลต์ ขนาด 30 – 50 แอมป์ METER, WATTHOUR, SINGLE-PHASE, 2-WIRES, 220 V, RATING 30 – 50 A	1	–	06000005 or 06000007
28	ซี.ที. แรงต่ำ ใช้นอกอาคาร 500 โวลต์ เรโช 150/5 แอมป์ CT. L.T. OUT-DOOR, 500 V RATIO 150/5 A	–	1	06040009
29	ตู้อะลูมิเนียมใช้นอกอาคาร สำหรับดีมานด์มิเตอร์ OUT-DOOR ALUMINIUM CABINET FOR 3-PHASE DEMAND METER	–	1	06100007
30	หมายเลขผู้ใช้ไฟ NUMBER OF CUSTOMER	1	1	
31	ตะปูเกลียวชุบโครเมี่ยม ขนาด 15–20 มม. SCREW, CHROME PLATED, SIZE 15–20 mm	3	5	—

สำเนา

	แบบอ้างอิง REFERENCE DRAWING	แบบเลขที่ DWG. NO.	การประกอบเลขที่ ASSEMBLY NO.
1	การต่อลงดินระบบแรงสูง และแรงต่ำ แผ่นที่ 9 H.T. AND L.T. EARTHING SYSTEM, SHEET NO. 9	S02-015/20039	9701
2	ขนาดของ HRC ฟิวส์แรงต่ำ แผ่นที่ 2 RATING OF L.T. HRC FUSE, SHEET NO. 2	S01-015/18006	0602
3	การต่อสายแรงต่ำ ออกจากหม้อแปลง SECONDARY LEAD FROM TRANSFORMER	SAI-015/22011	0603
4	การติดตั้งหม้อแปลง TRANSFORMER INSTALLATION	S02-015/20065 S02-015/20075	2701 3701
5	การเข้าปลายสายหุ้มฉนวนแรงต่ำ L.T. INSULATED CONDUCTOR DEADENDING	SAI-015/22015 SAI-015/22016	9528 9529

กองวิศวกรรมไฟฟ้าและเครื่องกล
ฝ่ายวิศวกรรม

ผู้เขียน
ผู้ตรวจ
วิศวกร
หัวหน้าแผนก
ผู้อำนวยการกอง
ผู้อำนวยการฝ่าย

รองผู้ว่าการฝ่ายเทคนิค

การไฟฟ้าส่วนภูมิภาค

ผู้ว่าการ 30 ส.ค. 28

การติดตั้งมิเตอร์แรงต่ำ
สำหรับหม้อแปลง 1 เฟส ของผู้ใช้ไฟเฉพาะราย

L.T. kWh-METER INSTALLATION
FOR CUSTOMER'S 1-Ø TRANSFORMER

ใช้แทนแบบ
ถูกแทนโดยแบบ
เขียนเสร็จวันที่ 6 ก.พ. 28
แก้แบบวันที่
มิติเป็น
มาตราส่วน

แบบเลขที่ SAI-015/28004
แผ่นที่ 6 ของจำนวน 6 แผ่น

7 [illegible] 2528