การประกอบเลขที่ ASSEMBLY NO. 5687 K

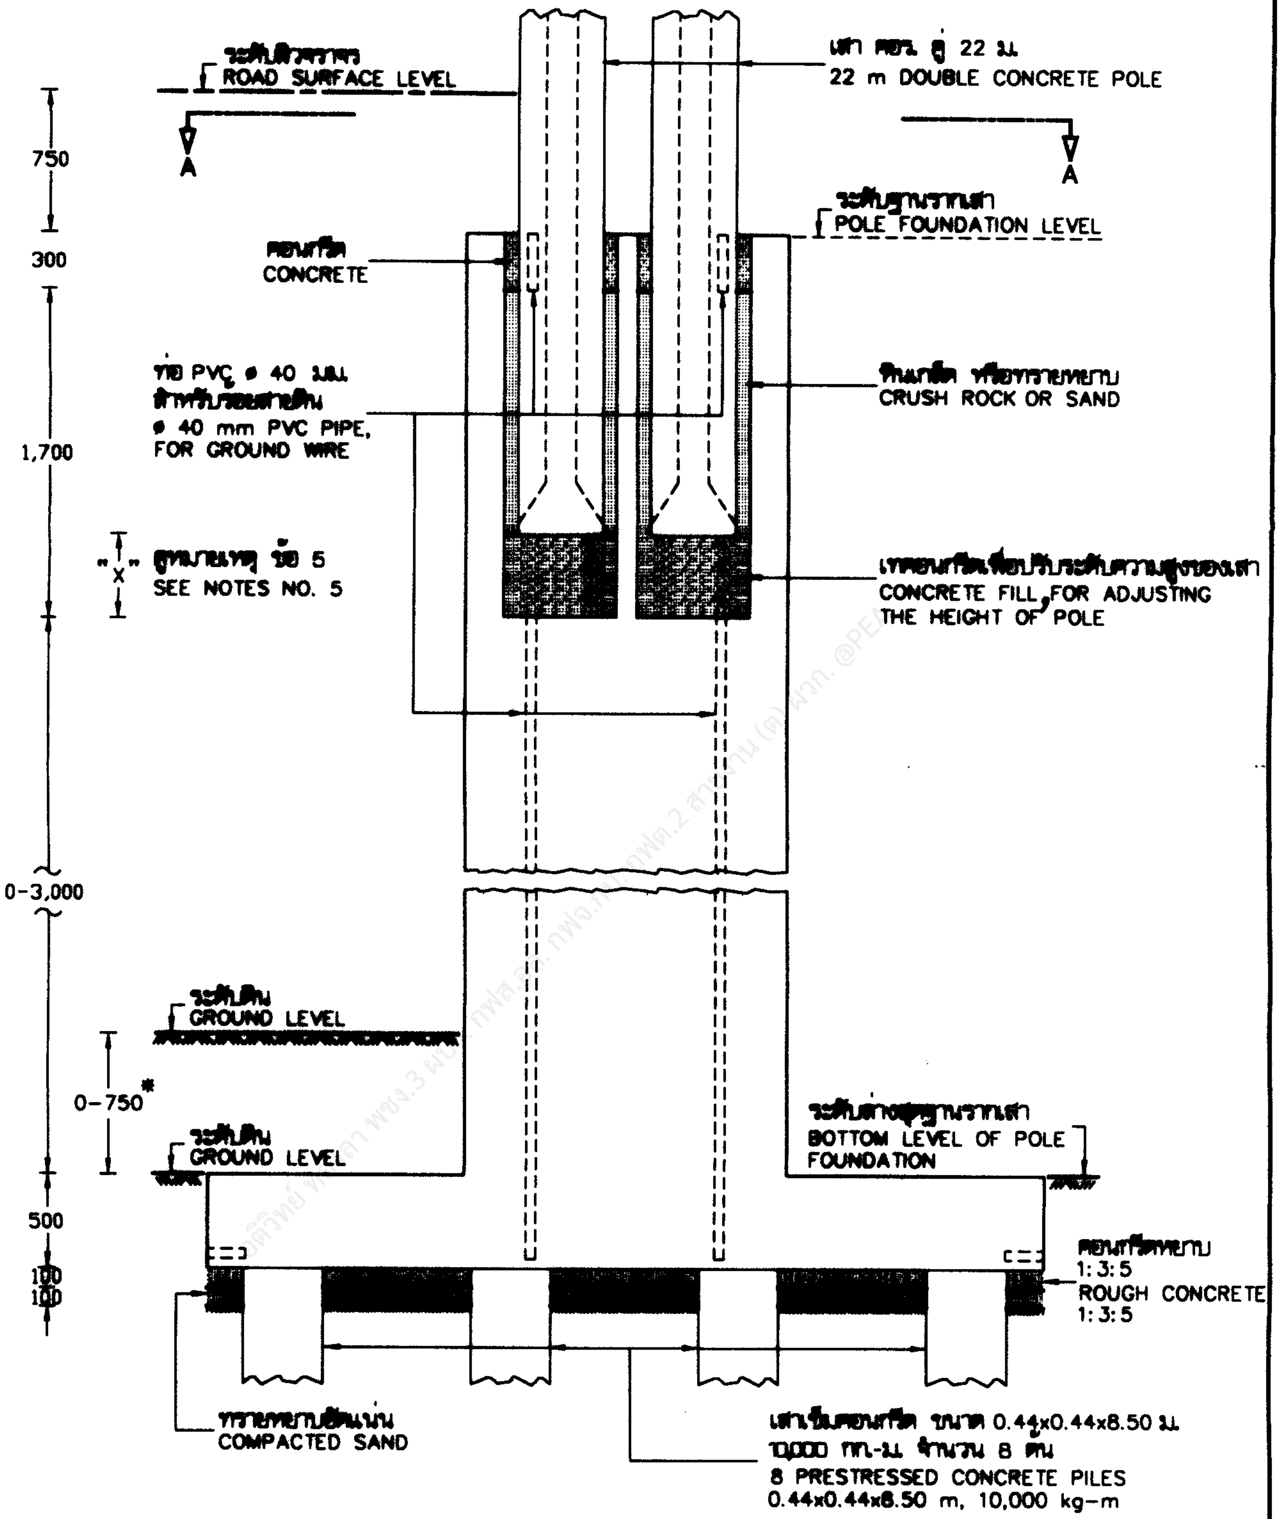

กองมาตรฐานระบบไฟฟ้า
ฝ่ายมาตรฐานและความปลอดภัย

ผู้เขียน ..สมชาย..........
ผู้ตรวจ..........
วิศวกร..........
หัวหน้าแผนก..........
ผู้อำนวยการกอง..........
ผู้อำนวยการฝ่าย..........

รองผู้ว่าการวางแผนและพัฒนาระบบไฟฟ้า

การไฟฟ้าส่วนภูมิภาค

ผู้ว่าการ..........

รายละเอียดที่ 10 B 3 ก.ย. 2547
ฐานรากเสา (แบบที่ 12)

DETAIL 10 B
POLE FOUNDATION (TYPE 12)

ใช้แทนแบบ SA1-015/45020
ถูกแทนโดยแบบ..........
เขียนเสร็จวันที่ .10 .พ.ค. 2547.
แก้แบบวันที่..........
มิติเป็น .มิลลิเมตร..........
มาตราส่วน....1:40..........
แบบเลขที่.SA1-015/47028
แผ่นที่ .1. ของจำนวน .2. แผ่น

12 3 ก.ย. 2547

การประกอบเลขที่
ASSEMBLY NO. 5687 K

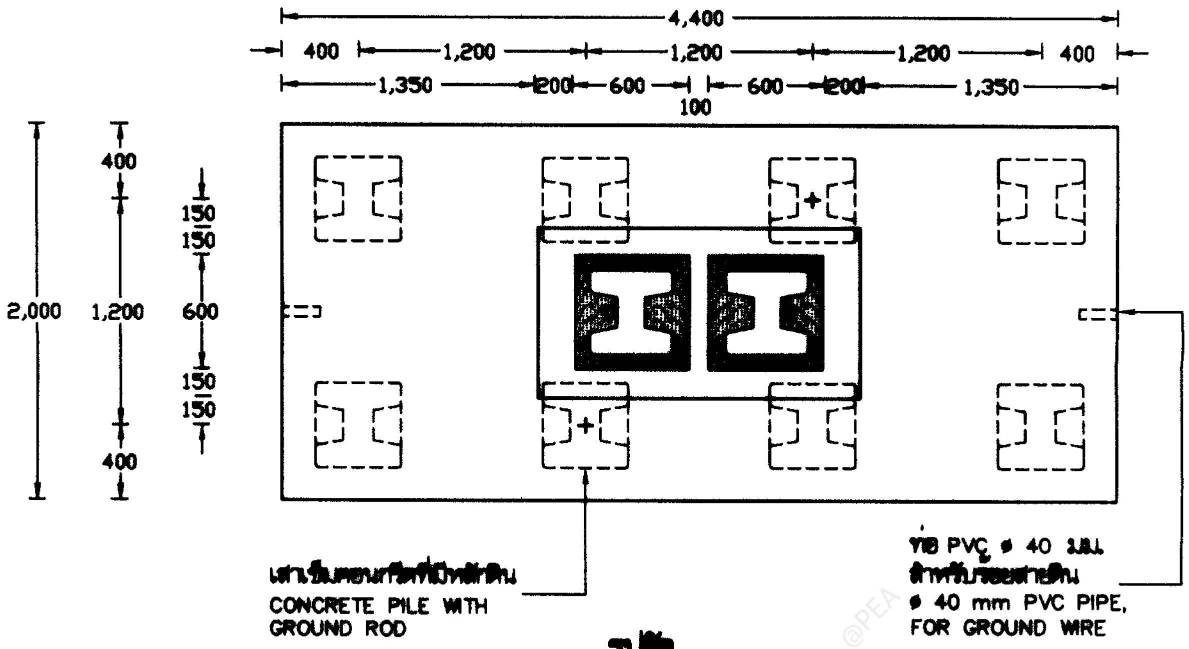

รูปตัด SECTION A-A

หมายเหตุ

1 ใช้ในการมีทางตรงหรือทางโค้ง ที่มีและไม่มีสายยึดโยง (กรณีพื้นที่ก่อสร้างฐานรากเสามีระดับต่ำกว่าระดับผิวจราจร 2.00-5.75 ม.)
2 ดูรายละเอียดเพิ่มเติมใน แบบเลขที่ IB2-011/44021
3 ดูข้อกำหนดการติดตั้งฐานรากเสาในเขตทางหลวง ตามแบบเลขที่ SA1-015/43012 (การประกอบเลขที่ 5687)
4* กรณีพื้นที่ก่อสร้างฐานรากเสามีระดับต่ำกว่าระดับผิวจราจร ระหว่าง 2.00-2.75 ม. ให้ก่อสร้างฐานรากเสาต่ำกว่าระดับดิน ระหว่าง 0.75-0.00 ม. (ระดับล่างสุดฐานรากเสาจะต่ำกว่าระดับผิวจราจร 2.75 ม.)
5 ระยะ "X"= 450 มม. สำหรับการก่อสร้างฐานรากเสาในพื้นที่ทางหลวงที่ไม่มีทางเท้า ส่วนพื้นที่อื่นๆ ระยะ "X"= 0 มม.

NOTES

1 USE FOR STRAIGHT OR ANGLE LINE WITH AND WITHOUT GUY (IN CASE OF GROUND SURFACE IS 2.00–5.75 m LOWER THAN ROAD SURFACE) .
2 SEE ADDITIONAL DETAIL, DWG. NO. IB2-011/44021 .
3 SEE RECOMMENDATION,FOR POLE FOUNDATION INSTALLATION IN HIGHWAY AREA, DWG. NO. SA1-015/43012 (ASSEMBLY NO. 5687) .
4* IN CASE OF GROUND SURFACE LEVEL IS BETWEEN 2.00–2.75 m LOWER THAN ROAD SURFACE LEVEL CONSTRUCTED FOUNDATION SHALL BE BETWEEN 0.75–0.00 m LOWER THAN GROUND SURFACE LEVEL (BOTTOM LEVEL OF POLE FOUNDATION IS 2.75 m. LOWER THAN ROAD SURFACE LEVEL) .
5 THE "X" IS 450 mm HEIGHT FOR FOUNDATION CONSTRUCTION IN HIGHWAY AREA WHICH HAVE NO PAVEMENT, OTHER AREA THE "X" IS ZERO .

กองมาตรฐานระบบไฟฟ้า
ฝ่ายมาตรฐานและความปลอดภัย
ผู้เขียน ..สมชาย..........
ผู้ตรวจ..........
วิศวกร..........
หัวหน้าแผนก..........
ผู้อำนวยการกอง..........
ผู้อำนวยการฝ่าย..........
รองผู้ว่าการวางแผนและพัฒนาระบบไฟฟ้า

การไฟฟ้าส่วนภูมิภาค

ผู้ว่าการ..........

รายละเอียดที่ 10 23 ก.ย. 2547
ฐานรากเสา (แบบที่ 12)

DETAIL 10 B
POLE FOUNDATION (TYPE 12)

ใช้แทนแบบ SA1-015/45020
ถูกแทนโดยแบบ..........
เขียนเสร็จวันที่ .10. มิ.ย. 2547
แก้แบบวันที่..........
มิติเป็น ..มิลลิเมตร..........
มาตราส่วน....1:40..........
แบบเลขที่ SA1-015/47028
แผ่นที่ .2. ของจำนวน .2. แผ่น

23 ก.ย. 2547