การประกอบการเลขที่ ASSEMBLY NO.	5431

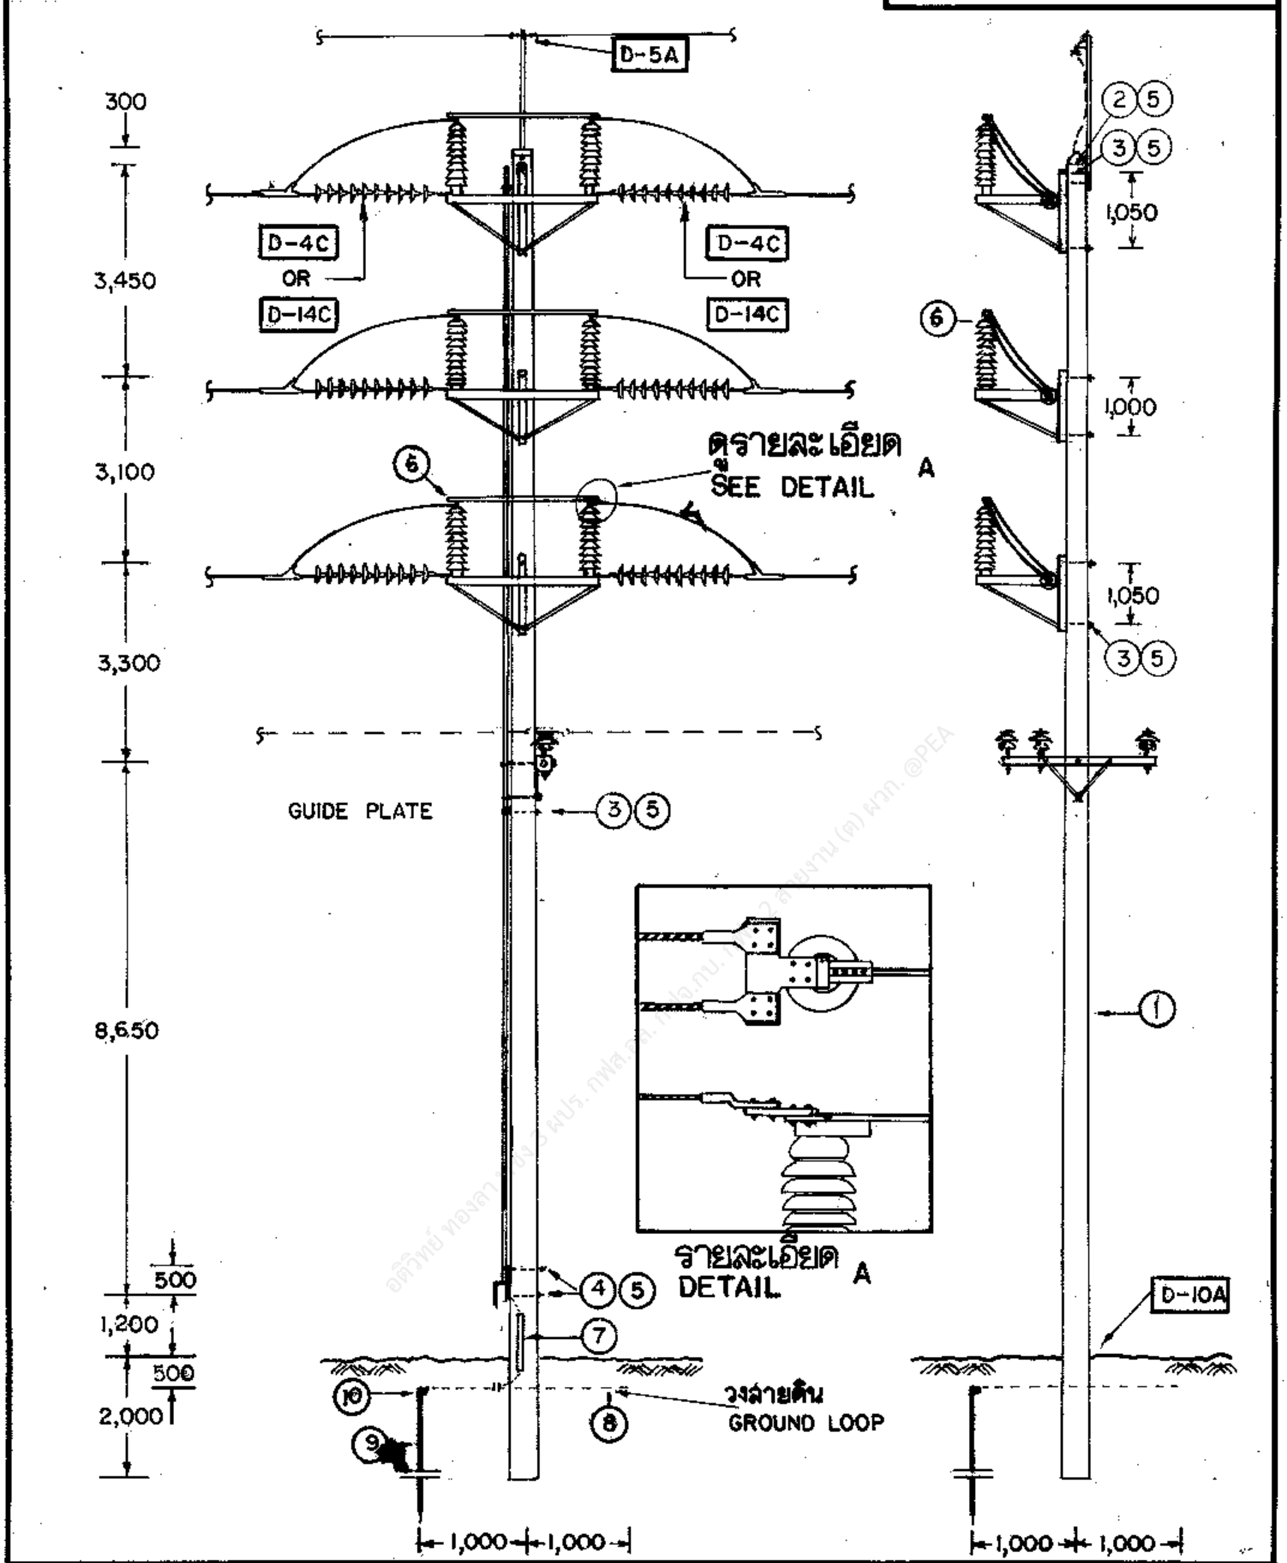

กองวิศวกรรมไฟฟ้าและเครื่องกล ฝ่ายวิศวกรรม	**การไฟฟ้าส่วนภูมิภาค**	ใช้แทนแบบ
ผู้เขียน ผู้สำรวจ วิศวกร หัวหน้าแผนก ผู้อำนวยการกอง ผู้อำนวยการฝ่าย	ผู้ว่าการ 31 มี.ค.2528	ถูกแทนโดยแบบ เขียนเสร็จวันที่ 20 มค.2538
	115 kV วงจรเดี่ยว สายไฟฟ้าคู่ การติดตั้งสวิตช์ตัดตอนสามขา (แอร์เบรคสวิตช์) แบบ SD-SW-2	แก้แบบวันที่ มิติเป็น มิลลิเมตร มาตราส่วน 1:125
รองผู้ว่าการฝ่ายเทคนิค	115 kV SINGLE CIRCUIT DOUBLE CONDUCTOR TRIPLE POLE AIR BREAK SWITCH INSTALLATION TYPE SD-SW-2	แบบเลขที่ SAI-015/38002 แผ่นที่ 1 ของจำนวน 2 แผ่น

29 มี.ค. 2538

การประกอบการเลขที่
ASSEMBLY NO. **5431**

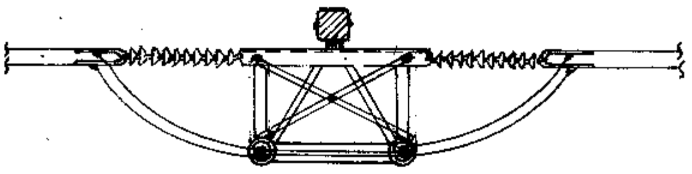

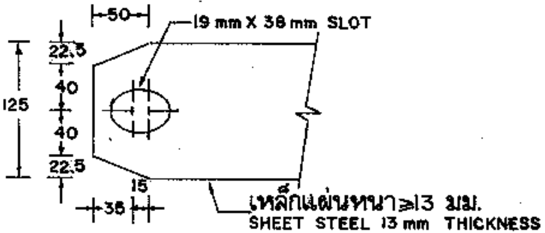

บัญชีวัสดุ
BILL OF MATERIAL

ลำดับที่ ITEM	รายละเอียด DESCRIPTION	จำนวน REQ'D	วัสดุเลขที่ MAT. NO.
1	เสาคอนกรีต 22 ม. POLE, CONCRETE 22 m LONG	1	00010011 0041
2	สลักเกลียว M 16 X 300 มม. BOLT, MACHINE, M 16 X 300 mm	2	01110204 0224
3	สลักเกลียว M 16 X 450 มม. BOLT, MACHINE, M 16 X 450 mm	7	01110207 0227
4	สลักเกลียว M 16 X 500 มม. BOLT, MACHINE, M 16 X 500 mm	2	01110208 0228
5	แหวนสี่เหลี่ยมแบน 52 X 52 X 4.5 มม. รู Ø 18 มม. มอก. 258 WASHER, SQUARE, FLAT 52 X 52 X 4.5 mm HOLE Ø 18 mm, TIS 258	11	01180100 0355
6	แอร์เบรคสวิตช์3 ขา 115 kV 1,200 A เปิดในแนวนอนพร้อมก้านโยกสวิตช์ คันโยกและอุปกรณ์ติดตั้ง SWITCH, AIR BREAK, TRIPLE POLE, 115 kV, 1,200 A, HORIZONTAL – OPENING, COMPLETE WITH MOUNTING ACCESSORIES	1	04060200 1556
7	ท่อ PVC แข็งขนาด Ø 20 X 1,000 มม.พร้อมอุปกรณ์ยึด CONDUIT, PVC RIGID, Ø 20 X 1,000 mm, COMP. WITH FIXING ACCESS	1	08040001 3285
8	สายทองแดงเปลือย 50 ต.มม. มอก. 64 CONDUCTOR, CU, SIZE 50 mm^2 TIS. 64	10	02000005 0504
9	หลักดินทำด้วยเหล็กเคลือบทองแดง GROUND ROD, COPPER – CLAD STEEL	1	01220007 1232
10	การต่อลงดินแบบเชื่อมด้วยความร้อน GROUND CONNECTION, WELDING SYSTEM	2	

รายละเอียด
DESCRIPTION

D-4C	การประกอบลูกถ้วยแขวน SUSPENSION INSULATOR ASSEMBLY	6	
OR D-14C	การประกอบลูกถ้วยแขวน SUSPENSION INSULATOR ASSEMBLY	6	
D-5A	การต่อสายล่อฟ้า OVERHEAD GROUND WIRE CONNECTION	1	
D-10A	ฐานรากเสา POLE FOUNDATION	1	

กองวิศวกรรมไฟฟ้าและเครื่องกล ฝ่ายวิศวกรรม	**การไฟฟ้าส่วนภูมิภาค**	ใช้แทนแบบ........
ผู้เขียน สมนึก สาคร ผู้สำรวจ........ วิศวกร........ หัวหน้าแผนก........ ผู้อำนวยการกอง........ ผู้อำนวยการฝ่าย........	ผู้ว่าการ........ 31. มี.ค. 2528 ยวถ.	ถูกแทนโดยแบบ........ เขียนเสร็จวันที่ 20 มค. 2538
	115 kV วงจรเดี่ยว สายไฟฟ้าคู่ การติดตั้งสวิตช์ตัดตอนสามขา (แอร์เบรคสวิตช์) แบบ SD-SW-2	แก้แบบวันที่........ มิติเป็น มิลลิเมตร มาตราส่วน —
รองผู้ว่าการฝ่ายเทคนิค	115 kV SINGLE CIRCUIT DOUBLE CONDUCTOR TRIPLE POLE AIR BREAK SWITCH INSTALLATION TYPE SD-SW-2	แบบเลขที่ SAI–015/38002 แผ่นที่ 2 ของจำนวน 2 แผ่น

29 ธ.ค. 2538