
การประกอบเลขที่ ASSEMBLY NO. 0551

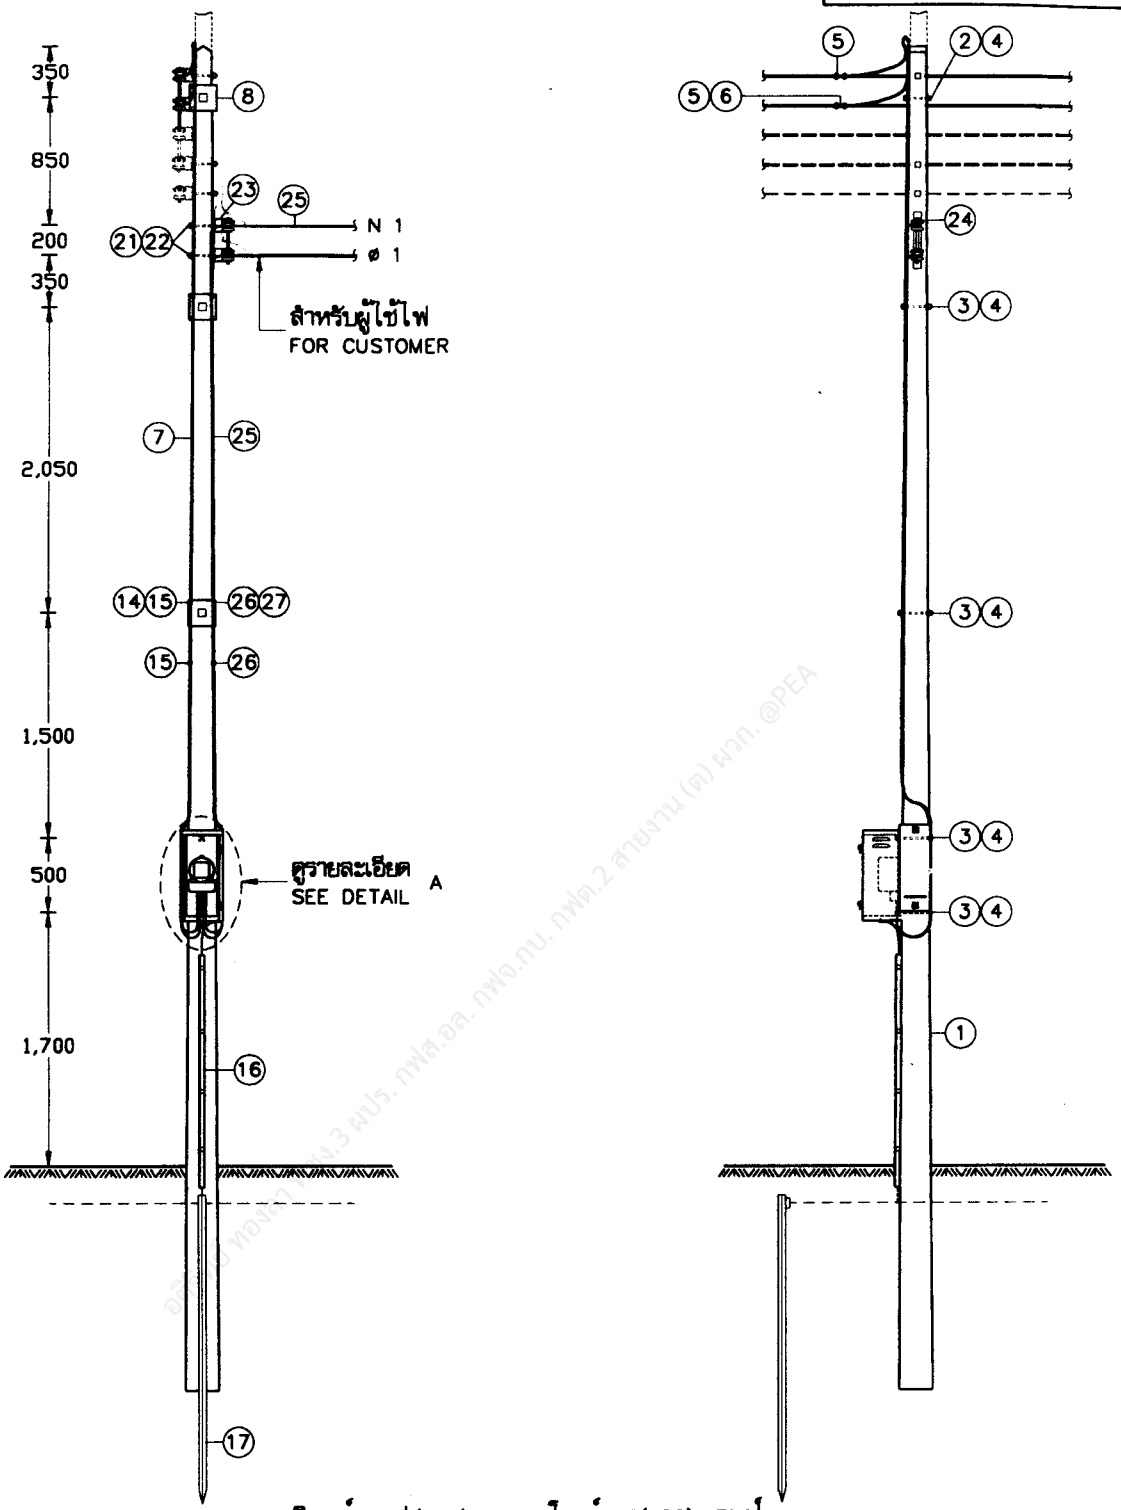


I TOU มิเตอร์ 1 เฟส 2 สาย 220 โวลต์ 10(100) แอมป์
10(100)A, 1-ø, 2-WIRE, 220 V, TOU METER

กองมาตรฐานระบบไฟฟ้า ฝ่ายมาตรฐานและความปลอดภัย	การไฟฟ้าส่วนภูมิภาค	ใช้แทนแบบ ..... ถูกแทนโดยแบบ ..... เขียนเสร็จวันที่ 1 เม.ย. 2546 แก้แบบวันที่ ..... มิติเป็น มิลลิเมตร มาตราส่วน 1:50
ผู้เขียน พงศักดิ์ ศิริสมบูรณ์ ..... ผู้สำรวจ ..... วิศวกร ..... หัวหน้าแผนก ..... ผู้อำนวยการกอง ..... ผู้อำนวยการฝ่าย	ผู้ว่าการ	
รองผู้ว่าการวางแผนและพัฒนาระบบไฟฟ้า	การติดตั้ง TOU มิเตอร์ 1 เฟส 2 สาย และ 3 เฟส 4 สาย 10(100) แอมป์ บนเสาระบบจำหน่าย 10(100)A, 1-ø, 2-WIRE AND 3-ø, 4-WIRE METER, TOU INSTALLATION ON DISTRIBUTION POLE	แบบเลขที่ SA2-015/46004 แผ่นที่ 1 ของจำนวน 6 แผ่น

21 เม.ย. 2546


การประกอบเลขที่ ASSEMBLY NO. 0551

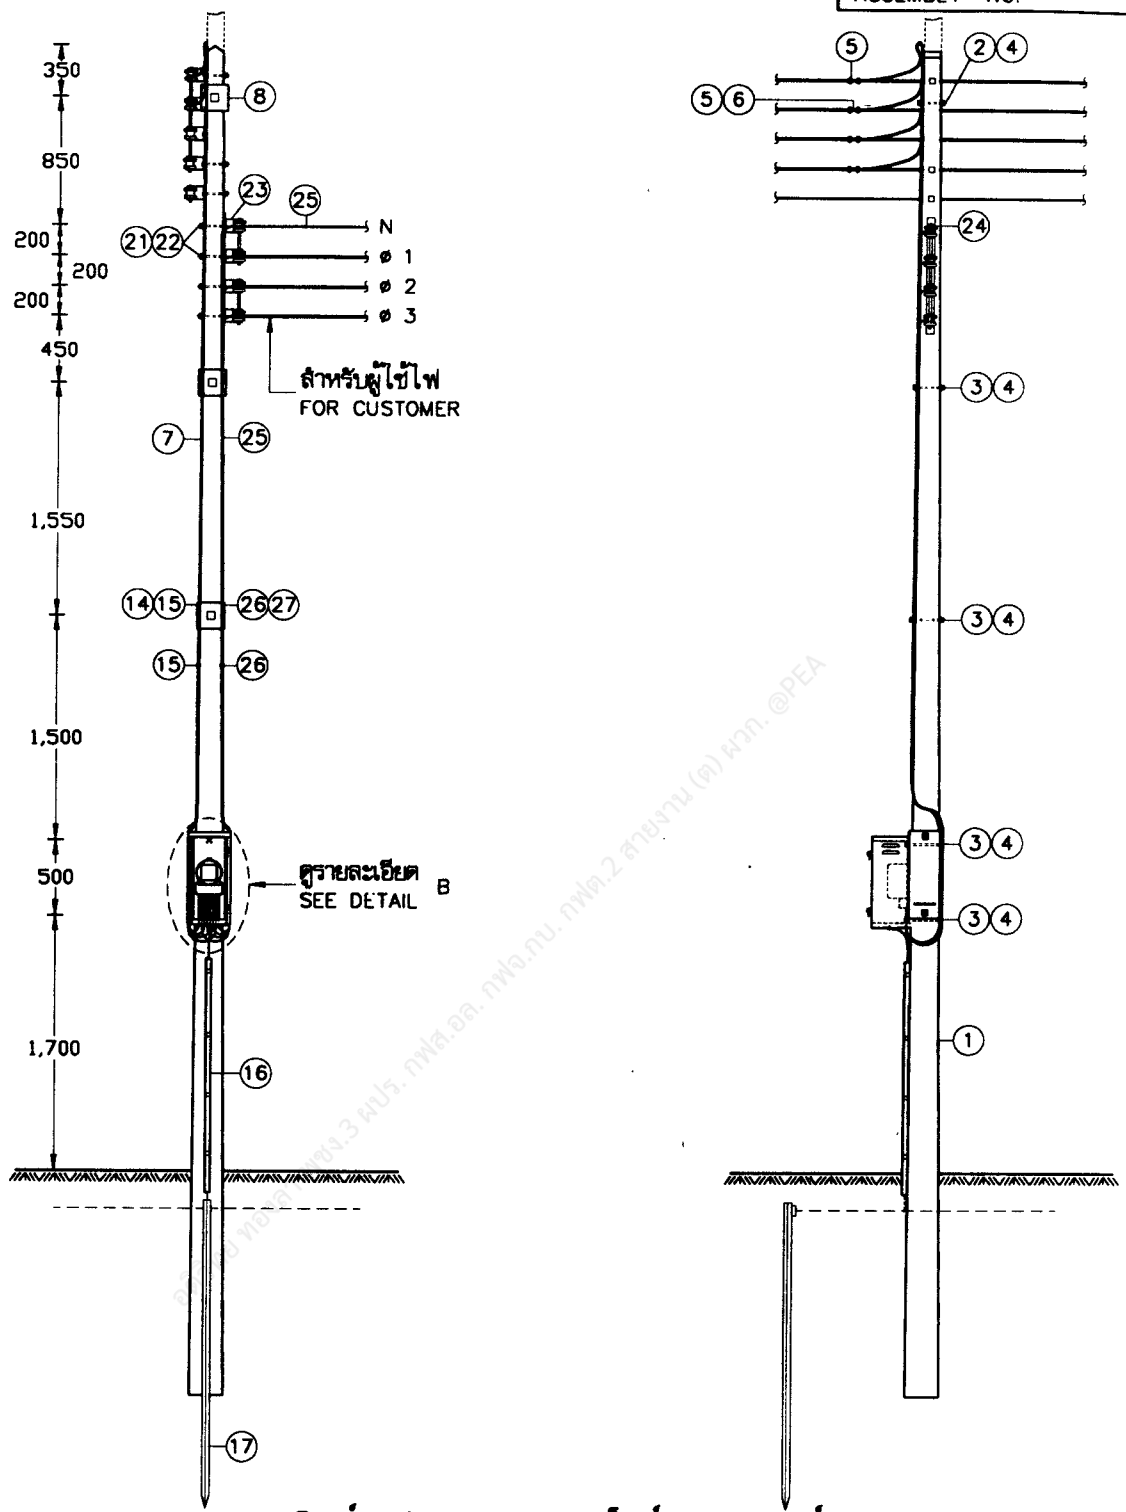


II TOU มิเตอร์ 3 เฟส 4 สาย 380/220 โวลต์ 10(100) แอมป์
10(100)A, 3-ø, 4-WIRE, 380/220V, TOU METER

กองมาตรฐานระบบไฟฟ้า ฝ่ายมาตรฐานและความปลอดภัย	การไฟฟ้าส่วนภูมิภาค	ใช้แทนแบบ ..... ถูกแทนโดยแบบ .....
ผู้เขียน พยุงศักดิ์ ศิริสมบูรณ์ ผู้สำรวจ ..... วิศวกร ..... หัวหน้าแผนก ..... ผู้อำนวยการกอง ..... ผู้อำนวยการฝ่าย	ผู้ว่าการ ..... 21 เมษ 2546 การติดตั้ง TOU มิเตอร์ 1 เฟส 2 สาย และ 3 เฟส 4 สาย 10(100) แอมป์ บนเสาระบบจำหน่าย	เขียนเสร็จวันที่ 1 เมษ 2546 แก้แบบวันที่ ..... มิติเป็น มิลลิเมตร มาตราส่วน 1:50
ของผู้อำนวยการวางแผนและพัฒนาระบบไฟฟ้า ..... 21 เมษ 2546	10(100)A, 1-ø, 2-WIRE AND 3-ø, 4-WIRE METER, TOU INSTALLATION ON DISTRIBUTION POLE	แบบเลขที่ SA2-015/46004 แผ่นที่ 2 ของจำนวน 6 แผ่น

การประกอบเลขที่ ASSEMBLY NO. 0551

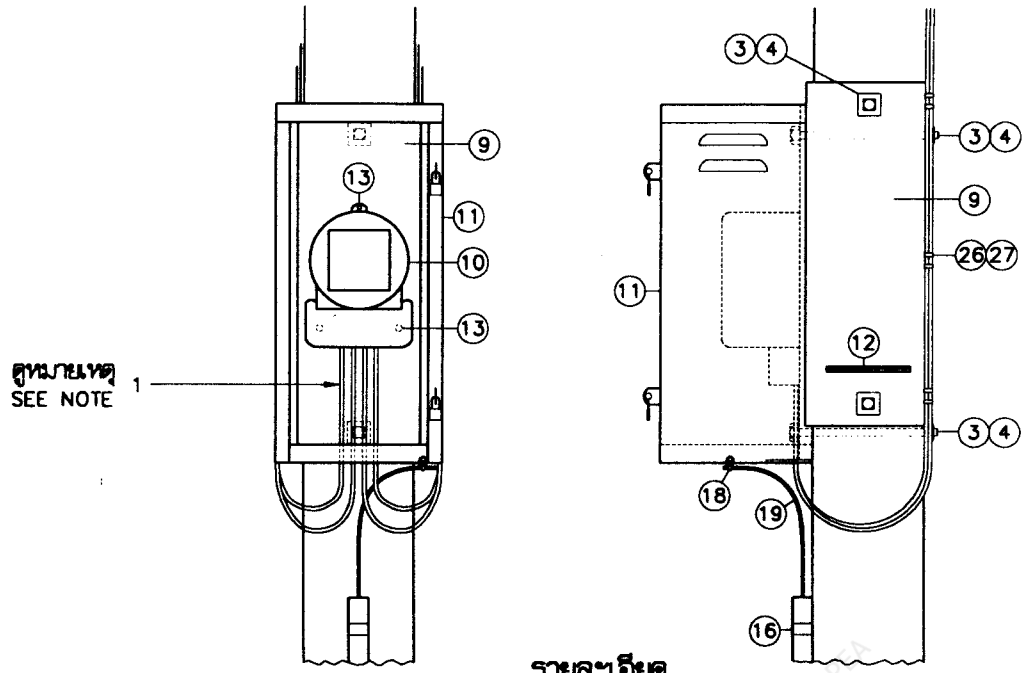

รายละเอียด A
DETAIL A

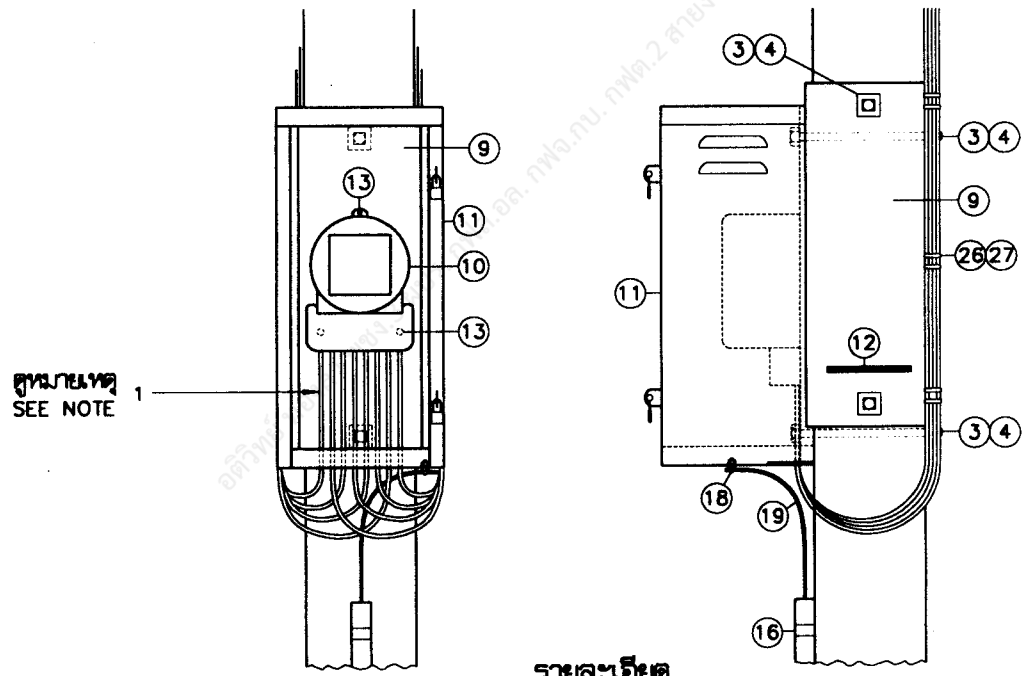

รายละเอียด B
DETAIL B

กองมาตรฐานระบบไฟฟ้า ฝ่ายมาตรฐานและความปลอดภัย	การไฟฟ้าส่วนภูมิภาค	ใช้แทนแบบ ..... ถูกแทนโดยแบบ ..... เขียนเสร็จวันที่ 1 เม.ย. 2546 แก้แบบวันที่ ..... มิติเป็น ..... มาตราส่วน .....
ผู้เขียน พงศักดิ์ ศิริสมบูรณ์ ผู้สำรวจ ..... วิศวกร ..... หัวหน้าแผนก ..... ผู้อำนวยการกอง ..... ผู้อำนวยการฝ่าย	ผู้ว่าการ ..... 21 เม.ย. 2546	
รองผู้ว่าการวางแผนและพัฒนาระบบไฟฟ้า	การติดตั้ง TOU มิเตอร์ 1 เฟส 2 สาย และ 3 เฟส 4 สาย 10(100) แอมป์ บนเสาระบบจำหน่าย 10(100)A, 1-ø, 2-WIRE AND 3-ø, 4-WIRE METER, TOU INSTALLATION ON DISTRIBUTION POLE	แบบเลขที่ SA2-015/46004 แผ่นที่ 3 ของจำนวน 6 แผ่น

21 เม.ย. 2546

การประกอบเลขที่ ASSEMBLY NO. 0 5 5 1

บัญชีวัสดุในส่วนที่ กฟภ. ลงทุน
BILL OF MATERIAL FOR PEA.

ลำดับที่ ITEM	รายละเอียด DESCRIPTION	จำนวน REQ'D I	จำนวน REQ'D II	วัสดุเลขที่ MAT. NO.
1	เสาคอนกรีต 8.00 ม. , 9.00 ม. , 12.00 ม. , 12.20 ม. , 14.00 ม. หรือ 14.30 ม. POLE, CONCRETE, 8.00 m, 9.00 m, 12.00 m, 12.20 m, 14.00 m OR 14.30 m	1	1	00010001-2 00010004 00010006 00010012-3
2	สลักเกลียว M 16x200 มม. สำหรับเสาคอนกรีต 8.00 ม. หรือ 9.00 ม. BOLT, MACHINE, M 16x200 mm; FOR 8.00 m OR 9.00 m CONCRETE POLE	1	1	01110202
	สลักเกลียว M 16x250 มม. สำหรับเสาคอนกรีต 12.00 ม. หรือ 14.00 ม. BOLT, MACHINE, M 16x250 mm; FOR 12.00 m OR 14.00 m CONCRETE POLE			01110203
	สลักเกลียว M 16x300 มม. สำหรับเสาคอนกรีต 12.20 ม. BOLT, MACHINE, M 16x300 mm; FOR 12.20 m CONCRETE POLE			01110204
	สลักเกลียว M 16x350 มม. สำหรับเสาคอนกรีต 14.30 ม. BOLT, MACHINE, M 16x350 mm; FOR 14.30 m CONCRETE POLE			01110205
3	สลักเกลียว M 16x250 มม. สำหรับเสาคอนกรีต 8.00 ม. หรือ 9.00 ม. BOLT, MACHINE, M 16x250 mm; FOR 8.00 m OR 9.00 m CONCRETE POLE	6	6	01110203
	สลักเกลียว M 16x300 มม. สำหรับเสาคอนกรีต 12.00 ม. หรือ 14.00 ม. BOLT, MACHINE, M 16x300 mm; FOR 12.00 m OR 14.00 m CONCRETE POLE			01110204
	สลักเกลียว M 16x350 มม. สำหรับเสาคอนกรีต 12.20 ม. BOLT, MACHINE, M 16x350 mm; FOR 12.20 m CONCRETE POLE			01110205
	สลักเกลียว M 16x400 มม. สำหรับเสาคอนกรีต 14.30 ม. BOLT, MACHINE, M 16x400 mm; FOR 14.30 m CONCRETE POLE			01110206
4	แหวนสี่เหลี่ยมแบน 52x52x4.5 มม. รู ø 18 มม. มอก. 258 WASHER, SQUARE, FLAT, 52x52x4.5 mm HOLE ø 18 mm, TIS 258	14	14	01180100
5	คอนเน็คเตอร์ชนิดบีบ แบบ H ขนาดตามต้องการ CONNECTOR, COMPRESSION, H TYPE, SIZE AS REQUIRED	2	4	02320003 02320002
6	PVC. เทป กว้าง 19 มม. (ใช้ความยาว 2 ม. ต่อ 1 จุด) มอก. 386 PVC. TAPE, 19 mm WIDE (2 m PER POINT) TIS 386	ม. m	ม. m	02180001
7	สายอะลูมิเนียม ขนาด 50 ตร.มม. หรือสายทองแดง ขนาด 35 ตร.มม. หุ้มฉนวน PVC 750 โวลต์ ความยาวตามต้องการ CABLE, Al 50 mm^2 OR Cu 35 mm^2, PVC-INSULATED, 750 V, LENGTH AS REQUIRED	ม. m	ม. m	02070002 ——
8	แป้นไม้สำหรับยึดสาย เข้า และออกจากมิเตอร์ ไสแล้ว ขนาด 20x20x2 ซม. CABLE PLATE, HARD WOOD, SURFACE FINISHED, 20x20x2 cm	3	3	06100000
9	แป้นไม้ รองรับมิเตอร์ไสแล้ว ขนาด 60x20x2 ซม. METER PLATE, HARD WOOD, SURFACE FINISHED, 60x20x2 cm	3	3	06100001
10	TOU มิเตอร์ 1 เฟส 2 สาย 220 โวลต์ 10(100) แอมป์ METER, TOU, 1-PHASE, 2-WIRE, 220 V, 10(100) A	1	–	06000510
	TOU มิเตอร์ 3 เฟส 4 สาย 220/380 โวลต์ 10(100) แอมป์ METER, TOU, 3-PHASE, 4-WIRE, 220/380 V, 10 (100) A	–	1	06000509
11	ตู้อะลูมิเนียม ใช้นอกอาคาร สำหรับมิเตอร์ 3 เฟส CABINET, ALUMINIUM, OUTDOOR, FOR 3-PHASE WATTHOUR METER	1	1	06100006
12	หมายเลขผู้ใช้ไฟ CUSTOMER NUMBER	1	1	

กองมาตรฐานระบบไฟฟ้า ฝ่ายมาตรฐานและความปลอดภัย	การไฟฟ้าส่วนภูมิภาค	ใช้แทนแบบ .....
ผู้เขียน พงศักดิ์ ศิริสมบูรณ์	ผู้ว่าการ	ถูกแทนโดยแบบ .....
ผู้สำรวจ		เขียนเสร็จวันที่ 1 เมษ. 2546
วิศวกร	21 เม.ย. 2546	แก้แบบวันที่ .....
หัวหน้าแผนก	การติดตั้ง TOU มิเตอร์ 1 เฟส 2 สาย และ 3 เฟส 4 สาย 10(100) แอมป์ บนเสาระบบจำหน่าย	มิติเป็น .....
ผู้อำนวยการกอง		มาตราส่วน .....
ผู้อำนวยการฝ่าย		
รองผู้ว่าการวางแผนและพัฒนาระบบไฟฟ้า	10(100)A, 1-ø, 2-WIRE AND 3-ø, 4-WIRE METER, TOU INSTALLATION ON DISTRIBUTION POLE	แบบเลขที่ SA2-015/46004
		แผ่นที่ 4 ของจำนวน 6 แผ่น

21 เม.ย. 2546

การประกอบเลขที่ ASSEMBLY NO. 0551

บัญชีวัสดุในส่วนที่ กฟภ. ลงทุน
BILL OF MATERIAL FOR PEA.

ลำดับที่ ITEM	รายละเอียด DESCRIPTION	จำนวน REQ'D I	จำนวน REQ'D II	วัสดุเลขที่ MAT. NO.
13	ตะปูเกลียวชุบโครเมี่ยม ขนาด 15–20 มม. SCREW, CHROME PLATED, SIZE 15–20 mm	3	3	
14	ตะปูหัวกลมแบน ø 1 มม. ยาว 15–20 มม. มอก. 113 NAIL, ROUND, MILD STEEL WIRE ø 1 mm, 15–20 mm, LONG TIS 113	24	24	
15	เข็มขัดรัดสาย (ทำด้วยสวดอะลูมิเนียม 1x10 มม.) ช่วงระยะ 50 ซม. สำหรับมิเตอร์ 1 เฟส 2 สาย และช่วงระยะ 25 ซม. สำหรับมิเตอร์ 3 เฟส 4 สาย CABLE, STRAP (MADE OF ARMOUR TAPE 1x10 mm) AT 50 cm INTERVAL FOR 1ø, 2–WIRE, METER AND AT 25 cm INTERVAL FOR 3ø 4–WIRE METER	กก. kg	กก. kg	02200000
16	ท่อ พีวีซีแข็ง ขนาด ø 20 มม. ยาว 2,500 มม. มอก. 216 มม. พร้อมอุปกรณ์ยึด (การประกอบเลขที่ 9704, 9704 A) CONDUIT, PVC RIGID, ø 20 mm, 2,500 mm LONG TIS 216 COMPLETE WITH FIXING ACCESS. (ASSEMBLY NO. 9704, 9704A)	1	1	08040001
17	หลักดิน 60x60x5 มม. ยาว 2 ม. ROD, GROUND 60x60x5 mm, 2 m LONG	1	1	01220002
18	ยูแคล้มป์ สลัก 1 ตัว M 8 (ไวร์ ไรป์ คลิพ) CLAMP, SINGLE U–BOLT, M 8 (WIRE ROPE CLIP)	1	1	01230000
19	ลวดเหล็กตีเกลียว 50/7 ตร.มม. WIRE, STEEL STRANDED, 50/7 mm^2	ม. m	ม. m	01100004
20				

บัญชีวัสดุในส่วนของผู้ใช้ไฟ

21	สลักเกลียว M 16x250 มม. สำหรับเสาคอนกรีต 8.00 ม. หรือ 9.00 ม. BOLT, MACHINE, M 16x250 mm; FOR 8.00 m OR 9.00 m CONCRETE POLE	2	4	01110202
	สลักเกลียว M 16x300 มม. สำหรับเสาคอนกรีต 12.00 ม. หรือ 14.00 ม. BOLT, MACHINE, M 16x300 mm; FOR 12.00 m OR 14.00 m CONCRETE POLE			01110203
	สลักเกลียว M 16x350 มม. สำหรับเสาคอนกรีต 12.20 ม. BOLT, MACHINE, M 16x350 mm; FOR 12.20 m CONCRETE POLE			01110204
	สลักเกลียว M 16x400 มม. สำหรับเสาคอนกรีต 14.30 ม. BOLT, MACHINE, M 16x400 mm; FOR 14.30 m CONCRETE POLE			01110205
22	แหวนสี่เหลี่ยมแบน 52x52x4.5 มม. รู ø 18 มม. มอก. 258 WASHER, SQUARE, FLAT, 52x52x4.5 mm, HOLE ø 18 mm, TIS 258	2	4	01180100
23	แร็ค 2x200 มม. แบบหลังยื่น RACK, SECONDARY, MEDIUM PRESSED STEEL, 2x200 mm, EXTENDED BACK	1	–	03130000
	แร็ค 4x200 มม. แบบหลังยื่น RACK, SECONDARY, MEDIUM PRESSED STEEL, 4x200 mm, EXTENDED BACK	–	1	03130002

กองมาตรฐานระบบไฟฟ้า ฝ่ายมาตรฐานและความปลอดภัย	การไฟฟ้าส่วนภูมิภาค	ใช้แทนแบบ .....
ผู้เขียน พงศักดิ์ ศิริสมบูรณ์	ผู้ว่าการ	ถูกแทนโดยแบบ .....
ผู้สำรวจ		เขียนเสร็จวันที่ 1 เม.ย. 2546
วิศวกร สุพล	การติดตั้ง TOU มิเตอร์ 1 เฟส 2 สาย และ 3 เฟส 4 สาย	แก้แบบวันที่ .....
หัวหน้าแผนก	10(100) แอมป์ บนเสาระบบจำหน่าย	มีติเป็น .....
ผู้อำนวยการกอง		มาตราส่วน .....
ผู้อำนวยการฝ่าย		
ของผู้วางการวางแผนและพัฒนาระบบไฟฟ้า	10(100)A, 1–ø, 2–WIRE AND 3–ø, 4–WIRE METER, TOU INSTALLATION ON DISTRIBUTION POLE	แบบเลขที่ SA2–015/46004
		แผ่นที่ 5 ของจำนวน 6 แผ่น

21 เม.ย. 2546

การประกอบเลขที่ ASSEMBLY NO. 0551

บัญชีวัสดุในส่วนของผู้ใช้ไฟ
BILL OF MATERIAL FOR CUSTOMER

ลำดับที่ ITEM	รายละเอียด DESCRIPTION	จำนวน REQ'D I	จำนวน REQ'D II	วัสดุเลขที่ MAT. NO.
24	ลูกรอกแรงต่ำ มอก. 227 แบบ ข. (แบบ 53-2) INSULALATOR, SPOOL TYPE, L.V. TIS 227 TYPE B (CLASS 53-2)	2	4	03030000
25	สายอะลูมิเนียม ขนาด 50 ตร.มม. หรือสายทองแดง ขนาด 35 ตร.มม. หุ้มฉนวน PVC. 750 โวลต์ CABLE, Al 50 mm^2 OR Cu 35 mm^2, PVC-INSULATED, 750 V	ม. m	ม. m	——
26	เข็มขัดรัดสาย (ทำด้วยลวดอะลูมิเนียม 1x10 มม.) ช่วงระยะ 50 ซม. สำหรับมิเตอร์ 1 เฟส 2 สาย และช่วงระยะ 25 ซม. สำหรับมิเตอร์ 3 เฟส 4 สาย CABLE, STRAP (MADE OF ARMOUR TAPE 1x10 mm) AT 50 cm INTERVAL FOR 1ø, 2-WIRE, METER AND AT 25 cm INTERVAL FOR 3ø 4-WIRE METER	กก. kg	กก. kg	02200000
27	ตะปูหัวกลมแบน ø 1 มม. ยาว 15-20 มม. มอก. 113 NAIL, ROUND, MILD STEEL WIRE ø 1 mm, 15-20 mm, LONG TIS 113	20	20	

หมายเหตุ 1 การต่อสาย TOU มิเตอร์ (แบบตรง) ใช้สำหรับ :

— TOU มิเตอร์ 1 เฟส 2 สาย 220 โวลต์ 10(100) แอมป์ ผลิตภัณฑ์ของ ABB

— TOU มิเตอร์ 3 เฟส 4 สาย 380/220 โวลต์ 10(100) แอมป์ ผลิตภัณฑ์ของ ISKRA

2 สำหรับการต่อสายเข้ามิเตอร์อื่นๆ ให้ดูตามแผ่นป้ายที่แนบมากับมิเตอร์ นั้นๆ

NOTES 1 THE CONNECTION DIAGRAM OF TOU METER (DIRECT CONNECTED) FOR :

— 1-PHASE, 2-WIRE 220V, 10(100)A, TOU METER MANUFACTURED) BY ABB

— 3-PHASE, 4-WIRE 380/220V, 10(100)A, TOU METER MANUFACTURED) BY ISKRP

2 FOR CONNECTION DIAGRAM OF ANY TYPE SEE DIAGRAM ATTACHES TO THE METER .

กองมาตรฐานระบบไฟฟ้า ฝ่ายมาตรฐานและความปลอดภัย	การไฟฟ้าส่วนภูมิภาค	ใช้แทนแบบ .....
ผู้เขียน พงษ์ศักดิ์ ศิริสมบูรณ์	ผู้ว่าการ	ถูกแทนโดยแบบ .....
ผู้สำรวจ		เขียนเสร็จวันที่ 1 เมษ. 2546
วิศวกร	21 เมษ. 2546	แก้แบบวันที่ .....
หัวหน้าแผนก	การติดตั้ง TOU มิเตอร์ 1 เฟส 2 สาย และ 3 เฟส 4 สาย 10(100) แอมป์ บนเสาระบบจำหน่าย	มิติเป็น .....
ผู้อำนวยการกอง		มาตราส่วน .....
ผู้อำนวยการฝ่าย		
ของผู้ว่าการวางแผนและพัฒนาระบบไฟฟ้า	10(100)A, 1-ø, 2-WIRE AND 3-ø, 4-WIRE METER, TOU INSTALLATION ON DISTRIBUTION POLE	แบบเลขที่ SA2-015/46004 แผ่นที่ 6 ของจำนวน 6 แผ่น

21 เมษ. 2546