การประกอบเลขที่ ASSEMBLY NO.	5155

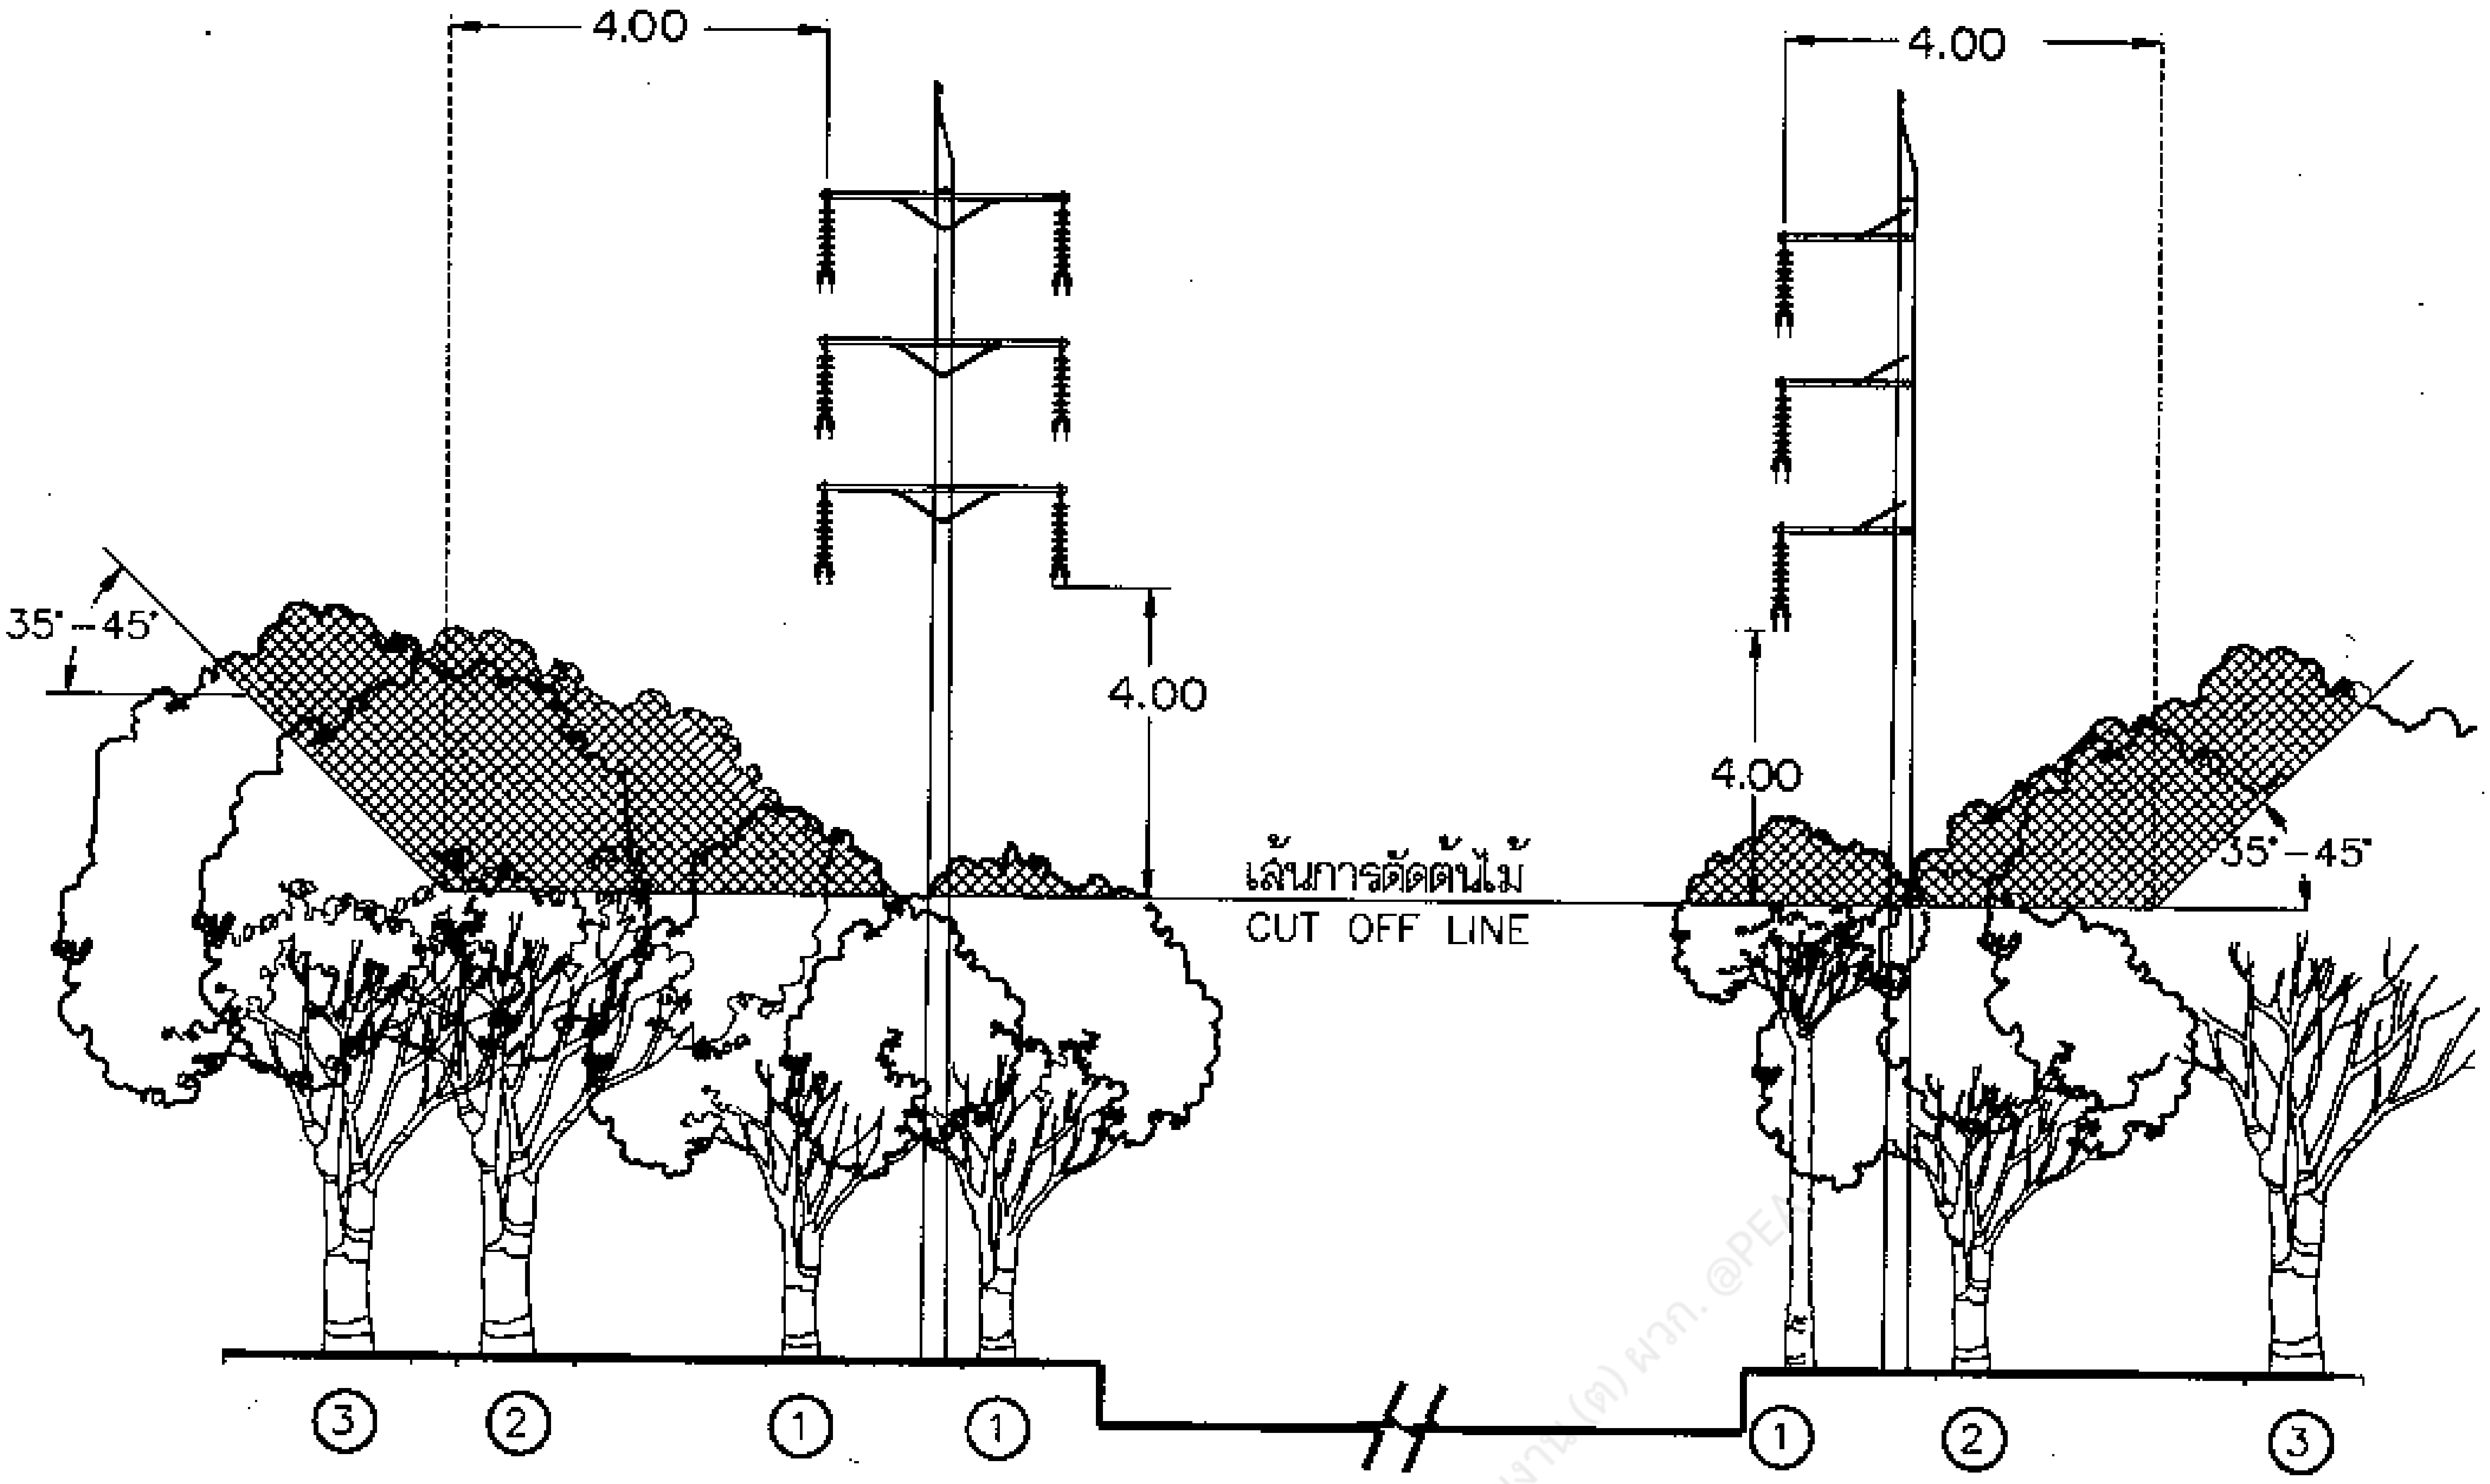

ระยะห่างจากสายไฟฟ้า CLEARANCE FROM CONDUCTOR	ระยะห่างน้อยสุด (ม.) MINIMUM CLEARANCE IN (m)	หมายเหตุ NOTE
ถึงส่วนบนของต้นไม้ TO TOP OF TREE	4.00	ตามตำแหน่งที่ ① และ ② ACCORDING TO POSITION ① & ②
ถึงด้านข้างของต้นไม้ TO SIDE OF TREE	4.00	ตามตำแหน่งที่ ③ ACCORDING TO POSITION ③

อติวิทย์ ทอง[illegible] พชง.3 ผบร. กฟส.อ[illegible] กฟล.กบ. กฟต.2 สายงาน (ต) ผวก. @PEA

หมายเหตุ

กรณีมีระบบอื่นใต้ไลน์สายส่ง ให้พิจารณาระยะห่างการตัดต้นไม้ ตามแบบเลขที่ S02-015/18070 (การประกอบเลขที่ 8603) ด้วย

NOTE

IF HAVE OTHER SYSTEMS,UNDER TRANSMISSION LINE, THE CLEARANCE OF TREE TRIMMING SHALL BE CONSIDERED ACCORDING TO DWG.NO. S02-015/18070 (ASSEMBLY No.8603) ALSO.

กองวิศวกรรมไฟฟ้าและเครื่องกล
ฝ่ายวิศวกรรม

การไฟฟ้าส่วนภูมิภาค

ผู้เขียน วิสุทธิ์ ชื่อเพราะ
ผู้สำรวจ
วิศวกร
หัวหน้าแผนก
ผู้อำนวยการกอง
ผู้อำนวยการฝ่าย

ผู้ว่าการ ก.ค. 2539

การตัดต้นไม้
สำหรับแนวสายส่ง 115 kV

TREE TRIMMING
FOR 115 kV LINE

รองผู้ว่าการ

ใช้แทนแบบ
ถูกแทนโดยแบบ
เขียนเสร็จวันที่ 8 กค. 39
แก้แบบวันที่
มิติเป็น ม. / m.
มาตราส่วน NOT TO SCALE
แบบเลขที่ SA1-015/39009
แผ่นที่ 1 ของจำนวน 1 แผ่น

15 ก.ค. 2539