การประกอบเลขที่
ASSEMBLY NO. 5687 H

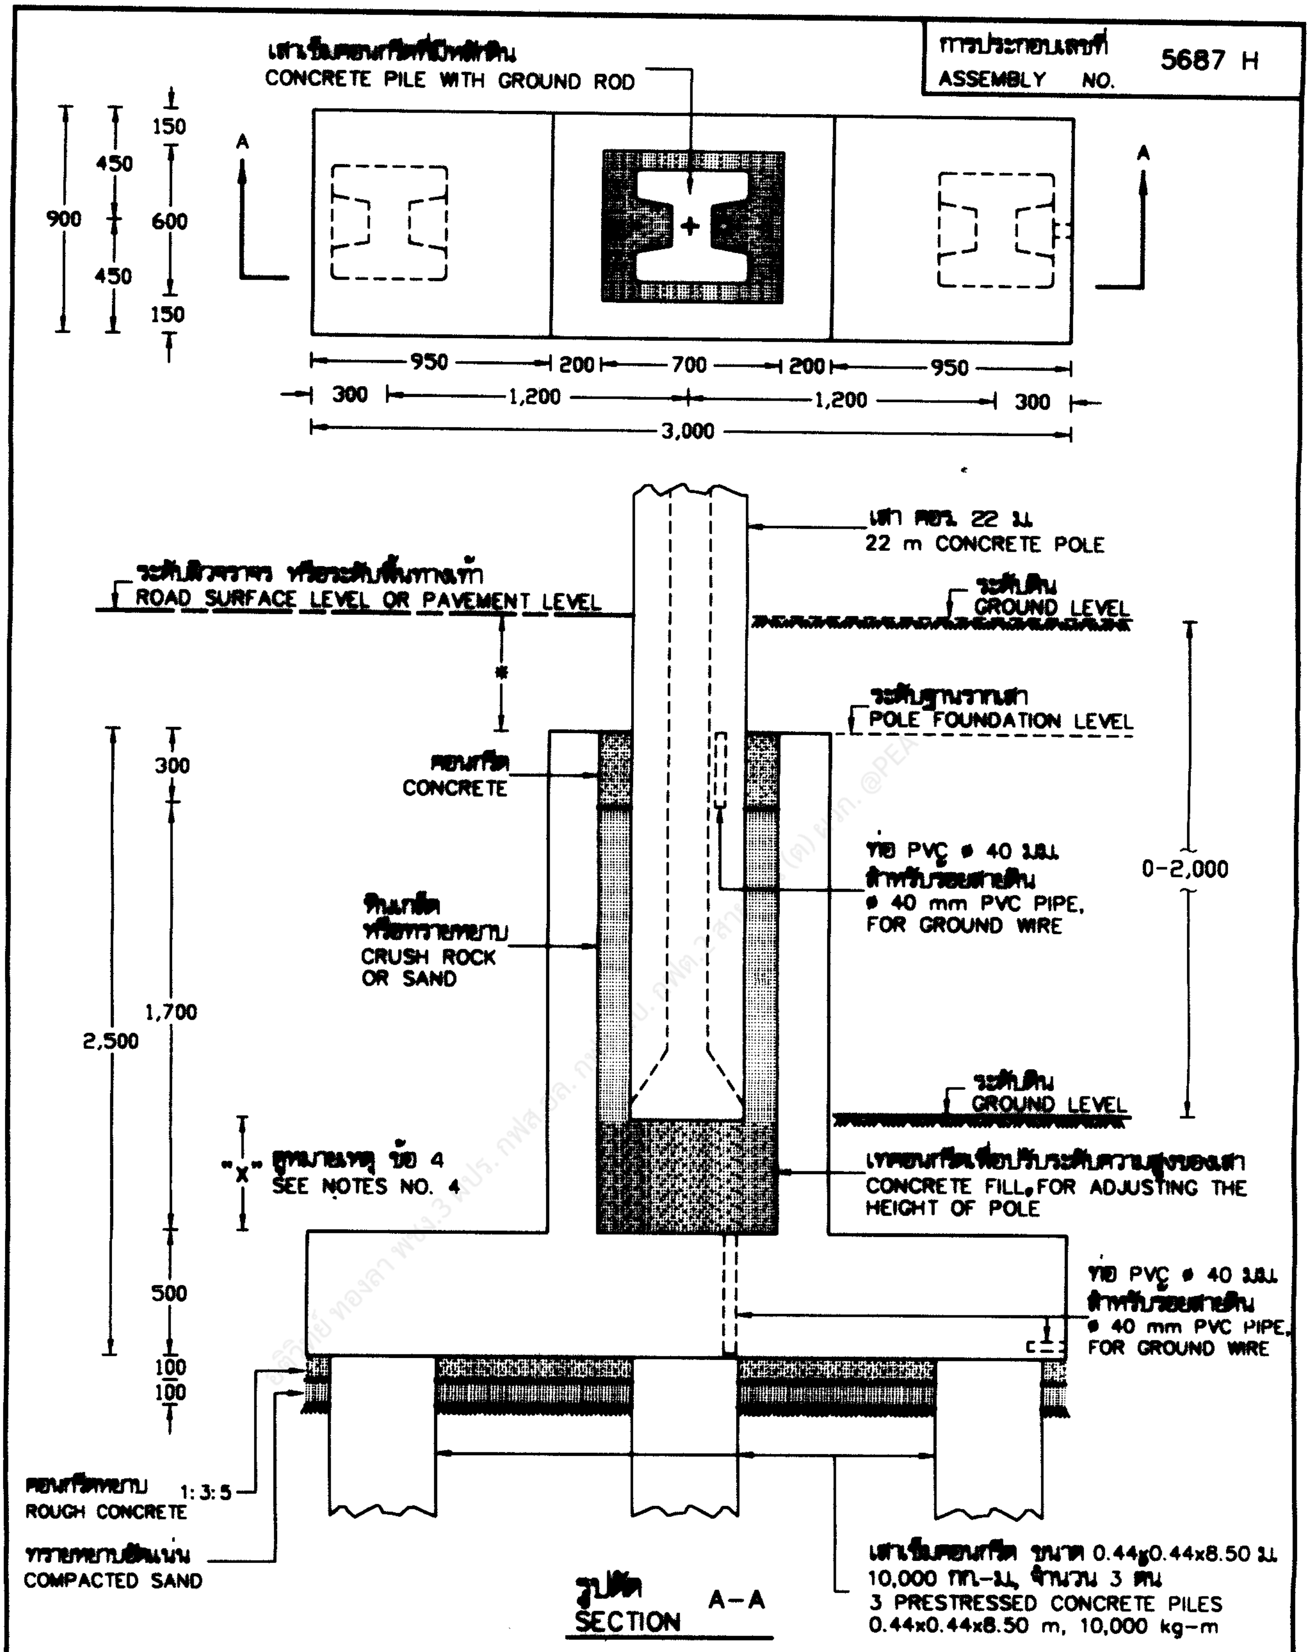
เสาเข็มคอนกรีตที่มีหลักดิน
CONCRETE PILE WITH GROUND ROD
A
A
900
450
450
150
600
150
950
200
700
200
950
300
1,200
1,200
300
3,000
เสา คอร. 22 ม.
22 m CONCRETE POLE
ระดับผิวจราจร หรือระดับพื้นทางเท้า
ROAD SURFACE LEVEL OR PAVEMENT LEVEL
ระดับดิน
GROUND LEVEL
*
ระดับฐานรากเสา
POLE FOUNDATION LEVEL
คอนกรีต
CONCRETE
ท่อ PVC ⌀ 40 มม. สำหรับร้อยสายดิน
⌀ 40 mm PVC PIPE, FOR GROUND WIRE
0–2,000
หินเกล็ด หรือทรายหยาบ
CRUSH ROCK OR SAND
300
1,700
2,500
500
100
100
ระดับดิน
GROUND LEVEL
"X" ดูหมายเหตุ ข้อ 4
SEE NOTES NO. 4
เทคอนกรีตเพื่อปรับระดับความสูงของเสา
CONCRETE FILL, FOR ADJUSTING THE HEIGHT OF POLE
ท่อ PVC ⌀ 40 มม. สำหรับร้อยสายดิน
⌀ 40 mm PVC PIPE, FOR GROUND WIRE
คอนกรีตหยาบ 1:3:5
ROUGH CONCRETE
ทรายหยาบอัดแน่น
COMPACTED SAND
เสาเข็มคอนกรีต ขนาด 0.44x0.44x8.50 ม. 10,000 กก.-ม., จำนวน 3 ต้น
3 PRESTRESSED CONCRETE PILES 0.44x0.44x8.50 m, 10,000 kg-m

รูปตัด A–A
SECTION A–A

กองมาตรฐานระบบไฟฟ้า
ฝ่ายมาตรฐานและความปลอดภัย

การไฟฟ้าส่วนภูมิภาค

ผู้เขียน ...สมชาย...
ผู้ตรวจ ....
วิศวกร ....
หัวหน้าแผนก ....
ผู้อำนวยการกอง ....
ผู้อำนวยการฝ่าย ....

รองผู้ว่าการวางแผนและพัฒนาระบบไฟฟ้า

ผู้ว่าการ ....

รายละเอียดที่ 10A 23 ก.ย. 2547
ฐานรากเสา (แบบที่ 22)

DETAIL 10A
POLE FOUNDATION (TYPE 22)

ใช้แทนแบบ SA1-015/45017
ถูกแทนโดยแบบ ....
เขียนเสร็จวันที่ 10 มี.ค. 2547
แก้แบบวันที่ ....
มิติเป็น มิลลิเมตร
มาตราส่วน 1:30
แบบเลขที่ SA1-015/47025
แผ่นที่ 1 ของจำนวน 2 แผ่น

23 ก.ย. 2547

การประกอบเลขที่ / ASSEMBLY NO. 5687 H

หมายเหตุ

1 ใช้ในกรณีทางตรงหรือทางโค้ง ที่มีสายยึดโยง (กรณีพื้นที่ก่อสร้างฐานรากเสามีระดับต่ำกว่าระดับผิวจราจรหรือระดับพื้นทางเท้า 0.00-2.00 ม.)

2 ดูรายละเอียดเพิ่มเติมใน แบบเลขที่ IB2-011/44017

3* ดูข้อกำหนดการติดตั้งฐานรากเสาในเขตทางหลวง ตามแบบเลขที่ SA1-015/43012 (การประกอบเลขที่ 5687)

4 ระยะ "X"= 450 มม. สำหรับการก่อสร้างฐานรากเสาในพื้นที่ทางหลวงที่ไม่มีทางเท้า ส่วนพื้นที่อื่นๆ ระยะ "X"= 0 มม.

NOTES

1 USE FOR STRAIGHT OR ANGLE LINE WITH GUY (IN CASE OF GROUND SURFACE LEVEL IS BETWEEN 0.00–2.00 m LOWER THAN ROAD SURFACE LEVEL OR PAVEMENT LEVEL) .

2 SEE ADDITIONAL DETAIL, DWG. NO. IB2–011/44017 .

3* SEE RECOMMENDATION, FOR POLE FOUNDATION INSTALLATION IN HIGHWAY AREA, DWG. NO SA1–015/43012 (ASSEMBLY NO. 5687) .

4 THE "X" IS 450 mm HEIGHT FOR FOUNDATION CONSTRUCTION IN HIGHWAY AREA WHICH HAVE NO PAVEMENT, OTHER AREA THE "X" IS ZERO .

อดิวิทย์ ทองลา พชง.3 ผปร. กฟส.อล. กฟจ.กบ. กฟต.2 สายงาน (ต) ผวก. @PEA

กองมาตรฐานระบบไฟฟ้า
ฝ่ายมาตรฐานและความปลอดภัย

ผู้เขียน ..[illegible]..
ผู้ตรวจ
วิศวกร
หัวหน้าแผนก
ผู้อำนวยการกอง
ผู้อำนวยการฝ่าย

รองผู้ว่าการวางแผนและพัฒนาระบบไฟฟ้า

การไฟฟ้าส่วนภูมิภาค

ผู้ว่าการ

รายละเอียดที่ 10A 23 ก.ย. 2547
ฐานรากเสา (แบบที่ 22)

DETAIL 10A
POLE FOUNDATION (TYPE 22)

ใช้แทนแบบ SA1–015/45017
ถูกแทนโดยแบบ
เขียนเสร็จวันที่ 10 ส.ค. 2547
แก้แบบวันที่
มิติเป็น
มาตราส่วน

แบบเลขที่ SA1–015/47025
แผ่นที่ 2 ของจำนวน 2 แผ่น

ก.ย. 2547