


การประกอบเลขที่ 3308
ASSEMBLY NO.

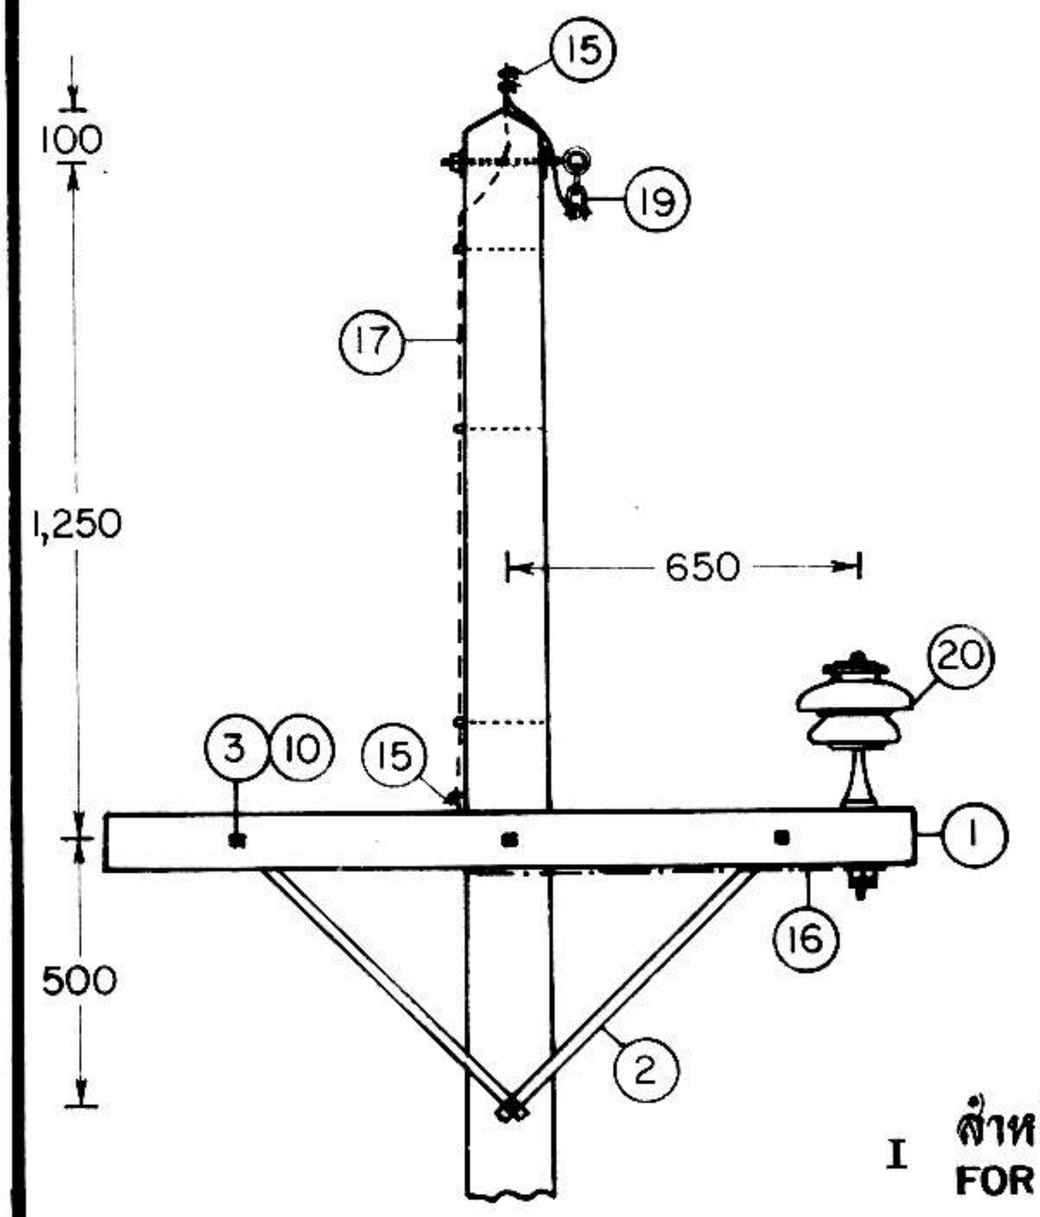


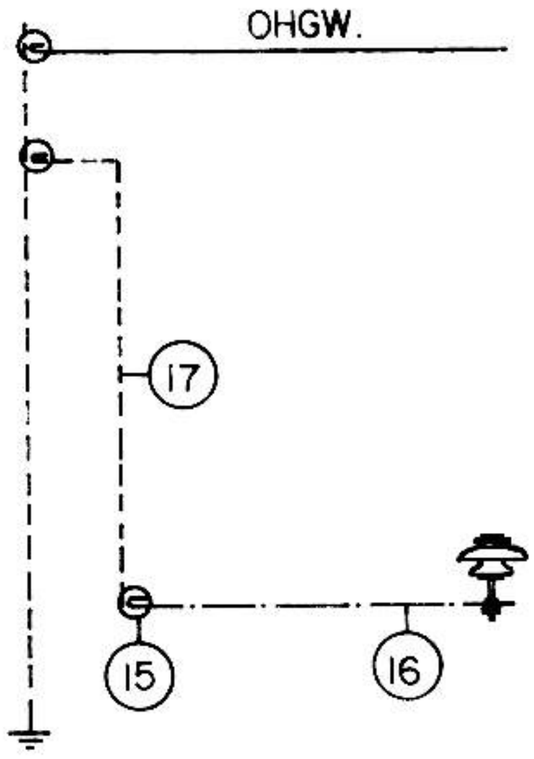


ไดอะแกรมแสดงการต่อลงดิน
EARTHING DIAGRAM

I สำหรับทางตรง 0°-5°
FOR LINE ANGLE

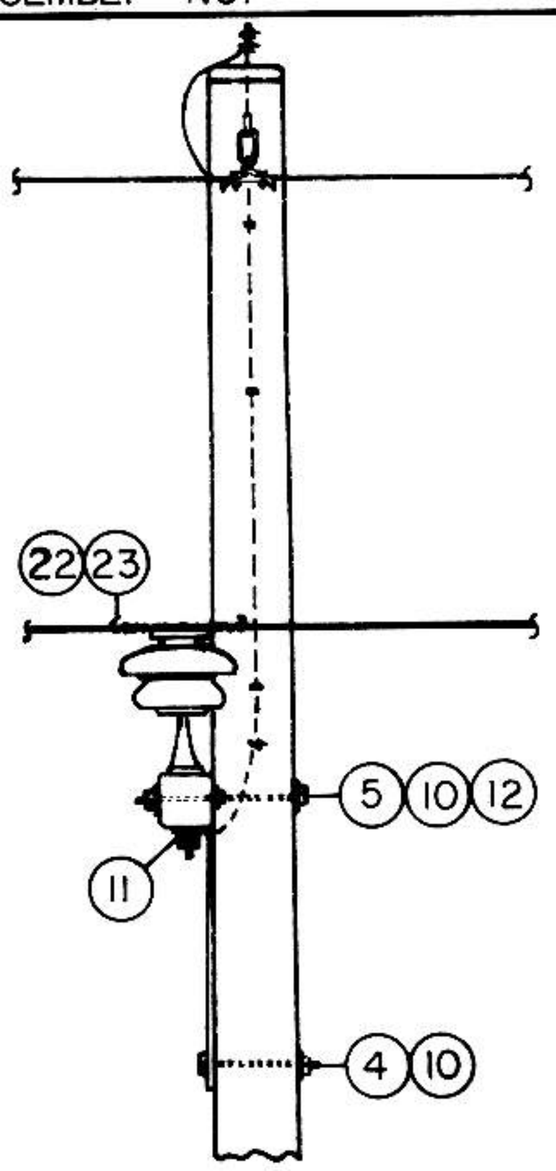


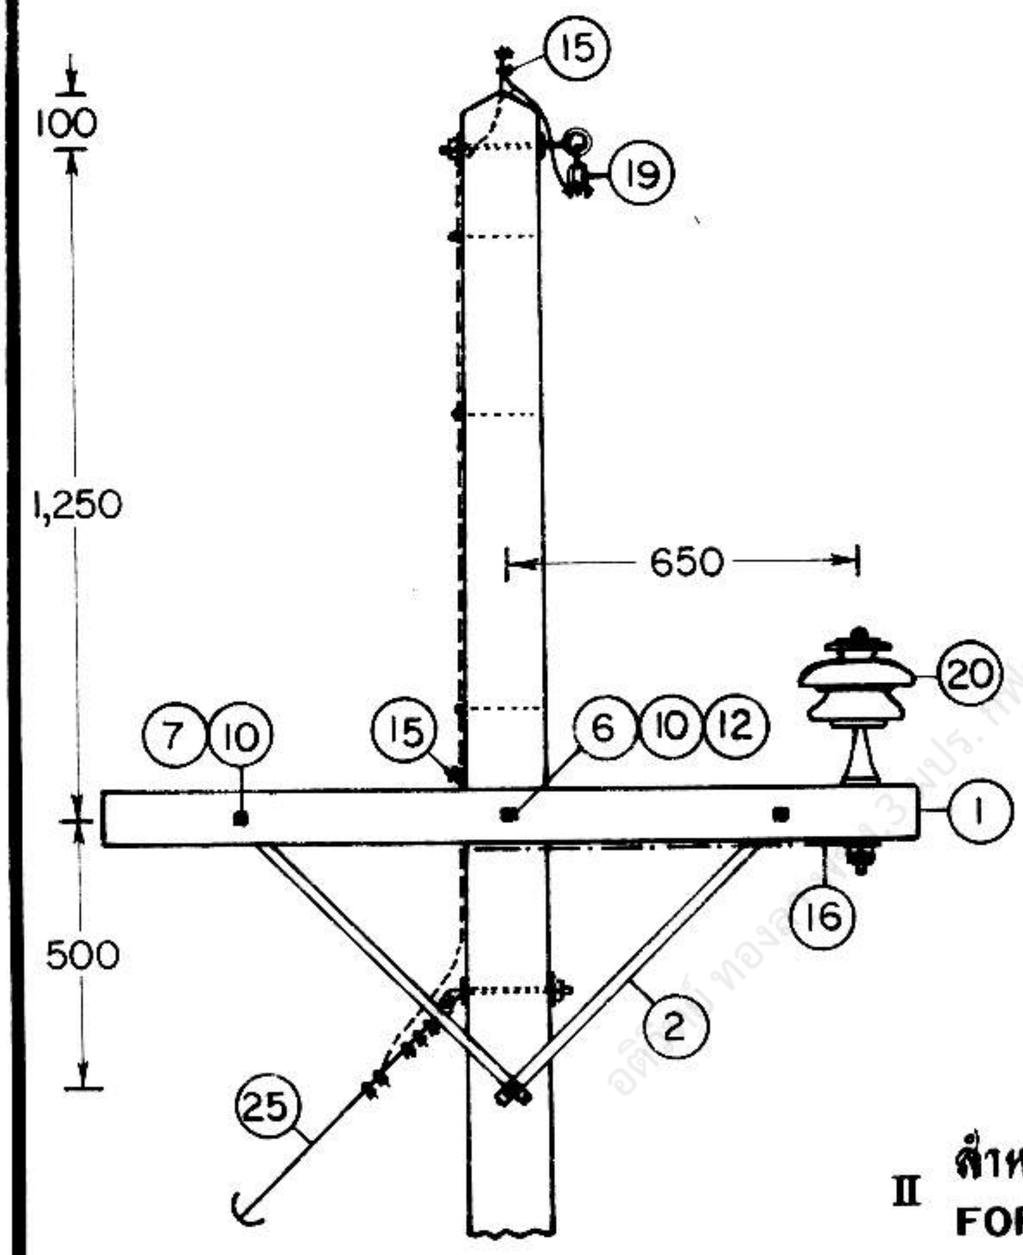

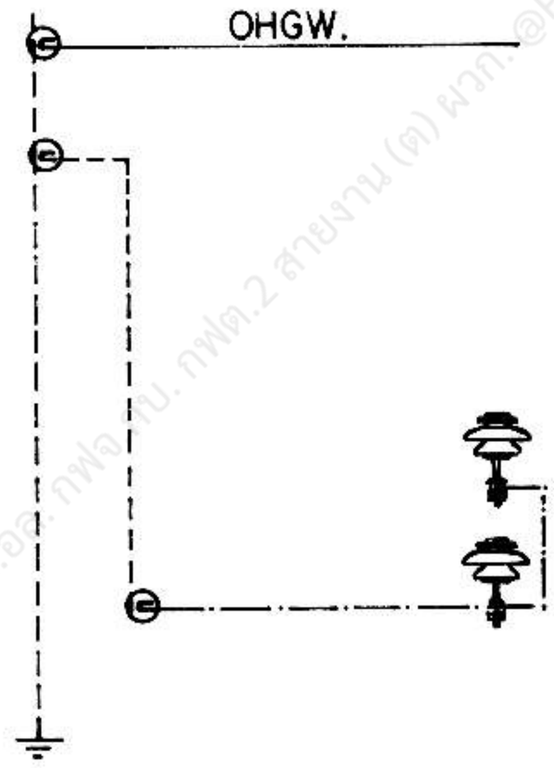

ไดอะแกรมแสดงการต่อลงดิน
EARTHING DIAGRAM

II สำหรับทางโค้งมุม 5°-30°
FOR LINE ANGLE

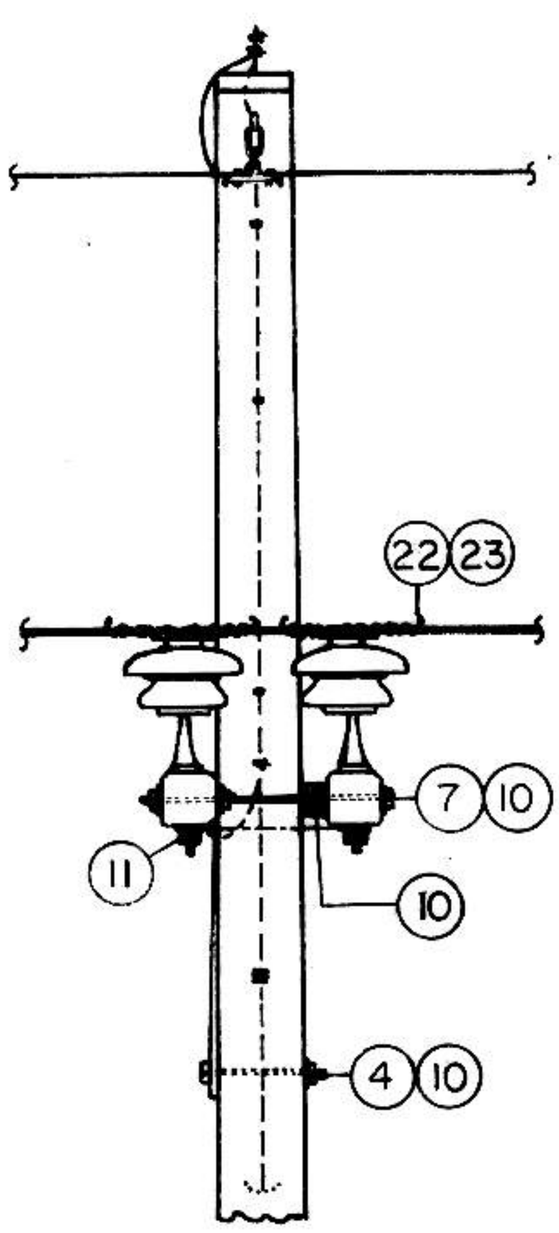


สำหรับใช้ก่อสร้างในบริเวณที่มีโหลดน้อย และ ไม่มีการปรับปรุงเป็นระบบ 3 เฟส 33 kV ในอนาคตอันใกล้
FOR LIGHT LOAD SITE CONSTRUCTION AND SHALL NOT BE REVAMPED TO 3-PHASE 33 kV SYSTEM IN THE NEAR FUTURE


กองวิศวกรรมไฟฟ้าและเครื่องกล ฝ่ายวิศวกรรม	การไฟฟ้าส่วนภูมิภาค	ใช้แทนแบบ..... ถูกแทนโดยแบบ..... เขียนเสร็จวันที่ 25 พ.ย. 29
ผู้เขียน..... ผู้สำรวจ..... วิศวกร..... หัวหน้าแผนก..... ผู้อำนวยการกอง..... ผู้อำนวยการฝ่าย.....	ผู้ว่าการ..... 9 เม.ย. 30.	แก้แบบวันที่..... มิติเป็น mm. มาตราส่วน 1 : 25
รองผู้ว่าการฝ่ายเทคนิค.....	การประกอบคอน คอนกรีต กับเสาคอนกรีต 12 ม. ระบบ 1 เฟส 19 kV CONCRETE CROSSARM ASSEMBLY ON 12 m CONCRETE POLE 1-PHASE 19 kV SYSTEM	แบบเลขที่ SAI-015/29023 แผ่นที่ 1 ของจำนวน 4 แผ่น

- 8 เม.ย. 2530

การประกอบเลขที่ ASSEMBLY NO. 3308

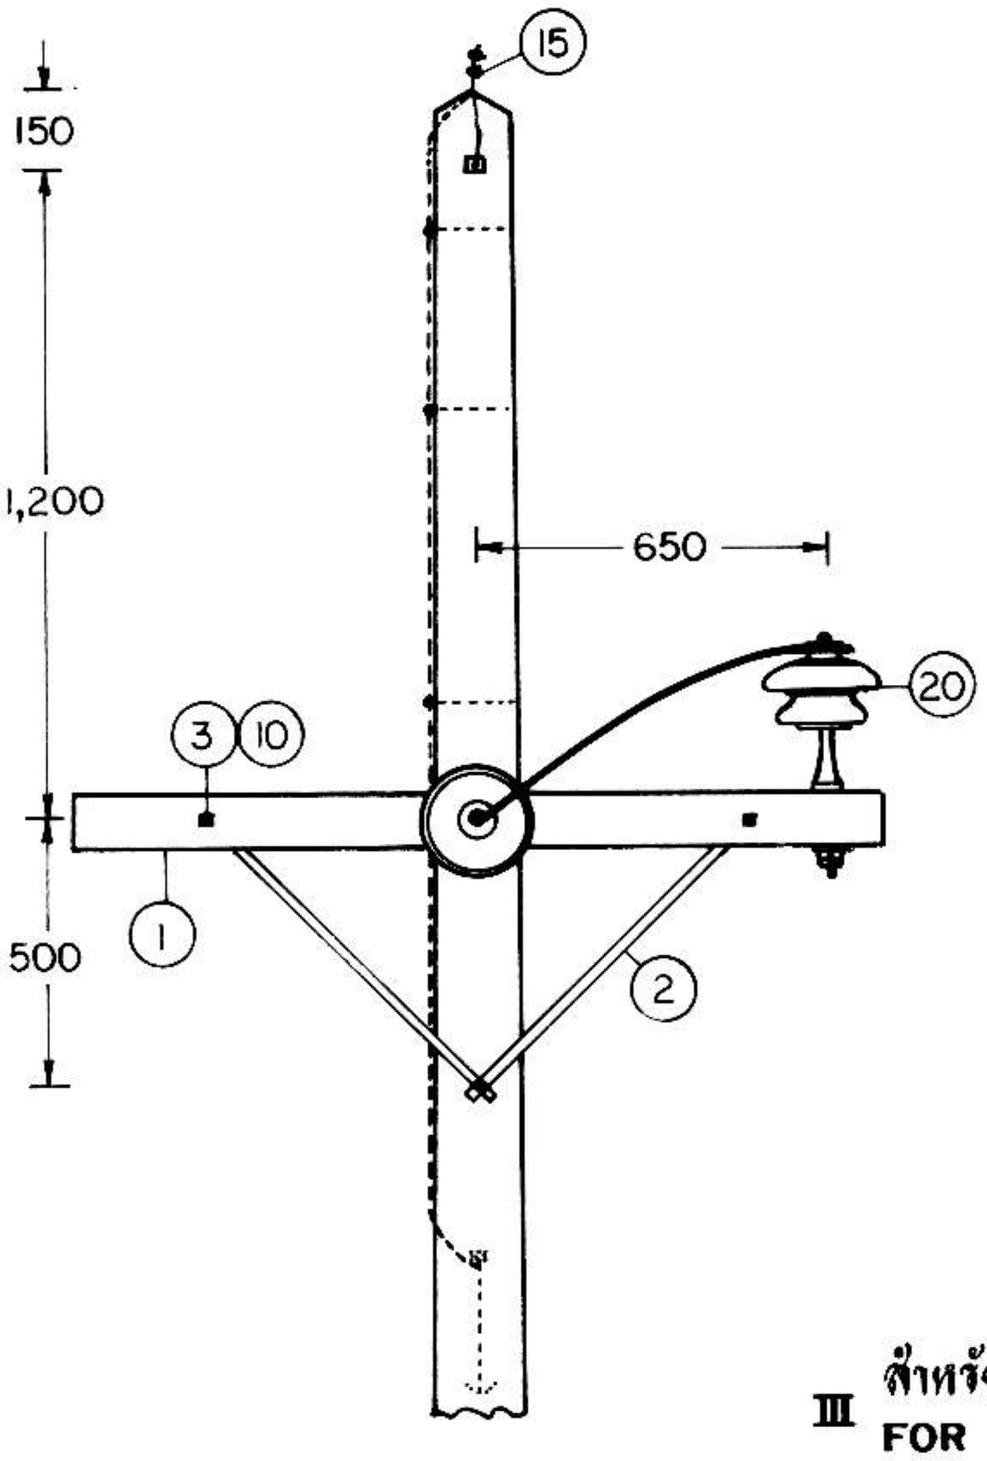

III สำหรับเข้าปลายสายสองข้าง
FOR DOUBLE DEADEND

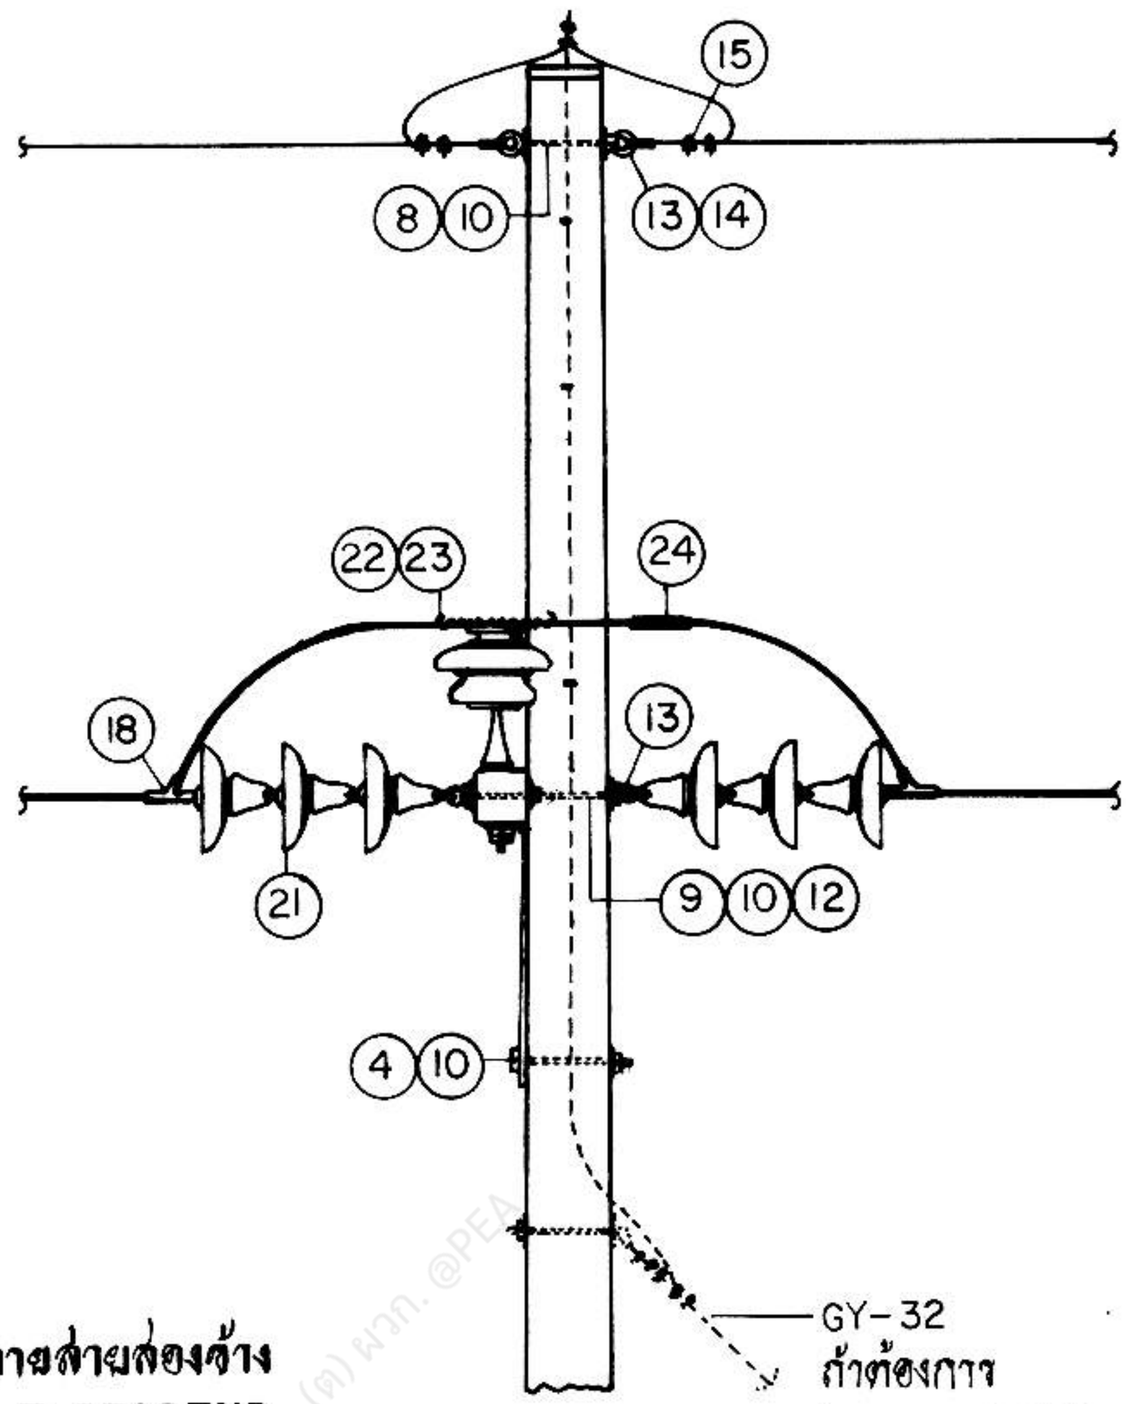

บัญชีวัสดุ
BILL OF MATERIAL

ลำดับที่ ITEM	รายละเอียด DESCRIPTION	จำนวน REQ'D I	II	III	วัสดุเลขที่ MAT. NO.
1	คอน คอร. ขนาด 100 X 100 X 1,500 มม. PRESTRESSED CONCRETE CROSSARM, 100 X 100 X 1,500 mm	1	2	1	01100000 (0106)
2	เหล็กประกับคอน 30 X 6 X 760 มม. BRACE, FLAT FOR CROSSARM 30 X 6 X 760 mm	2	2	2	01200001 (0120)
3	สลักเกลียว M 16 X 130 มม. BOLT, MACHINE M 16 X 130 mm	2	-	2	01110200 (0220)
4	สลักเกลียว M 16 X 200 มม. BOLT, MACHINE M 16 X 200 mm	1	1	1	01110202 (0222)
5	สลักเกลียว M 16 X 300 มม. BOLT, MACHINE M 16 X 300 mm	1	-	-	01110204 (0224)
6	สลักเกลียว M 16 X 450 มม. BOLT, MACHINE M 16 X 450 mm	-	1	-	01110206 (0226)
7	สลักเกลียวตลอด M 16 X 450 มม. BOLT, DOUBLE ARMING M 16 X 450 mm	-	2	-	01030003 (0244)

กองวิศวกรรมไฟฟ้าและเครื่องกล ฝ่ายวิศวกรรม	การไฟฟ้าส่วนภูมิภาค	ใช้แทนแผน ถูกแทนโดยแผน เขียนเสร็จวันที่ 25 พ.ย. 29
ผู้เขียน ผู้สำรวจ วิศวกร หัวหน้าแผนก ผู้อำนวยการกอง ตู้อำนวยการฝ่าย	ผู้ว่าการ 9 เม.ย. 30.	แก้แผนวันที่ มิติเป็น มม. มาตราส่วน 1 : 25
รองผู้ว่าการฝ่ายเทคนิค	การประกอบคอน คอนกรีต กับเสาคอนกรีต 12 ม. ระบบ 1 เฟส 19 kV CONCRETE CROSSARM ASSEMBLY ON 12 m CONCRETE POLE 1-PHASE 19 kV SYSTEM	แผนเลขที่ SAI-015/29023 แผ่นที่ 2 ของจำนวน 4 แผ่น

- 8 เม.ย. 2530

การประกอบเลขที่ ASSEMBLY NO. **3308**

บัญชีวัสดุ
BILL OF MATERIAL

ลำดับที่ ITEM	รายละเอียด DESCRIPTION	จำนวน REQ'D I	II	III	วัสดุเลขที่ MAT.NO.
8	สลักห่วงกลม M 16 X 200 มม. BOLT, ROUND EYE, M 16 X 200 mm	–	–	1	01140001 (0253)
9	สลักห่วงกลม M 16 X 300 มม. BOLT, ROUND EYE, M 16 X 300 mm	–	–	1	01140003 (0255)
10	แหวนสี่เหลี่ยมแบน 52 X 52 X 4.5 มม. รู Ø 18 มม. มอก. 258 WASHER, SQUARE, FLAT 52 X 52 X 4.5 mm HOLE Ø 18 mm TIS 258	5	13	7	01180100 (0355)
11	แหวนสี่เหลี่ยมโค้ง 60 X 60 X 5 มม. รู Ø 22 มม. WASHER, SQUARE, CURVED 60 X 60 X 5 mm HOLE Ø 22 mm	1	2	–	01180201 (0361)
12	แหวนสปริง M 16 มอก. 259 WASHER, LOCK M 16 TIS 259	1	1	1	01180301 (0365)
13	น็อตรูปห่วง M 16 DIN 582 NUT, EYE M 16 DIN 582	–	–	2	01180001 (0345)
14	กายทิมเบิ้ลสำหรับสายยึดโยง 50-95 ต.มม. THIMBLE, GUY, FOR STEEL WIRE 50-95 mm^2	–	–	2	01210304 (0150)
15	ยูแคล้มป์ สลัก 1 ตัว M 8 CLAMP, SINGLE U-BOLT, M 8	3	1	6	01230000 (0165)
16	ลวดเหล็กกลมเส้นผ่านศูนย์กลาง 4 มม. เส้นเดียว (มอก.71) น้ำหนักประมาณ 0.1 กก./ม. WIRE, STEEL, SOLID, DIAMETER 4 mm TIS 71 WEIGHT APPROX. 0.1 kg/m	0.8 ม. m	1.0 ม. m	–	01100000 (0191)
17	ลวดเหล็กตีเกลียว 25 ต.มม. มอก. 404 STEEL STRANDED WIRE 25 mm^2 TIS 404	1.5 ม. m	–	–	01100002 (0181)
18	สเตรนแคล้มป์ สำหรับสายอะลูมิเนียม 35-95 ต.มม. อะลูมิเนียมแกนเหล็ก 35-50 ต.มม. CLAMP, STRAIN FOR Al 35-95 mm^2, ACSR 35-50 mm^2	–	–	2	03110000 03110001
19	กราวด์วายแคล้มป์ สำหรับเสาคอนกรีต GROUND WIRE SUPPORT AND CLAMP, FOR CONCRETE POLE	1	1	–	01230201 (0298)
20	ลูกถ้วยก้านตรง 33 kV (แบบ 56-3) มอก. 279 แบบ ค พร้อมก้าน INSULATOR, PIN TYPE, 33 kV TYPE C (CLASS 56-3) TIS 279 COMP. WITH PIN	1	2	1	03000002 03100001
21	ลูกถ้วยแขวน มอก. 354 แบบ ง (แบบ 52-4) INSULATOR, SUSPENSION TYPE, TIS 354 TYPE D (CLASS 52-4)	–	–	6	03020000 (0415)
22	ลวดอะลูมิเนียมแบน ขนาด 1 X 10 มม. ความยาวตามต้องการ TAPE, ARMOUR, Al 1 X 10 mm LENGTH AS REQUIRED				02200000 (0700)
23	ลวดอะลูมิเนียมกลม ขนาด Ø 4 มม. ความยาวตามต้องการ TIE WIRE, Al Ø 4 mm LENGTH AS REQUIRED				02200002 (0704)
24	หลอดต่อสายชนิดบีบไม่รับแรงดึง สายอะลูมิเนียม 35-95 ต.มม. อะลูมิเนียมแกนเหล็ก 35-50 ต.มม. CONNECTOR, SPLICE, COMPRESSION TYPE, TENSIONLESS Al 35-95 mm^2 ACSR 35-50 mm^2	–	–	1	02410001 – 02410004
25	การประกอบสายยึดโยง GY-32 GUY ASSEMBLY GY-32	–	1	–	

กองวิศวกรรมไฟฟ้าและเครื่องกล
ฝ่ายวิศวกรรม

ผู้เขียน
ผู้สำรวจ
วิศวกร
หัวหน้าแผนก
ผู้อำนวยการกอง
ผู้อำนวยการฝ่าย

รองผู้ว่าการฝ่ายเทคนิค

การไฟฟ้าส่วนภูมิภาค

ผู้ว่าการ

การประกอบคอน คอนกรีต กับเสาคอนกรีต 12 ม.
ระบบ 1 เฟส 19 kV

CONCRETE CROSSARM ASSEMBLY ON 12 m CONCRETE POLE
1-PHASE 19 kV SYSTEM

ใช้แทนแบบ
ถูกแทนโดยแบบ
เขียนเสร็จวันที่ 25 พ.ย. 29
แก้แบบวันที่
มิติเป็น
มาตราส่วน

แบบเลขที่ SAI-015/29023
แผ่นที่ 3 ของจำนวน 4 แผ่น

- 8 เม.ย. 2530

การประกอบเลขที่ ASSEMBLY NO. **3308**

	แบบอ้างอิง REFERENCE DRAWING	แบบเลขที่ DWG. NO.	การประกอบเลขที่ ASSEMBLY NO.
1	ข้อแนะนำในการก่อสร้าง ระบบจำหน่าย 1 เฟส 19 kV CONSTRUCTION SUGGESTION OF 1-PHASE 19 kV SYSTEM	S02-015/20016	3305
2	การประกอบลูกถ้วยกับเสาคอนกรีต ระบบ 1 เฟส 19 kV INSULATOR ASSEMBLY ON CONCRETE POLE 1-PHASE 19 kV SYSTEM		
	2.1 ทางโค้ง 30°-60° ANGLE STRUCTURE 30°-60°	S02-015/20013	3302
	2.2 ทางโค้ง 60°-90° ANGLE STRUCTURE 60°-90°	S02-015/20014	3303
	2.3 สำหรับเข้าปลายสาย DEADEND STRUCTURE	S02-015/20015	3304
3	รายละเอียดการประกอบสายยึดโยง ชุด GY-32 DETAIL OF GUY ASSEMBLY GY-32	SAI-015/20040	8453
4	การประกอบสายลงดินด้วยวิธียึดลวดเหล็ก GROUND LEAD ASSEMBLY STEEL WIRE FITTING	S02-015/19166	9703

อดิวัฒน์ ทองลา พชง.3 ผปร. กฟส.อด. กฟจ.กบ. กฟต.2 สายงาน (ค) ผวก. @PEA

กองวิศวกรรมไฟฟ้าและเครื่องกล ฝ่ายวิศวกรรม	การไฟฟ้าส่วนภูมิภาค	ใช้แทนแบบ ..... ถูกแทนโดยแบบ ..... เขียนเสร็จวันที่ 25 พ.ย. 29
ผู้เขียน ..... ผู้สำรวจ ..... วิศวกร ..... หัวหน้าแผนก ..... ผู้อำนวยการกอง ..... ผู้อำนวยการฝ่าย	ผู้ว่าการ	แก้แบบวันที่ ..... มิติเป็น ..... มาตราส่วน .....
รองผู้ว่าการฝ่ายเทคนิค	การประกอบคอนกรีต กับเสาคอนกรีต 12 ม. ระบบ 1 เฟส 19 kV CONCRETE CROSSARM ASSEMBLY ON 12 m CONCRETE POLE 1-PHASE 19 kV SYSTEM	แบบเลขที่ SAI-015/29023 แผ่นที่ 4 ของจำนวน 4 แผ่น

- 8 เม.ย. 2530