
การประกอบเลขที่ ASSEMBLY NO. 3511

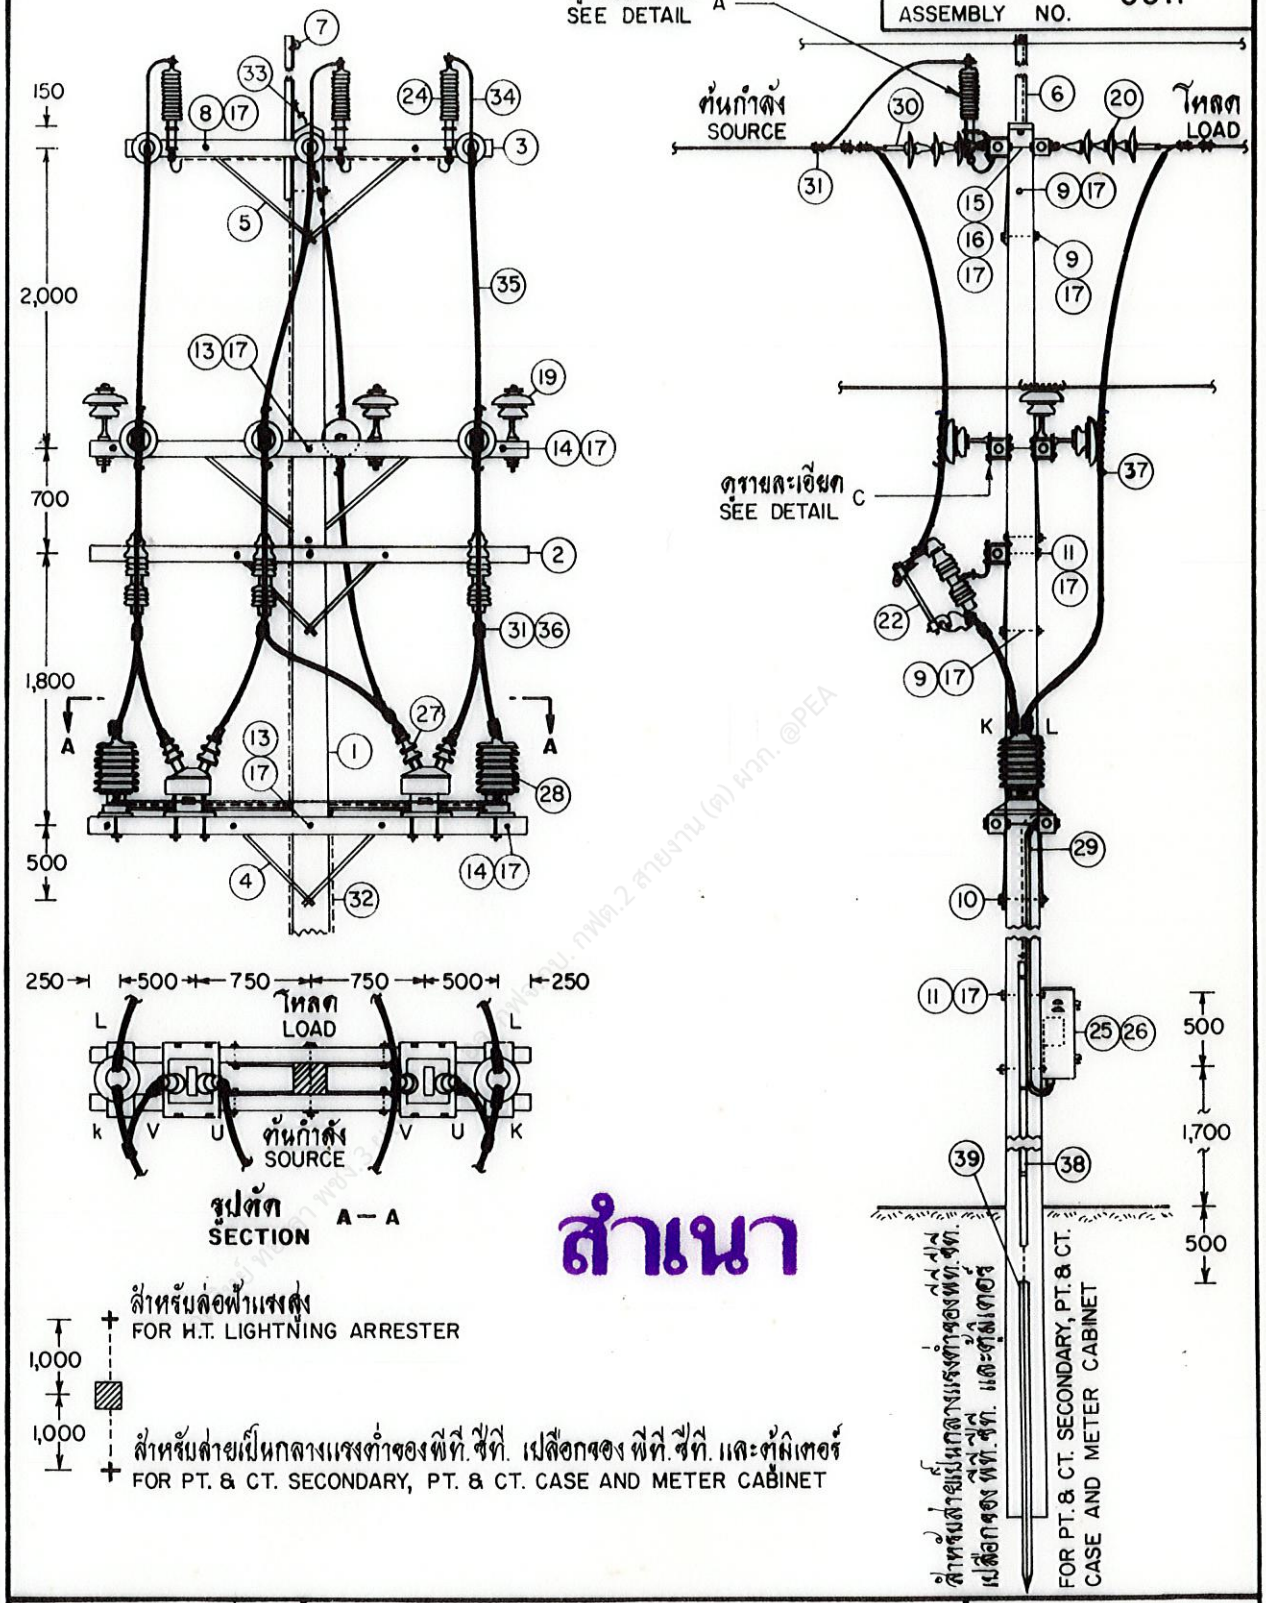

รูปตัด SECTION A — A

สำหรับล่อฟ้าแรงสูง
FOR H.T. LIGHTNING ARRESTER

1,000


1,000

สำหรับสายเป็นกลางแรงต่ำของพีที. ซีที. เปลือกของ พีที. ซีที. และตู้มิเตอร์
FOR PT. & CT. SECONDARY, PT. & CT. CASE AND METER CABINET

สำเนา

กองวิศวกรรมไฟฟ้าและเครื่องกล ฝ่ายวิศวกรรม ผู้เขียน ผู้สำรวจ วิศวกร หัวหน้าแผนก ผู้อำนวยการกอง ผู้อำนวยการฝ่าย รองผู้ว่าการฝ่ายเทคนิค	การไฟฟ้าส่วนภูมิภาค ผู้ว่าการ 4 ธ.ค. 36 การติดตั้งมิเตอร์ 3 เฟส 3 สาย 33 kV ประกอบพีที. และซีที. สำหรับวงจรยนของเส้าคอนกรีต 14 ม. I สำหรับโหลดไม่เกิน 2,000 kVA INSTALLATION OF 33 kV, 3-Ø, 3-W, METER WITH PT. & CT. FOR UPPER FEEDER ON 14 m CONCRETE POLE I FOR LOAD NOT EXCEED 2,000 kVA	ใช้แทนแบบ ถูกแทนโดยแบบ เขียนเสร็จวันที่ 20 ก.ค. 36 แก้แบบวันที่ มิติเป็น มิลลิเมตร มาตราส่วน 1 : 50 แบบเลขที่ SA4-015/36011 แผ่นที่ 1 จากจำนวน 5 แผ่น

การประกอบเลขที่ ASSEMBLY NO. 3511

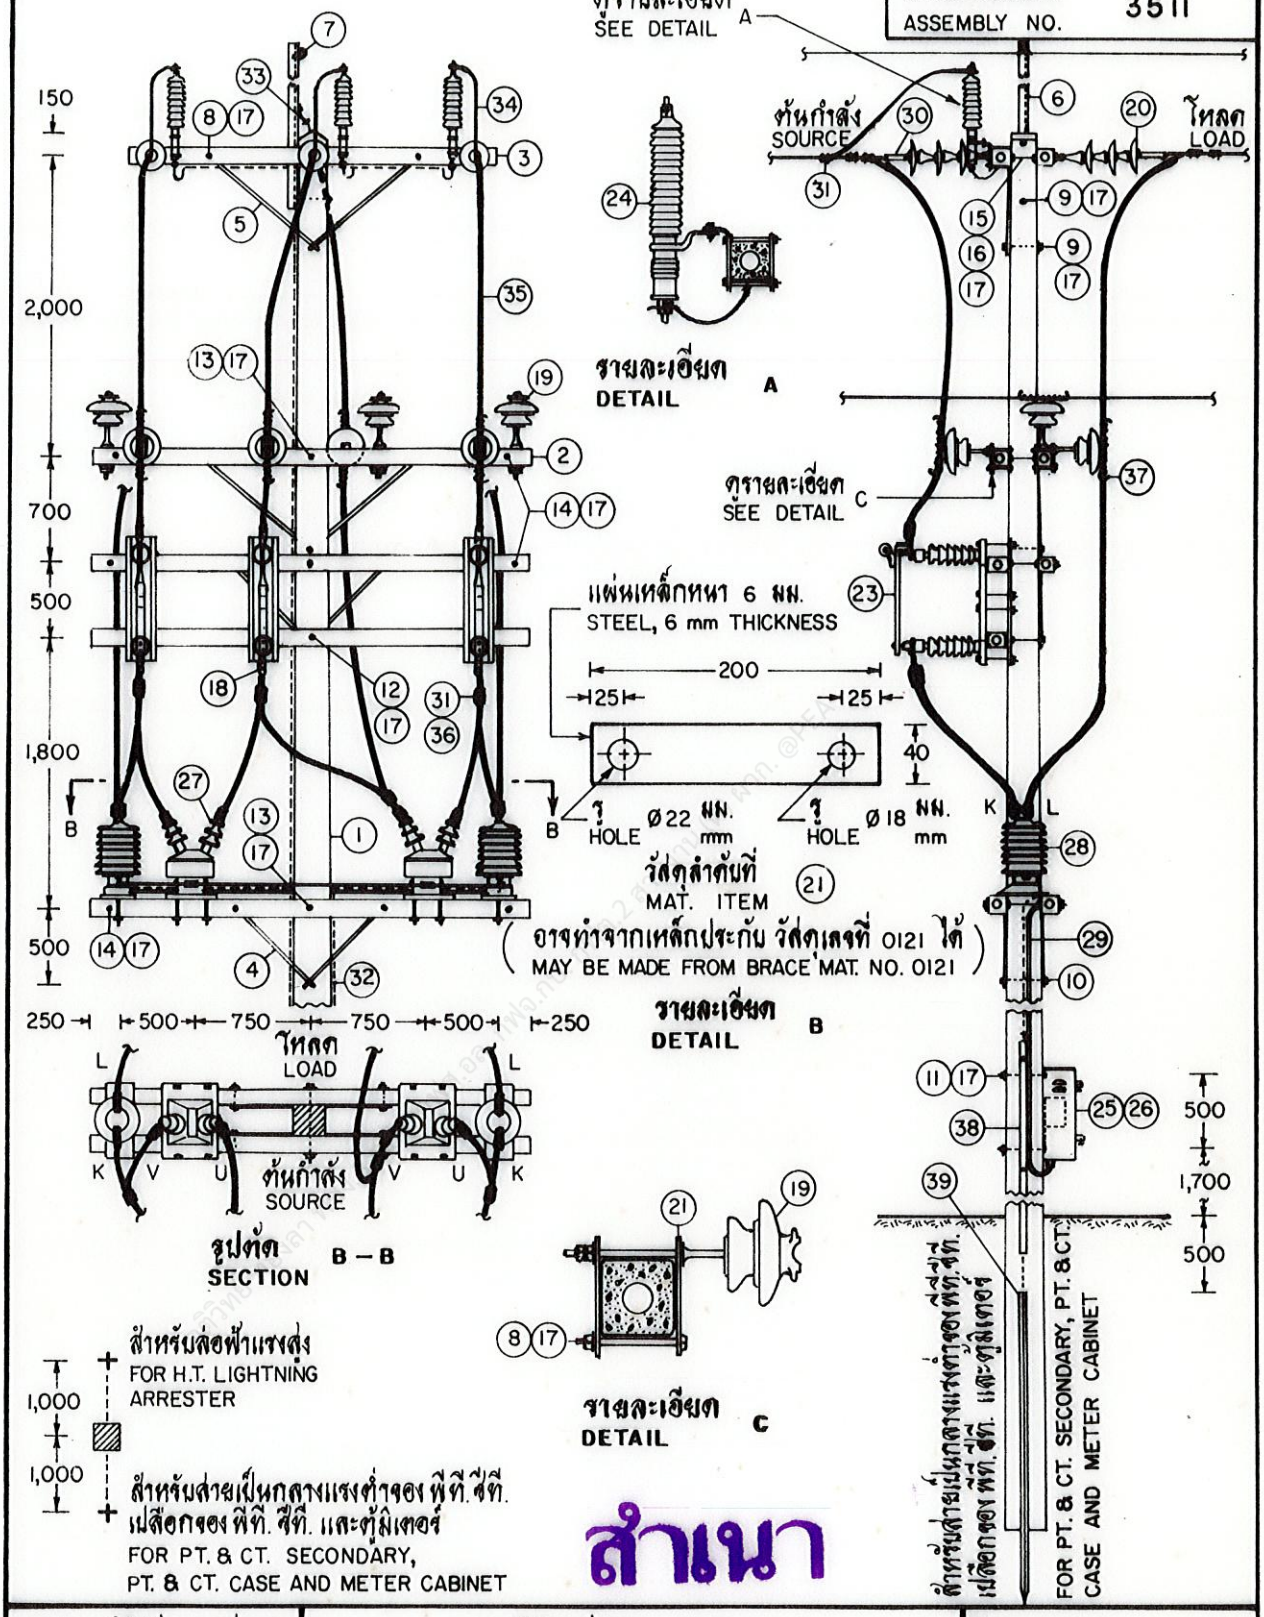

สำเนา

กองวิศวกรรมไฟฟ้าและเครื่องกล ฝ่ายวิศวกรรม	การไฟฟ้าส่วนภูมิภาค	ใช้แทนแบบ
ผู้เขียน ผู้สำรวจ วิศวกร หัวหน้าแผนก ผู้อำนวยการกอง ผู้อำนวยการฝ่าย	ผู้ว่าการ 4 ก.ค. 36	ถูกแทนโดยแบบ เขียนเสร็จวันที่ 20 ก.ค. 36 แก้แบบวันที่ มิติเป็น มิลลิเมตร มาตราส่วน 1 : 50
ของผู้ว่าการฝ่ายเทคนิค	การติดตั้งมิเตอร์ 3 เฟส 3 สาย 33 kV ประกอบพี.ที. และซี.ที. สำหรับวางจรบนเสาคอนกรีต 14 ม. II สำหรับมีโหลดเกินกว่า 2,000 kVA	
	INSTALLATION OF 33 kV, 3-Ø, 3-W, METER WITH PT. & CT. FOR UPPER FEEDER ON 14 m CONCRETE POLE II FOR LOAD EXCEED 2,000 kVA	แบบเลขที่ SA4-015/36011 แผ่นที่ 2 ของจำนวน 5 แผ่น

การประกอบเลขที่ ASSEMBLY NO. 3511

บัญชีวัสดุ BILL OF MATERIAL

ลำดับที่ ITEM	รายละเอียด DESCRIPTION	จำนวน REQ'D I	จำนวน REQ'D II	วัสดุเลขที่ MAT. NO.
1	เสาคอนกรีต 14 ม. POLE, CONCRETE, 14 m LONG	1	1	00010007
2	คอน คอร. สปัน ขนาด 120 X 120 X 3,000 มม. CROSSARM, SPUN, PRESTRESSED CONCRETE, 120 X 120 X 3,000 mm	5	7	00110002
3	คอน คอร. สปัน (สำหรับเข้าปลายสาย) ขนาด 120 X 120 X 2,500 CROSSARM, SPUN, PRESTRESSED (FOR DEADENDING), 120 X 120 X 2,500 mm	2	2	00110004
4	เหล็กประกันคอน 30 X 6 X 760 มม. BRACE, FLAT, FOR CROSSARM, 30 X 6 X 760 mm	6	6	01200001
5	เหล็กประกันคอน 40 X 6 X 1,000 มม. BRACE, FLAT, FOR CROSSARM, 40 X 6 X 1,000 mm	4	4	01200002
6	เหล็กฉากรัยสายล่อฟ้า OVERHEAD GROUND WIRE BAYONET	1	1	01010006 or 01010003
7	กราวด์วายเคลัมป์ แบบ J 1152 GROUND WIRE CLAMP, J 1152	1	1	01230205
8	สลักเกลียว M 16 X 170 มม. BOLT, MACHINE, M 16 X 170 mm	16	16	01110201
9	สลักเกลียว M 16 X 250 มม. BOLT, MACHINE, M 16 X 250 mm	5	4	01110203
10	สลักเกลียว M 16 X 300 มม. BOLT, MACHINE, M 16 X 300 mm	1	1	01110204
11	สลักเกลียว M 16 X 350 มม. BOLT, MACHINE, M 16 X 350 mm	3	2	01110205
12	สลักเกลียว M 16 X 400 มม. BOLT, MACHINE, M 16 X 400 mm	–	1	01110206
13	สลักเกลียว M 16 X 500 มม. BOLT, MACHINE, M 16 X 500 mm	2	3	01110208
14	สลักเกลียวตลอด M 16 X 500 มม. BOLT, DOUBLE ARMING, M 16 X 500 mm	4	6	01120002
15	สลักเกลียวห่วงกลม M 16 X 500 มม. BOLT, DOUBLE ARMING, ROUND EYE, M 16 X 500 mm	3	3	01130002
16	นัทรูปห่วง M 16 DIN 582 NUT, EYE, M 16, DIN 582	3	3	01180001
17	แหวนสี่เหลี่ยมแบน 52 X 52 X 4.5 มม. รู Ø 18 มม. มอก. 258 WASHER, SQUARE, FLAT, 52 X 52 X 4.5 mm, HOLE Ø 18 mm, TIS 258	57	65	01180100
18	หางปลาเจาะรูตามมาตรฐาน NEMA สำหรับสายอะลูมิเนียม 120-185 ต.มม. CONNECTOR (OR LUG), TERMINAL, NEMA HOLE, COMPRESSION TYPE, Al, 120-185 mm^2	–	6	02420105 02420106
19	ลูกถ้วยก้านตรง 33 kV มอก. 279 แบบ ค (แบบ 56-3) พร้อมก้าน INSULATOR, PIN TYPE, 33 kV, TIS 279, TYPE C (CLASS 56-3); COMP. WITH PIN	9	9	03000002 03100001
20	ลูกถ้วยแขวน มอก. 354 แบบ ง (แบบ 52-4) INSULATOR, SUSPENSION TYPE, TIS 354, TYPE D (CLASS 52-4)	18	18	03020002

สำเนา

กองวิศวกรรมไฟฟ้าและเครื่องกล ฝ่ายวิศวกรรม	การไฟฟ้าส่วนภูมิภาค	ใช้แทนแบบ
ผู้เขียน ปิยะ ผู้สำรวจ วิศวกร หัวหน้าแผนก ผู้อำนวยการกอง ผู้อำนวยการฝ่าย	ผู้ว่าการ 4 มิ.ย. 36	ถูกแทนโดยแบบ เขียนเสร็จวันที่ 20 ก.ค. 36 แก้แบบวันที่ มิติเป็น มาตราส่วน
รองผู้ว่าการฝ่ายเทคนิค	การติดตั้งมิเตอร์ 3 เฟส 3 สาย 33 kV ประกอบซี.ที. และซี.ที. สำหรับวงจรบนของเสาคอนกรีต 14 ม. INSTALLATION OF 33 kV, 3-Ø, 3-W, METER WITH PT. & CT. FOR UPPER FEEDER ON 14 m CONCRETE POLE	แบบเลขที่ SA4-015/36011 แผ่นที่ 3 ของจำนวน 5 แผ่น

การประกอบเลขที่ ASSEMBLY NO. 3511

บัญชีวัสดุ BILL OF MATERIAL

ลำดับที่ ITEM	รายละเอียด DESCRIPTION	จำนวน REQ'D I	จำนวน REQ'D II	วัสดุเลขที่ MAT. NO.
21	แผ่นเหล็ก 40 X 6 มม. ยาว 200 มม. เจาะรูตามรายละเอียด B STEEL PLATE, 40X 6 mm, 200 mm LONG; PUNCH HOLE AS DETAIL B	12	12	——
22	คัตเอาต์ ฟิวส์คัตเอาต์ หนึ่งอินซูเลเตอร์ 33 kV, 100 A CUTOUT, FUSE, OPEN TYPE, SINGLE INSULATOR, DROPOUT, 33 kV, 100 A	3	–	04010100
23	สวิตช์ตัดตอนชนิดตากหนึ่งขั้ว 33 kV 600 แอมป์ ชนิดติดตั้งในระบบจำหน่าย SWITCH, DISCONNECTING, SINGLE POLE, 33 kV, 600 A, DISTRIBUTION CLASS	–	3	04050100
24	ล่อฟ้าแรงสูง 30 kV, 5 kA LIGHTNING ARRESTER, 30 kV, 5 kA	3	3	04000100
25	ดีมานด์มิเตอร์ ชนิดสะสม 3 เฟส 3 สาย 110 โวลต์ 5 แอมป์ DEMAND METER, CUMULATIVE, 3-Ø, 3-W, 110 V, 5 A	1	1	06000300
26	ตู้โลหะมิเตอร์แรงสูง พร้อมแป้นไม้ ALUMINIUM METER CABINET, FOR H.T. METER; COMP. WITH METER PLATE	1	1	06100007 06100001
27	พี.ที. หนึ่งเฟส ใช้นอกอาคาร 33,000/110 V พร้อมอุปกรณ์ติดตั้ง TRANSFORMER, POTENTIAL, 1-Ø, OUTDOOR, 33,000/110 V; COMP. WITH MOUNT. ACCESS.	2	2	06020100
28	ซี.ที. ใช้นอกอาคาร 33 kV เรโชตามต้องการ พร้อมอุปกรณ์ติดตั้ง TRANSFORMER, CURRENT, OUTDOOR, 33 kV, RATIO AS REQUIRED, COMP. WITH MOUNT. ACCESS.	2	2	06040101_ 06040104
29	คอนโทรลเคเบิล ขนาด 7 X 2.5 ต.มม. CONTROL CABLE, SIZE 7 X 2.5 mm^2	10 ม. m	9.5 ม. m	02080402
30	สเตรนแคล้มป์ สำหรับสายอะลูมิเนียม ขนาดตามต้องการ CLAMP, STRAIN, FOR Al, SIZE AS REQUIRED	6	6	03110002_ 03110004
31	พี.จี. คอนเน็คเตอร์ 3 สลัก สำหรับสายอะลูมิเนียม ขนาดตามต้องการ CONNECTOR, PARALLEL GROOVE, TRIPLE BOLTS, Al; SIZE AS REQUIRED	20	20	02300102_ 02300103
32	ลวดเหล็กตีเกลียว 50/7 ต.มม. มอก. 404 WIRE, STEEL STRANDED, 50/7 mm^2, TIS 404	30 ม. m	30 ม. m	01100004
33	ยูแคล้มป์ สลัก 1 ตัว M 8 CLAMP, SINGLE U-BOLT, M 8	9	9	01230000
34	สายอะลูมิเนียมหุ้มฉนวน ใช้ภายนอก 750 V, 75° C ขนาด 35-95 ต.มม. CONDUCTOR, INSULATED, WEATHER-PROOF, 750 V, 75° C, Al, 35-95 mm^2	4 ม. m	4 ม. m	02070001 or 02070004
35	เคเบิลอากาศอะลูมิเนียม 33 kV ขนาดตามต้องการ CABLE, AERIAL, Al, 33 kV SIZE AS REQUIRED	29 ม. m	29 ม. m	02050101_ 02050104
36	เทปพันเคเบิลอากาศแรงสูง ขนาด 3/4" X 30' ELECTRICAL, SPLICING TAPE, FOR H.T. AERIAL CABLE, SIZE 3/4" X 30'	ม้วน roll	ม้วน roll	02180003
37	ลวดอะลูมิเนียมกลม Ø 4 มม. ความยาวตามต้องการ TIE WIRE, Al, Ø 4 mm, LENGTH AS REQUIRED	ม. m	ม. m	02200002
38	ท่อ PVC แข็ง ขนาด Ø 20 X 2,500-4,000 มม. พร้อมอุปกรณ์ยึด CONDUIT, PVC RIGID, Ø 20 X 2,500-4,000 mm; COMP. WITH FIXING ACCESS.	2	2	08040002 08040001 or
39	หลักดิน 60 X 60 X 5 มม. ยาว 2 ม ROD, GROUND, 60 X 60 X 5 mm, 2 m LONG	2	2	01220002

สำเนา

กองวิศวกรรมไฟฟ้าและเครื่องกล ฝ่ายวิศวกรรม

ผู้เขียน ..... ผู้สำรวจ ..... วิศวกร ..... หัวหน้าแผนก ..... ผู้อำนวยการกอง ..... ผู้อำนวยการฝ่าย .....

ของผู้ว่าการฝ่ายเทคนิค .....

การไฟฟ้าส่วนภูมิภาค

ผู้ว่าการ ..... 4 ก.ย. 36

การติดตั้งมิเตอร์ 3 เฟส 3 สาย 33 kV ประกอบพี.ที. และซี.ที. สำหรับวงจรบนของเสาคอนกรีต 14 ม.

INSTALLATION OF 33 kV, 3-Ø, 3-W, METER WITH PT. & CT. FOR UPPER FEEDER ON 14 m CONCRETE POLE

ผู้ใช้แทนแบบ .....
ถูกแทนที่โดยแบบ .....
เขียนเสร็จวันที่ 20 ก.ค. 36
แก้ไขวันที่ .....
ลิขิตเป็น .....
มาตราส่วน .....

แบบเลขที่ SA4-015/36011
แผ่นที่ 4 ของจำนวน 5 แผ่น

การประกอบเลขที่ ASSEMBLY NO.	3511

	แบบอ้างอิง REFERENCE DRAWING	แบบเลขที่ DWG. NO.	การประกอบเลขที่ ASSEMBLY NO.
1	แผนผังการต่อมิเตอร์แรงสูง 3 เฟส 3 สาย 11-33 kV CONNECTION DIAGRAM OF 3-PHASE, 3-WIRE H.T. METER, 11-33 kV	S02-015/16005	0506
2	การต่อลงดินระบบแรงสูง และแรงต่ำ แผ่นที่ 15 และ 17 H.T. AND L.T. EARTHING SYSTEM, SHEET NO. 15 AND 17	S02-015/20039	9701
3	การประกอบสายดินวิธียึดลวดเหล็ก GROUND LEAD ASSEMBLY, STEEL WIRE FITTING	S02-015/19166 SAI-015/31012	9703 9703 A
4	การประกอบที่ยึดท่อ PVC สำหรับสายดิน PVC PIPE FITTING ASSEMBLY FOR GROUND WIRE	S02-015/19128 SAI-015/31013	9704 9704 A

ข้อแนะนำ

เมื่อติดตั้งมิเตอร์ตามแบบแผ่นที่ 2 แล้ว หากมีความผิดพร่องเกิดขึ้นในระบบจำหน่าย ภายในบริเวณของผู้ใช้ไฟบ่อยๆ ก็ให้แจ้ง กวจ. เพื่อพิจารณาดำเนินการต่อไป

SUGGESTION

AFTER THE METER WAS INSTALLED AS PER THE DRAWING IN SHEET NO. 2 ; IF THE DISTRIBUTION LINE IN CUSTOMER'S AREA HAS MANY FAULTS, IT SHALL BE REQUESTED TO REPORT TO RESEARCH DIVISION FOR CONSIDERATION .

คำเตือน

ในการติดตั้งตู้ใส่มิเตอร์ ให้ดำเนินการตามมาตรการ และวิธีปฏิบัติเกี่ยวกับการละเมิดสิทธิการใช้ไฟฟ้า โดยการเอียงมิเตอร์ ตามมันทึกที่ ผต. 2145 ลว. 31 พ.ค. 2528 (อนุมัติ ผวก. ลว. 28 พ.ค. 2528) ดังนี้ :

(1) การยึดแป้นไม้ของมิเตอร์ และตู้ใส่มิเตอร์ ให้ยึดด้วยสลักเกลียว 2 ชุด โดยให้น็อตของสลักเกลียวอยู่ในตู้

(2) ให้เจาะรูร้อยลวดตีตราตะกั่วที่ปลายสลัก ตามข้อ (1) ทั้ง 2 ชุด

(3) ให้ร้อยลวดตีตราตะกั่วที่ฝาตู้ใส่มิเตอร์ทั้ง 2 ชุด

หมายเหตุ

1. การติดตั้งชุดเครื่องวัดแรงสูงตามแบบแผ่นที่ 2 ใช้กับผู้ใช้ไฟที่ติดตั้งหม้อแปลงรวมกัน เกินกว่า 2,000 kVA แต่ไม่ส่งควรเกิน 8,000 kVA

2. การติดตั้งชุดเครื่องวัดแรงสูงวงจรล่าง ให้ดำเนินการตามแบบเลขที่ SAI-015/29005 และแบบเลขที่ SAI-015/34011 (การประกอบเลขที่ 3506 และ 3507) โดยเพิ่มความยาวของสลักเกลียวตามแบบนี้

NOTES

1. H.T. METER INSTALLATION AS PER THE DRAWING IN SHEET NO. 2 IS USED FOR CUSTOMER'S TRANSFORMER EXCEED 2,000 kVA, BUT SHOULD NOT EXCEED 8,000 kVA .

2. H.T. METER FOR LOWER FEEDER SHALL BE INSTALLED AS PER DWG. NO. SAI-015/29005 AND DWG. NO. SAI-015/34011 (ASSEMBLY NO. 3506 AND 3507) BY INCREASING THE LENGTH OF BOLT AS PER THIS DRAWING .

สำเนา

กองวิศวกรรมไฟฟ้าและเครื่องกล ฝ่ายวิศวกรรม ผู้เขียน ผู้สำรวจ วิศวกร หัวหน้าแผนก ผู้อำนวยการกอง ผู้อำนวยการฝ่าย รองผู้ว่าการฝ่ายเทคนิค	การไฟฟ้าส่วนภูมิภาค ผู้ว่าการ การติดตั้งมิเตอร์ 3 เฟส 3 สาย 33 kV ประกอบพีที. และซีที. สำหรับวงจรของเสาคอนกรีต 14 ม. INSTALLATION OF 33 kV, 3-Ø, 3-W, METER WITH PT. & CT. FOR UPPER FEEDER ON 14 m CONCRETE POLE	ใช้แทนแบบ ถูกแทนโดยแบบ เขียนเสร็จวันที่ 20 ก.ค. 36 แก้แบบวันที่ มิติเป็น มาตราส่วน แบบเลขที่ SA4-015/36011 แผ่นที่ 5 ของทั้งหมด 5 แผ่น