การประกอบเลขที่
ASSEMBLY NO. 3211

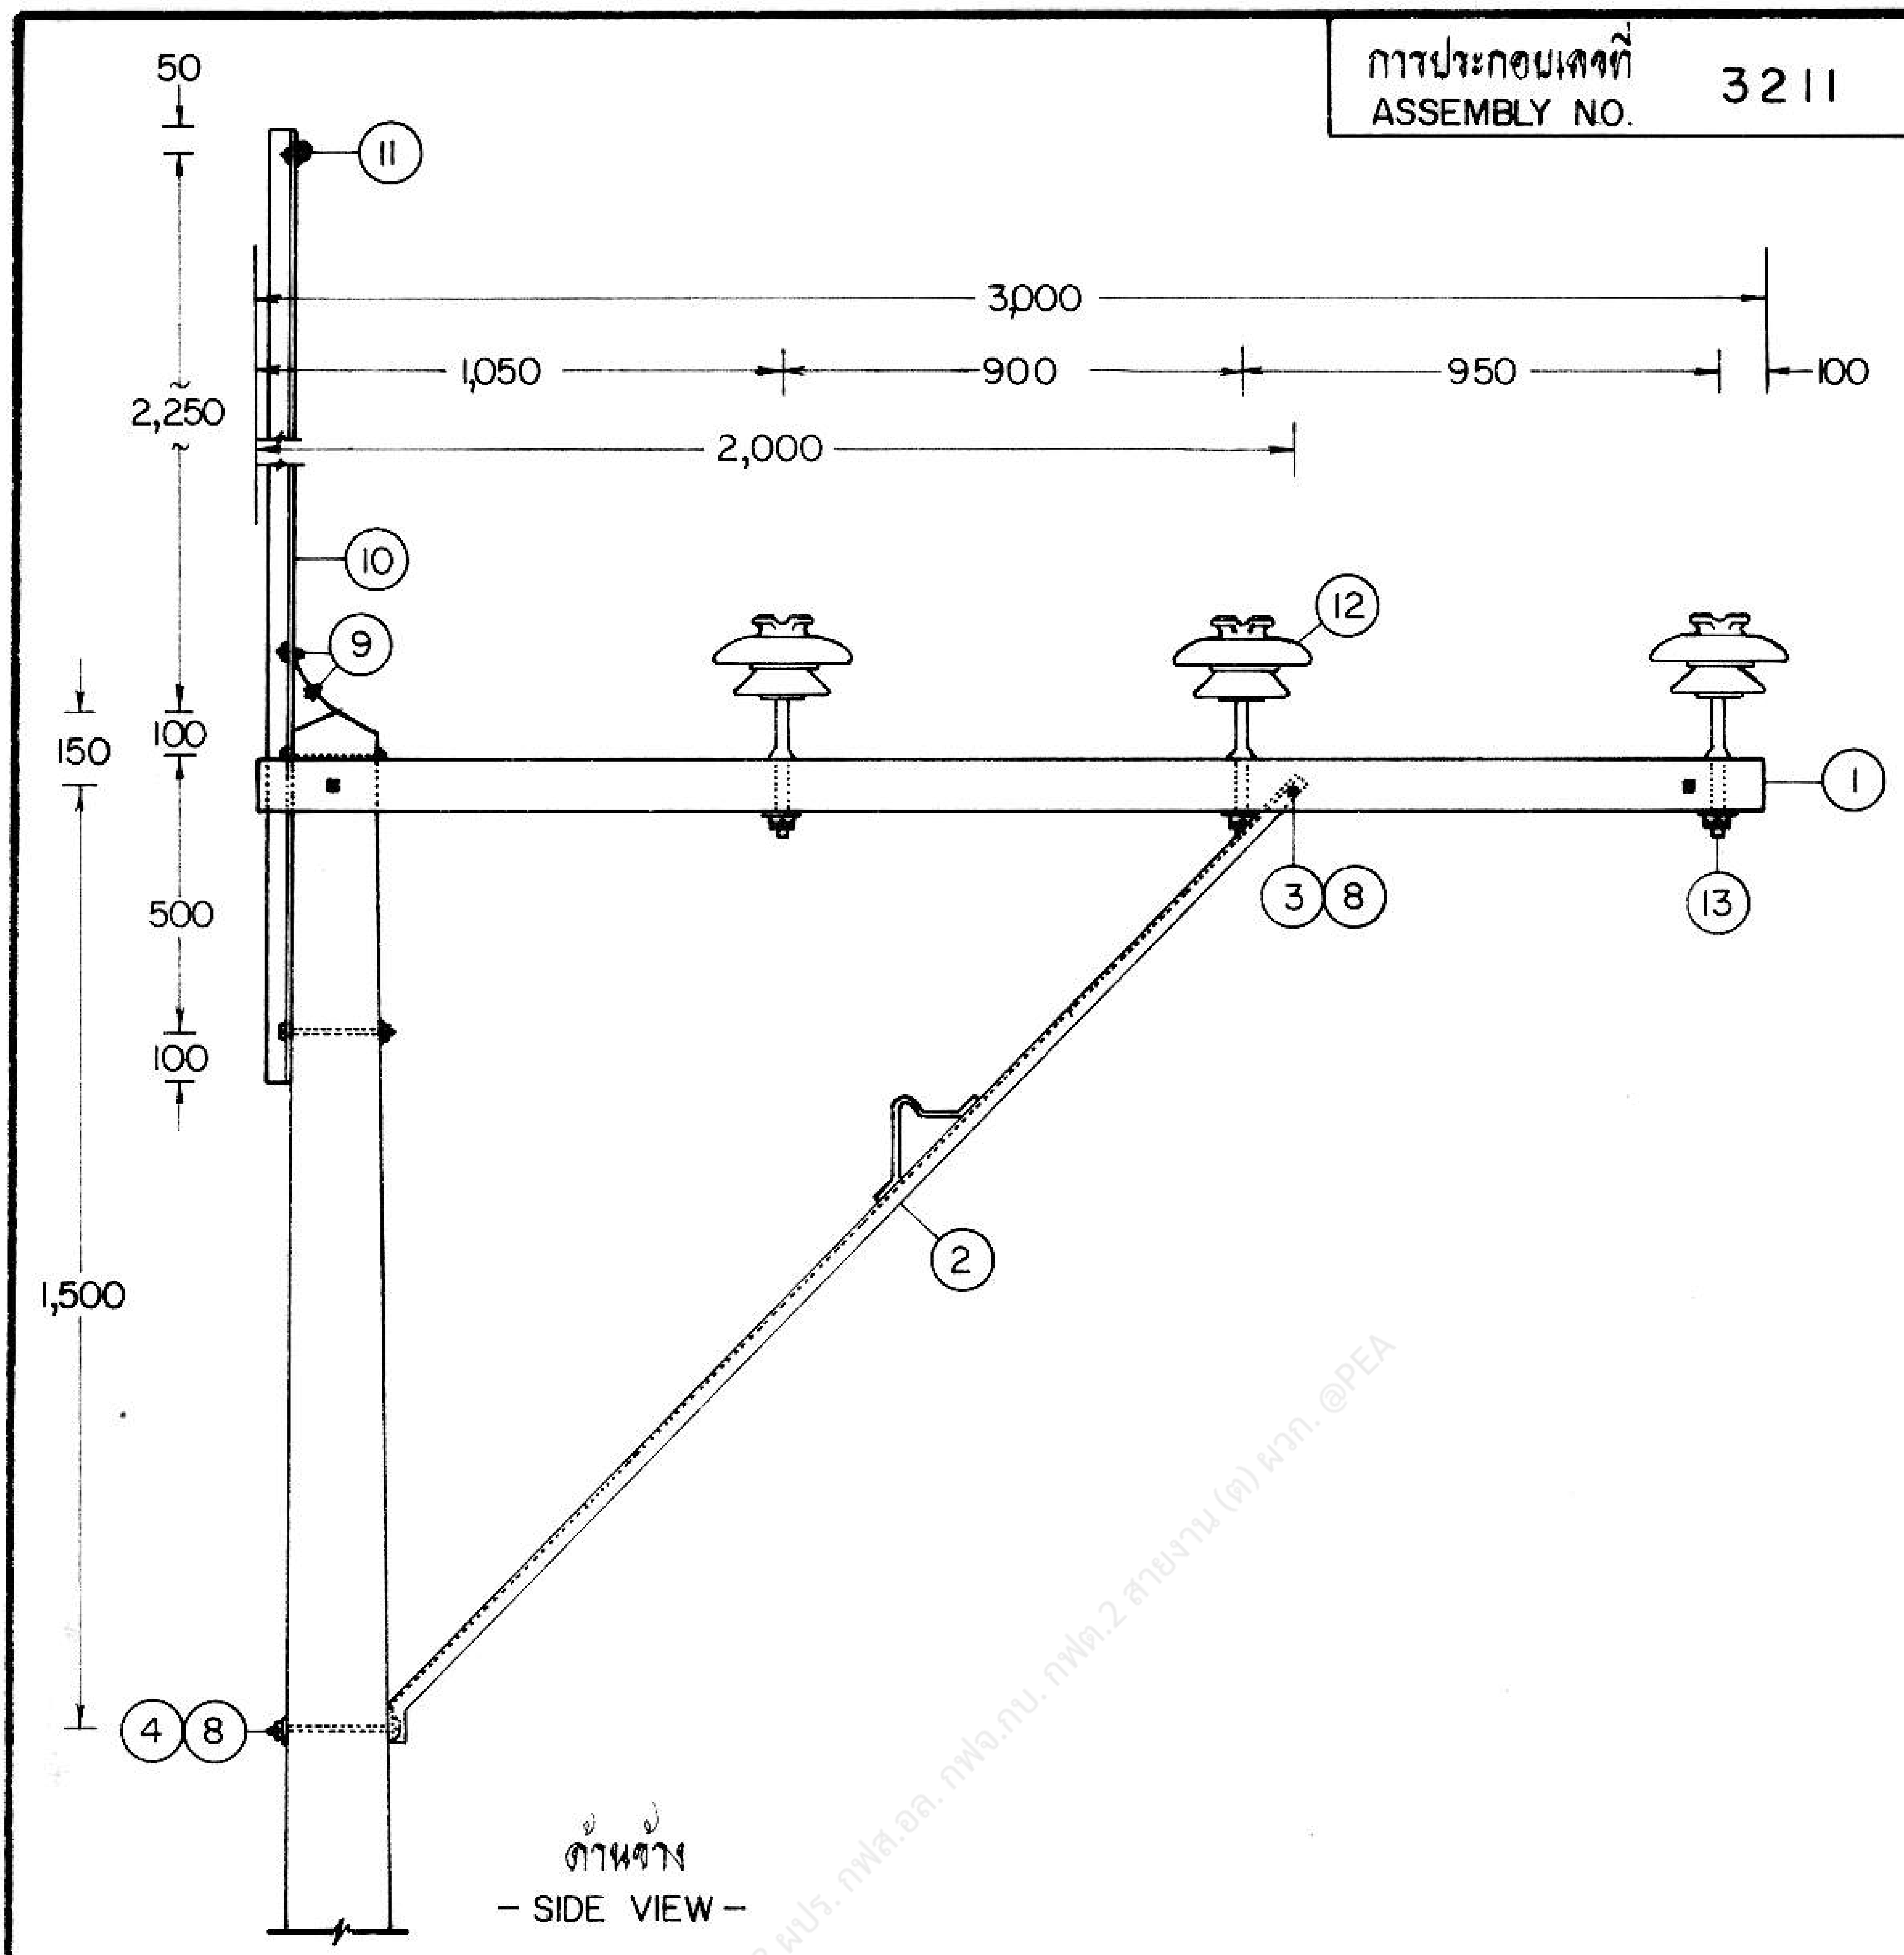

ด้านข้าง
- SIDE VIEW -

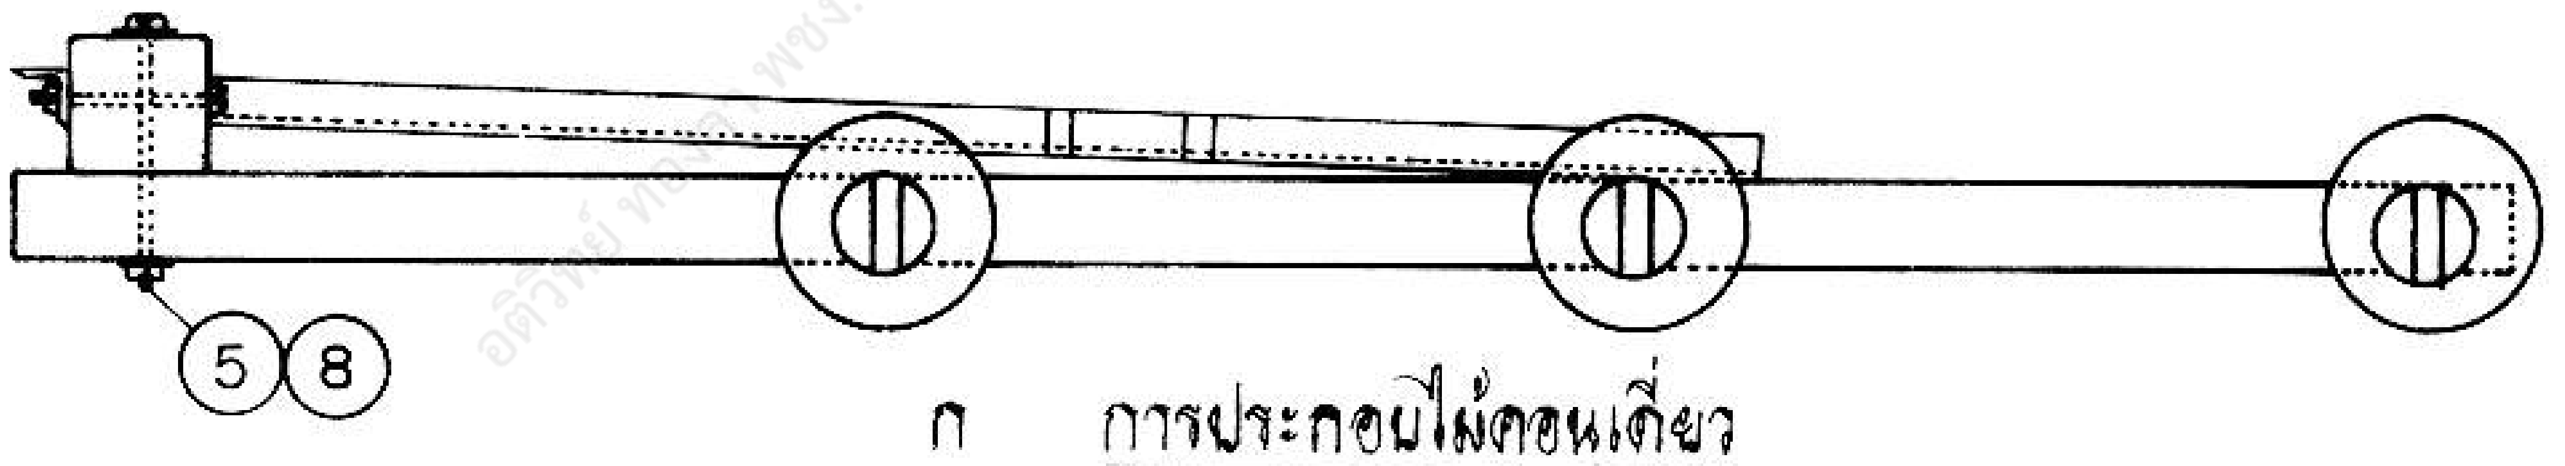

ก การประกอบไม้คอนเดี่ยว
A SINGLE CROSSARM ASSEMBLY

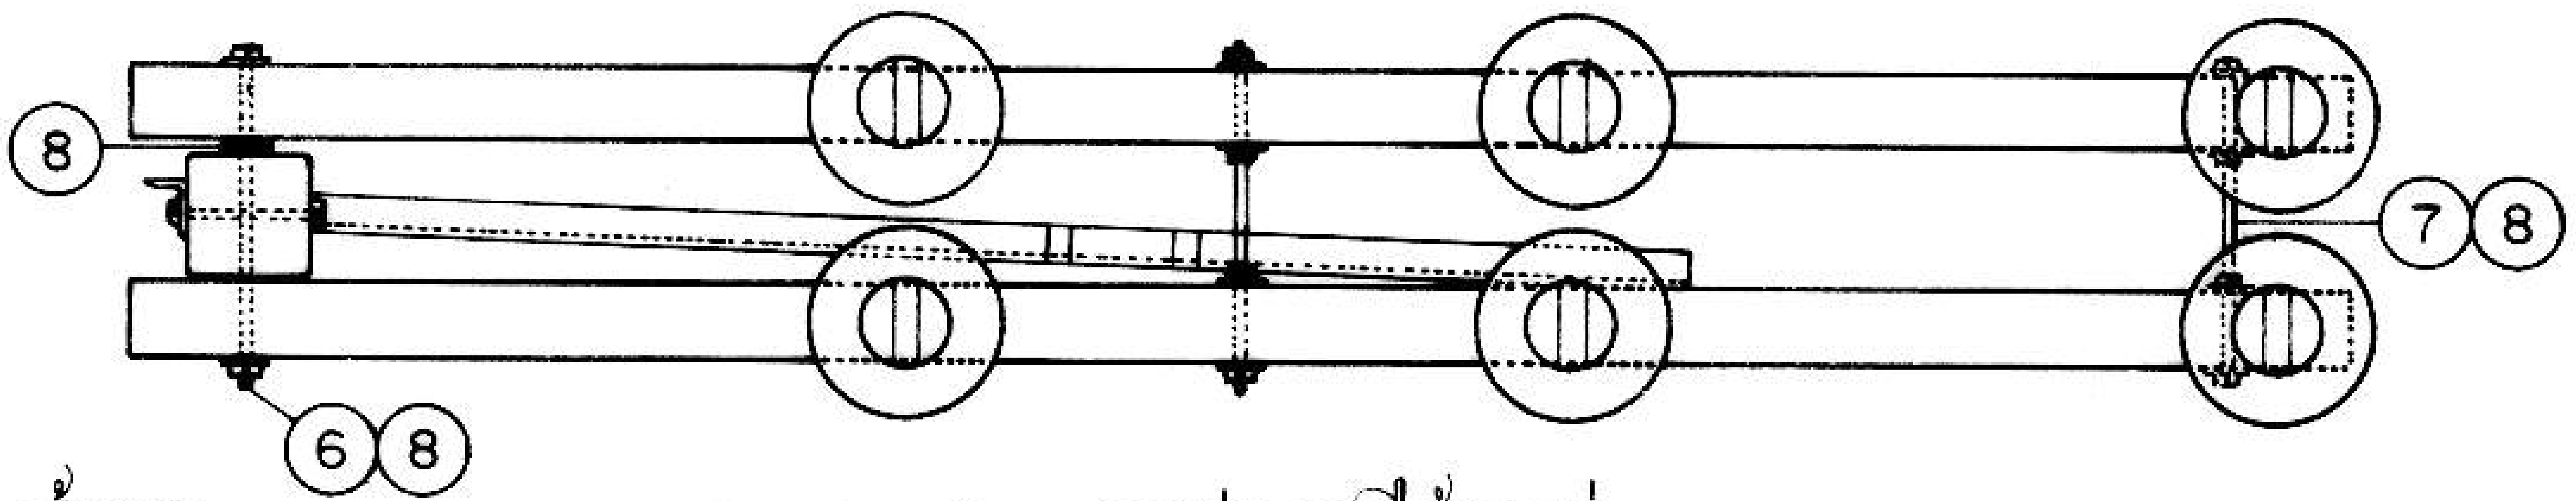

ด้านบน
- TOP VIEW -

ข การประกอบไม้คอนคู่
B DOUBLE CROSSARM ASSEMBLY

อติวิทย์ ทอง[illegible] พชง.3 ผปร. กฟส.อล. กฟจ.กบ. กฟต.2 สายงาน (ต) ผวก. @PEA

กองวิศวกรรมและวางแผน

ผู้เขียน
สถาปนิก
วิศวกร
หัวหน้าแผนก
ผู้อำนวยการกอง

รองผู้ว่าการฝ่ายเทคนิค

การไฟฟ้าส่วนภูมิภาค

ผู้ว่าการ

การประกอบเหล็กประกับไม้คอนแบบท้าวแขน
ระบบ 33 kV ไม้คอนเดี่ยว และ ไม้คอนคู่

ALLEY ARM ASSEMBLY 33 kV
SINGLE CROSSARM & DOUBLE CROSSARM

ใช้แทนแบบ
ถูกแทนโดยแบบ
เขียนเสร็จวันที่ 21 ส.ค. 13
แก้แบบวันที่ 24 ก.ค. 24
มิติเป็น มม
มาตราส่วน 1 : 25

แบบเลขที่ 150/015/130319
แผ่นที่ 1 ของจำนวน 2 แผ่น

การประกอบเลขที่
ASSEMBLY NO. 3211

BILL OF MATERIAL

ITEM	DESCRIPTION	RQE'D A	RQE'D B	MAT. NO.
1	ไม้คอนสาย แรงสูง ขนาด 100 X 120 X 3000 มม. CROSSARM (HT.) WOOD, 100 X 120 X 3000 mm	1	2	00100003 (0101)
2	เหล็กประกับไม้คอนแบบท้าวแขน 50 X 50 X 5 มม. ยาว 2350 มม. BRACE, ALLEY ARM 50X50X5 mm, 2350 mm LONG	1	1	01200005 (0125)
3	สลักเกลียว M 16 X 130 มม. BOLT, MACHINE, M 16 X 130 mm	1	1	01110200 (0220)
4	สลักเกลียว M 16 X 250 มม. BOLT, MACHINE, M16 X 250 mm	3	3	01110203 (0223)
5	สลักเกลียว M 16 X 300 มม. BOLT, MACHINE, M16X300 mm	1	–	01110204 (0224)
6	สลักเกลียว M 16 X 450 มม. BOLT, MACHINE M16 X 450 mm	–	1	01110207 (0227)
7	สลักเกลียวตลอด M 16 X 450 มม. BOLT, DOUBLE ARMING M16 X 450 mm	–	2	01120001 (0244)
8	แหวนเหลี่ยมแบน ขนาด 52 X 52 X 4.5 มม. ขนาดรู Ø 18 มม. มอก. 258 WASHER, SQUARE FLAT, 52X52X4.5 mm HOLE Ø18 mm TIS 258	6	18	01180100 (0355)
9	ยู-แคล้มป์สลัก 1 ตัว M 8 (ไวร์โรปคลิ๊พ) CLAMP, SINGLE U-BOLT M 8 (WIRE ROPE CLIP)	2	2	01230000 (0165)
10	เหล็กฉากรับสายล่อฟ้า OVERHEAD GROUND WIRE BAYONET	1	1	01010006 (0128)
11	กราวด์ไวร์แคล้มป์แบบ J 1152 GROUND WIRE CLAMP J 1152	1	1	01230205 (0296)
12	ลูกถ้วยก้านตรง 33 kV มอก. 279 แบบ ค (แบบ 56-3) INSULATOR, PIN TYPE, 33kV TIS 279 TYPE C (CLASS 56-3)	3	6	03000002 (0409)
13	ก้านลูกถ้วย 33 kV PIN, INSULATOR	3	6	03100001 (0422)

กองวิศวกรรมและวางแผน	**การไฟฟ้าส่วนภูมิภาค**	ใช้แทนแบบ.....
ผู้เขียน.....	ผู้ว่าการ.....	ถูกแทนโดยแบบ.....
สถาปนิก.....		เขียนเสร็จวันที่ 21 ส.ค. 13
วิศวกร.....	การประกอบเหล็กประกับไม้คอนแบบท้าวแขน ระบบ 33 kV ไม้คอนเดี่ยว และ ไม้คอนคู่	แก้แบบวันที่ 24 ก.ค. 24
หัวหน้าแผนก.....		มิติเป็น มม.
ผู้อำนวยการกอง.....		มาตราส่วน.....
รองผู้ว่าการฝ่ายเทคนิค 18 ก.ค. 2513	ALLEY ARM ASSEMBLY 33 kV SINGLE CROSSARM & DOUBLE CROSSARM	แบบเลขที่ I50-015/130319 แผ่นที่ 2 ของจำนวน 2 แผ่น