การประกอบเลขที่
ASSEMBLY NO. 0304

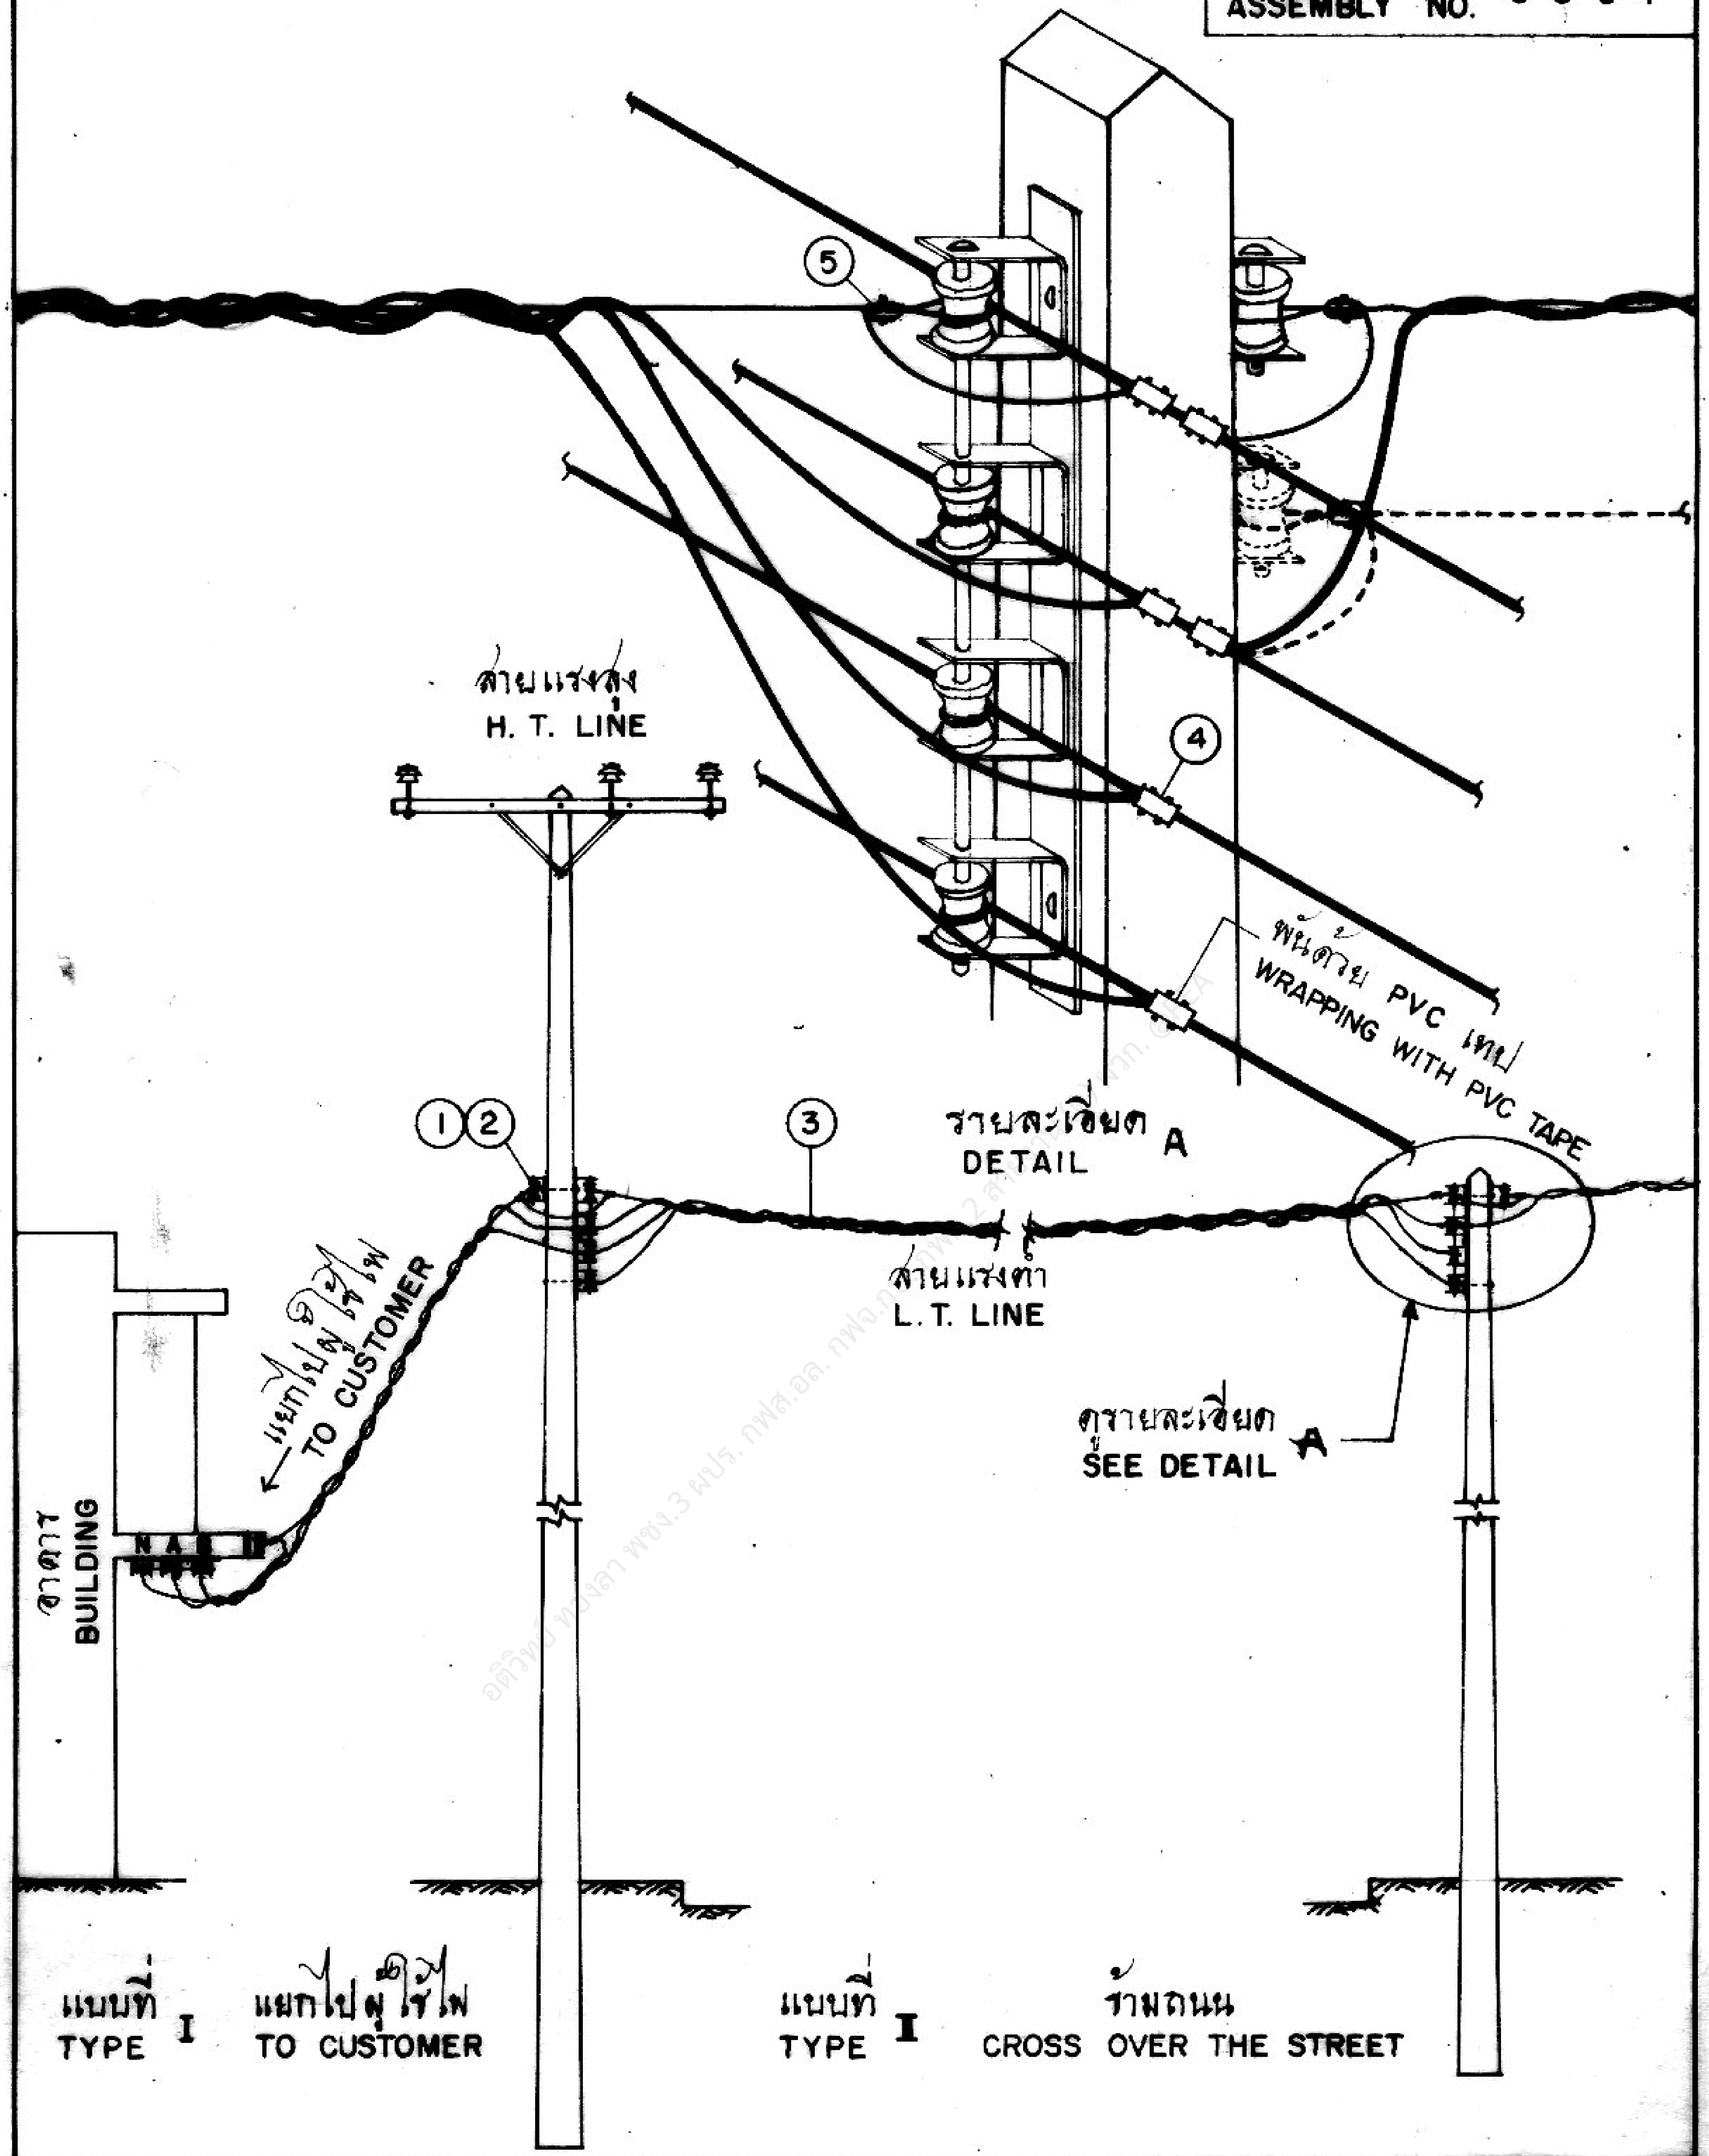

แบบที่ I แยกไปผู้ใช้ไฟ
TYPE I TO CUSTOMER

แบบที่ I ข้ามถนน
TYPE I CROSS OVER THE STREET

กองวิศวกรรม	การไฟฟ้าส่วนภูมิภาค	ใช้แทนแบบ........
ผู้เขียน อนันต์ ครุฑคงเอมพันธ์ ผู้ลอก........ วิศวกร........ หัวหน้าแผนก บุญเลิศ ผู้อำนวยการกอง........	ผู้ว่าการ .... 2 ธ.ค. 18	ถูกแทนโดยแบบ........ เขียนเสร็จวันที่ 24 พ.ย. 18 แก้แบบวันที่........
	การติดตั้งสายพันร่วมหลายสาย	มิติเป็น........ มาตราส่วน........
รองผู้ว่าการฝ่ายเทคนิค	MULTIPLEX CABLE INSTALLATION	แบบเลขที่ S02-015/18079 แผ่นที่ 1 ของจำนวน 2 แผ่น

การประกอบเลขที่
ASSEMBLY NO. 0304

บัญชีวัสดุ
BILL OF MATERIAL

ลำดับที่ ITEM	รายละเอียด DESCRIPTION	จำนวน REQ'D แบบที่ TYPE I	จำนวน REQ'D แบบที่ TYPE II	วัสดุเลขที่ MAT. NO.
1	ลูกรอกแรงต่ำ มอก.227 แบบ ข (แบบ 53-2) INSULATOR, SPOOL TYPE, L.T. TIS 227 TYPE B (CLASS 53-2)	2	–	03030000
2	ที่จับรอกสำหรับลูกรอก มอก. 227 (แบบ 53-2) CLEVIS, FLAT STEEL, FOR INSULATOR TIS 227 (CLASS 53-2)	2	–	03130100
3	สายพันร่วมหลายเส้น ขนาดและความยาวตามต้องการ MULTIPLEX CABLE, SIZE AND LENGTH AS REQUIRED	–	–	–
4	พี.จี. คอนเนคเตอร์สลักคู่ สำหรับสายอะลูมิเนียม 16-70 ต.มม. CONNECTOR, PARALLEL GROOVE, DOUBLE BOLT, Al 16-70 mm^2	*	*	02300101
5	คอนเนคเตอร์เข้าปลายสาย ขนาดตามต้องการ CONNECTOR, DEADEND, SIZE AS REQUIRED	2	2	02310000-1
	แบบเลือก ALTERNATIVE			
5 Alt	ปรีฟอร์มกริพเข้าปลายสาย PREFORMED GRIP, DEADEND	2	2	–

หมายเหตุ :

1 ระยะห่างที่ปลอดภัยดูแบบเลขที่ S02-015/17068

2 การยึดโยงใช้เมื่อมีความจำเป็น

3 สายพันร่วมหลายเส้น คือ สายพันร่วมสองเส้น สายพันร่วมสามเส้น และสายพันร่วมสี่เส้น

4 * สายพันร่วมสองเส้นใช้ พี.จี. คอนเนคเตอร์ 4 ตัว
สายพันร่วมสามเส้นใช้ พี.จี. คอนเนคเตอร์ 6 ตัว
สายพันร่วมสี่เส้น ใช้ พี.จี. คอนเนคเตอร์ 8 ตัว

5 พื้นที่หน้าตัดของสายพันร่วมหลายเส้นไม่ควรเกิน 70 ต.มม.

NOTES :

1 SAFETY CLEARANCE SEE DRAWING NUMBER S02-015/17068.

2 GUYING SHALL BE INSTALLED IF REQUIRED.

3 MULTIPLEX CABLES ARE DUPLEX CABLE, TRIPLEX CABLE AND QUADRUPLEX CABLE.

4 * DUPLEX CABLE; USE 4 P.G. CONNECTORS,
TRIPLEX CABLE; USE 6 P.G. CONNECTORS,
QUADRUPLEX CABLE; USE 8 P.G. CONNECTORS.

5 CROSS SECTION AREA OF MULTIPLEX CABLE SHALL NOT BE EXCEEDED 70 mm^2.

กองวิศวกรรม
ผู้เขียน
สถาปนิก
วิศวกร
หัวหน้าแผนก
ผู้อำนวยการกอง
รองผู้ว่าการฝ่ายเทคนิค

การไฟฟ้าส่วนภูมิภาค

ผู้ว่าการ 20-ค-18

การติดตั้งสายพันร่วมหลายสาย

MULTIPLEX CABLE INSTALLATION

ใช้แทนแบบ
ถูกแทนโดยแบบ
เขียนเสร็จวันที่ 21 พ.ย.18
แก้แบบวันที่
มิติเป็น
มาตราส่วน
แบบเลขที่ S02-015/1807
แผ่นที่ 2 ของจำนวน 2 แผ่น