การประกอบเลขที่ ASSEMBLY NO. **5222**

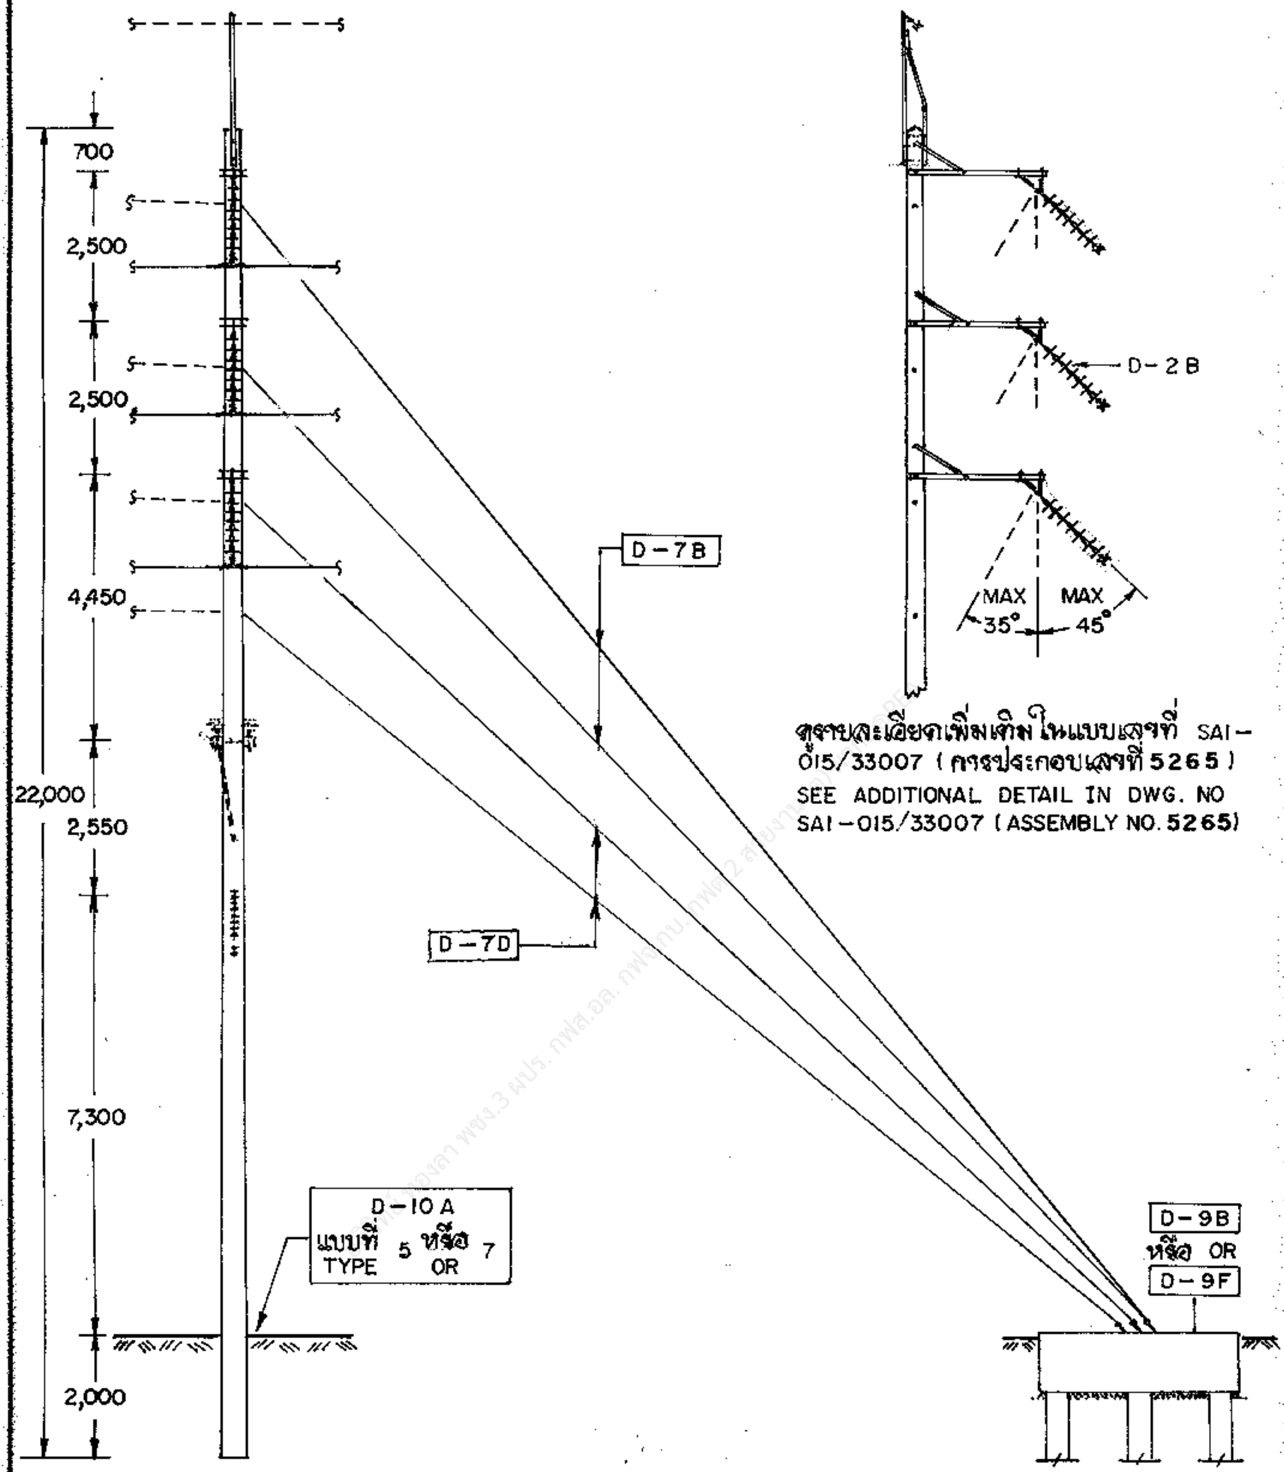

ดูรายละเอียดเพิ่มเติมในแบบเลขที่ SAI-015/33007 (การประกอบเลขที่ **5265**)
SEE ADDITIONAL DETAIL IN DWG. NO SAI-015/33007 (ASSEMBLY NO. **5265**)

กองวิศวกรรมไฟฟ้าและเครื่องกล ฝ่ายวิศวกรรม	**การไฟฟ้าส่วนภูมิภาค**	ใช้แทนแบบ ...... ถูกแทนโดยแบบ ......
ผู้เขียน ...... ผู้ตรวจ ...... วิศวกร ...... หัวหน้าแผนก ...... ผู้อำนวยการกอง ...... ผู้อำนวยการฝ่าย	**ผู้ว่าการ** ...... 115 kV วงจรเดี่ยว สายไฟฟ้าเดี่ยว เสาสำหรับทางโค้ง ต่อจากต้นเข้าปลายสายสองข้าง แบบ SS-SA-4	เขียนเสร็จวันที่ 5 ก.ย.39 แก้แบบวันที่ 15 ก.ย.40 หน่วยเป็น มิลลิเมตร มาตราส่วน 1:125
รองผู้ว่าการ	115 kV SINGLE-CIRCUIT SINGLE-CONDUCTOR ANGLE STRUCTURE ADJACENT TO SINGLE DEADEND STRUCTURE TYPE SS-SA-4	แบบเลขที่ SAI-015/39015 แผ่นที่ 1 ของจำนวน 3 แผ่น

การประกอบเลขที่ ASSEMBLY NO. **5222**

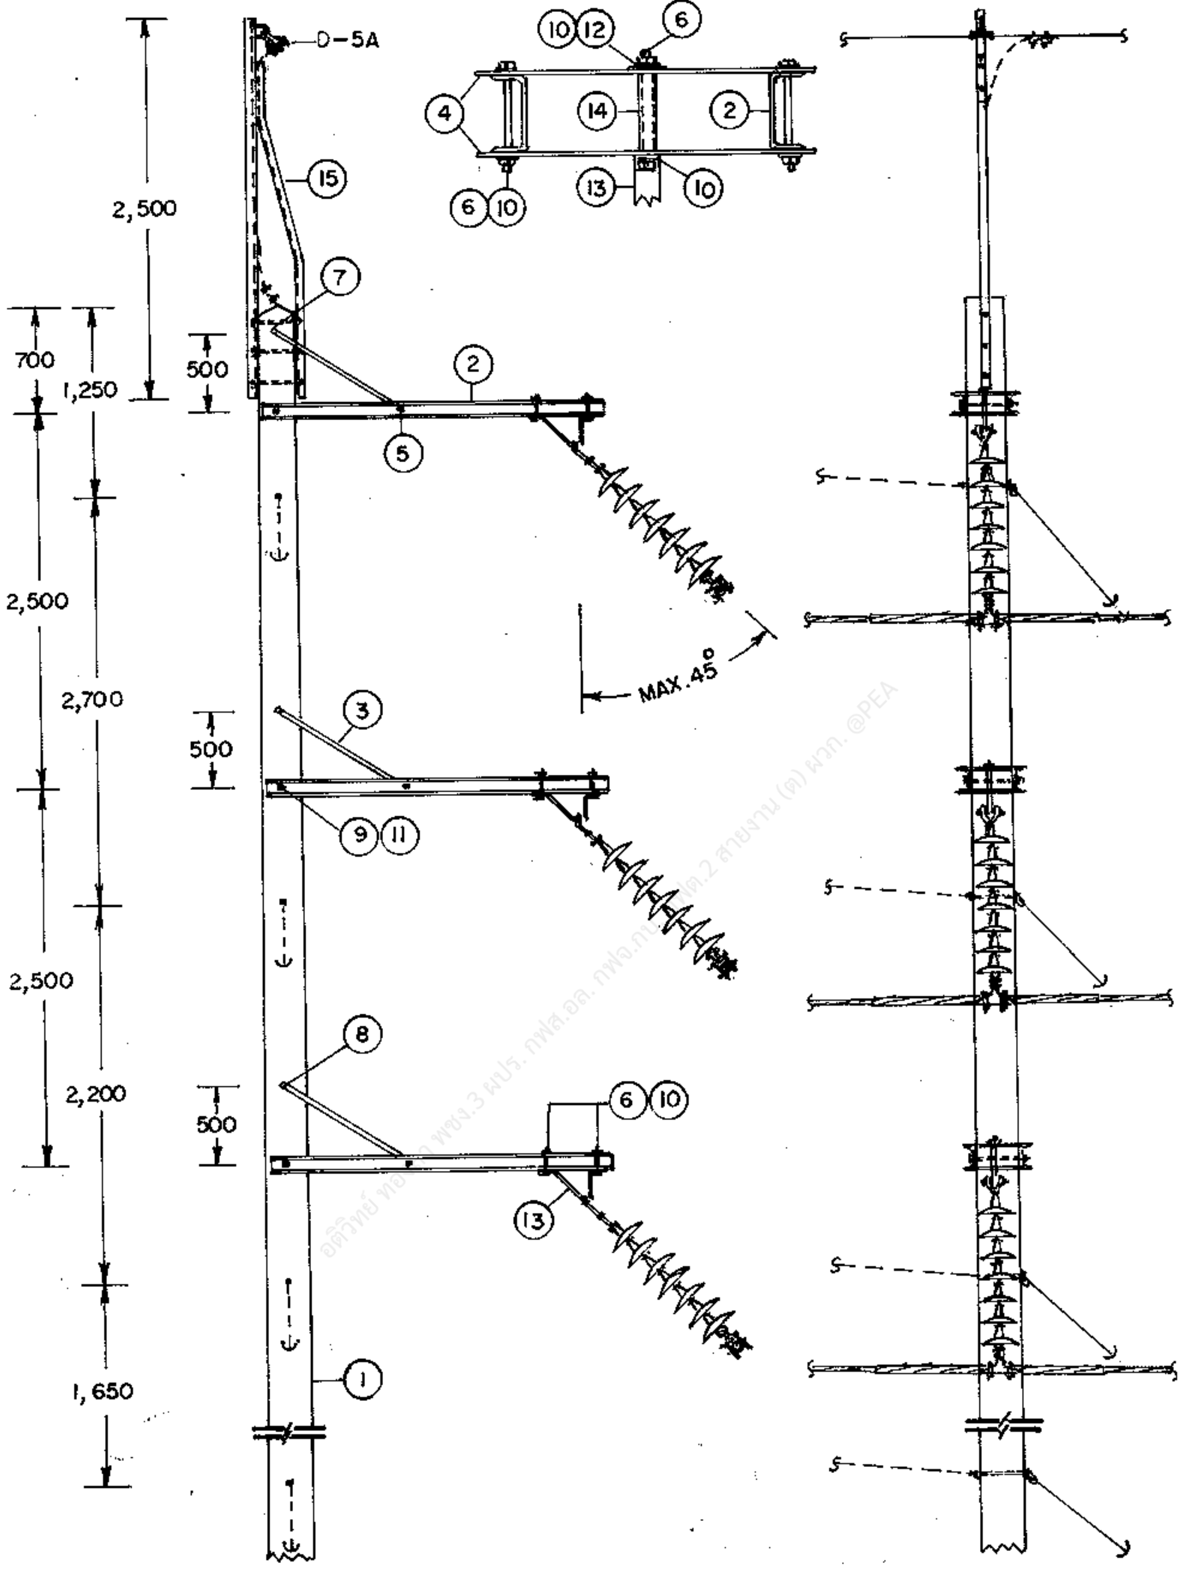

อติวิทย์ ทอ[illegible] พชง.3 ผปร. กฟส.อล. กฟจ.กบ. [illegible]ฟต.2 สายงาน (ต) ผวก. @PEA

กองวิศวกรรมไฟฟ้าและเครื่องกล
ฝ่ายวิศวกรรม

การไฟฟ้าส่วนภูมิภาค

ผู้เขียน ....
ผู้ตรวจ ....
วิศวกร ....
หัวหน้าแผนก ....
ผู้อำนวยการกอง ....
ผู้อำนวยการฝ่าย ....

ผู้ว่าการ ....

รองผู้ว่าการ
....

115 kV วงจรเดี่ยว, สายไฟฟ้าเดี่ยว
เสาสำหรับทางโค้ง ต่อจากต้นเสาปลายสายสองข้าง
แบบ SS–SA–4

115 kV SINGLE-CIRCUIT SINGLE-CONDUCTOR
ANGLE STRUCTURE ADJACENT TO SINGLE DEADEND STRUCTURE
TYPE SS–SA–4

ใช้แทนแบบ ....
ถูกแทนโดยแบบ ....
เขียนเสร็จวันที่ 5 ก.ย. 39
แก้แบบวันที่ ....
มิติเป็น มิลลิเมตร
มาตราส่วน 1 : 50
แบบเลขที่ SAI-015/39015
แผ่นที่ 2 ของจำนวน 3 แผ่น

การประกอบเลขที่ ASSEMBLY NO. **5222**

บัญชีวัสดุ
BILL OF MATERIAL

ลำดับที่ ITEM	รายละเอียด DESCRIPTION	จำนวน REQ'D	วัสดุเลขที่ MAT. NO.
1	เสาคอนกรีต 22 เมตร POLE, CONCRETE, 22 m LONG	1	0041 00010011
2	คอนเหล็กแบบก้านแขนขนาด [100x50x5 มม. ยาว 2.25 ม. มอก 116 STEEL ALLEY ARM, [100x50x5 mm., 2.25 m.,LONG ,TIS 116	6	6012 01000100
3	เหล็กประกับคอน ขนาด 40x6 มม. ยาว 1,000 มม. BRACE, FLAT, FOR CROSSARM 40x6x1,000 mm	6	0121 01200002
4	แผ่นเหล็ก ขนาด 6x100x450 มม. PLATE, STEEL 6x100x450 mm	12	0143 01030002
5	สลักเกลียวหัวหกเหลี่ยม เอ็ม 16x75 มม. พร้อมแหวนกลม 2 อัน BOLT, MACHINE, HEXAGON, M.16x75 mm,COMPLETE WITH 2 ROUND WASHER	6	0236 01110400
6	สลักเกลียว เอ็ม 16x170 มม. BOLT, MACHINE M.16x170 mm	18	0221 01110201
7	สลักเกลียว เอ็ม 16x300 มม. BOLT, MACHINE M.16x300 mm	4	0224 01110204
8	สลักเกลียว เอ็ม 16x350 มม. BOLT, MACHINE M.16x350 mm	2	0225 01110205
9	สลักเกลียว เอ็ม 20x350 มม. BOLT, MACHINE M.20x350 mm	3	0232 01110300
10	แหวนรองแบบเรียบ ประเภทจัตุรัสขนาดใหญ่ 52x52x4.5 มม เส้นผ่าศูนย์กลางรู 18 มม มอก. 258 WASHER, PLAIN, SQUARE, LARGE 52x52x4.5 mm HOLE DIA. 18 mm TIS 258	36	0355 01180100
11	แหวนรองแบบเรียบ ประเภทจัตุรัสขนาดใหญ่ 62x62x6 มม เส้นผ่าศูนย์กลางรู 22 มม มอก. 258 WASHER, PLAIN, SQUARE, LARGE 62x62x6 mm HOLE DIA. 22 mm TIS 258	6	0356 01180101
12	แหวนรองแบบสปริง ขนาดระบุ 16 มม. ประเภทใช้งานทั่วไป มอก. 259 WASHER, LOCK, SPRING, SIZE 16 mm, GENERAL PURPOSE, TIS 259	6	0365 01180301
13	ที่แขวนลูกถ้วยทางโค้ง BRACKET, CORNER SUSPENSION	3	0489 03140012
14	ท่อเหล็กขนาดระบุ 20 ประเภทที่ 2 ยาว 100 มม. มอก.277 แต่ไม่มีเกลียวที่ปลาย PIPE,STEEL,SIZE 20,TYPE 2,100 mm. LONG TIS.277 BUT WITOUT THREADED END	6	0905 01050000
15	เหล็กฉาก รับสายล่อฟ้าทางโค้ง 65x65x6 มม. ยาว 2,500 มม. STEEL ANGLE, OVERHEAD GROUND WIRE CORNER BAYONET 65x65x6 mm 2,500 mm LONG	1	0136 01010005

รายละเอียด DESCRIPTION			การประกอบเลขที่ ASSEMBLY.NO.
D-2B	การประกอบลูกถ้วยแขวน SUSPENSION INSULATOR ASSEMBLY	3	5602
D-5A	การต่อสายล่อฟ้า OVERHEAD GROUND WIRE CONNECTOR	1	5626
D-10A	ฐานรากเสา POLE FOUNDATION	1	5661
D-7B	การประกอบสายยึดโยง ลวดเหล็กตีเกลียว 95 ต.มม. STEEL STRANDED WIRE 95 Sq.mm. GUY ASSEMBLY	2	5639
D-7D	การประกอบสายยึดโยง ลวดเหล็กตีเกลียว 95 ต.มม. STEEL STRANDED WIRE 95 Sq.mm. GUY ASSEMBLY	2	5639
D-9B OR D-9F	สมอบกคอนกรีต ตามแบบเลขที่ IB1-015/240027 หรือ IB1-017/25034 (การประกอบแบบเลขที่ 5652) CONCRETE ANCHOR ACCD.TO DWG.NO. IB1-240027 OR IB1-25034 (ASSEMBLY NO. 5652..)	1	5652

กองวิศวกรรมไฟฟ้าและเครื่องกล ฝ่ายวิศวกรรม	การไฟฟ้าส่วนภูมิภาค	ใช้แทนแบบ .... ถูกแทนโดยแบบ ....
ผู้เขียน ...วิสุทธิ์ ชื่อเพราะ.... ผู้สำรวจ.................. วิศวกร .... หัวหน้าแผนก .... ผู้อำนวยการกอง .... ผู้อำนวยการฝ่าย	ผู้ว่าการ ....ธน ปานเครือ แทน 28 ต.ค. 2539 115 kV วงจรเดี่ยว สายไฟฟ้าเดี่ยว เสาสำหรับทางโค้ง ต่อจากต้นข้างปลายสายสองข้าง แบบ SS-SA-4	เขียนเสร็จวันที่ 5 ก.ย. 39 แก้แบบวันที่ 15 ก.พ.40 มิติเป็น ....มิลลิเมตร..... มาตราส่วน ....
รองผู้ว่าการ ....ธน ปานเครือ....	115 kV SINGLE-CIRCUIT SINGLE CONDUCTOR ANGLE STRUCTURE ADJACENT TO DOUBLE DEADEND STRUCTURE TYPE SS-SA-4	แบบเลขที่ SA1-015/39015 แผ่นที่ 3 ของจำนวน 3 แผ่น

28 ต.ค. 2539