การประกอบเลขที่
ASSEMBLY NO. **3406**

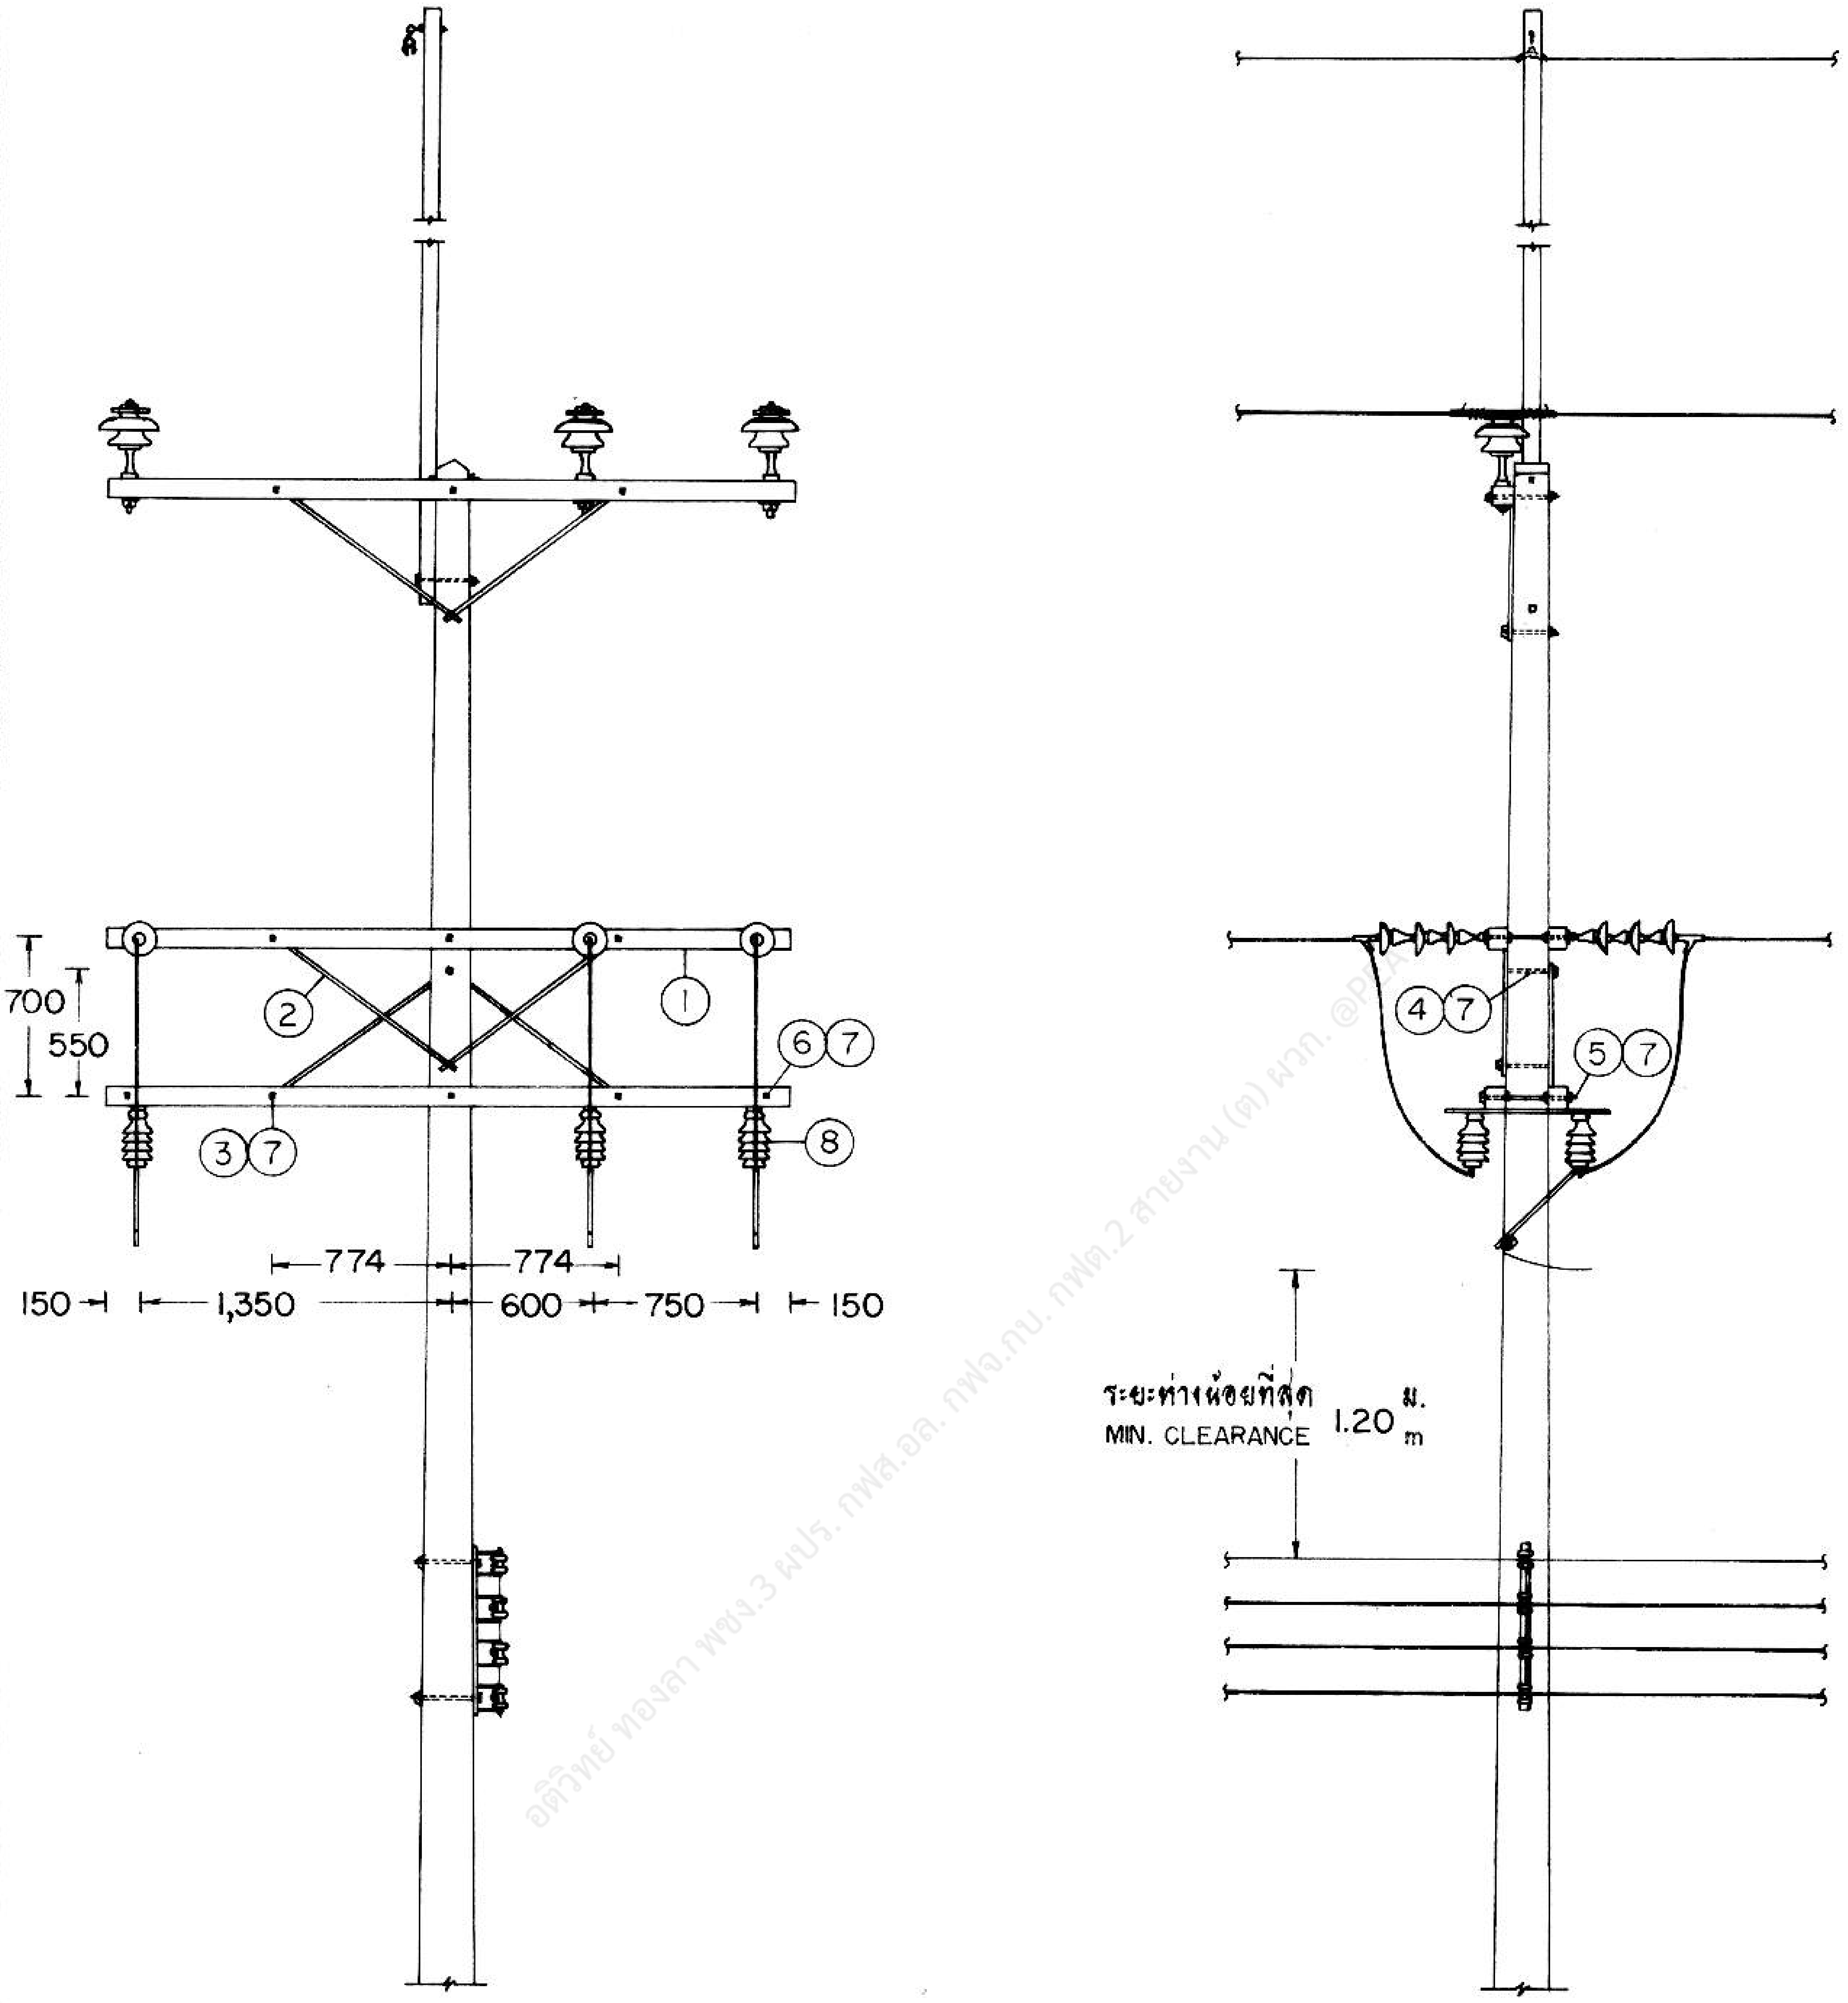

อดิวิทย์ ทองลา พชง.3 ผปร. กฟส.อล. กฟจ.กบ. กฟต.2 สายงาน (ต) ผวก. @PEA

กองวิศวกรรม

ผู้เขียน
ผู้สำรวจ
วิศวกร
หัวหน้าแผนก
หัวหน้ากอง

รองผู้ว่าการฝ่ายเทคนิค

การไฟฟ้าส่วนภูมิภาค

ผู้ว่าการ

26 พ.ค. 2520

การติดตั้งสวิตช์ธรรมดา หนึ่งขา แบบเข้าปลายสายสองข้างที่วงจรล่าง
ระบบ 33 kV

SINGLE POLE ISOLATING SWITCH INSTALLATION
DOUBLE DEADEND TYPE OF LOWER FEEDER
33 kV SYSTEM

ใช้แทนแบบ
ถูกแทนโดยแบบ
เขียนเสร็จวันที่ 28 เม.ย.20
แก้แบบวันที่
ผลิตเป็น
มาตราส่วน 1 : 50
แบบเลขที่ S02-015/20064
แผ่นที่ 1 ของจำนวน 2 แผ่น

การประกอบเลขที่
ASSEMBLY NO. **3406**

บัญชีวัสดุ
BILL OF MATERIAL

ลำดับที่ ITEM	รายละเอียด DESCRIPTION	จำนวน REQ'D	วัสดุเลขที่ MAT. NO.
1	ไม้คอนสายแรงสูง 100 X 120 X 3,000 มม. CROSSARM, WOOD, H.T. 100 X 120 X 3,000 mm	2	00100003
2	เหล็กประกับไม้คอน 40 X 6 X 1,000 มม. BRACE, FLAT, FOR CROSSARM 40 X 6 X 1,000 mm	2	01200002
3	สลักเกลียว M 16 X 130 มม. BOLT, MACHINE, M 16 X 130 mm	2	01110200
4	สลักเกลียว M 16 X 250 มม. BOLT, MACHINE, M 16 X 250 mm	1	01110203
5	สลักเกลียว M 16 X 450 มม. BOLT, MACHINE, M 16 X 450 mm	1	01110207
6	สลักเกลียวตลอด M 16 X 450 มม. BOLT, DOUBLE ARMING M 16 X 450 mm	2	01120000
7	แหวนสี่เหลี่ยมแบน 52X52X4.5 มม. รู Ø 18 มม. มอก. 258 WASHER, SQUARE, FLAT 52X52X4.5 mm HOLE Ø 18 mm TIS 258	13	01180100
8	สวิตช์ธรรมดา หนึ่งขา 33 kV ชนิดติดในสายจำหน่าย SWITCH, ISOLATING, SINGLE POLE, 33 kV DISTRIBUTION CLASS	3	04050100 - 04059801

อดิวิทย์ ทองลา พชง.3 ผปร. กฟส.อล. กฟจ.กบ. กฟต.2 สายงาน (ต) ผวก. @PEA

กองวิศวกรรม

ผู้เขียน
ผู้สำรวจ
วิศวกร
หัวหน้าแผนก
หัวหน้ากอง

รองผู้ว่าการฝ่ายเทคนิค

การไฟฟ้าส่วนภูมิภาค

ผู้ว่าการ

26 พ.ค. 2520

การติดตั้งสวิตช์ธรรมดาหนึ่งขา แบบเข้าปลายสายสองข้างที่วงจรล่าง
ระบบ 33 kV

SINGLE POLE ISOLATING SWITCH INSTALLATION
DOUBLE DEADEND TYPE OF LOWER FEEDER
33 kV SYSTEM

ใช้แทนแบบ
ถูกแทนโดยแบบ
เขียนเสร็จวันที่ 28 เม.ย. 20
แก้แบบวันที่
มิติเป็น
มาตราส่วน
แบบเลขที่ S 02-015/20064
แผ่นที่ 2 ของจำนวน 2 แผ่น