การประกอบเลขที่ ASSEMBLY NO. **3304**

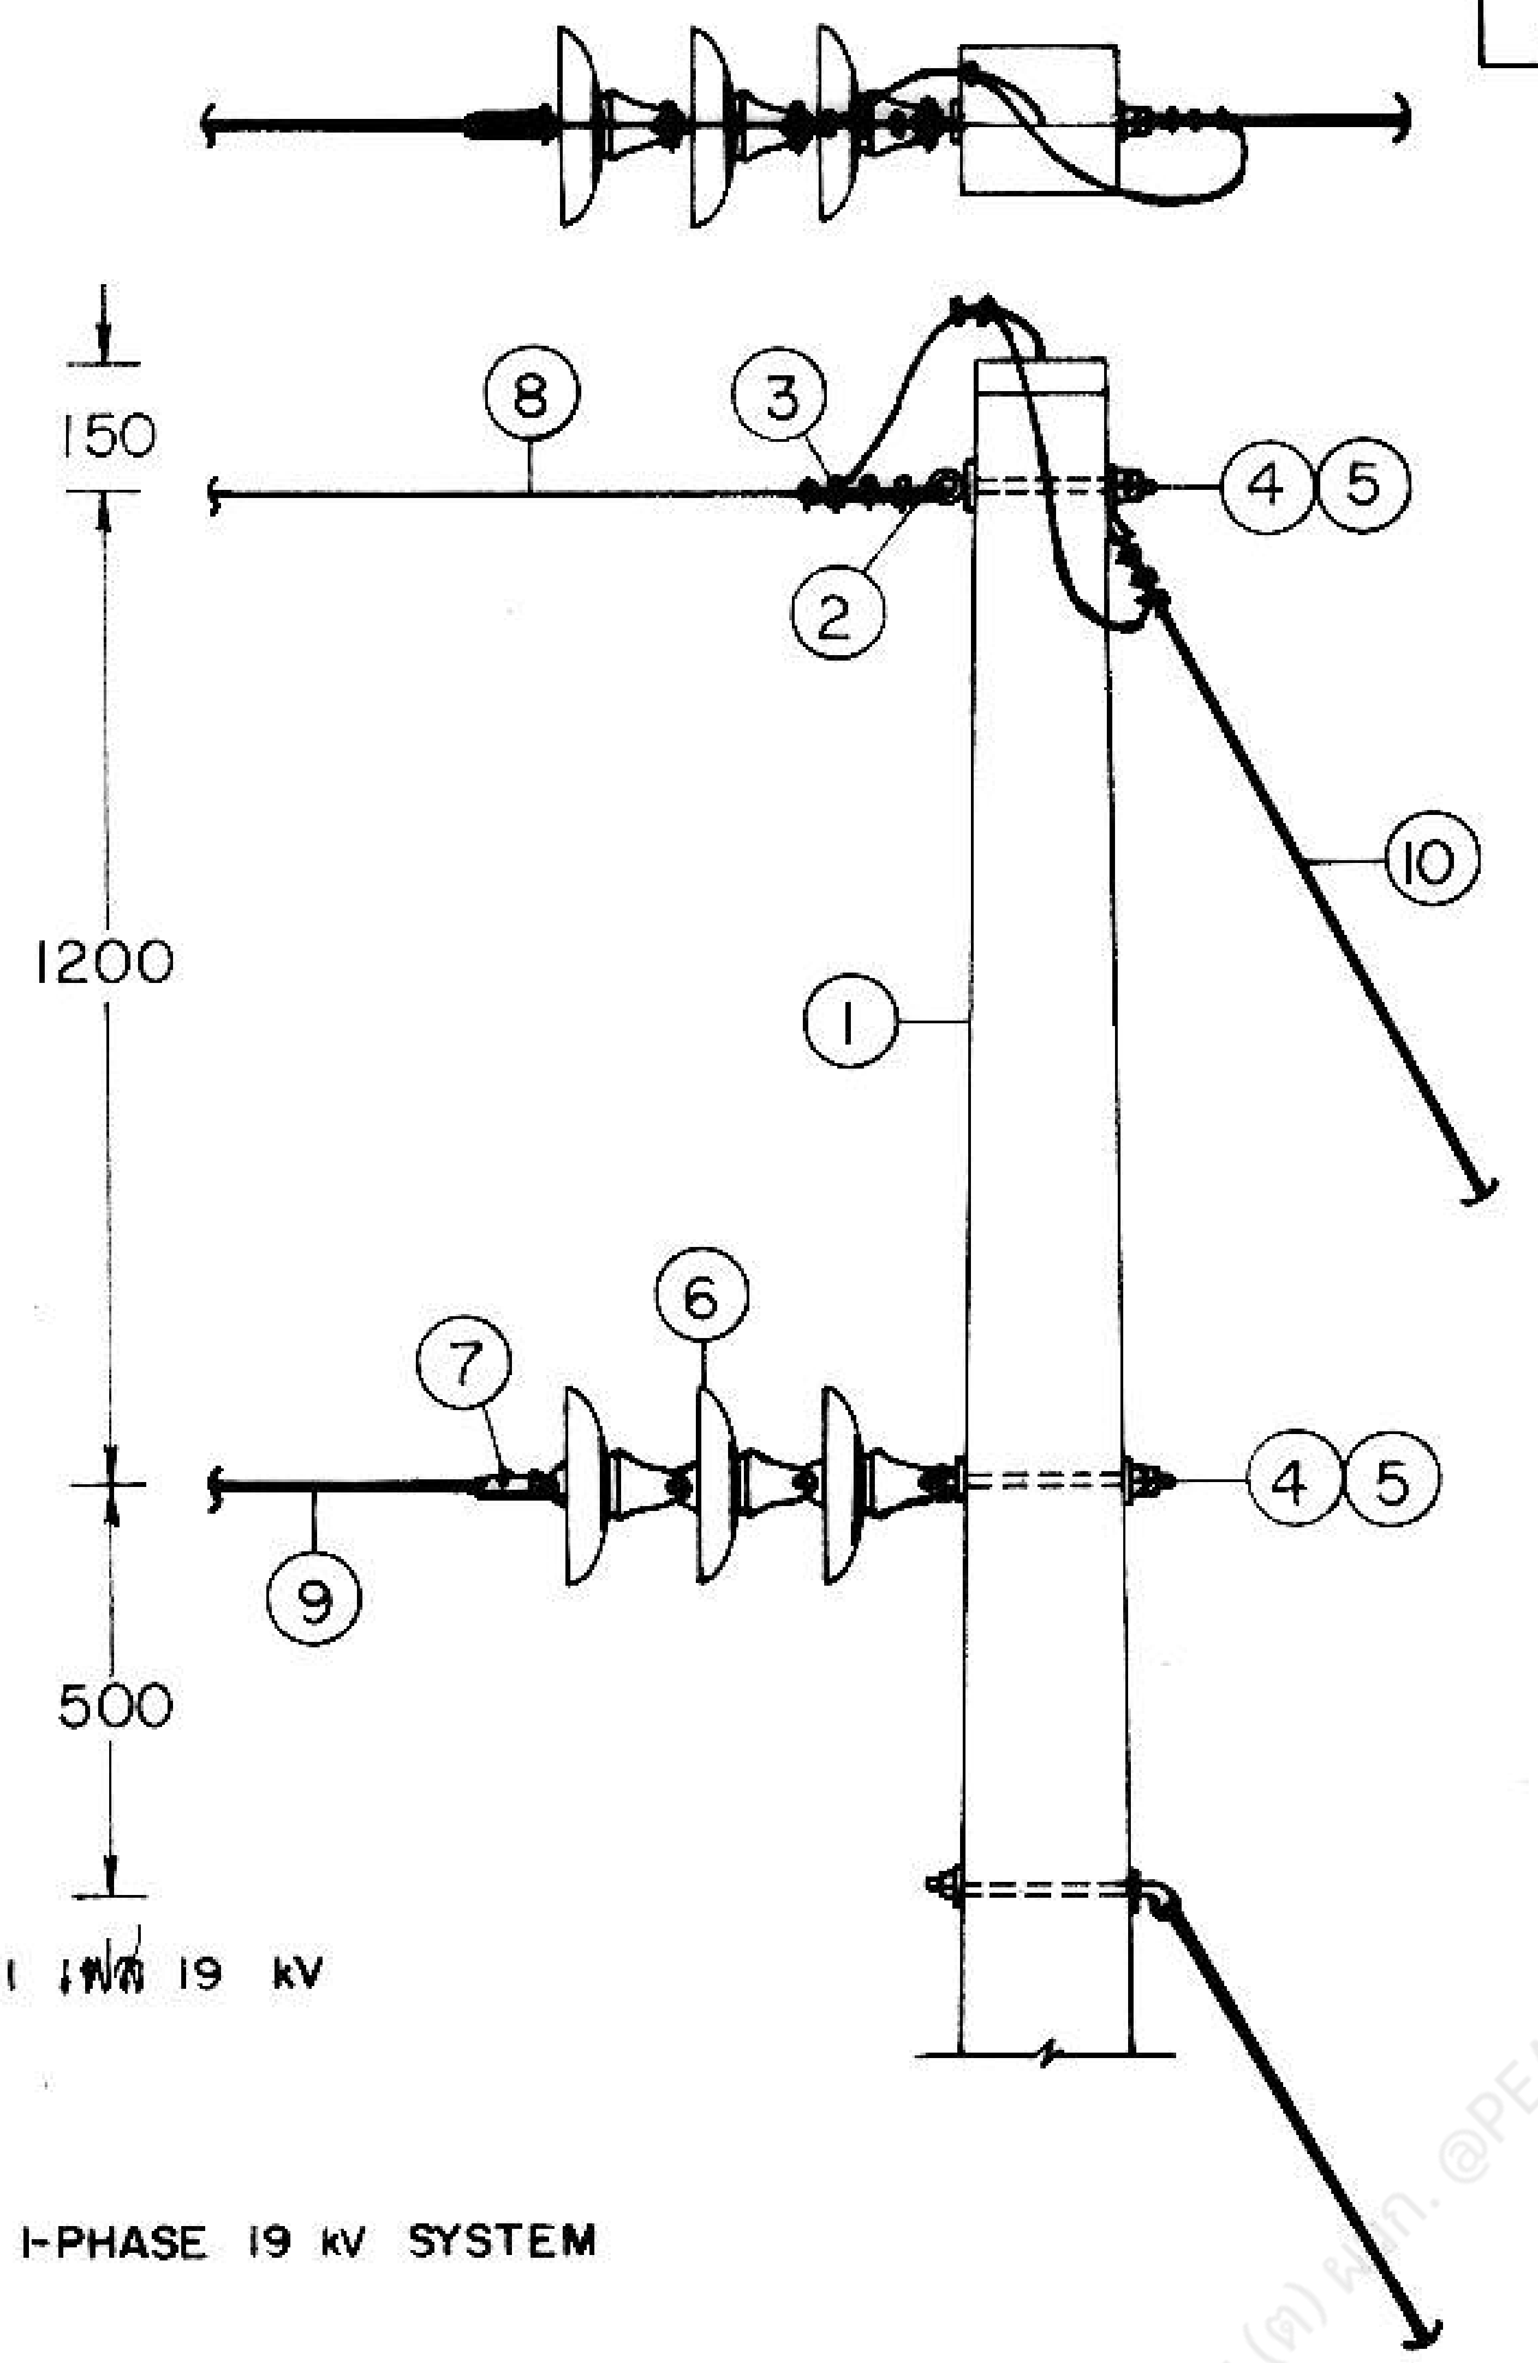

ดูข้อแนะนำในการก่อสร้างระบบจำหน่าย 1 เฟส 19 kV
แบบเลขที่ S02-015/20016

SEE CONSTRUCTION SUGGESTION OF 1-PHASE 19 kV SYSTEM
DWG. NO. S02-015/20016

บัญชีวัสดุ
BILL OF MATERIAL

ลำดับที่ ITEM	รายละเอียด DESCRIPTION	จำนวน REQ' D	วัสดุเลขที่ MAT. NO.
1	เสาคอนกรีต ขนาด 12 ม. (สำหรับระบบ 33 kV) CONCRET POLE 12 m LONG (FOR 33 kV SYSTEM)	1	00010004 (0034)
2	กายทิมเบิ้ลสำหรับสายยึดโยง ขนาด 50-95 ต.มม. THIMBLE, GUY, FOR STEEL WIRE 50-95 mm^2	1	01210304 (0150)
3	ยูแคล้มป์สลัก 1 ตัว M 8 (ไวร์ โร้ป คลิ๊ฟ) CLAMP, SINGLE U-BOLT M 8 (WIRE ROPE CLIP)	4	01230000 (0165)
4	สลักห่วงกลม M 16 X 250 มม. BOLT, ROUND EYE M 16 X 250 mm	2	01140002 (0254)
5	แหวนสี่เหลี่ยมแบน 52X52X4.5 มม.รู Ø 18 มม. มอก.258 WASHER, SQUARE, FLAT 52X52X4.5 mm HOLE Ø 18 mm TIS 258	4	01180100 (0355)
6	ลูกถ้วยแขวน มอก.354 แบบ ง (แบบ 52-4) INSULATOR, SUSPENSION TYPE, TIS 354 TYPE D (CLASS 52-4)	3	03020002 (0415)
7	สเตรนแคล้มป์ สำหรับสายอะลูมิเนียม 35-70 ต.มม. อะลูมิเนียมแกนเหล็ก 35-50 ต.มม. CLAMP, STRAIN FOR Al 35-70 mm^2, ACSR 35-50 mm^2	1	03110000 or 03110100
8	ลวดเหล็กตีเกลียว 25 ต.มม. มอก. 404 WIRE, STEEL STRANDED 25 mm^2 TIS 404		01100002 (0181)
9	สายอะลูมิเนียมแกนเหล็ก หรือ อะลูมิเนียมอัลลอย 35-50 ต.มม. CONDUCTOR, ACSR OR ALUMINIUM-ALLOY 35-50 mm^2		02020001-2 or 02030001-2
10	สายยึดโยงระบบ 33 kV พร้อมสมอบกครบชุด GY-33 ANCHOR GUY FOR 33 kV SYSTEM GY-33	2	——

กองวิศวกรรม

ผู้เขียน
ผู้สำรวจ
วิศวกร
หัวหน้าแผนก
หัวหน้ากอง

รองผู้ว่าการฝ่ายเทคนิค

การไฟฟ้าส่วนภูมิภาค

ผู้ว่าการ .20

การประกอบลูกถ้วยแขวนกับเสาคอนกรีต
ระบบ 1 เฟส 19 kV
สำหรับเข้าปลายสาย

SUSPENSION INSULATOR ASSEMBLY ON CONCRETE POLE
1-PHASE 19 kV SYSTEM
DEAD END STRUCTURE

ใช้แทนแบบ
ถูกแทนโดยแบบ
เขียนเสร็จวันที่ 22 ม.ค. 20
แก้แบบวันที่
มิติเป็น มม.
มาตราส่วน 1:25
แบบเลขที่ S02-015/20015
แผ่นที่ 1 ของจำนวน 1 แผ่น

8