การประกอบเลขที่ ASSEMBLY NO. 5353

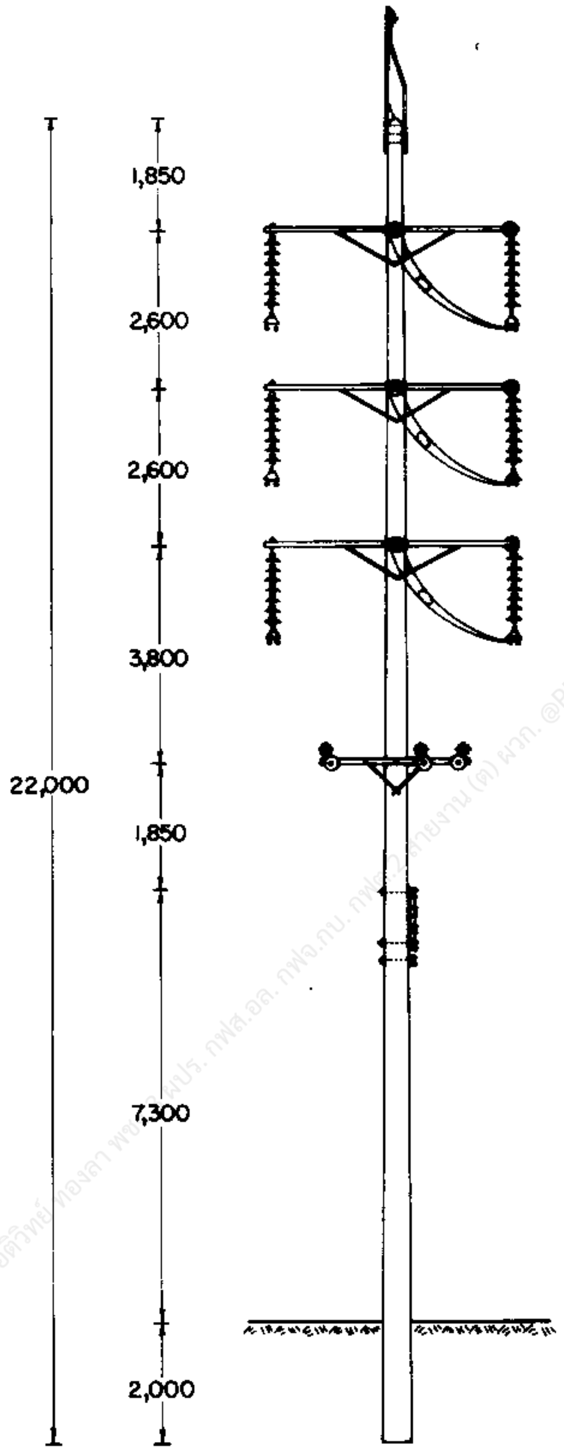

อดิวิทย์ ทองลา พช ฝปร. กฟส.อล. กฟจ.กบ. กฟจ.2 สายงาน (ต) ผวก. @PEA

กองวิศวกรรมไฟฟ้าและเครื่องกล
ฝ่ายวิศวกรรม

ผู้เขียน
ผู้ตรวจ
วิศวกร
หัวหน้าแผนก
หัวหน้ากอง
ผู้อำนวยการฝ่าย

รองผู้ว่าการฝ่ายเทคนิค

การไฟฟ้าส่วนภูมิภาค

ผู้ว่าการ 23 มิ.ย. 24

115 kV วงจรคู่ สายไฟฟ้าคู่
เสาสำหรับทางโค้ง (ช่วงไม่รับแรงดึง)
แบบ DD-AS-1

115 kV DOUBLE CIRCUIT DOUBLE CONDUCTOR
ANGLE STRUCTURE (SLACK SPAN)
TYPE DD-AS-1

ใช้แทนแบบ
ถูกแทนโดยแบบ
เขียนเสร็จวันที่ 31 มี.ค. 24
แก้แบบวันที่
มิติเป็น มม.
มาตราส่วน 1 : 125

แบบเลขที่ SAI-015/24003
แผ่นที่ 1 ของจำนวน 4 แผ่น

การประกอบเลขที่
ASSEMBLY NO. 5353

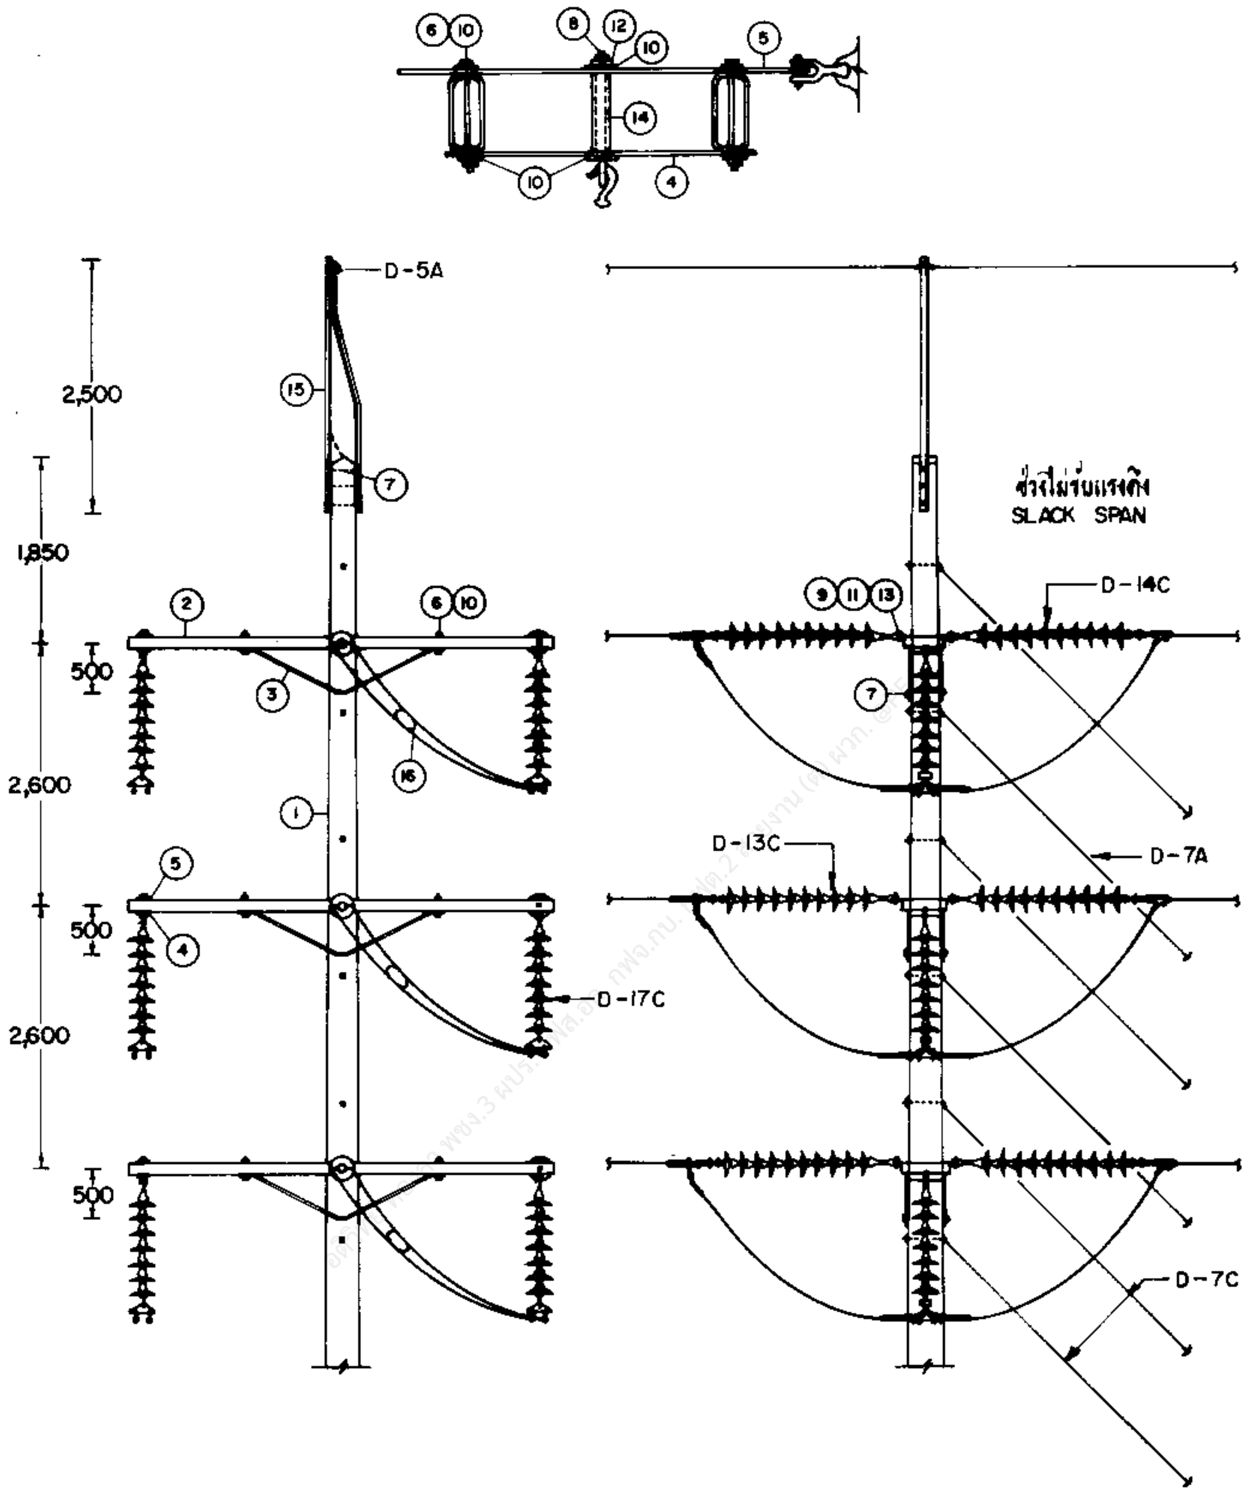
⑥ ⑩
⑧ ⑫ ⑩
⑤
⑭
⑩
④
D-5A
2,500
⑮
⑦
1,850
②
⑥ ⑩
500
③
⑯
2,600
①
⑤
500
④
D-17C
2,600
500
ช่วงไม่รับแรงดึง
SLACK SPAN
⑨ ⑪ ⑬
D-14C
⑦
D-13C
D-7A
D-7C

กองวิศวกรรมไฟฟ้าและเครื่องกล ฝ่ายวิศวกรรม	การไฟฟ้าส่วนภูมิภาค	ใช้แทนแบบ ถูกแทนโดยแบบ
ผู้เขียน ผู้ตรวจ วิศวกร หัวหน้าแผนก หัวหน้ากอง ผู้อำนวยการฝ่าย	ผู้ว่าการ 2-3 เม.ย. 24 115 kV วงจรคู่ สายไฟฟ้าคู่ เสาสำหรับทางโค้ง (ช่วงไม่รับแรงดึง) แบบ DD-AS-1	เขียนเสร็จวันที่ 31 มี.ค. 24 แก้แบบวันที่ 15 ก.ย. 40 มิติเป็น มม. มาตราส่วน 1:75
รองผู้ว่าการฝ่ายเทคนิค	115 kV DOUBLE CIRCUIT DOUBLE CONDUCTOR ANGLE STRUCTURE (SLACK SPAN) TYPE DD-AS-1	แบบเลขที่ SAI-015/24003 แผ่นที่ 2 ของจำนวน 4 แผ่น

การประกอบเลขที่
ASSEMBLY NO. 5353

บัญชีวัสดุ
BILL OF MATERIAL

ลำดับที่ ITEM	รายละเอียด DESCRIPTION	จำนวน REQ'D	วัสดุเลขที่ MAT. NO.
1	เสาคอนกรีต 22 ม. POLE, CONCRETE 22 m LONG	1	00010011 (0041)
2	คอนสายแบบเหล็ก 100 X 50 X 3.2 มม. ยาว 4.20 ม. CROSSARM, STEEL, 100 X 50 X 3.2 mm , 4.20 m LONG	6	00120001 (0116)
3	เหล็กฉากรับคอนสาย ขนาด 50 X 50 X 6 มม. ช่วงกว้าง 1,800 มม. ดรอพ 450 มม. BRACE, ANGLE STEEL, 50 X 50 X 6 mm, 1,800 mm WIDE, 450 mm DROP	6	01200007 (0119)
4	เหล็กแผ่น ขนาด 6 X 100 X 450 มม. PLATE, STEEL 6 X 100 X 450 mm	6	01030002 (0143)
5	เหล็กแผ่นยึดสองปลาย ขนาด 12 X 100 X 650 มม. PLATE, STEEL, DOUBLE ARMING 12 X 100 X 650 mm	6	01030100 (0145)
6	สลักเกลียว M 16 X 170 มม. BOLT, MACHINE, M 16 X 170 mm	24	01110201 (0221)
7	สลักเกลียว M 16 X 350 มม. BOLT, MACHINE, M 16 X 350 mm	6	01110205 (0225)
8	สลักห่วงโอแวล M 16 X 150 มม. BOLT, OVAL EYE M 16 X 150 mm	6	01150000 (0257)
9	สลักห่วงโอแวล M 20 X 450 มม. BOLT, OVAL EYE M 20 X 450 mm	3	01150101 (0261)
10	แหวนสี่เหลี่ยมแบน 52X52X4.5 มม. รู Ø 18 มม. มอก. 258 WASHER, SQUARE, FLAT 52X52 X4.5 mm HOLE Ø 18 mm, TIS 258	48	01180100 (0355)
11	แหวนสี่เหลี่ยมแบน 62 X 62 X 6 มม. รู Ø 22 มม. มอก. 258 WASHER, SQUARE, FLAT 62 X 62 X 6 mm HOLE Ø 22 mm, TIS 258	6	01180101 (0356)
12	แหวนสปริง M 16 มอก. 259 WASHER, LOCK, M 16, TIS 259	6	01180301 (0365)
13	แหวนสปริง M 20 มอก. 259 WASHER, LOCK, M 20, TIS 259	3	01180302 (0366)
14	ท่อเหล็ก รูขนาด 20 มม. หนา 2.65 มม. ยาว 100 มม. มอก. 277 ประเภท 2 PIPE, IRON DIA. 20 mm I.D., 2.65 mm THICKNESS, 100 mm LONG, TIS 277, TYPE 2	6	01050000 (0905)
15	เหล็กฉากรับสายล่อฟ้าทางโค้ง OVERHEAD GROUND WIRE CORNER BAYONET	1	01010005 (0136)
16	ปรีฟอร์มแยกสาย SPACER, HELICAL ROD, PREFORMED	6	02240000 (0918)

กองวิศวกรรมไฟฟ้าและเครื่องกล
ฝ่ายวิศวกรรม
ผู้เขียน
ผู้สำรวจ
วิศวกร
หัวหน้าแผนก
หัวหน้ากอง
ผู้อำนวยการฝ่าย
รองผู้ว่าการฝ่ายเทคนิค

การไฟฟ้าส่วนภูมิภาค

ผู้ว่าการ 23 เม.ย. 24

115 kV วงจรคู่ สายไฟฟ้าคู่
เสาสำหรับทางโค้ง (ช่วงไม่รับแรงดึง)
แบบ DD-AS-1

115 kV DOUBLE CIRCUIT DOUBLE CONDUCTOR
ANGLE STRUCTURE (SLACK SPAN)
TYPE DD-AS-1

ใช้แทนแบบ ....
ถูกแทนโดยแบบ ....
เขียนเสร็จวันที่ 31 มี.ค. 24
แก้แบบวันที่ ....
มิติเป็น ....
มาตราส่วน ....
แบบเลขที่ SAI-015/24003
แผ่นที่ 3 ของจำนวน 4 แผ่น

การประกอบเลขที่ 5353
ASSEMBLY NO.

	รายละเอียด DETAIL		
D-13C	การประกอบลูกถ้วยแขวน SUSPENSION INSULATOR ASSEMBLY	3	
D-14C	การประกอบลูกถ้วยแขวน SUSPENSION INSULATOR ASSEMBLY	3	
D-17C	การประกอบลูกถ้วยแขวน SUSPENSION INSULATOR ASSEMBLY	6	
D-5A	การต่อสายล่อฟ้า OVERHEAD GROUND WIRE CONNECTION	1	
D-7A	การประกอบสายยึดโยงลวดเหล็กตีเกลียว 95 ต.มม. STEEL STRANDED WIRE 95 mm² GUY ASSEMBLY	4	
D-7C	การประกอบสายยึดโยงลวดเหล็กตีเกลียว 95 ต.มม. STEEL STRANDED WIRE 95 mm² GUY ASSEMBLY	2	
D-9B	สมอบกคอนกรีต CONCRETE ANCHOR	1	
D-10A	ฐานรากเสา POLE FOUNDATION	1	

อติวิทย์ ทองลา พชง.3 ผปร. กฟส.อล. กฟจ.กบ. กฟต.2 สายงาน (ต) ผวก. @PEA

กองวิศวกรรมไฟฟ้าและเครื่องกล
ฝ่ายวิศวกรรม

ผู้เขียน
ผู้ตรวจ
วิศวกร
หัวหน้าแผนก
หัวหน้ากอง
ผู้อำนวยการฝ่าย
รองผู้ว่าการฝ่ายเทคนิค

การไฟฟ้าส่วนภูมิภาค

ผู้ว่าการ 23 เม.ย. 24

115 kV วงจรคู่ สายไฟฟ้าคู่
เสาสำหรับทางโค้ง (ช่วงไม่รับแรงดึง)
แบบ DD-AS-1

115 kV DOUBLE CIRCUIT DOUBLE CONDUCTOR
ANGLE STRUCTURE (SLACK SPAN)
TYPE DD-AS-1

ใช้แทนแบบ
ถูกแทนโดยแบบ
เขียนเสร็จวันที่ 31 มี.ค. 24
แก้แบบวันที่ 15 ก.ย. 40
มิติเป็น
มาตราส่วน
แบบเลขที่ SAI-015/24003
แผ่นที่ 4 ของจำนวน 4 แผ่น