การประกอบเลขที่ ASSEMBLY NO.	5426

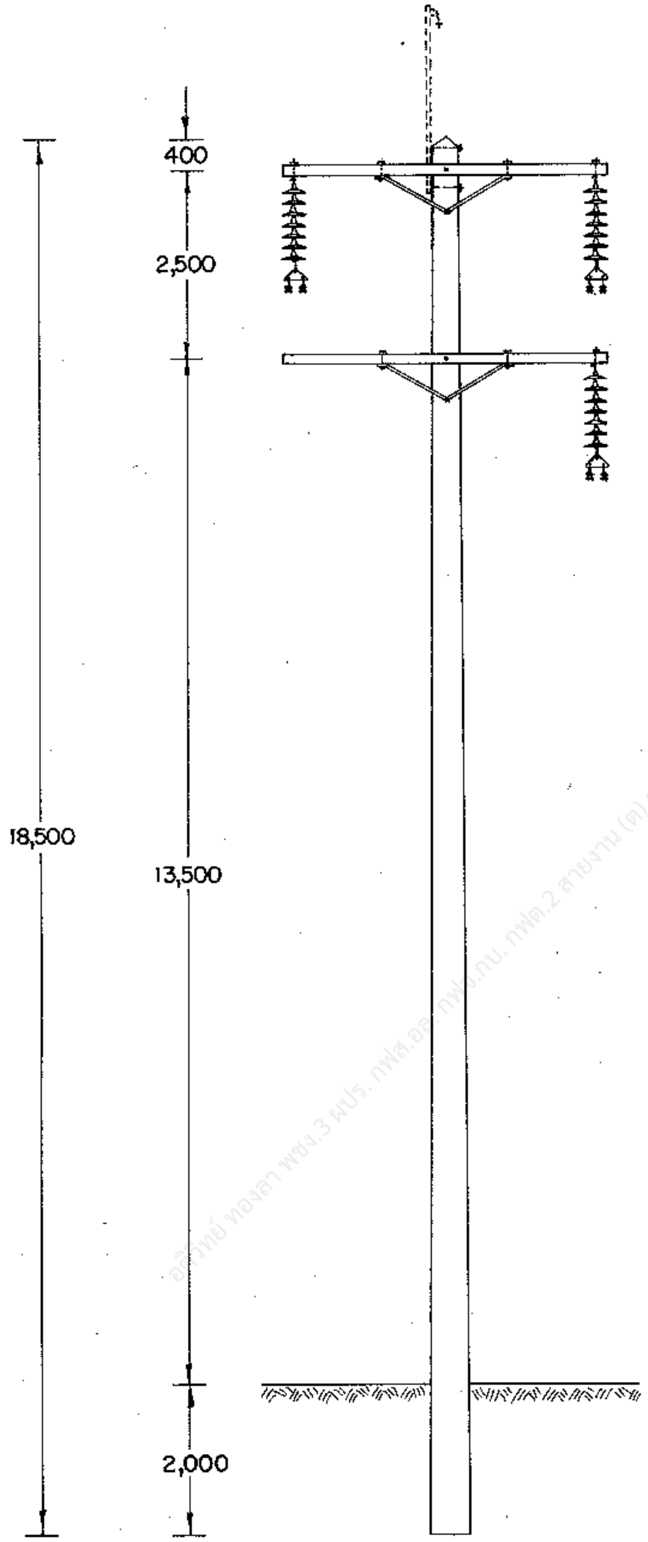

อดิศักดิ์ ทองลา พชง.3 ผปร. กฟส.อล. กฟน.กบ. กฟต.2 สายงาน (ต) ผวก. @PEA

กองวิศวกรรมไฟฟ้าและเครื่องกล
ฝ่ายวิศวกรรม

ผู้เขียน
ผู้ตรวจ
วิศวกร
หัวหน้าแผนก
หัวหน้ากอง
ผู้อำนวยการฝ่าย
23
รองผู้ว่าการฝ่ายเทคนิค

การไฟฟ้าส่วนภูมิภาค

ผู้ว่าการ 24 มี.ค. 23

115 kV วงจรเดี่ยว สายไฟฟ้าคู่
เสาสำหรับทางตรง ใช้เสาขนาด 18.50 ม.
แบบ SD - TG - 2

115 kV SINGLE CIRCUIT SINGLE CONDUCTOR
TANGENT STRUCTURE 18.50 m POLE
TYPE SD—TG—2

ใช้แทนแบบ
ถูกแทนโดยแบบ
เขียนเสร็จวันที่ 4 ม.ค. 23
แก้แบบวันที่
มิติเป็น มม.
มาตราส่วน 1 : 100
แบบเลขที่ SAI-015/23023
แผ่นที่ 1 ของจำนวน 3 แผ่น

ก.ค. 2523

การประกอบเลขที่
ASSEMBLY NO. 5426

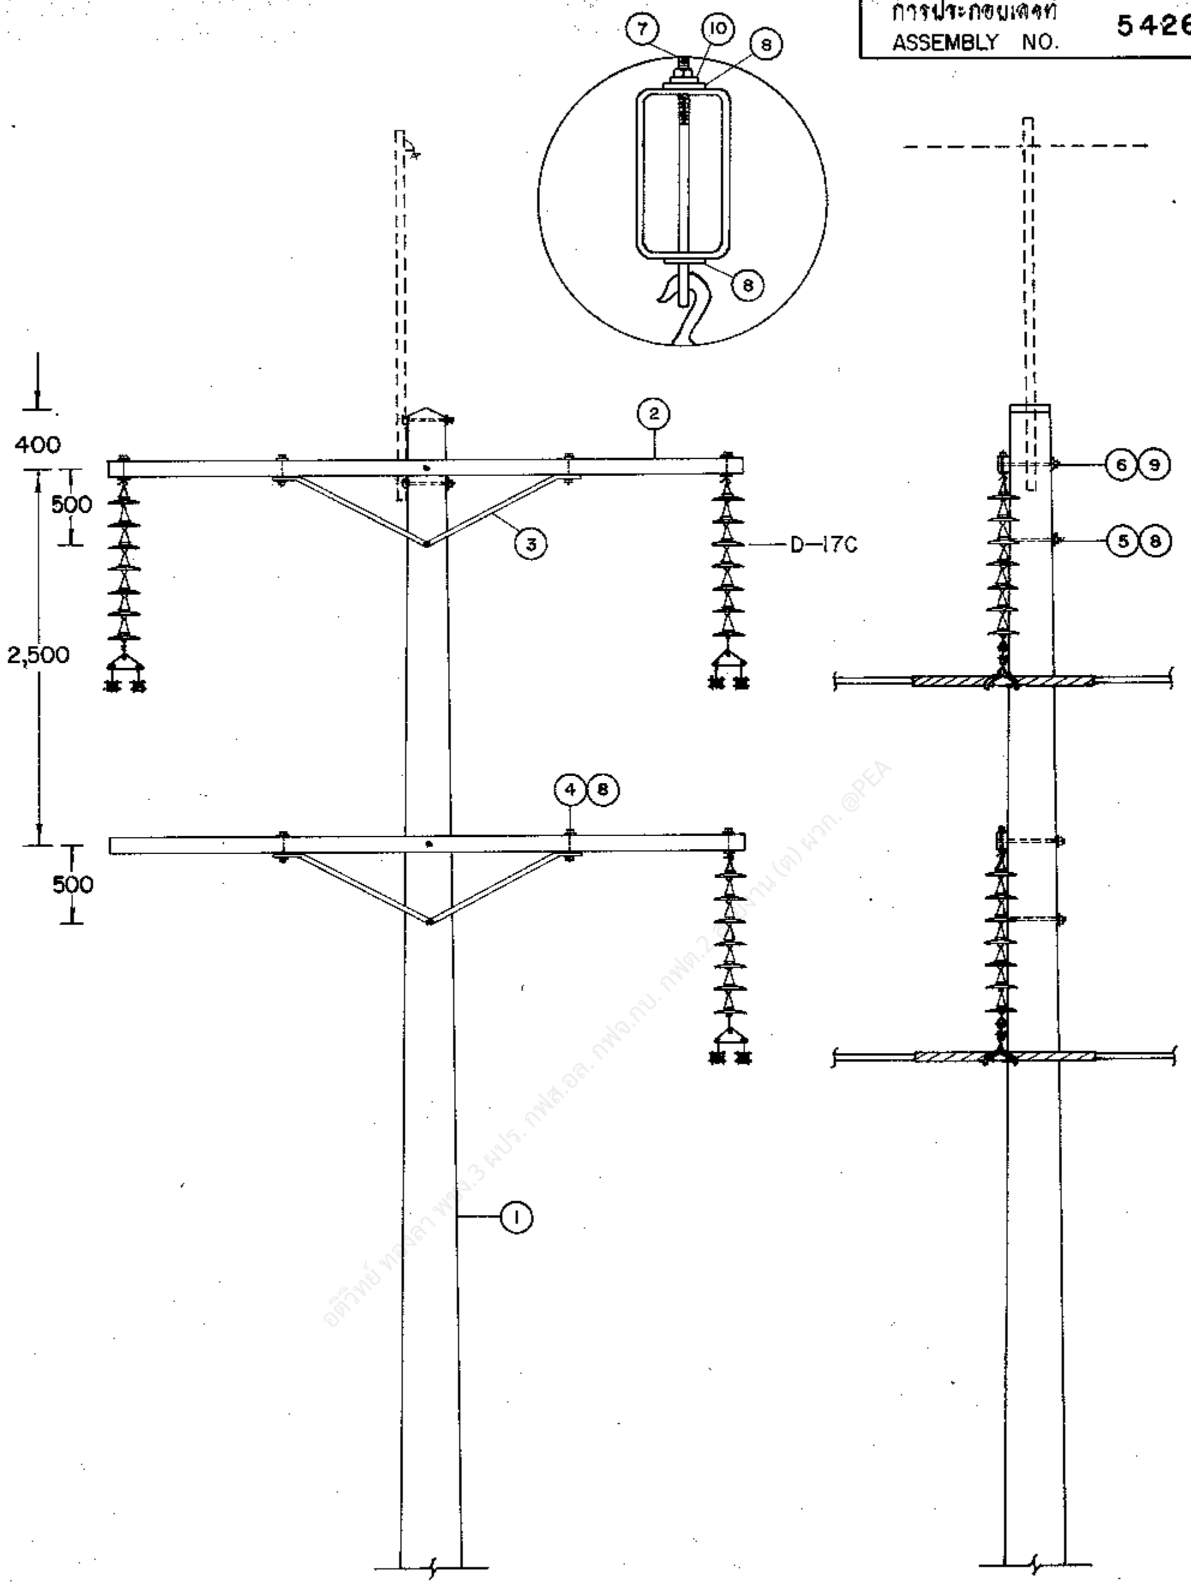

อดิวิทย์ ทองลา พชง.3 ผปร. กฟส.อล. กฟจ.กบ. กฟต.2 ... (ต) ผวก. @PEA

กองวิศวกรรมไฟฟ้าและเครื่องกล
ฝ่ายวิศวกรรม

ผู้เขียน
ผู้สำรวจ
วิศวกร
หัวหน้าแผนก
หัวหน้ากอง
ผู้อำนวยการฝ่าย
รองผู้ว่าการฝ่ายเทคนิค

การไฟฟ้าส่วนภูมิภาค

ผู้ว่าการ ๒๔ มี.ค. ๒๓

115 kV วงจรเดี่ยว สายไฟฟ้าคู่
เสาสำหรับทางตรง ใช้เสาขนาด 18.50 ม.
แบบ SD - TG - 2

115 kV SINGLE CIRCUIT SINGLE CONDUCTOR
TANGENT STRUCTURE 18.50 m POLE
TYPE SD—TG—2

ใช้แทนแบบ
ถูกแทนโดยแบบ
เขียนเสร็จวันที่ 4 ม.ค. 23
แก้แบบวันที่
มิติเป็น มม.
มาตราส่วน 1 : 75
แบบเลขที่ SAL-015/23023
แผ่นที่ 2 ของจำนวน 3 แผ่น

1 มี.ค. 2523

การประกอบเลขที่ ASSEMBLY NO.	5426

บัญชีวัสดุ
BILL OF MATERIAL

ลำดับที่ ITEM	รายละเอียด DESCRIPTION	จำนวน REQ'D	วัสดุเลขที่ MAT. NO.
1	เสาคอนกรีต 18.5 ม. POLE, CONCRETE 18.5 m LONG	1	00010009 (0039)
2	คอนสายแบบเหล็ก ขนาด 100 X 50 X 3.2 มม. ยาว 4.20 ม. CROSSARM, STEEL 100 X 50 X 3.2 mm , 4.20 m LONG	2	00120001 (0116)
3	เหล็กฉากรับคอนสาย ขนาด 50 X 50 X 6 มม. ช่วงกว้าง 1,800 มม. ดรอพ 450 มม. BRACE, ANGLE STEEL 50 X 50 X 6 mm , 1,800 mm WIDE 450 mm DROP	2	01200007 (0119)
4	สลักเกลียว M 16 X 130 มม. BOLT, MACHINE, M 16 X 130 mm	4	01110200 (0220)
5	สลักเกลียว M 16 X 350 มม. BOLT, MACHINE, M 16 X 350 mm	2	01110205 (0225)
6	สลักเกลียว M 20 X 400 มม. BOLT, MACHINE, M 20 X 400 mm	2	01110301 (0233)
7	สลักห่วง โอแวล M 16 X 150 มม. BOLT, OVAL EYE M 16 X 150 mm	3	01150000 (0257)
8	แหวนสี่เหลี่ยมแบน 52X52X4.5 มม. รู Ø 18 มม. มอก. 258 WASHER, SQUARE, FLAT 52X52X4.5 mm HOLE Ø 18 mm TIS 258	12	01180100 (0355)
9	แหวนสี่เหลี่ยมแบน 62 X 62 X 6 มม. รู Ø 22 มม. มอก. 258 WASHER, SQUARE, FLAT 62 X 62 X 6 mm HOLE Ø 22 mm TIS 258	4	01180101 (0356)
10	แหวนสปริง M 16 มอก. 259 WASHER, LOCK, M 16, TIS 259	3	01180301 (0365)

รายละเอียด
DETAIL

D-17C	การประกอบลูกถ้วยแขวน SUSPENSION INSULATOR ASSEMBLY	3	
D-10A	ฐานรากเสา POLE FOUNDATION	1	

อดิวิทย์ ทองลา พชง.3 ผปร. กฟส.อล. กฟจ.กบ. กฟต.2 สายงาน (ต) ผวก. @PEA

กองวิศวกรรมไฟฟ้าและเครื่องกล
ฝ่ายวิศวกรรม

ผู้เขียน
ผู้สำรวจ
วิศวกร
หัวหน้าแผนก
หัวหน้ากอง
ผู้อำนวยการฝ่าย
28 [illegible] 23
รองผู้ว่าการฝ่ายเทคนิค

การไฟฟ้าส่วนภูมิภาค

ผู้ว่าการ 24 มี.ค.23

115 kV วงจรเดี่ยว สายไฟฟ้าคู่
เสาสำหรับทางตรง ใช้เสาขนาด 18.50 ม.
แบบ SD-TG-2

115 kV SINGLE CIRCUIT SINGLE CONDUCTOR
TANGENT STRUCTURE 18.50 m POLE
TYPE SD-TG-2

ใช้แทนแบบ
ถูกแทนโดยแบบ
เขียนเสร็จวันที่ 4 ม.ค. 23
แก้แบบวันที่
มิติเป็น
มาตราส่วน
แบบเลขที่ SAL-015/23023
แผ่นที่ 3 ของจำนวน 3 แผ่น

[illegible] มี.ค. 2523