การประกอบเลขที่
ASSEMBLY NO. **5203**

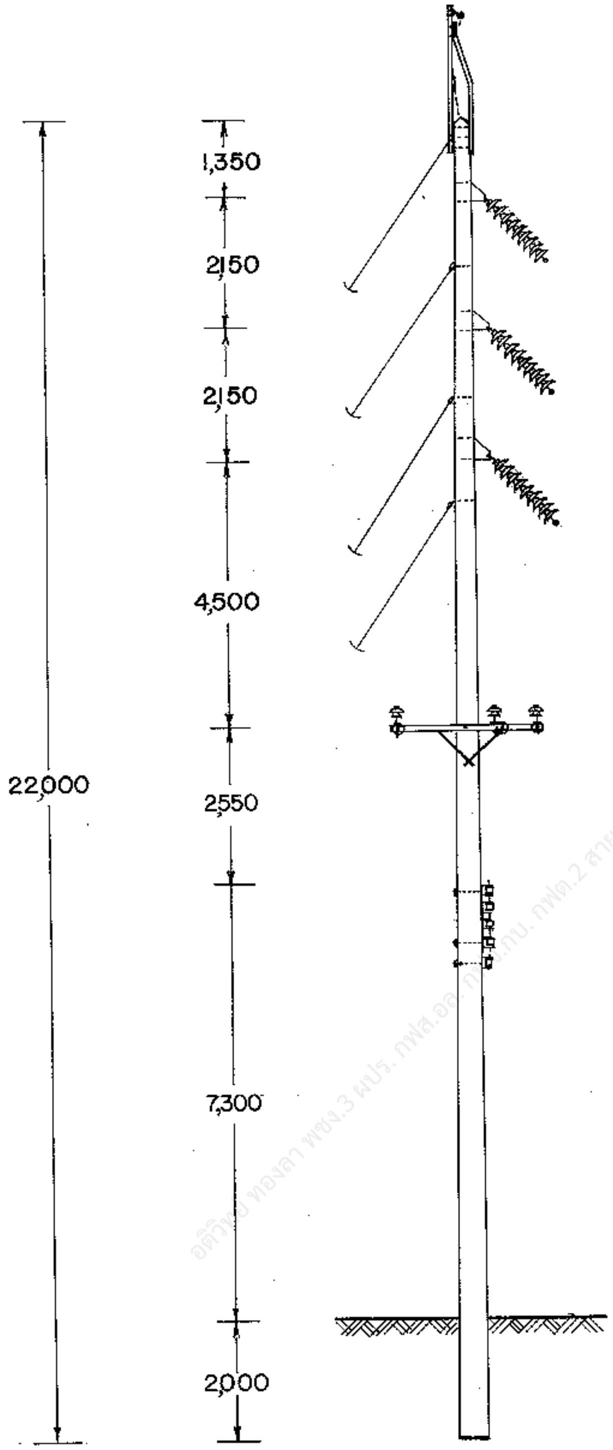

แบบ
TYPE SS-MA-1

อดิศักดิ์ ทองลา พชง.3 ผปร. กฟส.อล. กบ. กฟต.2 สายงาน (ต) ผวก. @PEA

JAPANESE EXPERT TO PEA.

กองวิศวกรรม	**การไฟฟ้าส่วนภูมิภาค**	ใช้แทนแบบ.......... ถูกแทนโดยแบบ..........
ผู้เขียน.......... สถาปนิก.......... วิศวกร.......... หัวหน้าแผนก.......... ผู้อำนวยการกอง..........	ผู้ว่าการ.......... 26 มี.ค.19	เขียนเสร็จวันที่ 17 มี.ค.19 แก้แบบวันที่ 24 มี.ค.23 มิติเป็น มม. มาตราส่วน 1 : 125
	แบบโครงสร้างเสาส่งระบบ 115 KV วงจรเดี่ยว แบบเสาสำหรับทางโค้ง	
รองผู้ว่าการฝ่ายเทคนิค	115 kV. LINE STRUCTURE CONSTRUCTURE SINGLE CIRCUIT MEDIUM ANGLE STRUCTURE	แบบเลขที่ S02-015/19022 แผ่นที่ 1 ของจำนวน 3 แผ่น

การประกอบเลขที่
ASSEMBLY NO. 5203

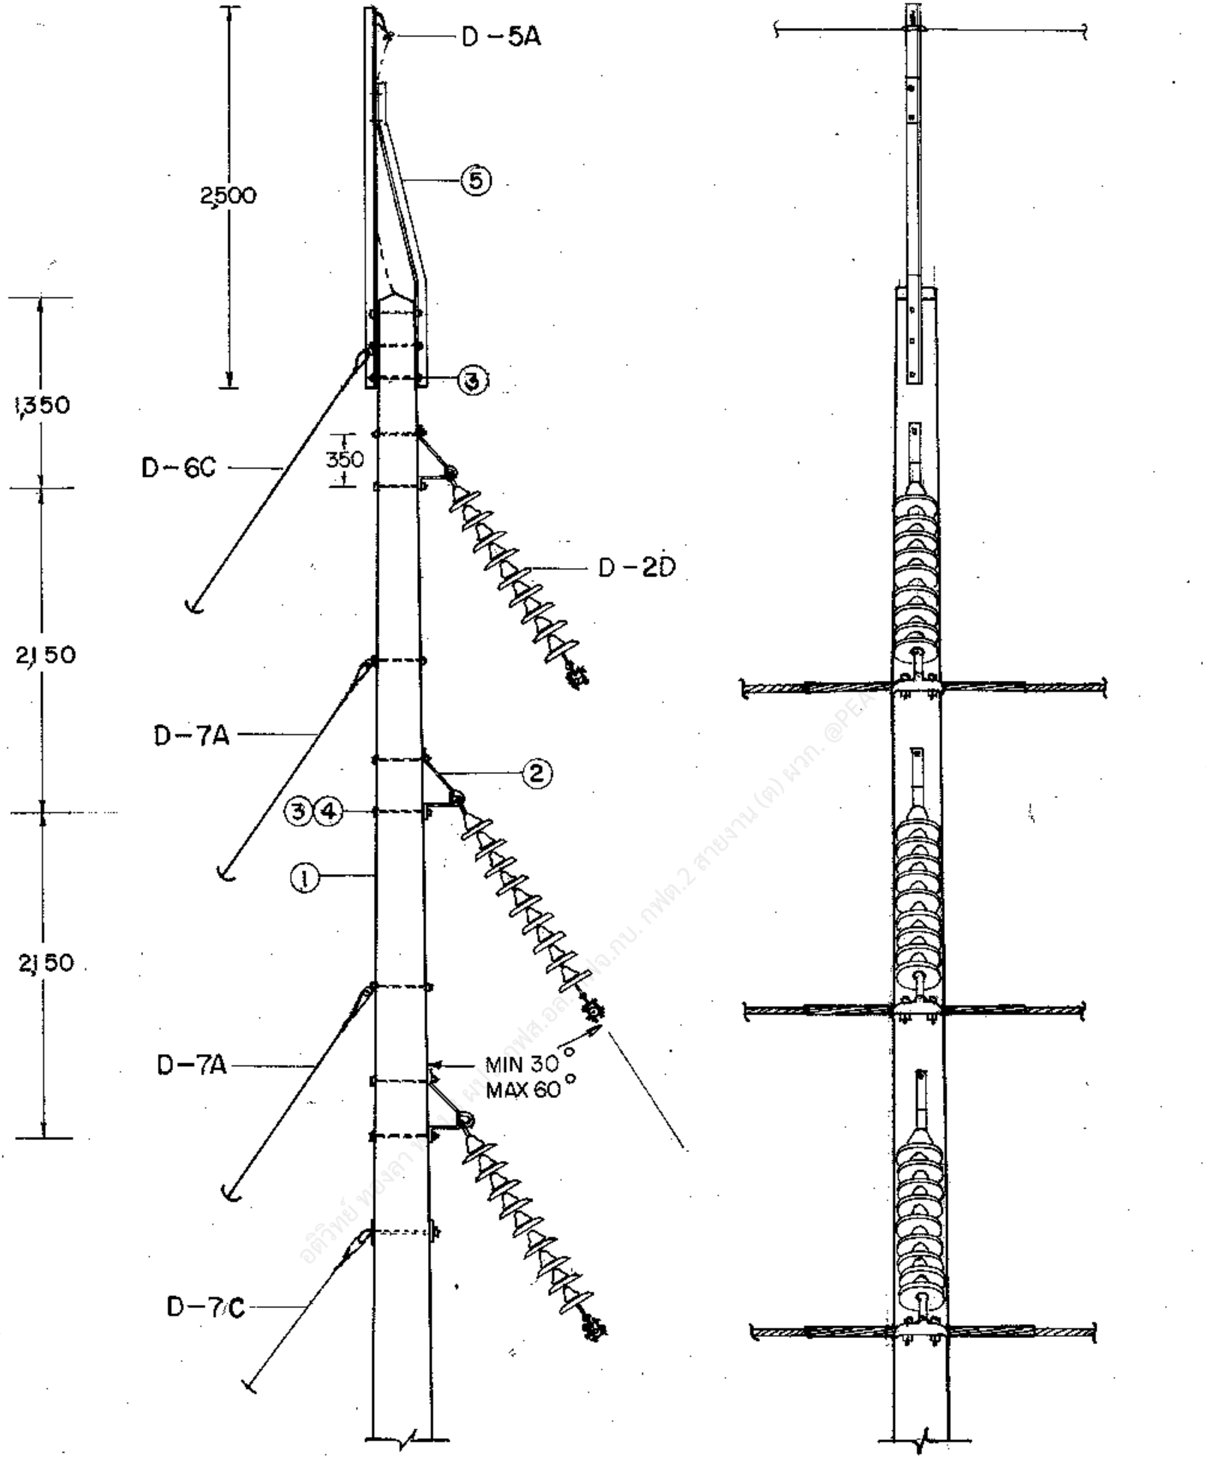
D-5A
⑤
2,500
③
1,350
350
D-6C
D-2D
2,150
D-7A
②
③④
①
2,150
D-7A
MIN 30°
MAX 60°
D-7C

JAPANESES EXPERT TO PEA. Yamada

กองวิศวกรรม

ผู้เขียน
สถาปนิก
วิศวกร
หัวหน้าแผนก
ผู้อำนวยการกอง
รองผู้ว่าการฝ่ายเทคนิค

การไฟฟ้าส่วนภูมิภาค

ผู้ว่าการ 26 มี.ค. 19

แบบโครงสร้างเสาส่งระบบ 115 kV
วงจรเดี่ยว
แบบเสาสำหรับทางโค้ง

115 kV. LINE STRUCTURE CONSTRUCTION
SINGLE CIRCUIT
MEDIUM ANGLE STRUCTURE

ใช้แทนแบบ
ถูกแทนโดยแบบ
เขียนเสร็จวันที่ 17 มี.ค. 19
แก้แบบวันที่ 24 มี.ค. 23 15 ก.ย. 40
มิติเป็น ม.ม.
มาตราส่วน 1:50
แบบเลขที่ S02-015/19022
แผ่นที่ 2 ของจำนวน 3 แผ่น

การประกอบเลขที่
ASSEMBLY NO. 5203

บัญชีวัสดุ
BILL OF MATERIAL

ลำดับที่ ITEM	รายละเอียด DESCRIPTION	จำนวน REQ'D	วัสดุเลขที่ MAT NO.
1	เสาคอนกรีต 22 ม. POLE, CONCRETE 22 m LONG	1	00010011 (0041)
2	ที่แขวนลูกถ้วยทางโค้ง BRACKET, CORNER SUSPENSION	3	03140012 (0489)
3	สลักเกลียว M 16X350 มม. BOLT, MACHINE, M 16 X 350 mm.	8	01110205 (0225)
4	แหวนสี่เหลี่ยมแบน 5.2x5.2x4.5มม. รู Ø 18 มม. มอก. 258 WASHER, SQUARE, FLAT 5.2x5.2x4.5 mm HOLE Ø 18 mm TIS. 258	6	01180100 (0355)
5	เหล็กฉากรับสายล่อฟ้าทางโค้ง OVERHEAD GROUND WIRE CORNER BAYONET	1	01010005 (0136)
	รายละเอียด DETAIL		
D-2D	การประกอบลูกถ้วยแขวน SUSPENSION INSULATOR ASSEMBLY	3	
D-5A	การต่อสายล่อฟ้า OVERHEAD GROUND WIRE CONNECTION	1	
D-6C	การประกอบสายยึดโยงลวดเหล็กตีเกลียว 50 ต.มม. STEEL STRANDED WIRE 50 mm^2 GUY ASSEMBLY	1	
D-7A	การประกอบสายยึดโยงลวดเหล็กตีเกลียว 95 ต.มม. STEEL STRANDED WIRE 95 mm^2 GUY ASSEMBLY	2	
D-7C	การประกอบสายยึดโยงลวดเหล็กตีเกลียว 95 ต.มม. STEEL STRANDED WIRE 95 mm^2 GUY ASSEMBLY	1	
D-9C	สมอบกคอนกรีต CONCRETE ANCHOR	1	
D-10A	ฐานรากเสา POLE FOUNDATION	1	

อติวิทย์ ทองลา พชง.3 ฝปร. กฟส. [illegible] สายงาน (ต) ผวก. @PEA

JAPANESE EXPERT TO PEA. Yamao

กองวิศวกรรม

ผู้เขียน
สถาปนิก
วิศวกร
หัวหน้าแผนก
ผู้อำนวยการกอง
รองผู้ว่าการฝ่ายเทคนิค

การไฟฟ้าส่วนภูมิภาค

ผู้ว่าการ 26 มี.ค. 19

แบบโครงสร้างเสาส่งระบบ 115 KV
วงจรเดี่ยว
แบบเสาสำหรับทางโค้ง

115 kV. LINE STRUCTURE CONSTRUCTION
SINGLE CIRCUIT
MEDIUM ANGLE STRUCTURE

ใช้แทนแบบ........
ถูกแทนโดยแบบ........
เขียนเสร็จวันที่ 17 มี.ค.19
แก้แบบวันที่ 24 มี.ค. 23
15 ก.ย. 40
มิติเป็น........
มาตราส่วน........
แบบเลขที่ S02-015/19022
แผ่นที่ 3 จากจำนวน 3 แผ่น