

การประกอบเลขที่
ASSEMBLY NO. 0553

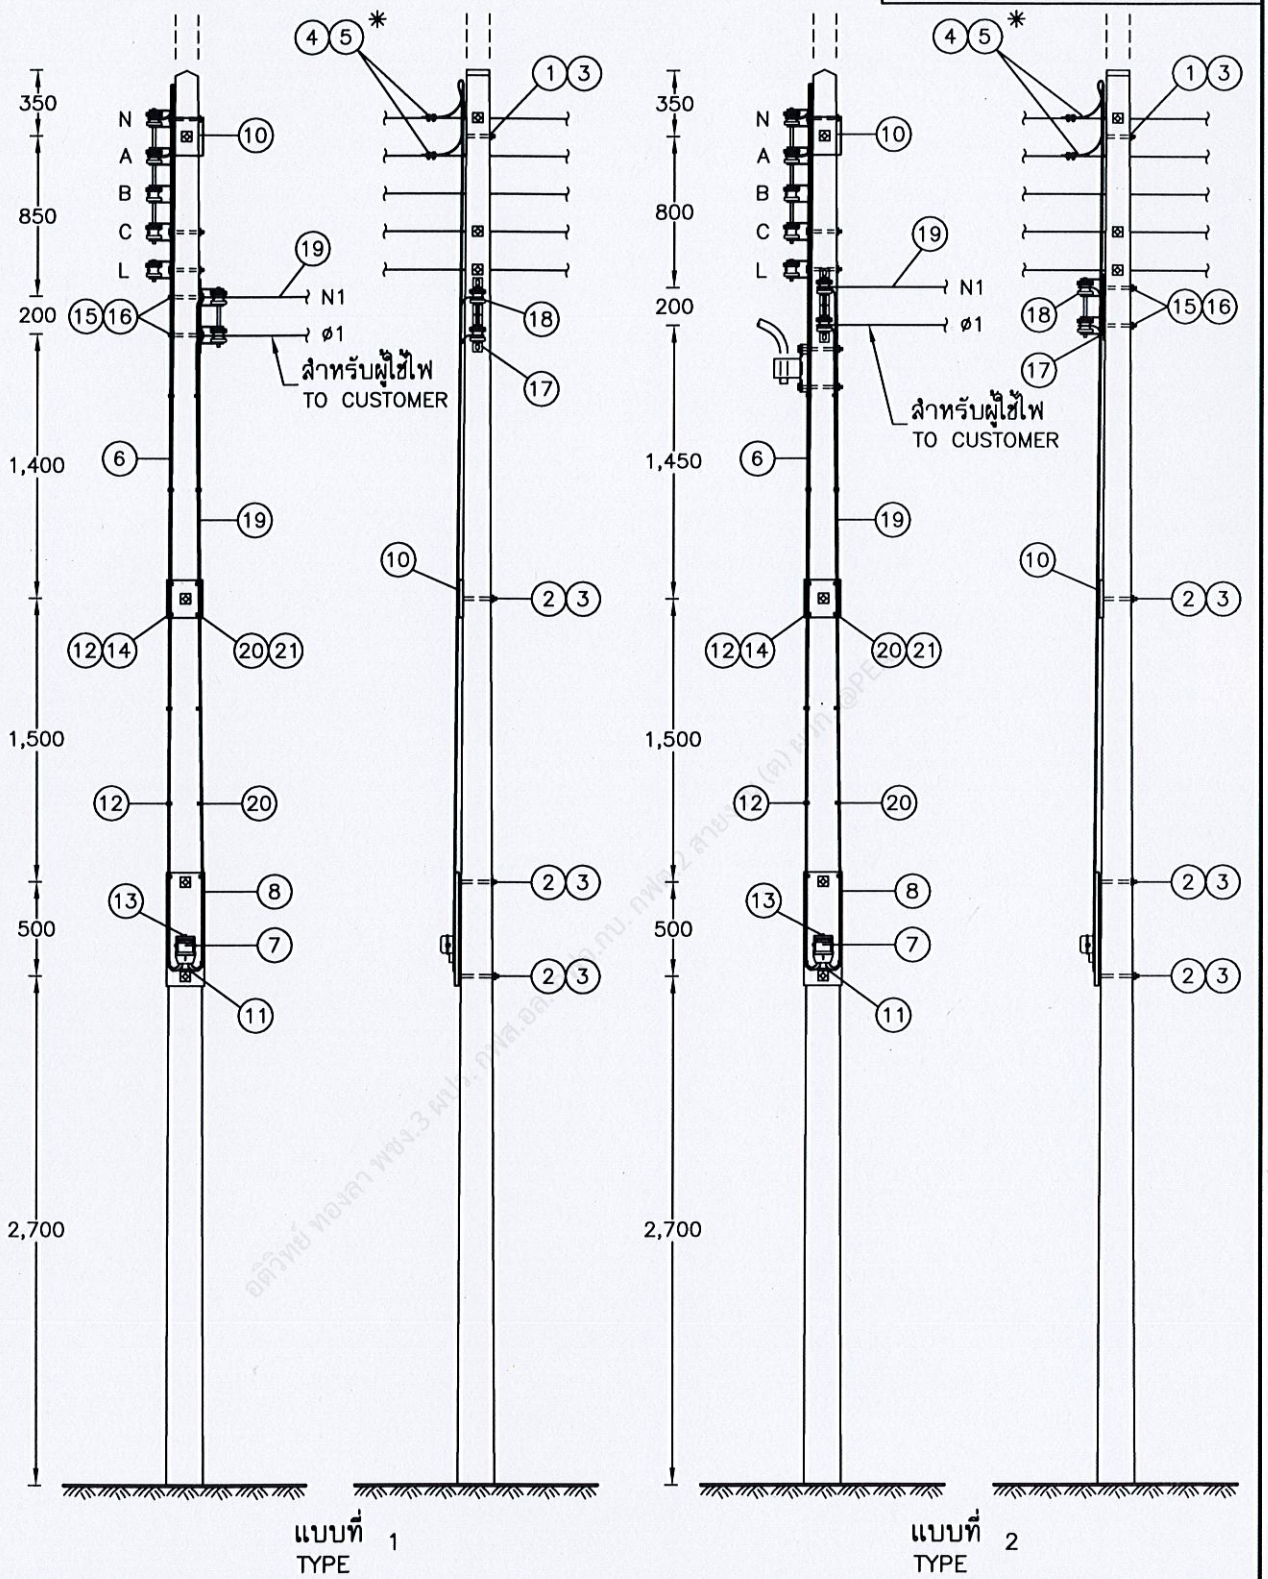


กองวิศวกรรมระบบไฟฟ้า ฝ่ายวิศวกรรม	การไฟฟ้าส่วนภูมิภาค	ใช้แทนแบบ ..... ถูกแทนโดยแบบ .....
ผู้เขียน Supphakit Boonrung ผู้สำรวจ ..... วิศวกร Supphakit Boonrung หัวหน้าแผนก อนุวัตร ผู้อำนวยการกอง ..... ผู้อำนวยการฝ่าย	ผู้ว่าการ ..... (แทน) 15 พ.ย. 2564	เขียนเสร็จวันที่ 15 ต.ค. 2564 แก้แบบวันที่ ..... มิติเป็น มิลลิเมตร มาตราส่วน 1 : 40
รองผู้ว่าการสายงานวิศวกรรม	การติดตั้งอิเล็กทรอนิกส์มิเตอร์พร้อมระบบสื่อสารไร้สาย 1 เฟส 230 โวลต ขนาด 5 (100) แอมป์ บนเสาระบบจำหน่าย I จำนวน 1 เครื่อง 5(100) A, 1 PHASE, 230 V ELECTRONIC METER WITH WIRELESS COMMUNICATION INSTALLATION ON DISTRIBUTION CONCRETE POLE I 1 UNIT	แบบเลขที่ SA4-015/64018 แผ่นที่ 1 ของจำนวน 7 แผ่น

การประกอบเลขที่ ASSEMBLY NO. 0553

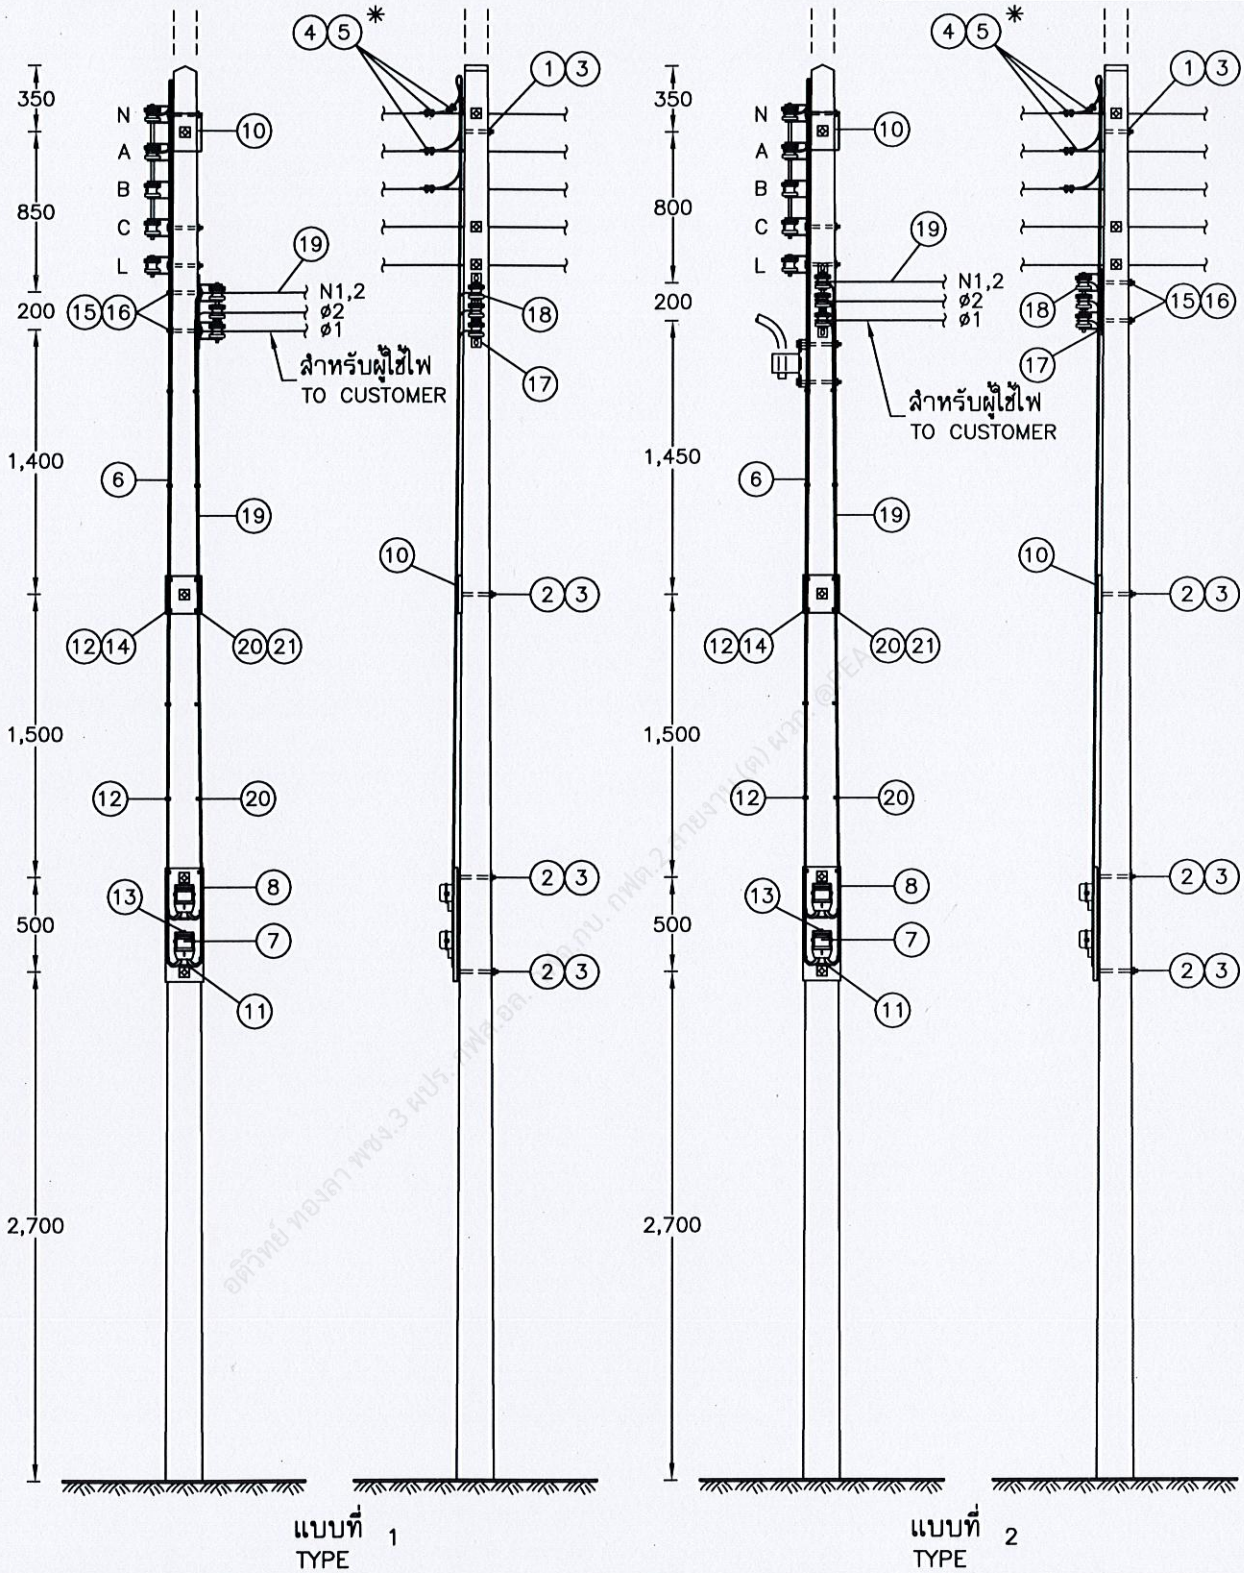

กองวิศวกรรมระบบไฟฟ้า ฝ่ายวิศวกรรม	การไฟฟ้าส่วนภูมิภาค	ใช้แทนแบบ ..... ถูกแทนโดยแบบ .....
ผู้เขียน Supphakit Boonreung ผู้สำรวจ ..... วิศวกร Supphakit Boonreung หัวหน้าแผนก อนุวัตร ผู้อำนวยการกอง ..... ผู้อำนวยการฝ่าย	ผู้ว่าการ ..... (แทน) 15 พ.ย. 2564	เขียนเสร็จวันที่ 15 ต.ค. 2564 แก้แบบวันที่ ..... มิติเป็น มิลลิเมตร มาตราส่วน 1 : 40
รองผู้ว่าการสายงานวิศวกรรม	การติดตั้งอิเล็กทรอนิกส์มิเตอร์พร้อมระบบสื่อสารไร้สาย 1 เฟส 230 โวลต์ ขนาด 5 (100) แอมแปร์ บนเสาระบบจำหน่าย II จำนวน 2 เครื่อง	
	5(100) A, 1 PHASE, 230 V ELECTRONIC METER WITH WIRELESS COMMUNICATION INSTALLATION ON DISTRIBUTION CONCRETE POLE II 2 UNITS	แบบเลขที่ SA4-015/64018 แผ่นที่ 2 ของจำนวน 7 แผ่น

การประกอบเลขที่ ASSEMBLY NO. 0553

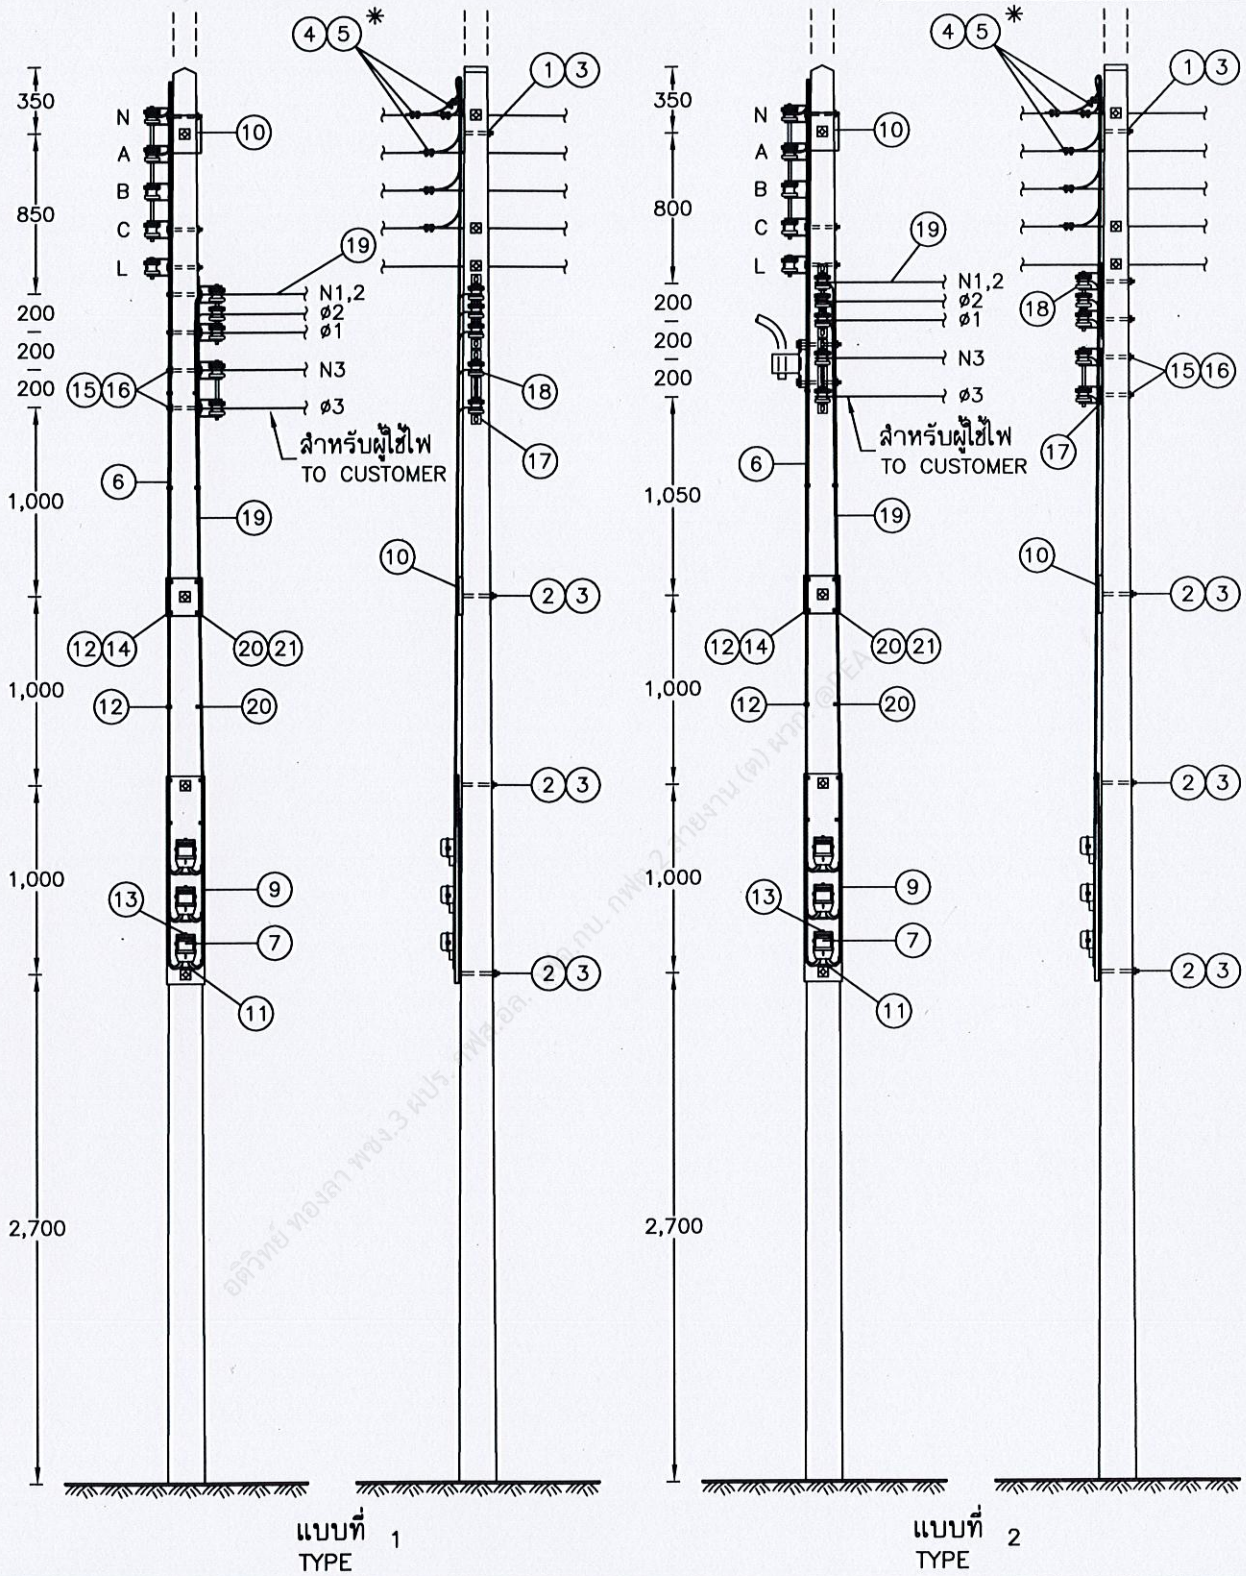


แบบที่ 1 TYPE

แบบที่ 2 TYPE

กองวิศวกรรมระบบไฟฟ้า ฝ่ายวิศวกรรม	การไฟฟ้าส่วนภูมิภาค	ใช้แทนแบบ ..... ถูกแทนโดยแบบ .....
ผู้เขียน ..Supphakit Boonruang.. ผู้สำรวจ ..... วิศวกร..Supphakit Boonruang.. หัวหน้าแผนก...อนุวัตร..... ผู้อำนวยการกอง..... ผู้อำนวยการฝ่าย.....	ผู้ว่าการ.....15 พ.ย. 2564 (แทน)	เขียนเสร็จวันที่ 15 ต.ค. 2564 แก้แบบวันที่ ..... มิติเป็น...มิลลิเมตร..... มาตราส่วน....1 : 40.....
รองผู้ว่าการสายงานวิศวกรรม	การติดตั้งอิเล็กทรอนิกส์มิเตอร์พร้อมระบบสื่อสารไร้สาย 1 เฟส 230 โวลต์ ขนาด 5 (100) แอมแปร์ บนเสาระบบจำหน่าย III จำนวน 3 ครื่อง 5(100) A, 1 PHASE, 230 V ELECTRONIC METER WITH WIRELESS COMMUNICATION INSTALLATION ON DISTRIBUTION CONCRETE POLE III 3 UNITS	แบบเลขที่ SA4–015/64018 แผ่นที่ 3 ของจำนวน 7 แผ่น

การประกอบเลขที่ ASSEMBLY NO. 0553

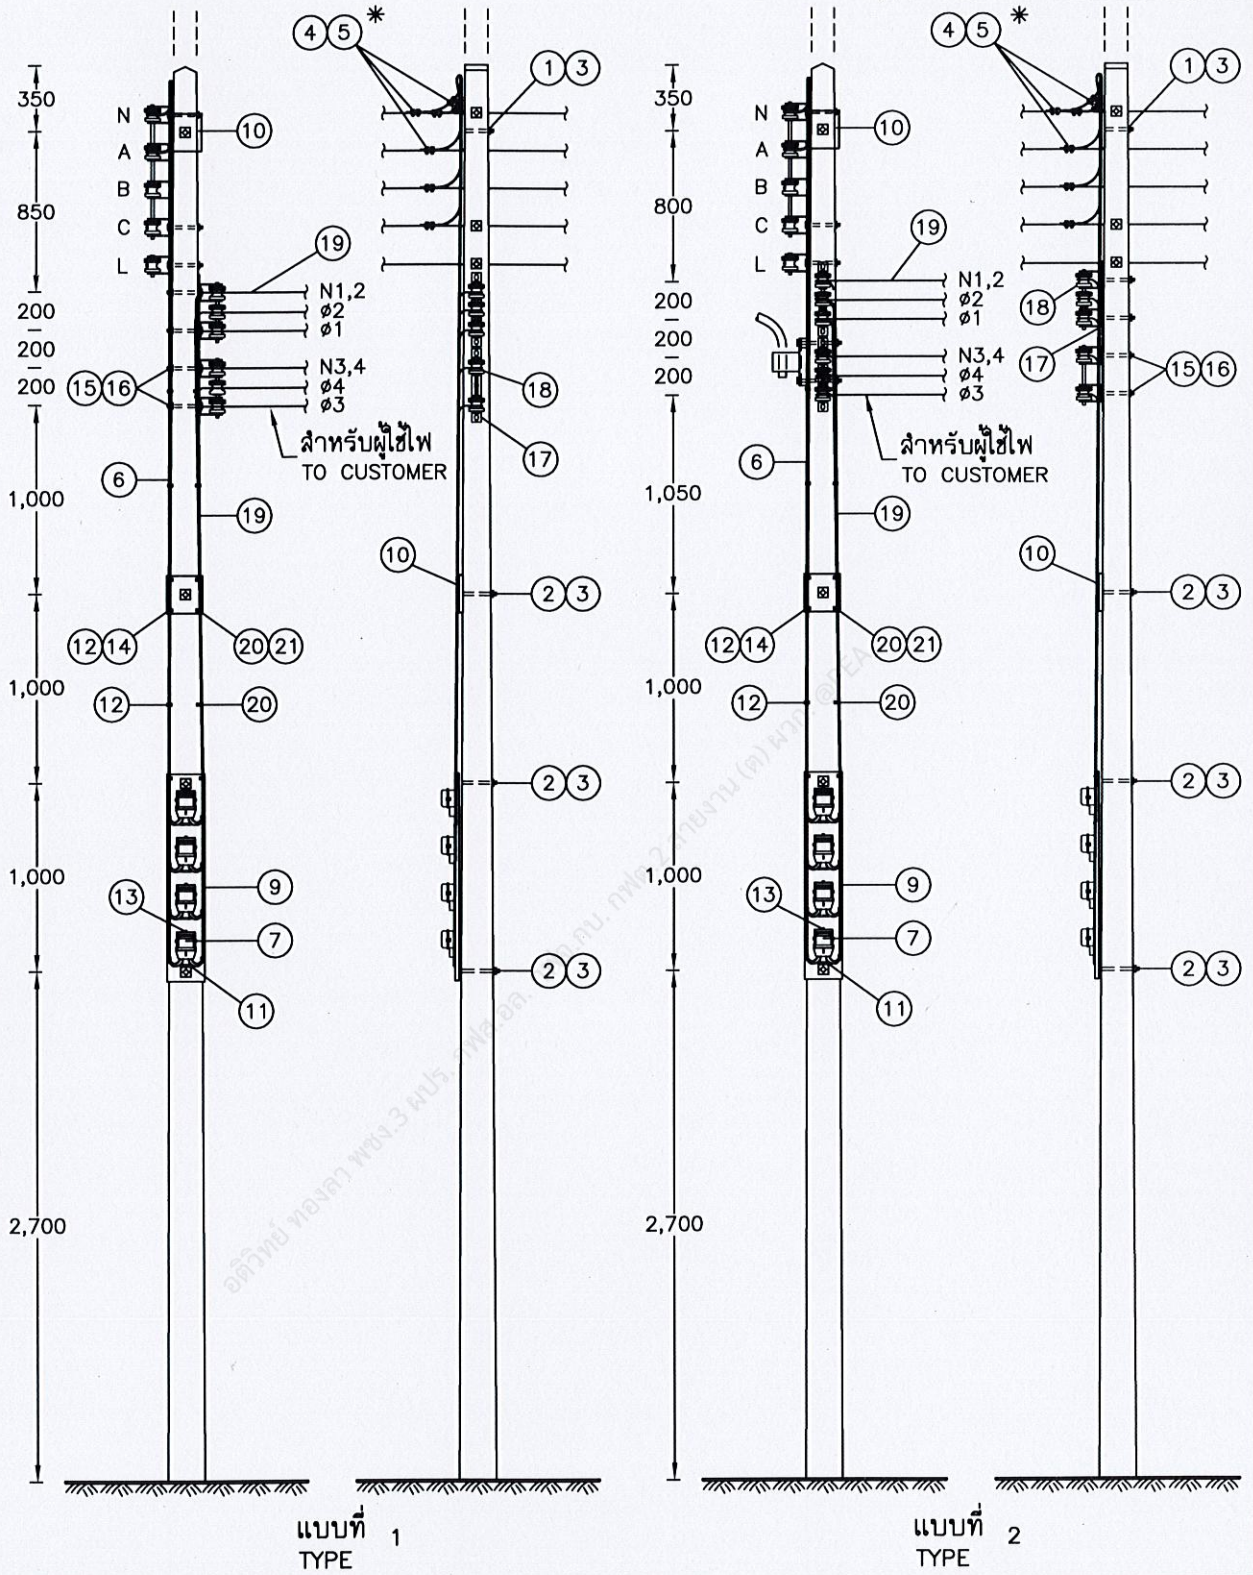

แบบที่ 1 TYPE

แบบที่ 2 TYPE

กองวิศวกรรมระบบไฟฟ้า ฝ่ายวิศวกรรม	การไฟฟ้าส่วนภูมิภาค	ใช้แทนแบบ ..... ถูกแทนโดยแบบ .....
ผู้เขียน Suphakit Boonrung ผู้สำรวจ ..... วิศวกร Suphakit Boonrung หัวหน้าแผนก อนุวัตร ผู้อำนวยการกอง ..... ผู้อำนวยการฝ่าย 2/ต.ค.	ผู้ว่าการ ..... 15 พ.ย. 2564 (แทน) การติดตั้งอิเล็กทรอนิกส์มิเตอร์พร้อมระบบสื่อสารไร้สาย 1 เฟส 230 โวลต์ ขนาด 5 (100) แอมแปร บนเสาระบบจำหน่าย IV จำนวน 4 เครื่อง	เขียนเสร็จวันที่ 15 ต.ค. 2564 แก้แบบวันที่ ..... มิติเป็น มิลลิเมตร มาตราส่วน 1 : 40
รองผู้ว่าการสายงานวิศวกรรม	5(100) A, 1 PHASE, 230 V ELECTRONIC METER WITH WIRELESS COMMUNICATION INSTALLATION ON DISTRIBUTION CONCRETE POLE IV 4 UNITS	แบบเลขที่ SA4-015/64018 แผ่นที่ 4 ของจำนวน 7 แผ่น

การประกอบเลขที่ ASSEMBLY NO.	0553

บัญชีวัสดุ
BILL OF MATERIAL

ลำดับที่ ITEM	รายละเอียด DESCRIPTION	จำนวน REQ'D I	II	III	IV	วัสดุเลขที่ MAT. NO.
	บัญชีวัสดุในส่วนที่ กฟภ. ลงทุน BILL OF MATERIAL FOR PEA					
1	สลักเกลียว M 16 x 200 มม. สำหรับเสาคอนกรีต 9.00 ม. BOLT, MACHINE, M 16 x 200 mm FOR 9.00 m CONCRETE POLE	1	1	1	1	1010110202
	สลักเกลียว M 16 x 250 มม. สำหรับเสาคอนกรีต 12.00 ม. BOLT, MACHINE, M 16 x 250 mm FOR 12.00 m CONCRETE POLE					1010110203
	สลักเกลียว M 16 x 300 มม. สำหรับเสาคอนกรีต 12.20, 14.00 ม. BOLT, MACHINE, M 16 x 300 mm FOR 12.20, 14.00 m CONCRETE POLE					1010110204
	สลักเกลียว M 16 x 350 มม. สำหรับเสาคอนกรีต 14.30, 16.00 ม. BOLT, MACHINE, M 16 x 350 mm FOR 14.30, 16.00 m CONCRETE POLE					1010110205
2	สลักเกลียว M 16 x 250 มม. สำหรับเสาคอนกรีต 9.00 ม. BOLT, MACHINE, M 16 x 250 mm FOR 9.00 m CONCRETE POLE	3	3	3	3	1010110203
	สลักเกลียว M 16 x 300 มม. สำหรับเสาคอนกรีต 12.00 ม. BOLT, MACHINE, M 16 x 300 mm FOR 12.00 m CONCRETE POLE					1010110204
	สลักเกลียว M 16 x 350 มม. สำหรับเสาคอนกรีต 12.20, 14.00 ม. BOLT, MACHINE, M 16 x 350 mm FOR 12.20, 14.00 m CONCRETE POLE					1010110205
	สลักเกลียว M 16 x 400 มม. สำหรับเสาคอนกรีต 14.30, 16.00 ม. BOLT, MACHINE, M 16 x 400 mm FOR 14.30, 16.00 m CONCRETE POLE					1010110206
3	แหวนสี่เหลี่ยมแบน 52x52x4.5 มม. รู ø 18 มม. มอก. 258 WASHER, SQUARE, FLAT 52x52x4.5 mm HOLE ø18 mm TIS 258	8	8	8	8	1010180100
4	คอนเนคเตอร์ชนิดบีบ แบบ H ขนาดตามต้องการ CONNECTOR, COMPRESSION, H TYPE ; SIZE AS REQUIRED	2	4	6	8	1020320002-6
5	PVC เทป กว้าง 19 มม. (ใช้ความยาว 2 ม. ต่อ 1 จุด) มอก. 386 PVC TAPE, 19 mm WIDE (2 m LONG PER POINT) TIS 386	ม. m	ม. m	ม. m	ม. m	1020180001 or 1020180002
6 a	สายทองแดง ขนาด 2x10 ตร.มม. หุ้มฉนวน PVC 600 โวลต์ สำหรับขนาดโหลดสูงสุดไม่เกิน 36 แอมแปร์ CABLE, Cu, 2x10 mm^2, PVC INSULATOR, 600 V FOR MAXIMUM LOAD NOT MORE THAN 36 A	ม. 5 m	ม. 11 m	ม. 17 m	ม. 23 m	1020080501
6 b	สายทองแดง ขนาด 2x35 ตร.มม. หุ้มฉนวน PVC 600 โวลต์ สำหรับขนาดโหลดสูงสุดไม่เกิน 80 แอมแปร์ CABLE, Cu, 2x35 mm^2, PVC INSULATOR, 600 V FOR MAXIMUM LOAD NOT MORE THAN 80 A					1020080502
7	อิเล็กทรอนิกส์มิเตอร์พร้อมระบบสื่อสารไร้สาย 1 เฟส 230 โวลต์ 5 (100) แอมแปร์ 1 PHASE, 230 V, 5(100) A, ELECTRONIC METER WITH WIRELESS COMMUNICATION	1	2	3	4	1060050019
8	แป้นรองรับมิเตอร์ ตกแต่งผิวเรียบร้อยแล้ว ขนาด 60x20x2 ซม. METER PLATE, SURFACE FINISHED, 60x20x2 cm	1	1	–	–	1060100001
9	แป้นรองรับมิเตอร์ ตกแต่งผิวเรียบร้อยแล้ว ขนาด 120x20x2 ซม. METER PLATE, SURFACE FINISHED, 120x20x2 cm	–	–	1	1	1060100002
10	แป้นสำหรับยึดสาย เข้าและออกจากมิเตอร์ ตกแต่งผิวเรียบร้อยแล้ว ขนาด 20x20x2 ซม. CABLE PLATE, SURFACE FINISHED, 20x20x2 cm	2	2	2	2	1060100000

กองวิศวกรรมระบบไฟฟ้า ฝ่ายวิศวกรรม	การไฟฟ้าส่วนภูมิภาค	ใช้แทนแบบ ..... ถูกแทนโดยแบบ .....
ผู้เขียน Supphakit Boonreung ผู้สำรวจ – วิศวกร Supphakit Boonreung หัวหน้าแผนก อนุวัตร ผู้อำนวยการกอง ผู้อำนวยการฝ่าย	ผู้ว่าการ ..... 15 พ.ย. 2564 (แทน)	เขียนเสร็จวันที่ 15 ต.ค. 2564 แก้แบบวันที่ ..... มิติเป็น ..... มาตราส่วน .....
รองผู้ว่าการสายงานวิศวกรรม –	การติดตั้งอิเล็กทรอนิกส์มิเตอร์พร้อมระบบสื่อสารไร้สาย 1 เฟส 230 โวลต์ ขนาด 5 (100) แอมแปร์ บนเสาระบบจำหน่าย 5(100) A, 1 PHASE, 230 V ELECTRONIC METER WITH WIRELESS COMMUNICATION INSTALLATION ON DISTRIBUTION CONCRETE POLE	แบบเลขที่ SA4-015/64018 แผ่นที่ 5 ของจำนวน 7 แผ่น

การประกอบเลขที่ ASSEMBLY NO.	0553

บัญชีวัสดุ
BILL OF MATERIAL

ลำดับที่ ITEM		รายละเอียด DESCRIPTION	จำนวน REQ'D I	II	III	IV	วัสดุเลขที่ MAT. NO.
11		หมายเลขผู้ใช้ไฟ NUMBER OF CUSTOMER	1	2	3	4	–
12		เข็มขัดรัดสาย (ทำด้วยลวดอะลูมิเนียมแบบ 1x10 มม.) ช่วงระยะ 50 ซม. CABLE STRAP (MADE OF ARMOUR TAPE 1x10 mm) AT 50 cm INTERVALS	ม. 2 m	ม. 3 m	ม. 5 m	ม. 5 m	1020200000
13		ตะปูเกลียวชุบโครเมี่ยม ขนาด 15–20 มม. SCREW, CHROME PLATED, SIZE 15–20 mm	3	6	9	12	
14		ตะปูหัวกลมแบน ยาว 15–20 มม., 1.00 มม. มอก.113 NAIL, ROUND MILD STEEL WIRE, 15–20 mm LONG, 1.00 mm TIS 113	24	24	40	40	
		บัญชีวัสดุในส่วนของผู้ใช้ไฟ BILL OF MATERIAL FOR CUSTOMER					
15		สลักเกลียว M 16 x 200 มม. สำหรับเสาคอนกรีต 9.00 ม. BOLT, MACHINE, M 16 x 200 mm FOR 9.00 m CONCRETE POLE	2	2	4	4	1010110202
		สลักเกลียว M 16 x 250 มม. สำหรับเสาคอนกรีต 12.00 ม. BOLT, MACHINE, M 16 x 250 mm FOR 12.00 m CONCRETE POLE					1010110203
		สลักเกลียว M 16 x 300 มม. สำหรับเสาคอนกรีต 12.20, 14.00 ม. BOLT, MACHINE, M 16 x 300 mm FOR 12.20, 14.00 m CONCRETE POLE					1010110204
		สลักเกลียว M 16 x 350 มม. สำหรับเสาคอนกรีต 14.30, 16.00 ม. BOLT, MACHINE, M 16 x 350 mm FOR 14.30, 16.00 m CONCRETE POLE					1010110205
16		แหวนสี่เหลี่ยมแบน 52x52x4.5 มม. รู ø 18 มม. มอก. 258 WASHER, SQUARE, FLAT 52x52x4.5 mm HOLE ø18 mm TIS 258	2	2	4	4	1010180100
17		แร็ค 2x200 มม. แบบหลังยื่น RACK, SECONDARY, MEDIUM PRESSED STEEL, 2x200 mm, EXTENDED RACK	1	1	2	2	1030130000
18		ลูกรอกแรงต่ำ มอก.227 แบบ ข (แบบ 53–2) INSULATOR, SPOOL TYPE, L.T., TIS 227 TYPE B (CLASS 53–2)	2	3	5	6	1030030000
19	a	สายทองแดง ขนาด 2x4 หรือ อะลูมิเนียม 2x10 ตร.มม. หุ้มฉนวน PVC 600 โวลต์ สำหรับขนาดโหลดสูงสุดไม่เกิน 12 แอมแปร์ CABLE, Cu, 2x4 mm^2 or Al, 2x10 mm^2 ,PVC INSULATOR, 600 V FOR MAXIMUM LOAD NOT MORE THAN 12 A	ม. m	ม. m	ม. m	ม. m	–
	b	สายทองแดง ขนาด 2x10 หรือ อะลูมิเนียม 2x25 ตร.มม. หุ้มฉนวน PVC 600 โวลต์ สำหรับขนาดโหลดสูงสุดไม่เกิน 36 แอมแปร์ CABLE, Cu, 2x10 mm^2 or Al, 2x25 mm^2 ,PVC INSULATOR, 600 V FOR MAXIMUM LOAD NOT MORE THAN 36 A					–
	c	สายทองแดง ขนาด 2x35 หรือ อะลูมิเนียม 2x50 ตร.มม. หุ้มฉนวน PVC 600 โวลต์ สำหรับขนาดโหลดสูงสุดไม่เกิน 80 แอมแปร์ CABLE, Cu, 2x35 mm^2 or Al, 2x50 mm^2, PVC INSULATOR, 600 V FOR MAXIMUM LOAD NOT MORE THAN 80 A					–
20		เข็มขัดรัดสาย (ทำด้วยลวดอะลูมิเนียมแบบ 1x10 มม.) ช่วงระยะ 50 ซม. CABLE STRAP (MADE OF ARMOUR TAPE 1x10 mm) AT 50 cm INTERVALS	ม. 2.5 m	ม. 2.5 m	ม. 5 m	ม. 5 m	1020200000
21		ตะปูหัวกลมแบน ยาว 15–20 มม., 1.00 มม. มอก.113 NAIL, ROUND MILD STEEL WIRE, 15–20 mm LONG, 1.00 mm TIS 113	24	24	40	40	

กองวิศวกรรมระบบไฟฟ้า ฝ่ายวิศวกรรม	การไฟฟ้าส่วนภูมิภาค	ใช้แทนแบบ ..... ถูกแทนโดยแบบ .....
ผู้เขียน Supphakit Boonreung ผู้สำรวจ ..... วิศวกร Supphakit Boonreung หัวหน้าแผนก อนุวัตร ผู้อำนวยการกอง ..... ผู้อำนวยการฝ่าย	ผู้ว่าการ ..... 15 พ.ย. 2564 (แทน)	เขียนเสร็จวันที่ 15 ต.ค. 2564 แก้แบบวันที่ ..... มิติเป็น ..... มาตราส่วน .....
รองผู้ว่าการสายงานวิศวกรรม –	การติดตั้งอิเล็กทรอนิกส์มิเตอร์พร้อมระบบสื่อสารไร้สาย 1 เฟส 230 โวลต์ ขนาด 5 (100) แอมแปร์ บนเสาระบบจำหน่าย 5(100) A, 1 PHASE, 230 V ELECTRONIC METER WITH WIRELESS COMMUNICATION INSTALLATION ON DISTRIBUTION CONCRETE POLE	แบบเลขที่ SA4–015/64018 แผ่นที่ 6 ของจำนวน 7 แผ่น

การประกอบเลขที่ ASSEMBLY NO.	0553

ข้อแนะนำในการติดตั้งแร็คแรงต่ำรับสายหลังมิเตอร์

ในกรณีที่ติดตั้งมิเตอร์ใหม่ จำนวน 3 หรือ 4 เครื่อง ในคราวเดียวกัน สามารถพิจารณาใช้แร็ค 4x200 มม. (วัสดุ 1030130002) แทนแร็ค 2x200 มม. วัสดุลำดับที่ 17 ได้ โดยลดจำนวนสลักเกลียว วัสดุลำดับที่ 15 ลงเหลือ 2 ชุด และลดจำนวนแหวนสี่เหลี่ยมแบน วัสดุลำดับที่ 16 ลงเหลือ 2 อัน

ข้อแนะนำในการจัดทำเข็มขัดรัดสายด้วยอะลูมิเนียมแบน 1x10 มม.

กรณีสายเข้าหรือออกจากมิเตอร์ จำนวน 1-2 เครื่อง ใช้ลวดอะลูมิเนียมแบน 1x10 มม. ยาว 15 ซม. ต่อหนึ่งจุด

กรณีสายเข้าหรือออกจากมิเตอร์ จำนวน 3-4 เครื่อง ใช้ลวดอะลูมิเนียมแบน 1x10 มม. ยาว 20 ซม. ต่อหนึ่งจุด

หมายเหตุ

* สามารถใช้ INSULATION PIERCING CONNECTOR (IPC) วัสดุเลขที่ 1020360000 ทดแทนวัสดุลำดับที่ ④ และ ⑤ ได้

	แบบอ้างอิง REFERENCE DRAWING	แบบเลขที่ DWG. No.	การประกอบเลขที่ ASSEMBLY No.
1	ขนาดสายไฟฟ้า เครื่องป้องกันกระแสเกิน และเครื่องปลดวงจร สำหรับกิโลวัตต์ชั่วโมงมิเตอร์ 1 เฟส 2 สาย SIZE OF CABLE, OVERCURRENT PROTECTION DEVICE AND DISCONNECTING MEANS FOR 1-PHASE, 2-WIRE kWh-METER CONNECTION	SA4-015/61012	0502
2	หลักเกณฑ์การกำหนดจุดติดตั้งมิเตอร์ และวิธีการเดินสายจากมิเตอร์ถึงตัวอาคาร STANDARD FOR kW-h METERS INSTALLATION AND THE METHOD TO CONNECT CONDUCTOR FROM METER TO CUSTOMER'S BUILDING	SA4-015/61011	0526
3	การเดินสายไฟฟ้า จากเสาต้นติดตั้งมิเตอร์ถึงตัวอาคารของผู้ใช้ไฟ CABLE CONNECTION FROM METER ON THE POLE TO CUSTOMER'S BUILDING	SA4-015/61010	0542
4	การเข้าปลายสายแรงต่ำด้วยลวดอะลูมิเนียมกลม L.T. DEAD-ENDING WITH ALUMINIUM TIE WIRE	SA1-015/21006	9529
5	คอนเนคเตอร์ชนิดบีบ แบบ H สำหรับใช้งานในระบบจำหน่ายแรงต่ำ COMPRESSION CONNECTOR, H-TYPE USE IN L.T. DISTRIBUTION SYSTEM	SA1-015/26021	9530
6	การติดตั้งอุปกรณ์ต่อแยกสายแรงต่ำแบบหุ้มฉนวน ในระบบจำหน่ายแรงต่ำ INSULATION PIERCING CONNECTOR (IPC) INSTALLATION FOR LOW VOLTAGE DISTRIBUTION SYSTEM	SA4-015/62004	9531
7	การติดตั้งมิเตอร์แรงต่ำ 1 เฟส 230 โวลต์ บนแป้นรองรับมิเตอร์ 1-PHASE 230 V kWh-METER INSTALLATION ON METER PLATE	SA4-015/61013	0532

กองวิศวกรรมระบบไฟฟ้า ฝ่ายวิศวกรรม	การไฟฟ้าส่วนภูมิภาค	ใช้แทนแบบ ..... ถูกแทนโดยแบบ .....
ผู้เขียน Supphakit Boonreung ผู้สำรวจ ..... วิศวกร Supphakit Boonreung หัวหน้าแผนก อนุวัตร ผู้อำนวยการกอง ..... ผู้อำนวยการฝ่าย	ผู้ว่าการ..... 15 พ.ย. 2564 (แทน)	เขียนเสร็จวันที่ 15 ต.ค. 2564 แก้แบบวันที่ ..... มิติเป็น ..... มาตราส่วน .....
	การติดตั้งอิเล็กทรอนิกส์มิเตอร์พร้อมระบบสื่อสารไร้สาย 1 เฟส 230 โวลต์ ขนาด 5 (100) แอมแปร์ บนเสาระบบจำหน่าย	
รองผู้ว่าการสายงานวิศวกรรม	5(100) A, 1 PHASE, 230 V ELECTRONIC METER WITH WIRELESS COMMUNICATION INSTALLATION ON DISTRIBUTION CONCRETE POLE	แบบเลขที่ SA4-015/64018 แผ่นที่ 7 ของจำนวน 7 แผ่น