
การประกอบเลขที่ ASSEMBLY NO. 3207

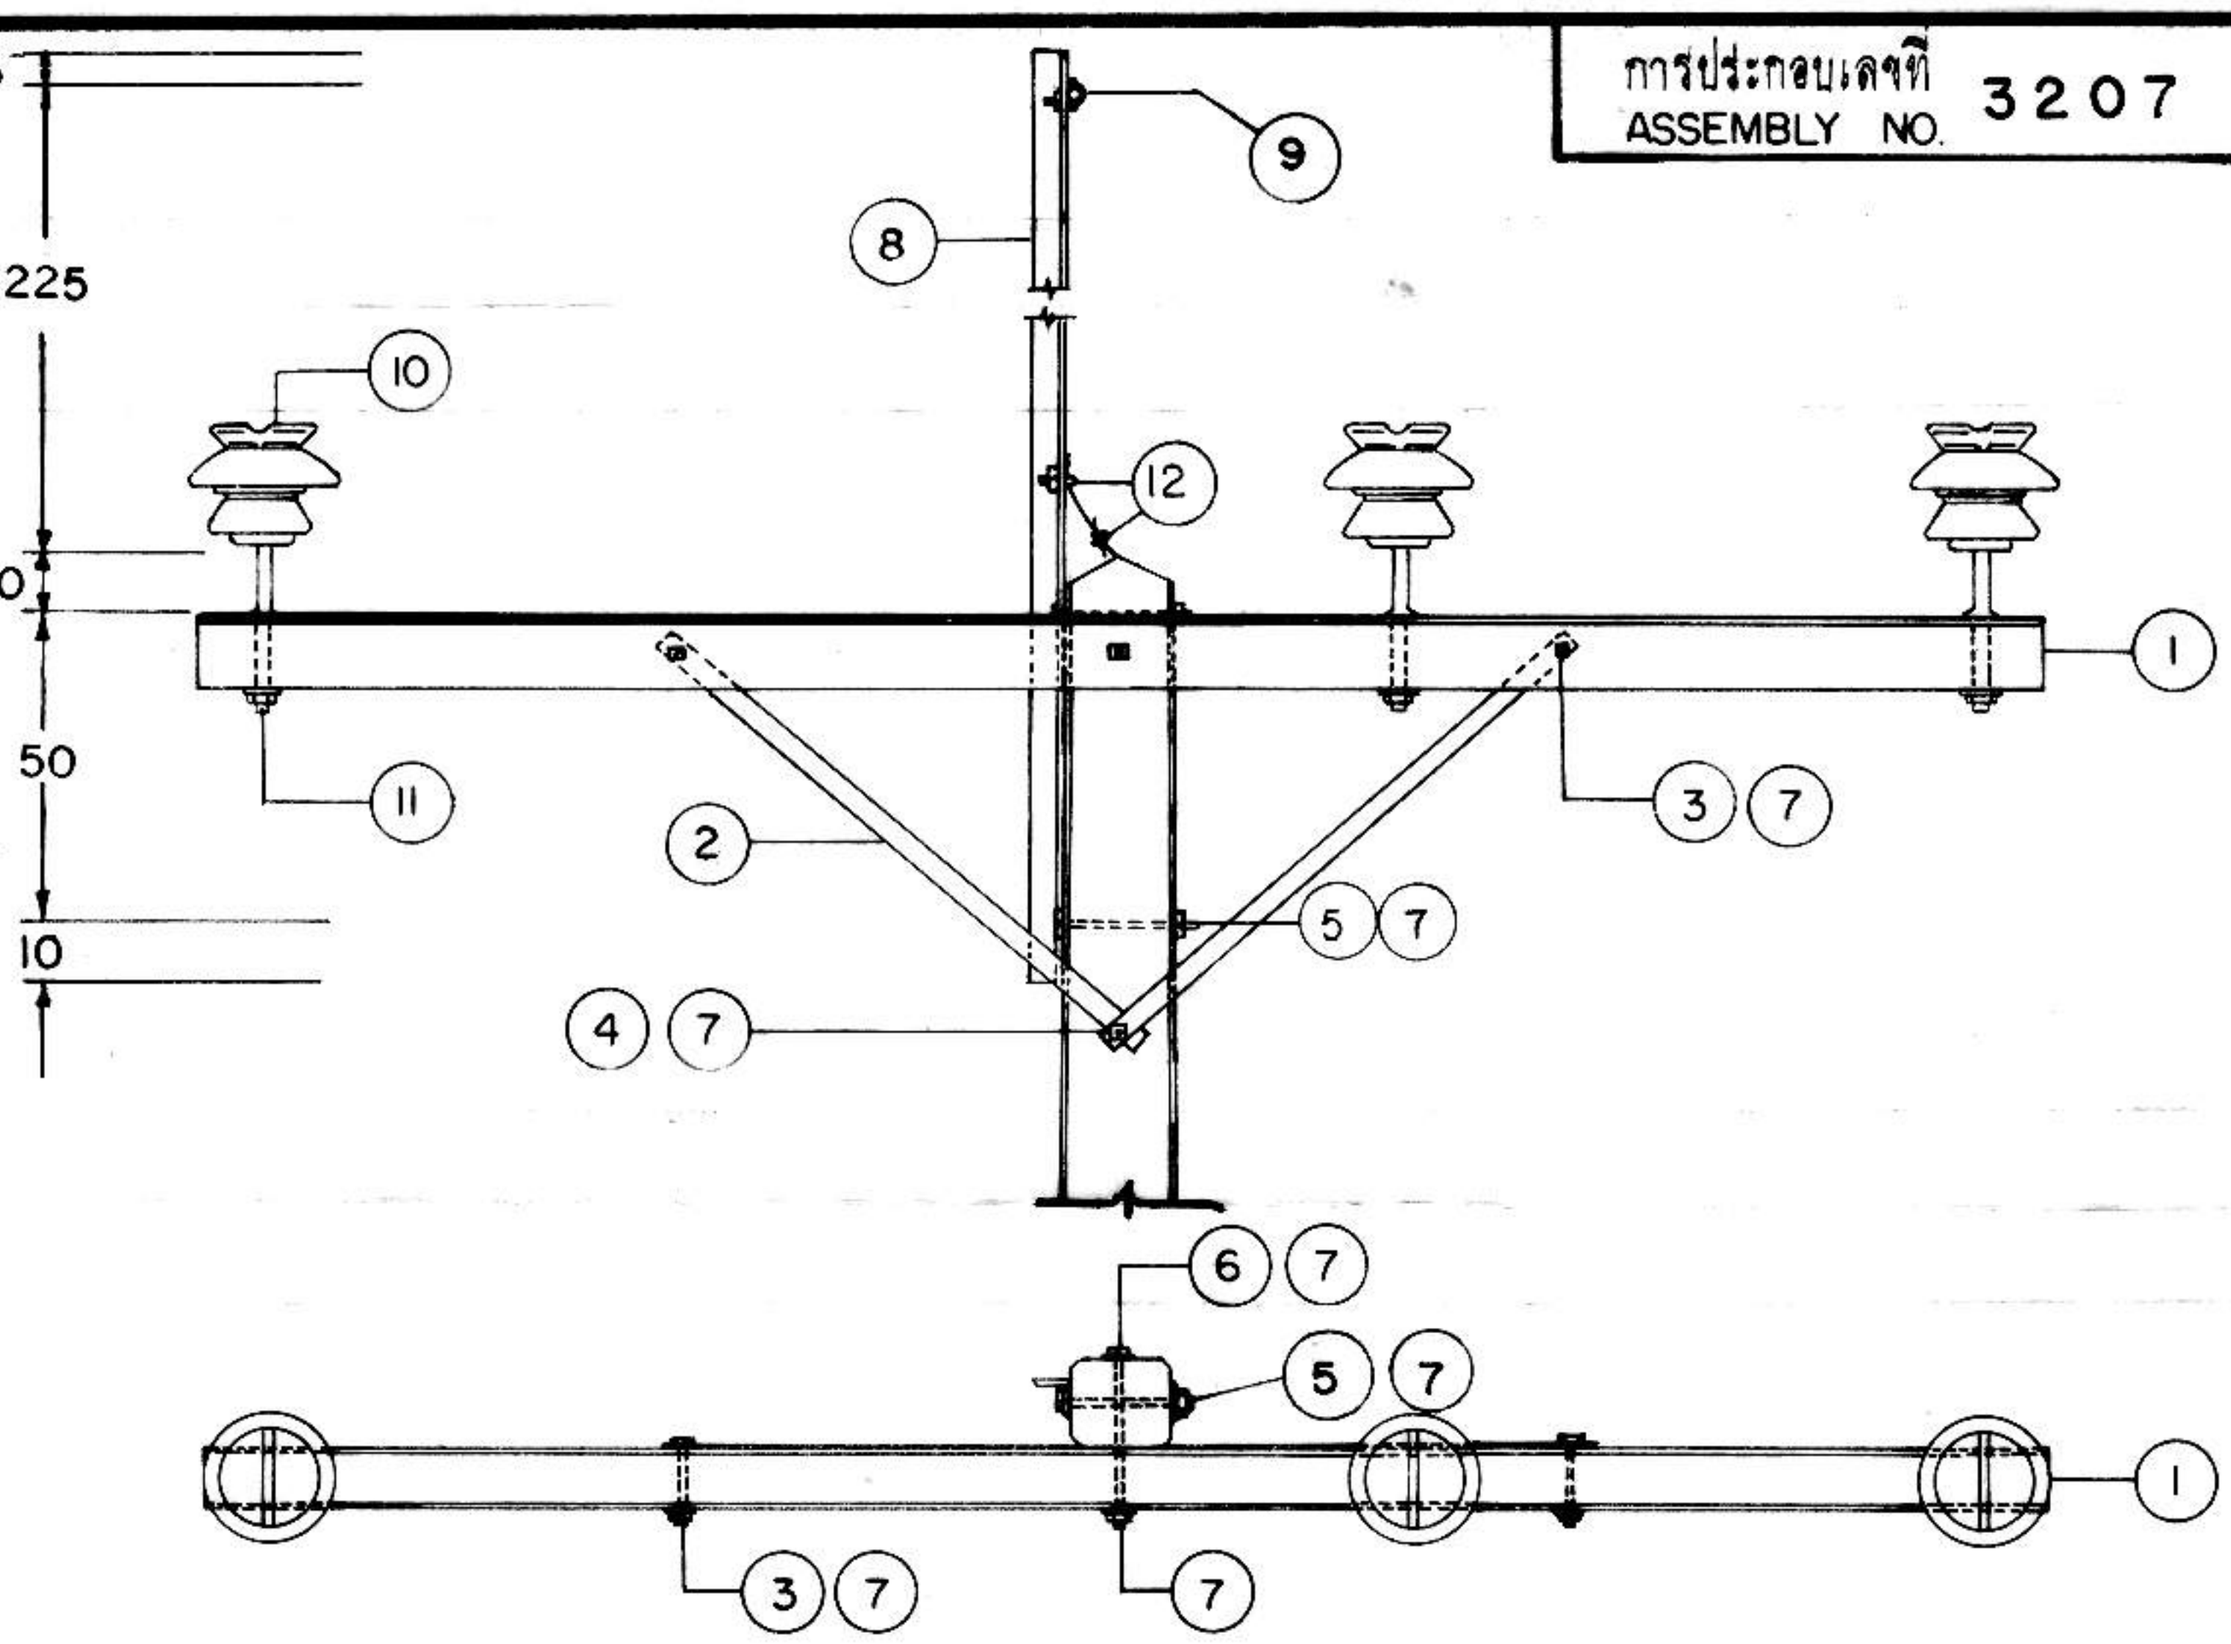

BILL OF MATERIAL			
ITEM	DESCRIPTION	REQ'D	MAT. NO.
1	ไม้คอนสายขนาด 100 X 120 X 3,000 มม. CROSSARM (H.T.) WOOD, 100 X 120 X 3,000 mm	1	00100003 (0101)
2	เหล็กประกับไม้คอน 40 X 6 X 1,000 มม. BRACE, FLAT, FOR CROSSARM , 40 X 6 X 1,000 mm	2	01200002 (0121)
3	สลักเกลียว M 16 X 130 มม. BOLT, MACHINE , M 16 X 130 mm	2	01110200 (0220)
4	สลักเกลียว M 16 X 200 มม. BOLT, MACHINE , M 16 X 200 mm	1	01110202 (0222)
5	สลักเกลียว M 16 X 250 มม. BOLT, MACHINE , M 16 X 250 mm	2	01110203 (0223)
6	สลักเกลียว M 16 X 300 มม. BOLT, MACHINE , M 16 X 300 mm	1	01110204 (0224)
7	แหวนสี่เหลี่ยมแบน 52 X 52 X 4.5 มม. ขนาดรู Ø 18 มม. มอก. 258 WASHER, SQUARE FLAT, 52X52X4.5 mm HOLE Ø 18 mm	7	01180100 (0355)
8	เหล็กฉากรับสายล่อฟ้า OVERHEAD GROUND WIRE BAYONET	1	01010006 (0128)
9	กร่างดิไวร์แคล้มน์แบบ J 1152 GROUND WIRE CLAMP J 1152	1	01230205 (0296)
10	ลูกถ้วยก้านตรง 33 kV มอก. 279 แบบ ค (แบบ 56-3) INSULATOR, PIN TYPE, 33 kV TIS 279 TYPE C (CLASS 56-3)	3	03000002 (0409)
11	ก้านลูกถ้วยแรงสูง 33 kV PIN, INSULATOR	3	03100001 (0422)
12	ยูแคล้มป์สลัก 1 ตัว M 8 (ไวร์โรป คลิ๊ป) CLAMP, SINGLE U-BOLT M 8 (WIRE ROPE CLIP)	2	01230000 (0165)

กองวิศวกรรมและวางแผน	การไฟฟ้าส่วนภูมิภาค	ใช้แทนแบบ ถูกแทนโดยแบบ
ผู้เขียน ไพโรจน์ วงษ์ สถาปนิก วิศวกร หัวหน้าแผนก ผู้อำนวยการกอง	ผู้จ่าการ	เขียนเสร็จวันที่ 13 ตค. 12 แก้แบบวันที่ มิติเป็น ซม. มาตราส่วน 1:25
ส่วนผู้จ่าการฝ่ายเทคนิค	การประกอบไม้คอนเดี่ยวกับเสาคอนกรีต ระบบ 33 kV., 3 เฟส, มุม 0°-5°	แบบเลขที่ I50-015/120292 แผ่นที่ 1 จากจำนวน 1 แผ่น
	33 kV SINGLE CROSSARM ASSEMBLY ON CONCRETE POLE, 3-PHASE, 0°-5°	