
การประกอบเลขที่ ASSEMBLY NO. 3409

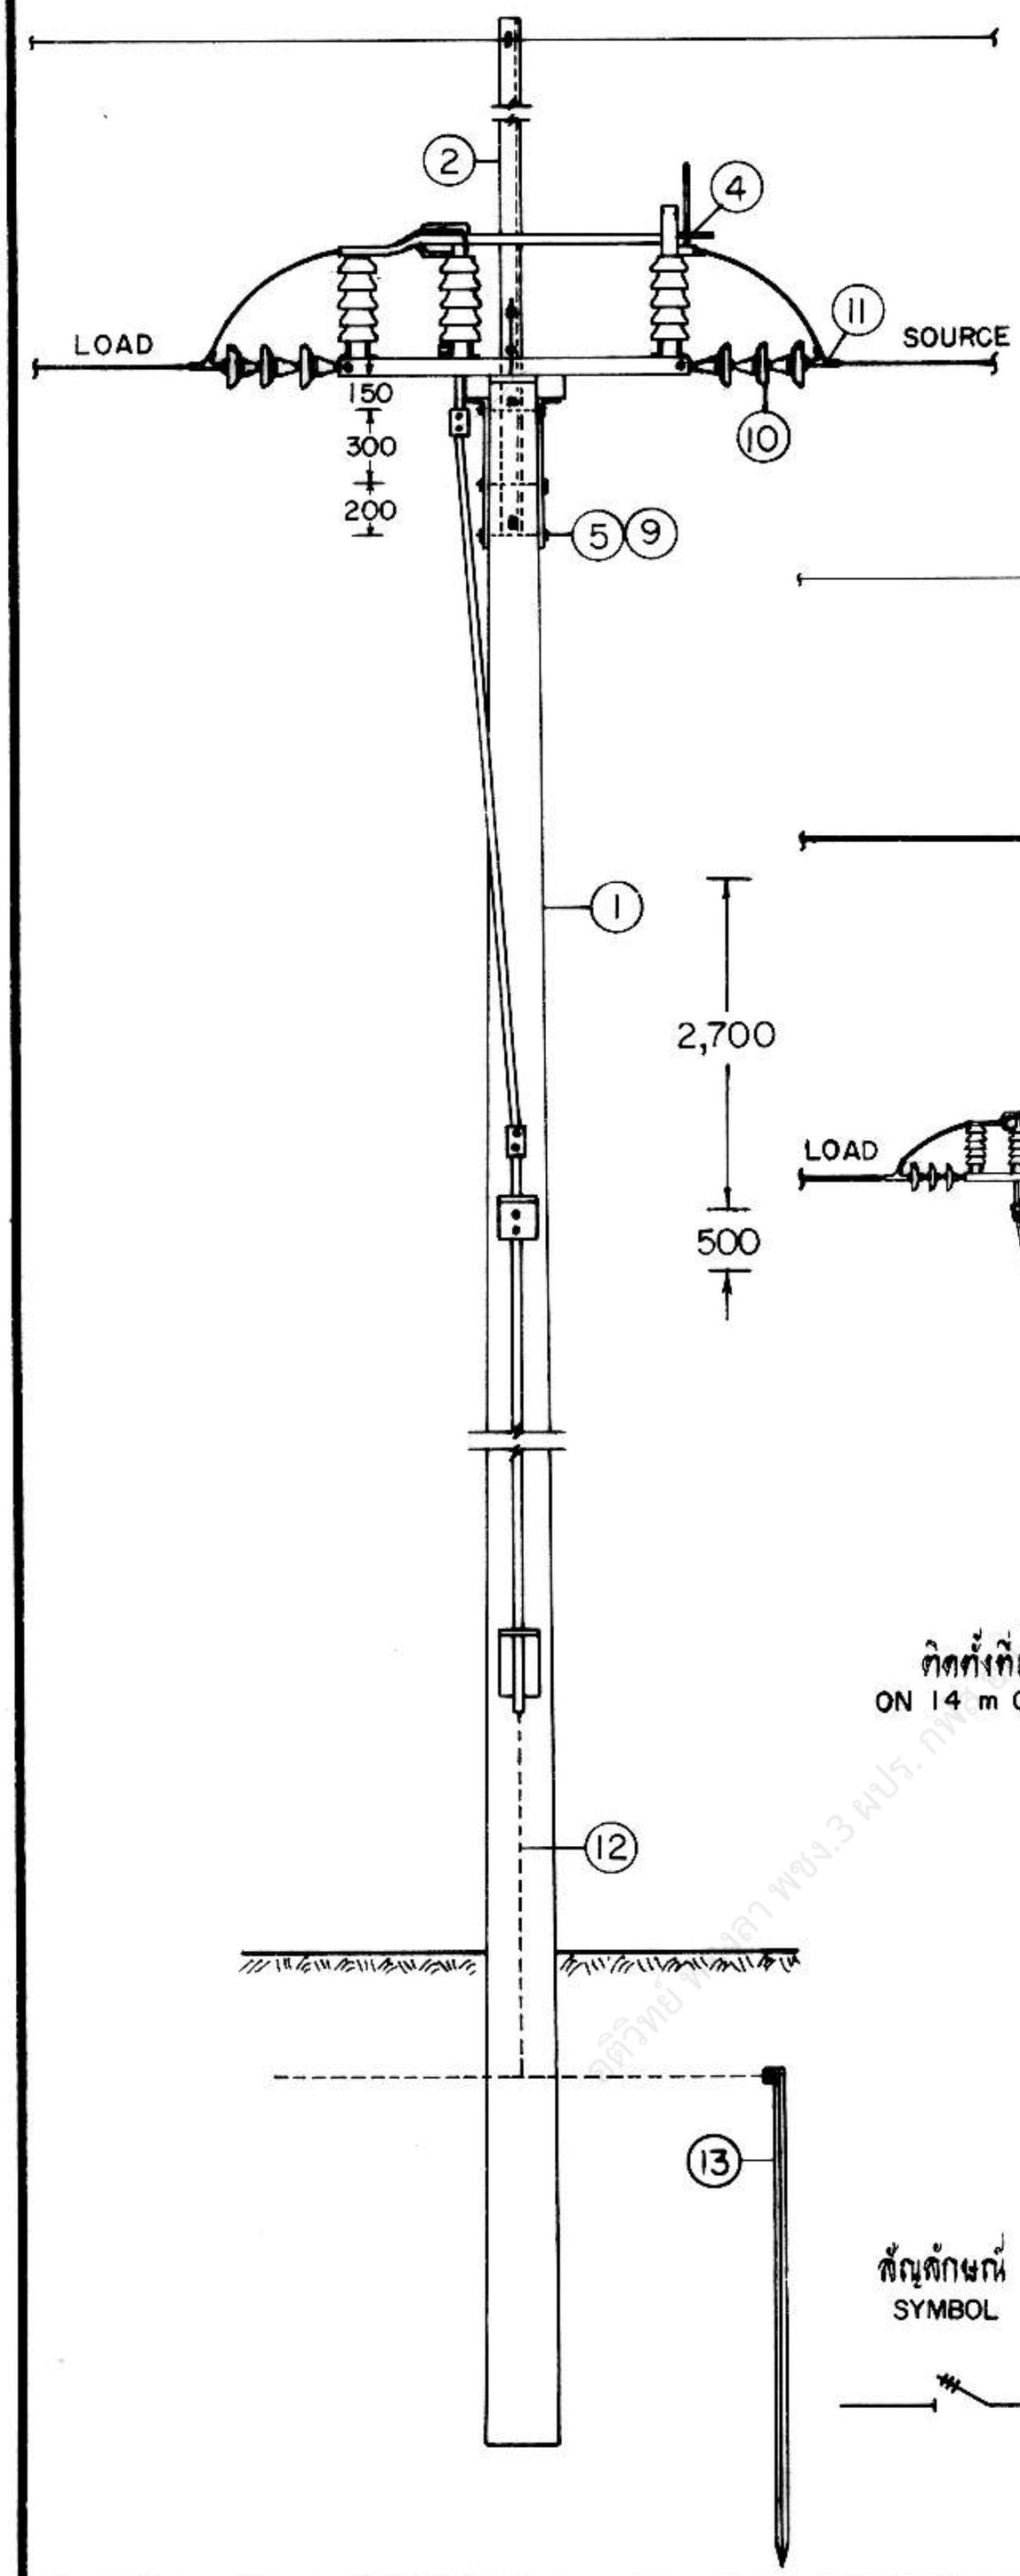

ติดตั้งที่เสาคอนกรีต 14 ม.
ON 14 m CONCRETE POLE

สัญลักษณ์
SYMBOL

แอร์เบรคสวิทช์
AIR BREAK SWITCH

กองวิศวกรรมไฟฟ้าและเครื่องกล ฝ่ายวิศวกรรม	การไฟฟ้าส่วนภูมิภาค	ใช้แทนแบบ ถูกแทนโดยแบบ เขียนเสร็จวันที่ 4 พ.ค. 21 แก้แบบวันที่ มิติเป็น มม. มาตราส่วน 1 : 50 , 1 : 100
ผู้เขียน ผู้สำรวจ วิศวกร หัวหน้าแผนก หัวหน้ากอง ผู้อำนวยการฝ่าย	ผู้ว่าการ 25 พ.ค. 21	
รองผู้ว่าการฝ่ายเทคนิค	การติดตั้งแอร์เบรคสวิทช์ 3 ขา 33 kV 33 kV TRIPLE POLE AIR BREAK SWITCH INSTALLATION	แบบเลขที่ SA1-015/21031 แผ่นที่ 1 ของจำนวน 2 แผ่น

การประกอบเลขที่ ASSEMBLY NO. 3409

บัญชีวัสดุ
BILL OF MATERIAL

ลำดับที่ ITEM	รายละเอียด DESCRIPTION	จำนวน REQ'D	วัสดุเลขที่ MAT. NO.
1	เสาคอนกรีต ขนาด 12 ม. CONCRETE POLE 12 m LONG	1	00010004
2	เหล็กฉากรับสายล่อฟ้า 60 X 60 X 6 มม. ยาว 3,000 มม. OVERHEAD GROUND WIRE BAYONET 60 X 60 X 6 mm 3,000 mm LONG	1	01010006
3	กราวด์วายรัแคล้มป์ แผน J 1152 GROUND WIRE CLAMP, J 1152	1	01230205
4	แอร์เบรคสวิทช์ 3 ขา 33 kV, 600 แอมป์ พร้อมฐานเหล็กสำหรับติดตั้งบนฝลายเสา และกลไกการบังคับด้วยมือ SWITCH, AIR BREAK, TRIPLE POLE 33 kV, 600 A INCLUDING STEEL BASE FOR POLE TOP INSTALLATION COMPLETE WITH MANUAL OPERATING MECHANISM	1 ชุด set	04079900 04069902
5	สลักเกลียว M 16 X 200 มม. BOLT, MACHINE, M 16 X 200 mm	3	01110202
6	สลักเกลียว M 16 X 250 มม. BOLT, MACHINE, M 16 X 250 mm	5	01110203
7	สลักเกลียว M 16 X 300 มม. BOLT, MACHINE, M 16 X 300 mm	1	01110204
8	แหวนสี่เหลี่ยมแผน 52X52X4.5 มม. รู Ø 18 มม. มอก. 258 WASHER, SQUARE, FLAT 52X52X4.5 mm HOLE Ø 18 mm TIS 258	5	01180100
9	แหวนสปริง M 16 มอก. 259 WASHER, LOCK M 16 TIS 259	6	01180301
10	ลูกถ้วยแขวน มอก. 354 แบบ ง (แบบ 52-4) INSULATOR, SUSPENSION TYPE, TIS 354 TYPE D (CLASS 52-4)	18	03020002
11	สเตรนแคล้มป์ สำหรับสายอะลูมิเนียม อะลูมิเนียมแกนเหล็ก CLAMP, STRIAN, FOR AI, ACSR	6	03110000 03110101
12	ลวดเหล็กตีเกลียว 50/7 ต.มม. มอก. 404 WIRE, STEEL STRANDED 50/7 mm^2 TIS 404	11 ม. m	01100004
13	หลักดิน 60 X 60 X 5 มม. ยาว 2 ม. ROD, GROUND 60 X 60 X 5 mm, 2 m LONG	1	01220002

หมายเหตุ
1. การประกอบแอร์เบรคสวิทช์ดูรายละเอียดจากคู่มือที่แนบมาพร้อมกับสวิทช์ แต่ละผลิตภัณฑ์
2. สามารถใช้ปิดหรือเปิดวงจรขณะที่มีโหลด ทั้งนี้กระแสโหลดขณะปิดหรือเปิดวงจร ต้องมีค่าไม่เกิน 10 แอมแปร์
3. ตำแหน่งการติดตั้งแอร์เบรคสวิทช์ในระบบจำหน่ายแรงสูง ดูแบบเลขที่ SAI-015/20026

NOTES
1. ASSEMBLY DETAIL SEE INSTRUCTION HANDBOOK WHICH IS PACKED TOGETHER WITH TRIPLE POLE AIR BREAK SWITCH.
2. THIS SWITCHES CAN BE OPERATED AS DISCONNECTING SWITCHES TO INTERRUPT CURRENT NOT MORE THAN 10 AMPERES.
3. TRIPLE POLE AIR BREAK SWITCH INSTALLATION IN H.T. DISTRIBUTION SYSTEM SEE DWG. NO. SAI-015/20026.

กองวิศวกรรมไฟฟ้าและเครื่องกล ฝ่ายวิศวกรรม	การไฟฟ้าส่วนภูมิภาค	ใช้แทนแบบ ถูกแทนโดยแบบ เขียนเสร็จวันที่ 4 พ.ค. 21 แก้แบบวันที่ มิติเป็น มาตราส่วน
ผู้เขียน ผู้สำรวจ วิศวกร หัวหน้าแผนก หัวหน้ากอง ผู้อำนวยการฝ่าย	ผู้ว่าการ การติดตั้งแอร์เบรคสวิทช์ 3 ขา 33 kV	
รองผู้ว่าการฝ่ายเทคนิค	33 kV TRIPLE POLE AIR BREAK SWITCH INSTALLATION	แบบเลขที่ SAI-015/21031 แผ่นที่ 2 ของจำนวน 2 แผ่น