การประกอบเลขที่
ASSEMBLY NO. 5653

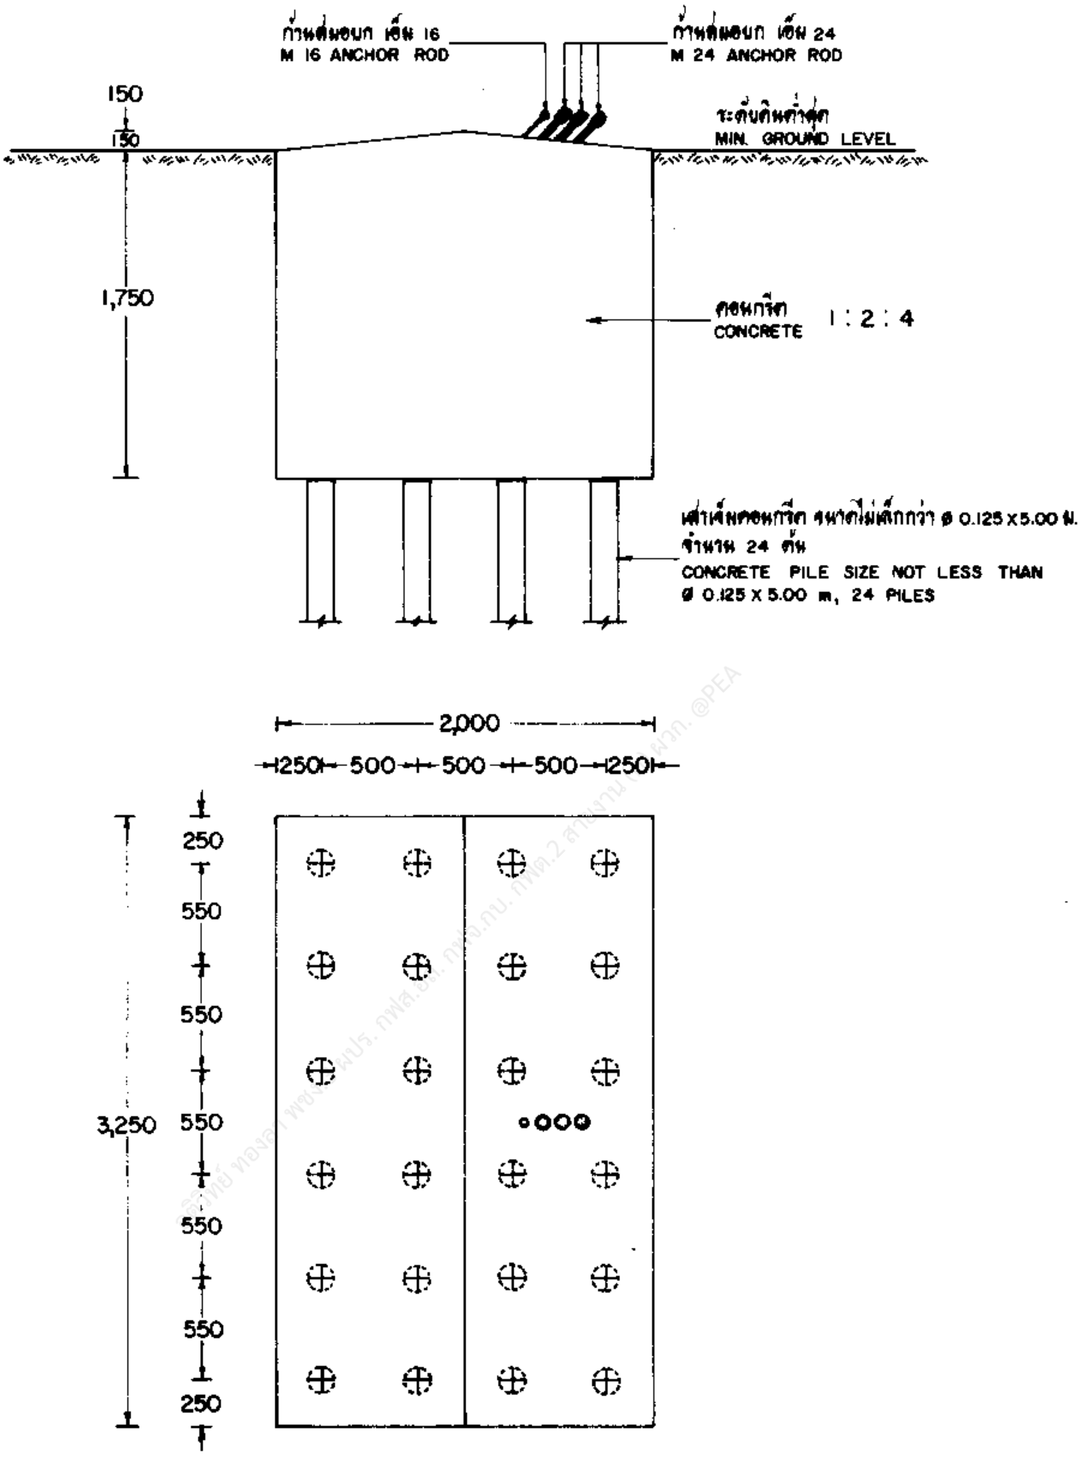

กองโยธา และสถาปัตย์
ฝ่ายแผนการ และงานโยธา

ผู้เขียน
ผู้ตรวจ
วิศวกร
หัวหน้าแผนก
หัวหน้ากอง
ผู้อำนวยการฝ่าย

รองผู้ว่าการฝ่ายเทคนิค

11 ส.ค. 252[illegible]

การไฟฟ้าส่วนภูมิภาค

ผู้ว่าการ 11 ส.ค. 25[illegible]

รายละเอียดที่ 9
สมอบกคอนกรีต (แบบที่ 2)

DETAIL 9
CONCRETE ANCHOR (TYPE 2)

ใช้แทนแบบ —
ถูกแทนโดยแบบ —
เขียนเสร็จวันที่ 9กค.24
แก้แบบวันที่ —
มิติเป็น มม.
มาตราส่วน 1 : 40
แบบเลขที่ IB-015/240028
แผ่นที่ 1 ของจำนวน 2 แผ่น

การประกอบเลขที่ 5653
ASSEMBLY NO. 5653

รายละเอียด DETAIL	จำนวนก้านสมอบก NO. OF ANCHOR ROD	
	ก้านสมอบก M 24 แบบห่วงสองห่วง ROD, ANCHOR, DOUBLE STRAND EYE, M 24	ก้านสมอบก M 16 แบบห่วงกลม ROD, ANCHOR, ROUND EYE, M 16
D - 9A	3	1
D - 9B	3	—

หมายเหตุ

1. สำหรับกรณีที่ดินสามารถรับน้ำหนักปลอดภัยได้มากกว่า 8 ตัน/ตร.ม.ขึ้นไป ไม่ต้องใช้เสาเข็มรองรับสมอบก
2. ดูรายละเอียดเพิ่มเติมจากแบบเลขที่ IBI-017/23063 (การประกอบเลขที่ 5952)

NOTES

1. IN CASE OF ALLOWABLE SOIL BEARING CAPACITY IS MORE THAN 8 TON/m^2, OMIT THE CONCRETE PILES FOR SUPPORTING THE CONCRETE ANCHOR.
2. SEE ADDITIONAL DETAILS IN DWG. NO. IBI-017/23063 (ASSEMBLY NO. 5952)

อดิวิทย์ ทองลา พชง.3 ผปร. กฟส.อล. กฟจ.กบ. กฟต.2 สายงาน

กองโยธา และสถาปัตย์
ฝ่ายแผนการ และงานโยธา

ผู้เขียน
ผู้ตรวจ
วิศวกร
หัวหน้าแผนก
หัวหน้ากอง
ผู้อำนวยการฝ่าย

รองผู้ว่าการฝ่ายเทคนิค

11 ส.ค. 2524

การไฟฟ้าส่วนภูมิภาค

ผู้ว่าการ 13 ส.ค. 2524

รายละเอียดที่ 9
สมอบกคอนกรีต (แบบที่ 2)

DETAIL 9
CONCRETE ANCHOR (TYPE 2)

ใช้แทนแบบ —
ถูกแทนโดยแบบ —
เขียนเสร็จวันที่ 9 ก.ค. 24
แก้แบบวันที่ —
มิติเป็น
มาตราส่วน

แบบเลขที่ IBI-015/240028
แผ่นที่ 2 ของจำนวน 2 แผ่น