การประกอบเลขที่
ASSEMBLY NO. 3222

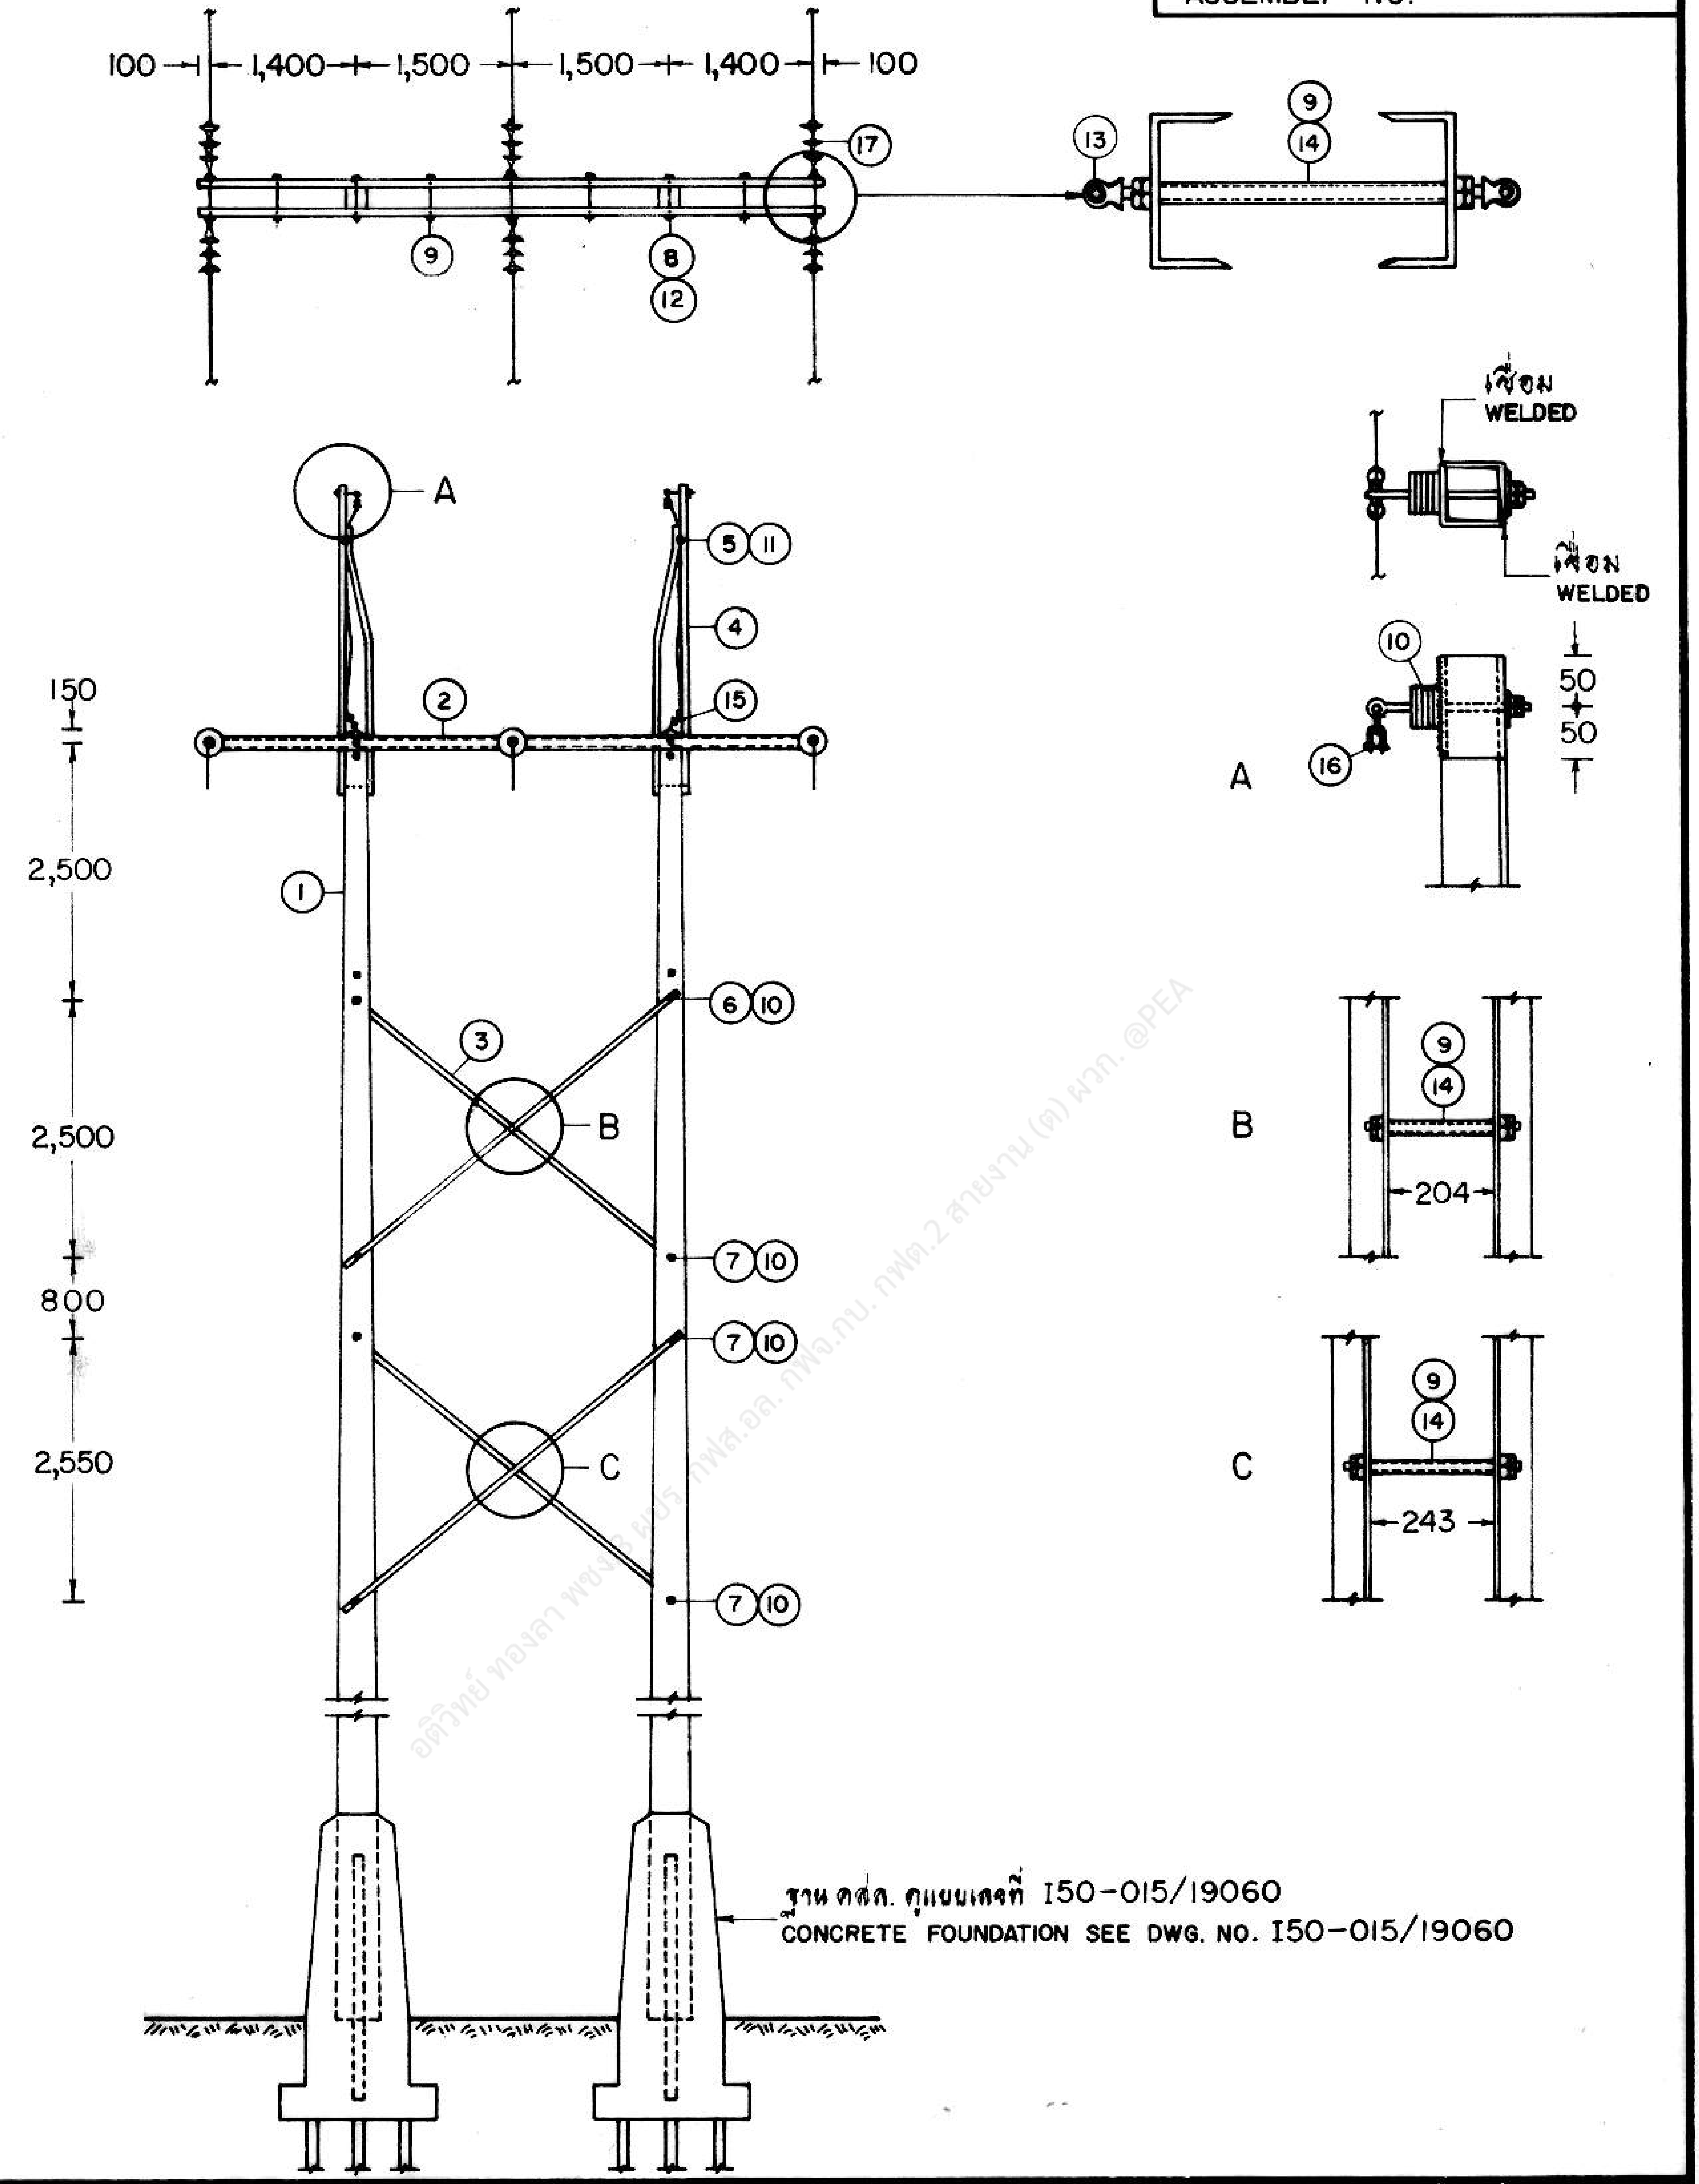

อดิวิทย์ ทองลา พชง.3 ผบร. กพส.อล. กพจ.กบ. กฟต.2 สายงาน (ต) ผวก. @PEA

กองวิศวกรรมไฟฟ้าและเครื่องกล
ฝ่ายวิศวกรรม

ผู้เขียน
ผู้ตรวจ
วิศวกร
หัวหน้าแผนก
หัวหน้ากอง
ผู้อำนวยการฝ่าย

รองผู้ว่าการฝ่ายเทคนิค

15 เมย

การไฟฟ้าส่วนภูมิภาค

ผู้ว่าการ 20 เม.ย. 22

มาตรฐานการก่อสร้างระบบ 33 kV
ช่วง 200 – 350 ม.

33 kV STANDARD CONSTRUCTION
SPAN 200 – 350 m

ใช้แทนแบบ I50-015/150009
ถูกแทนโดยแบบ
เขียนเสร็จวันที่ 3 เม.ย. 22
แก้แบบวันที่
มิติเป็น มม.
มาตราส่วน 1 : 100

แบบเลขที่ SAI-015/22022
แผ่นที่ 1 ของจำนวน 4 แผ่น

การประกอบเลขที่
ASSEMBLY NO. 3222

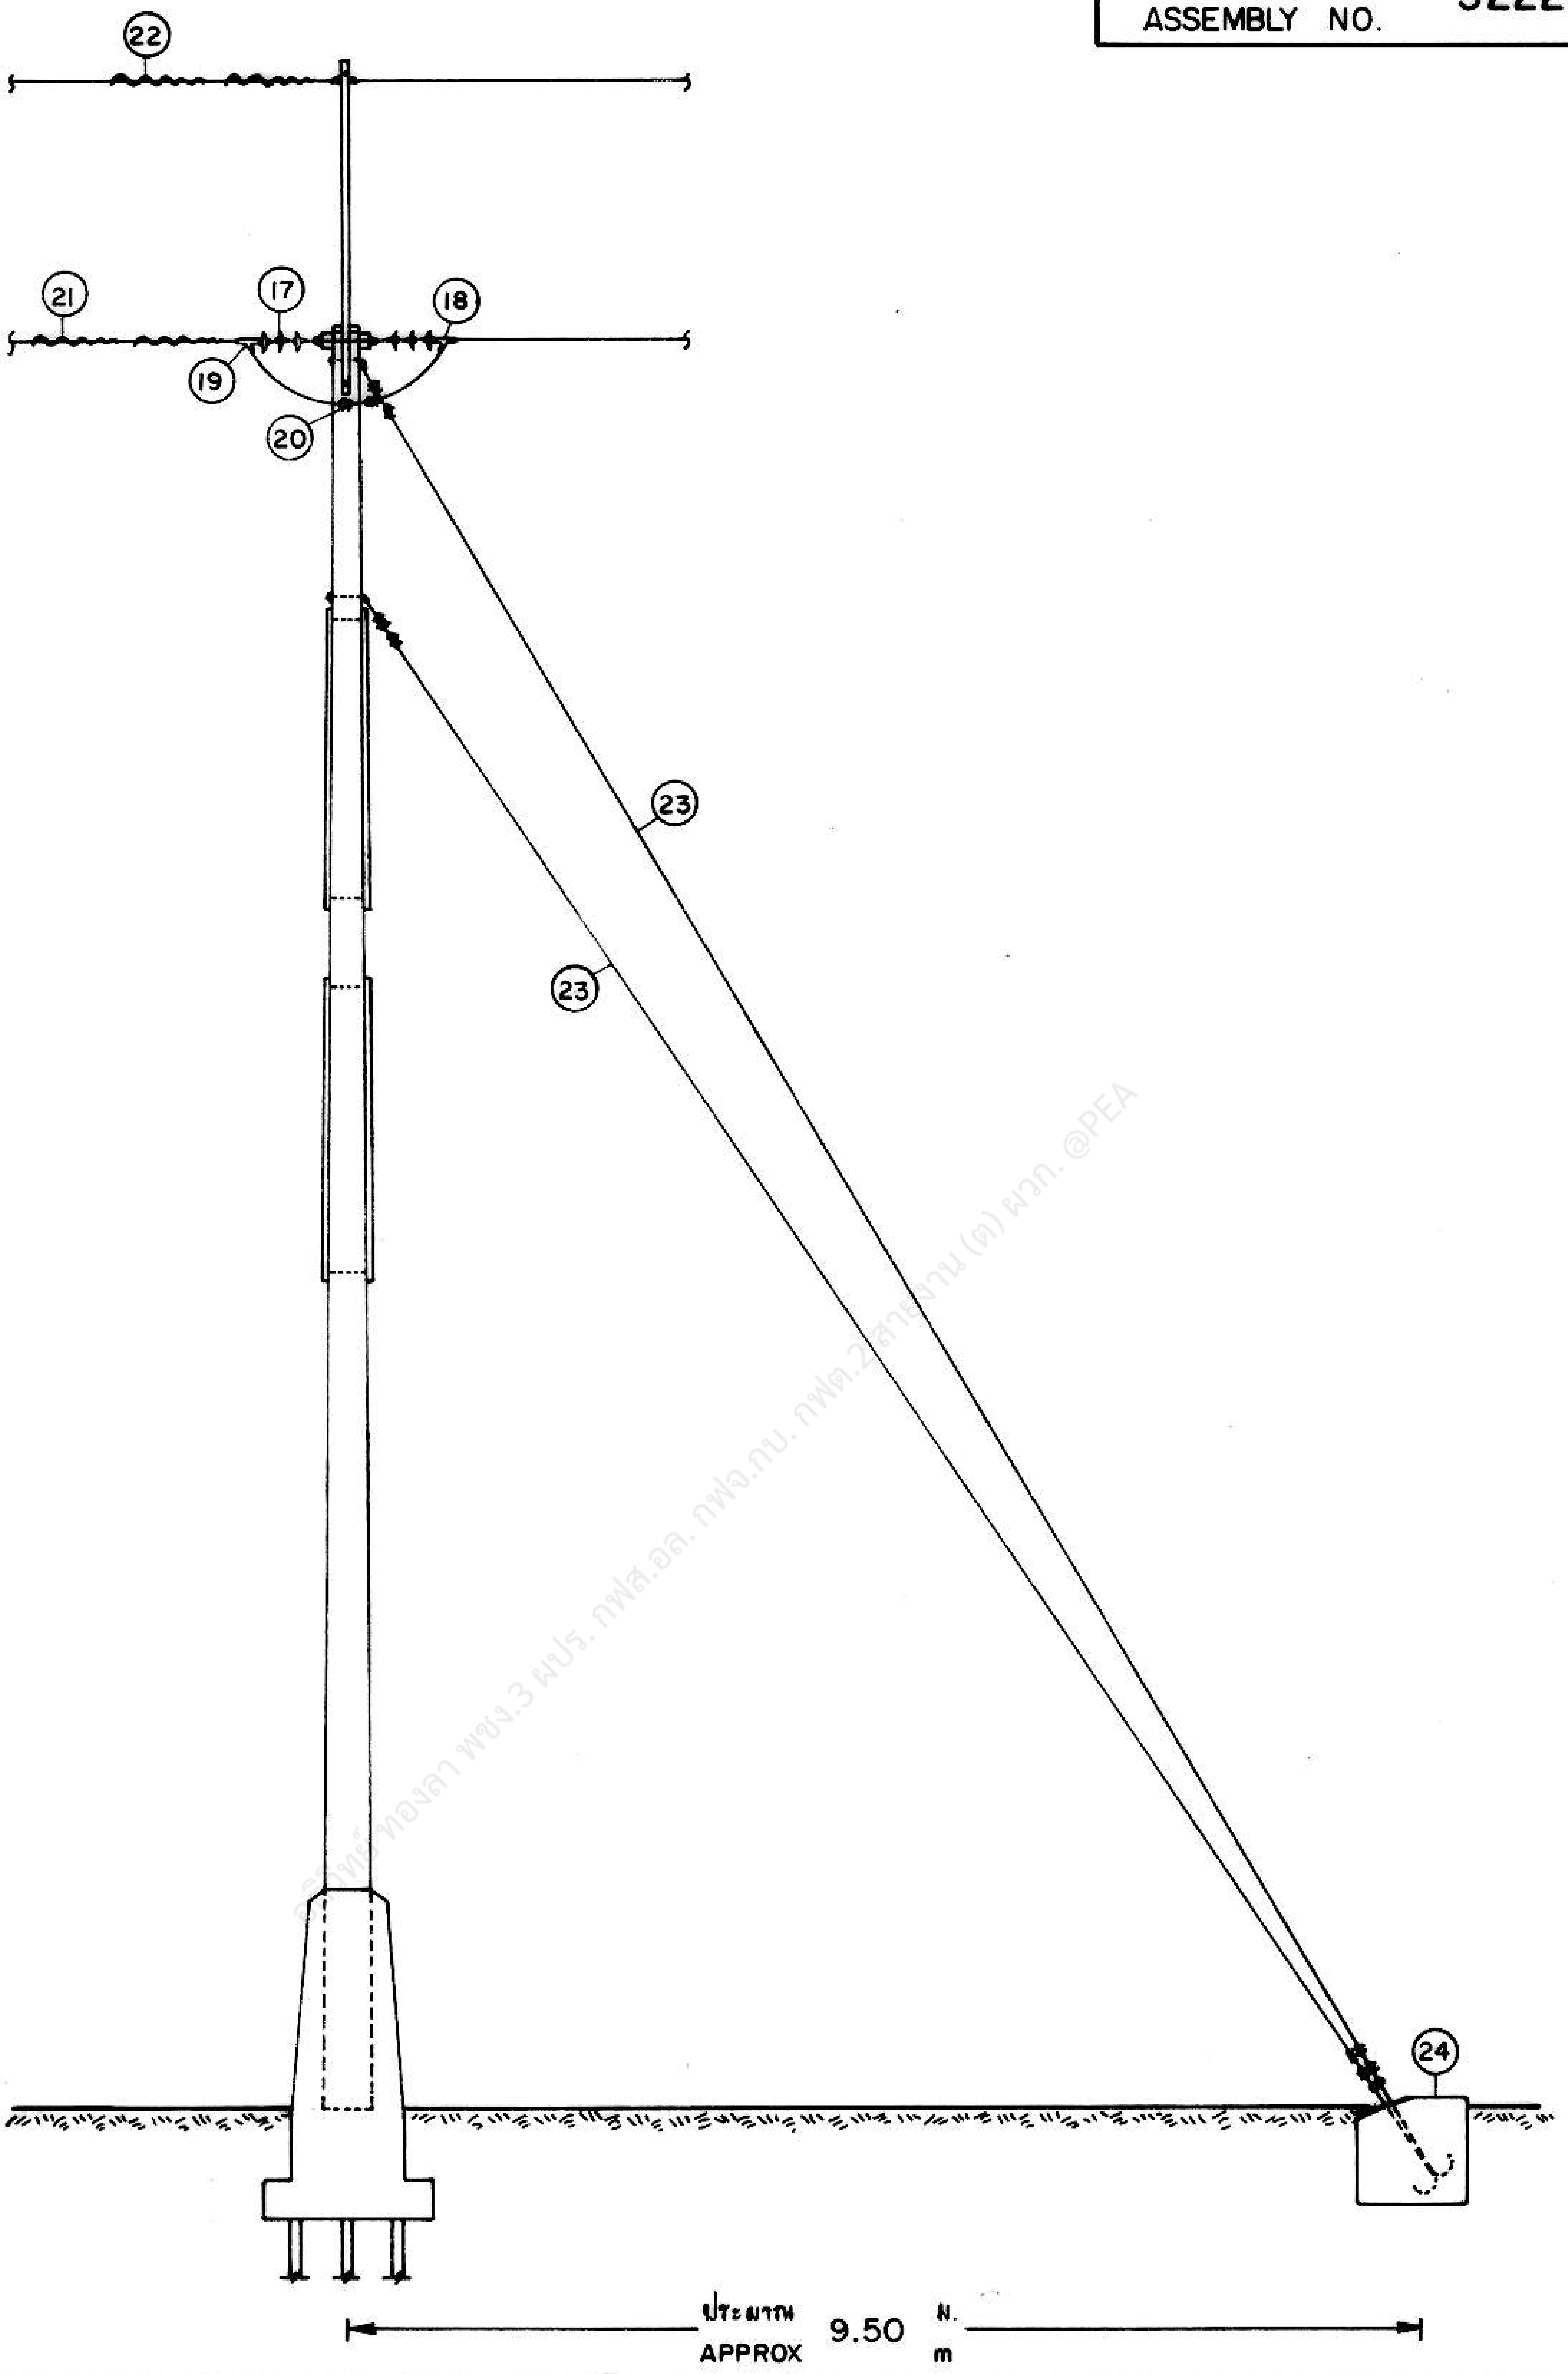

กองวิศวกรรมไฟฟ้าและเครื่องกล
ฝ่ายวิศวกรรม

ผู้เขียน
ผู้สำรวจ
วิศวกร
หัวหน้าแผนก
หัวหน้ากอง
ผู้อำนวยการฝ่าย

รองผู้ว่าการฝ่ายเทคนิค

การไฟฟ้าส่วนภูมิภาค

ผู้ว่าการ ๒๐ เม.ย. ๒๒

มาตรฐานการก่อสร้างระบบ 33 kV
ช่วง 200 - 350 ม.

33 kV STANDARD CONSTRUCTION
SPAN 200 - 350 m

ใช้แทนแบบ I50-015/150009
ถูกแทนโดยแบบ
เขียนเสร็จวันที่ 3 เม.ย. 22
แก้แบบวันที่
ผิดเป็น
มาตราส่วน 1 : 100

แบบเลขที่ SAI-015/22022
แผ่นที่ 2 ของจำนวน 4 แผ่น

15 ตค

การประกอบเลขที่
ASSEMBLY NO. 3222

บัญชีวัสดุ
BILL OF MATERIAL

ลำดับที่ ITEM	รายละเอียด DESCRIPTION	จำนวน REQ'D	วัสดุเลขที่ MAT. NO.
1	เสาคอนกรีต 16 ม. POLE, CONCRETE 16 m	2	00010008 (0038)
2	เหล็กรูปรางน้ำขนาด 150 X 75 X 6.5 มม. ยาว 6,000 มม. (น้ำหนัก 18.6 กก./ม.) STEEL CHANNEL 150 X 75 X 6.5 mm, 6,000 mm LONG (WEIGTH 18.6 kg/m)	2	01000303 (0117)
3	เหล็กฉากขนาด 75 X 75 X 6 มม. ยาว 4,100 มม. (น้ำหนัก 6.87 กก./ม.) STEEL ANGLE 75 X 75 X 6 mm, 4,100 mm LONG (WEIGTH 6.87 kg/m)	4	01010101 (0122)
4	เหล็กฉากรับสายล่อฟ้า ทางโค้ง 60 X 60 X 6 มม. OVERHEAD GROUND WIRE CORNER BAYONET 60 X 60 X 6 mm	2	01010007 (0129)
5	สลักเกลียว M 12 X 35 มม. BOLT, MACHINE, M 12 X 35 mm	4	01110100 (0212)
6	สลักเกลียว M 16 X 250 มม. BOLT, MACHINE, M 16 X 250 mm	6	01110203 (0223)
7	สลักเกลียว M 16 X 300 มม. BOLT, MACHINE, M 16 X 300 mm	6	01110204 (0224)
8	สลักเกลียว M 16 X 350 มม. BOLT, MACHINE, M 16 X 350 mm	2	01110205 (0225)
9	สลักเกลียว ตลอด M 16 X 400 มม. BOLT, DOUBLE ARMING, M 16 X 400 mm	9	01120000 (0413)
10	แหวนสี่เหลี่ยมแบน 52 X 52 X 4.5 มม. รู Ø 18 มม. มอก. 258 WASHER, SQUARE, FLAT 52 X 52 X 4.5 mm HOLE Ø 18 mm TIS 258	20	01180100 (0355)
11	แหวนสปริง M 12 มอก. 259 WASHER, LOCK M 12 TIS 259	4	01180300 (0364)
12	แหวนสปริง M 16 มอก. 259 WASHER, LOCK M 16 TIS 259	2	01180301 (0365)
13	นัทรูปห่วง M 16 DIN 582 NUT, EYE, M 16 DIN 582	6	01180001 (0345)
14	ท่อเหล็ก ขนาด Ø 20 มม. ความยาวตามต้องการ PIPE STEEL Ø 20 mm LENGTH AS REQUIRED	9	01050005 01050008
15	ยูแคล้มป์ สลัก 1 ตัว M 8 (ไวร์ โร้ป คลิ๊พ) CLAMP, SINGLE U-BOLT, M 8 (WIRE ROPE CLIP)	4	01230000 (0165)
16	กราวด์วายร์แคล้มป์ สำหรับไม้คอนสาย GROUND WIRE SUPPORT AND CLAMP, FOR WOOD BAYONET	2	01230200 (0297)
17	ลูกถ้วยแขวน มอก. 354 แบบ ง (แบบ 52-4) INSULATOR, SUSPENSION TYPE, TIS 354 TYPE D (CLASS 52-4)	18	03020002 (0415)
18	สเตรนแคล้มป์สำหรับสายอะลูมิเนียม CLAMP, STRAIN, FOR Al CONDUCTOR	3	03110000 - 03110101
19	สเตรนแคล้มป์สำหรับสายอะลูมิเนียมแกนเหล็ก CLAMP, STRAIN, FOR ACSR CONDUCTOR	3	03110000 - 03110101
20	พี.จี. คอนเนคเตอร์ สำหรับสายอะลูมิเนียม อะลูมิเนียมอัลลอย และ อะลูมิเนียมแกนเหล็ก CONNECTOR, PARALLEL GROOVE, FOR Al, Al-ALLOY AND ACSR	6	02300103 02300104

กองวิศวกรรมไฟฟ้าและเครื่องกล
ฝ่ายวิศวกรรม

ผู้เขียน
ผู้สำรวจ
วิศวกร
หัวหน้าแผนก
หัวหน้ากอง
ผู้อำนวยการฝ่าย

รองผู้ว่าการฝ่ายเทคนิค

การไฟฟ้าส่วนภูมิภาค

ผู้ว่าการ 20/เม.ย. 22

มาตรฐานการก่อสร้างระบบ 33 kV
ช่วง 200 - 350 ม.

33 kV STANDARD CONSTRUCTION
SPAN 200 - 350 m

ใช้แทนแบบ I50-015/150009
ถูกแทนโดยแบบ
เขียนเสร็จวันที่ 3 เม.ย. 22
แก้แบบวันที่
มิติเป็น
มาตราส่วน

แบบเลขที่ SAI-015/22022
แผ่นที่ 3 ของจำนวน 4 แผ่น

การประกอบเลขที่
ASSEMBLY NO. **3222**

บัญชีวัสดุ
BILL OF MATERIAL

ลำดับที่ ITEM	รายละเอียด DESCRIPTION	จำนวน REQ'D	วัสดุเลขที่ MAT. NO.
21	สไปแรลไวเบรชั่นแดมเปอร์ SPIRAL VIBRATION DAMPER	6	02200102 02200103
22	สไปแรลไวเบรชั่นแดมเปอร์ สำหรับสายลวดเหล็กตีเกลียว 25 ต.มม. SPIRAL VIBRATION DAMPER FOR 25 mm² STEEL STRANDED WIRE	4	02200100 (0903)
23	สายยึดโยง GY-32 (ไม่รวมท่อนไม้) GUY GY-32 (LOG ANCHOR NOT INCLUDED)	4	—
24	สมอบกคอนกรีต 1.00 X 1.00 X 1.00 ม. (คอนกรีต 1:2:4) CONCRETE ANCHOR 1.00 X 1.00 X 1.00 m (CONCRETE 1:2:4)	2	—

หมายเหตุ

1. อุปกรณ์ที่เป็นเหล็ก อาบสังกะสี หรือทาด้วยสีกันสนิม
2. สายล่อฟ้าใช้ลวดเหล็กตีเกลียว 25 ต.มม.

NOTES

1. STEEL PARTS SHALL BE GALVANIZED OR COATED WITH RUST-RESISTING PAINT.
2. USE STEEL STRANDED WIRE 25 mm² AS OVERHEAD GROUND WIRE.

อติวิทย์ ทองลา พชง.3 ผปร. กฟส.อล. กฟจ.กบ. [illegible] สายงาน (ต) ผวก. @PEA

กองวิศวกรรมไฟฟ้าและเครื่องกล
ฝ่ายวิศวกรรม

ผู้เขียน
ผู้สำรวจ
วิศวกร
หัวหน้าแผนก
หัวหน้ากอง
ผู้อำนวยการฝ่าย

รองผู้ว่าการฝ่ายเทคนิค

การไฟฟ้าส่วนภูมิภาค

ผู้ว่าการ 20 เม.ย. 22

มาตรฐานการก่อสร้างระบบ 33 kV
ช่วง 200-350 ม.

33 kV STANDARD CONSTRUCTION
SPAN 200 - 350 m

ใช้แทนแบบ I50-015/150009
ถูกแทนโดยแบบ
เขียนเสร็จวันที่ 3 เม.ย.22
แก้แบบวันที่
ผิดเป็น
มาตราส่วน

แบบเลขที่ SAI-015/22022
แผ่นที่ 4 ของจำนวน 4 แผ่น