การประกอบเลขที่ ASSEMBLY NO. **3602**

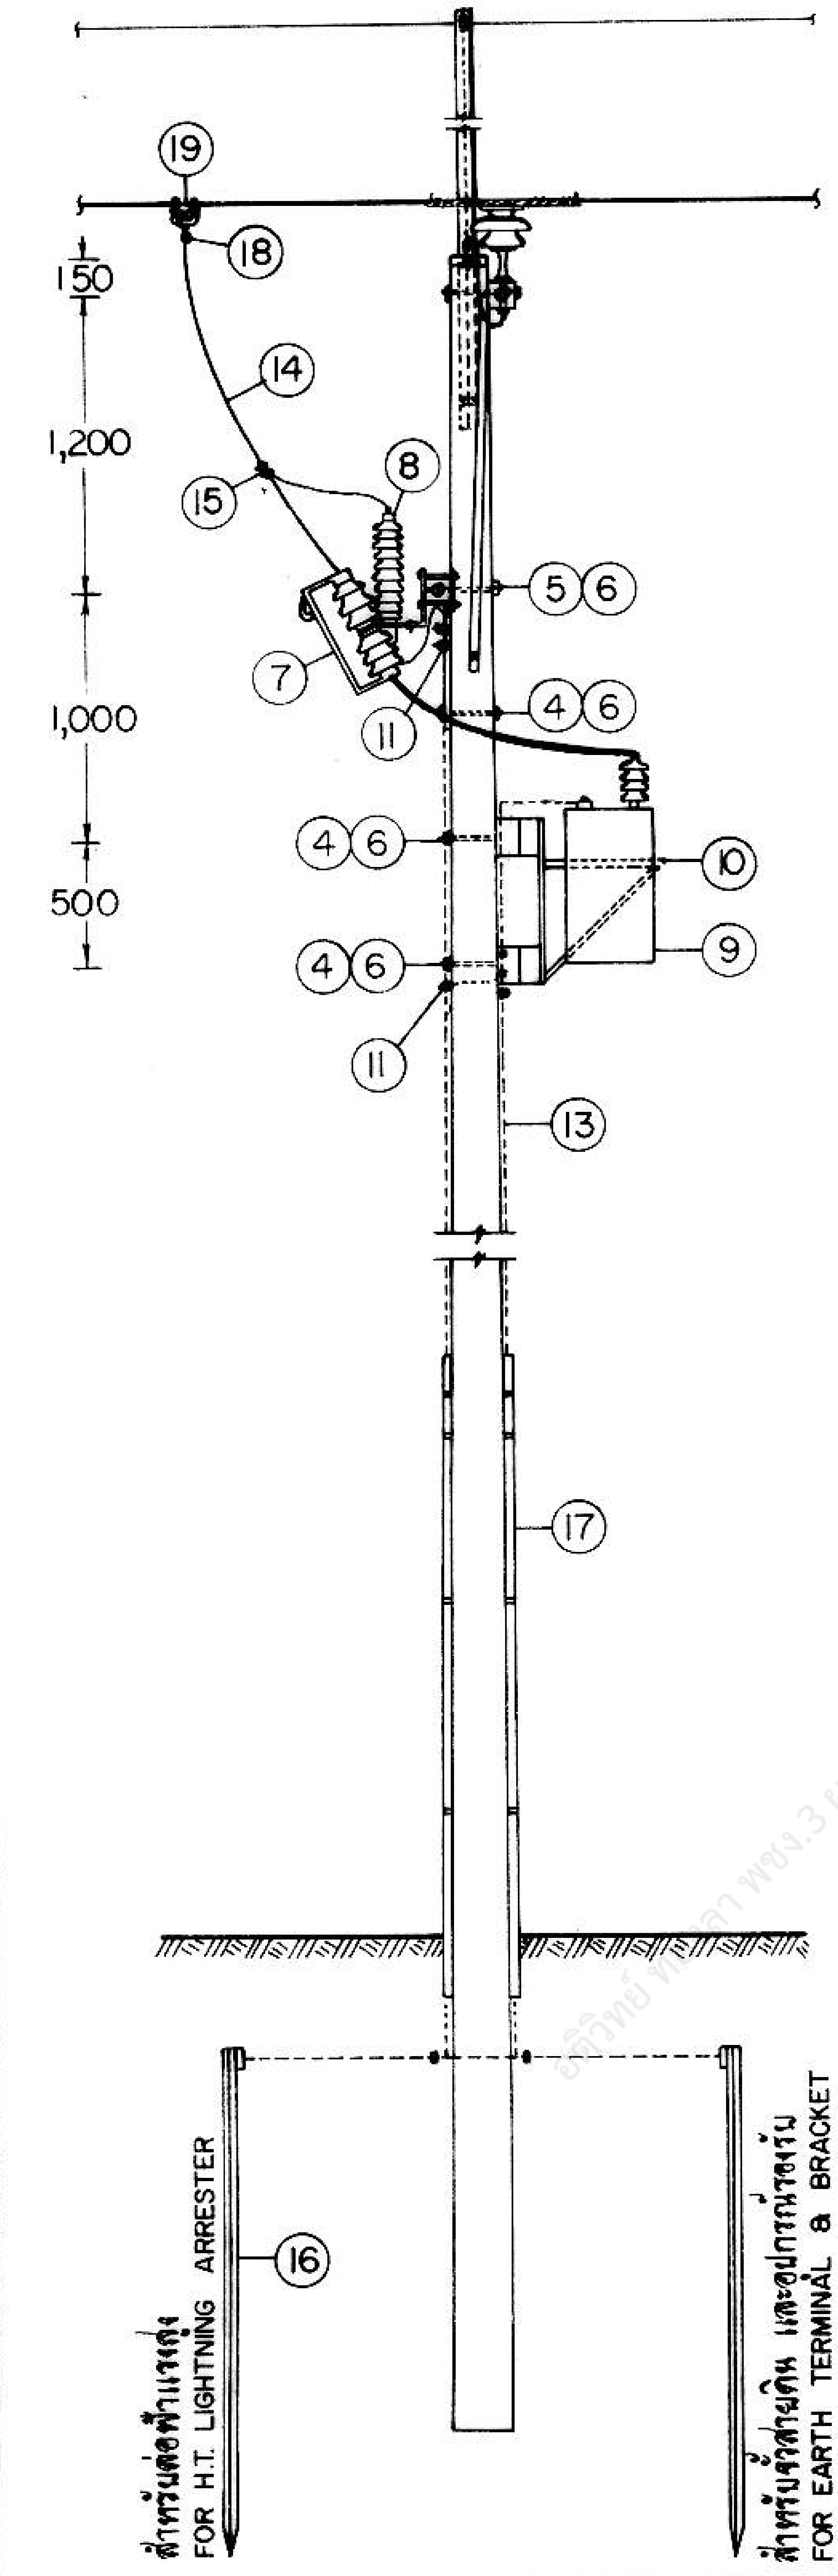

19
18
14
15
8
7
11
5 6
4 6
4 6
4 6
11
10
9
13
17
16
150
1,200
1,000
500
สำหรับต่อฟ้าแรงสูง FOR H.T. LIGHTNING ARRESTER
สำหรับจำสายดิน และอุปกรณ์รองรับ FOR EARTH TERMINAL & BRACKET

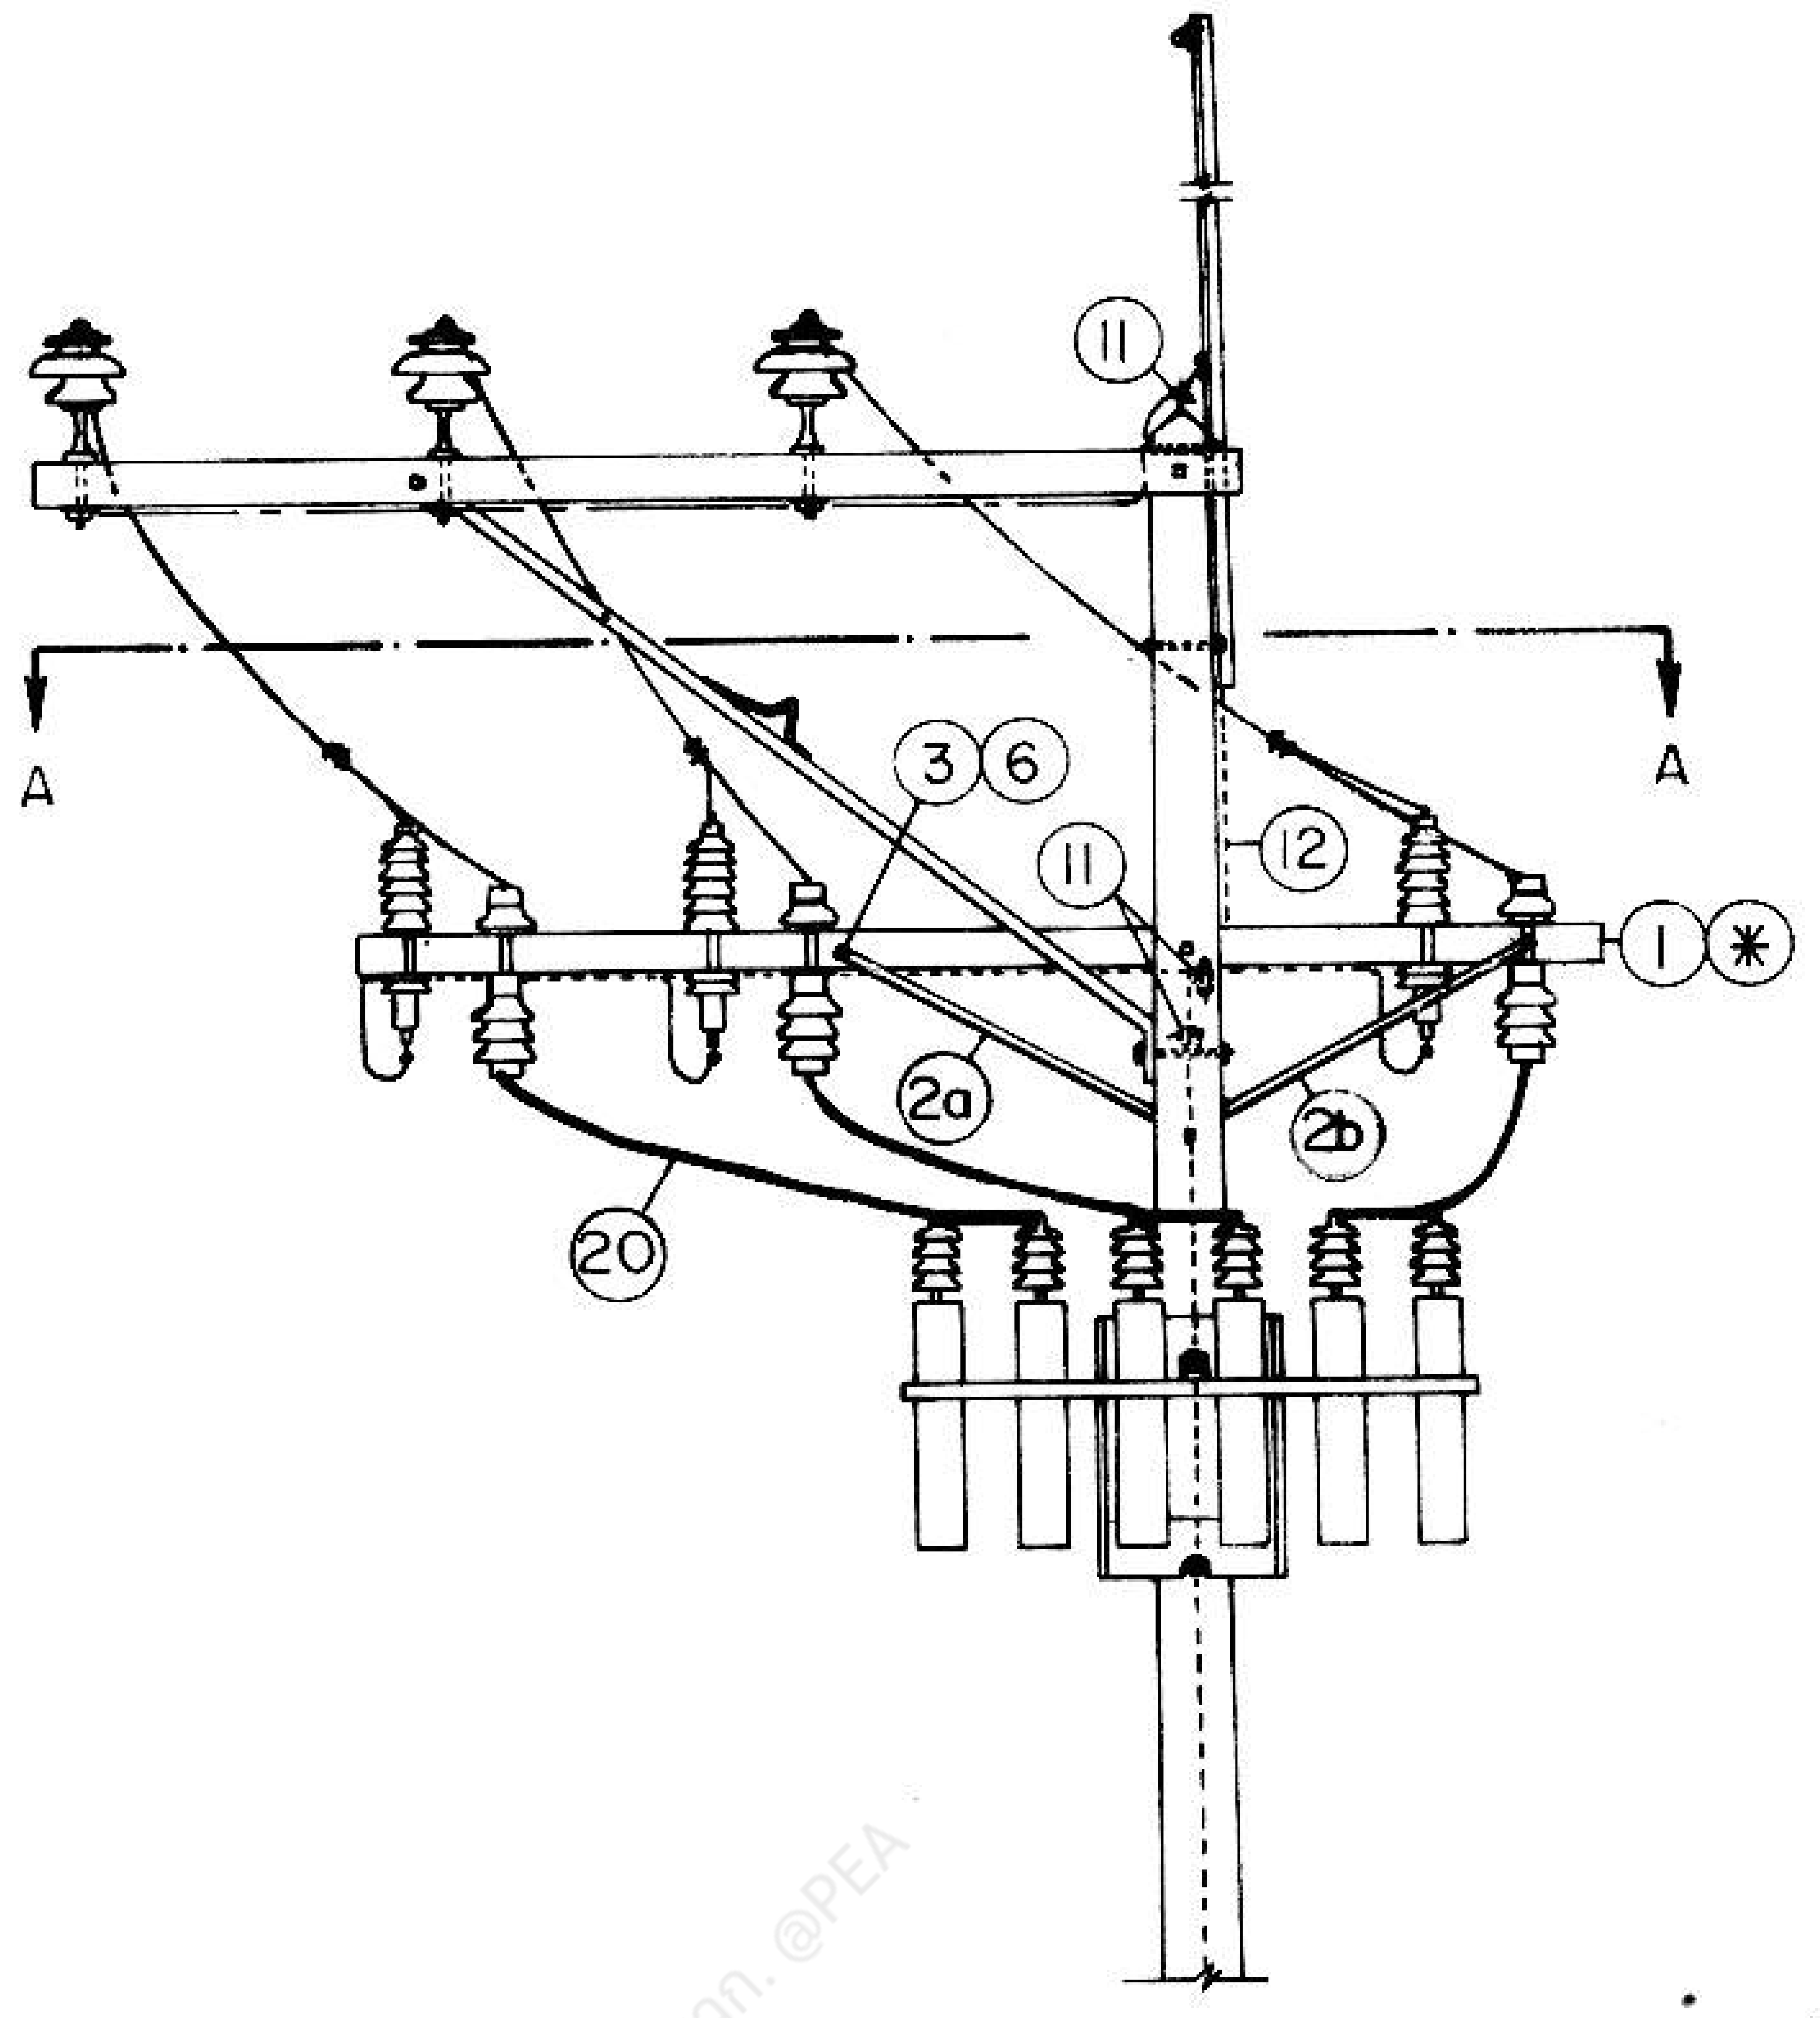

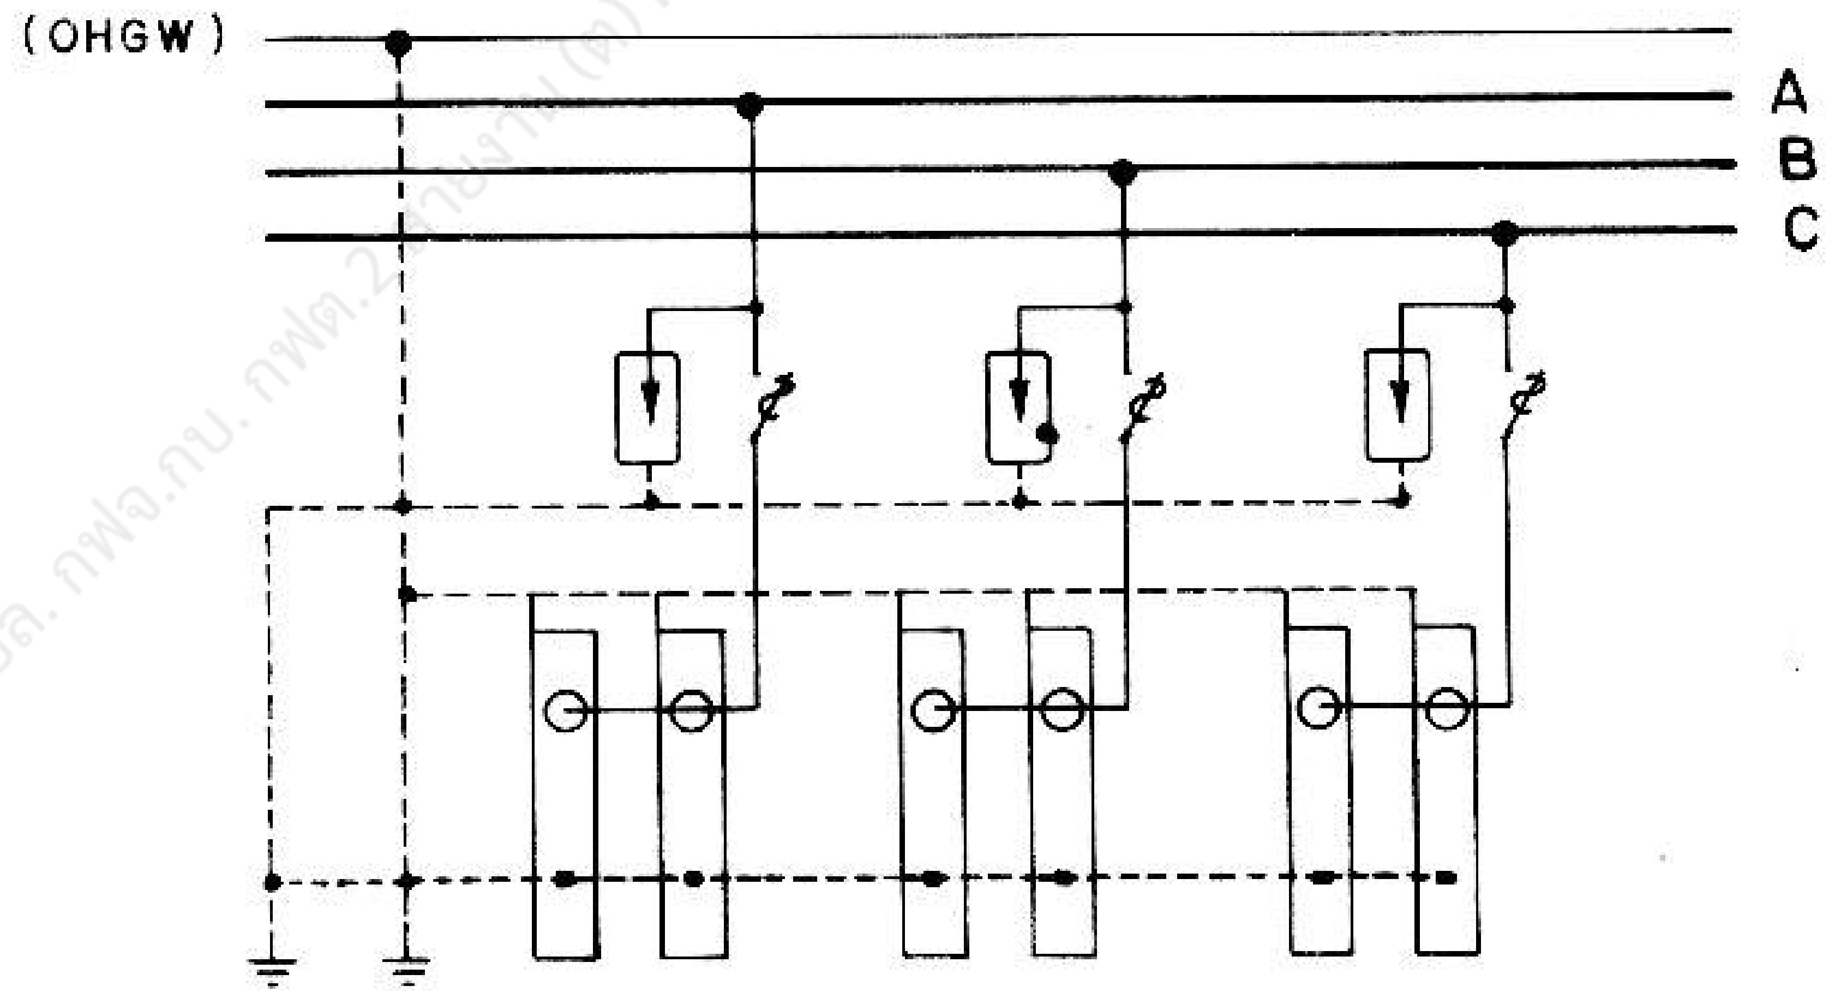

แผนผังแสดงการต่อแบบวาย
DIAGRAM OF WYE CONNECTION

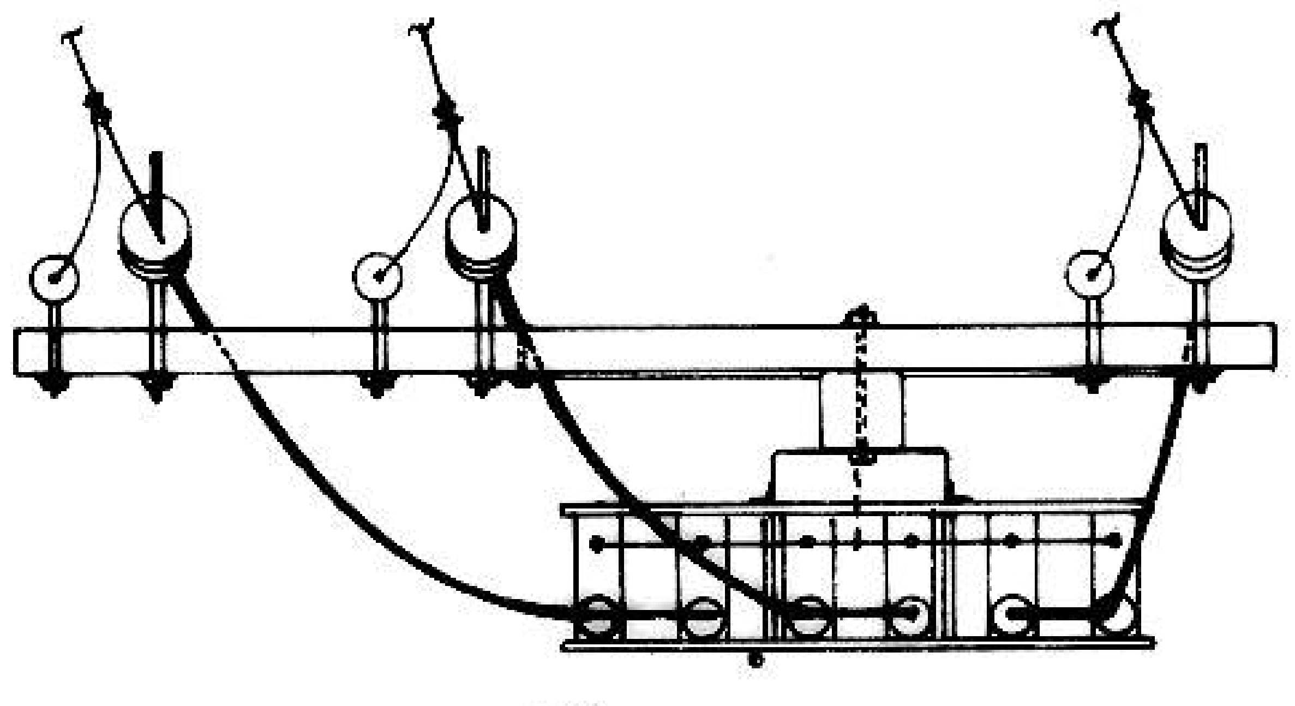

รูปตัด SECTION A—A

ลิขสิทธิ์ [illegible] พชง.3 ผปร. กฟส.อล. กฟจ.กบ. กฟต.2 [illegible] ผวก. @PEA

กองวิศวกรรมไฟฟ้าและเครื่องกล
ฝ่ายวิศวกรรม

ผู้เขียน
ผู้ตรวจ
วิศวกร
หัวหน้าแผนก
หัวหน้ากอง
ผู้อำนวยการฝ่าย

รองผู้ว่าการฝ่ายเทคนิค

การไฟฟ้าส่วนภูมิภาค

ผู้ว่าการ

2 5 พ.ย. 2520

การติดตั้งคะแปซิเตอร์ 33 kV
(สำหรับคอนแบนก้าวแขน)

CAPACITOR INSTALLATION 33 kV
(FOR ALLEY ARM)

ใช้แทนแบบ
ถูกแทนโดยแบบ
เขียนเสร็จวันที่ 17 พ.ย. 20
แก้แบบวันที่ 15 ธค.32
มิติเป็น มม.
มาตราส่วน 1 : 50

แบบเลขที่ SAI-015/20028
แผ่นที่ 1 ของจำนวน 3 แผ่น

การประกอบเลขที่ ASSEMBLY NO. **3602**

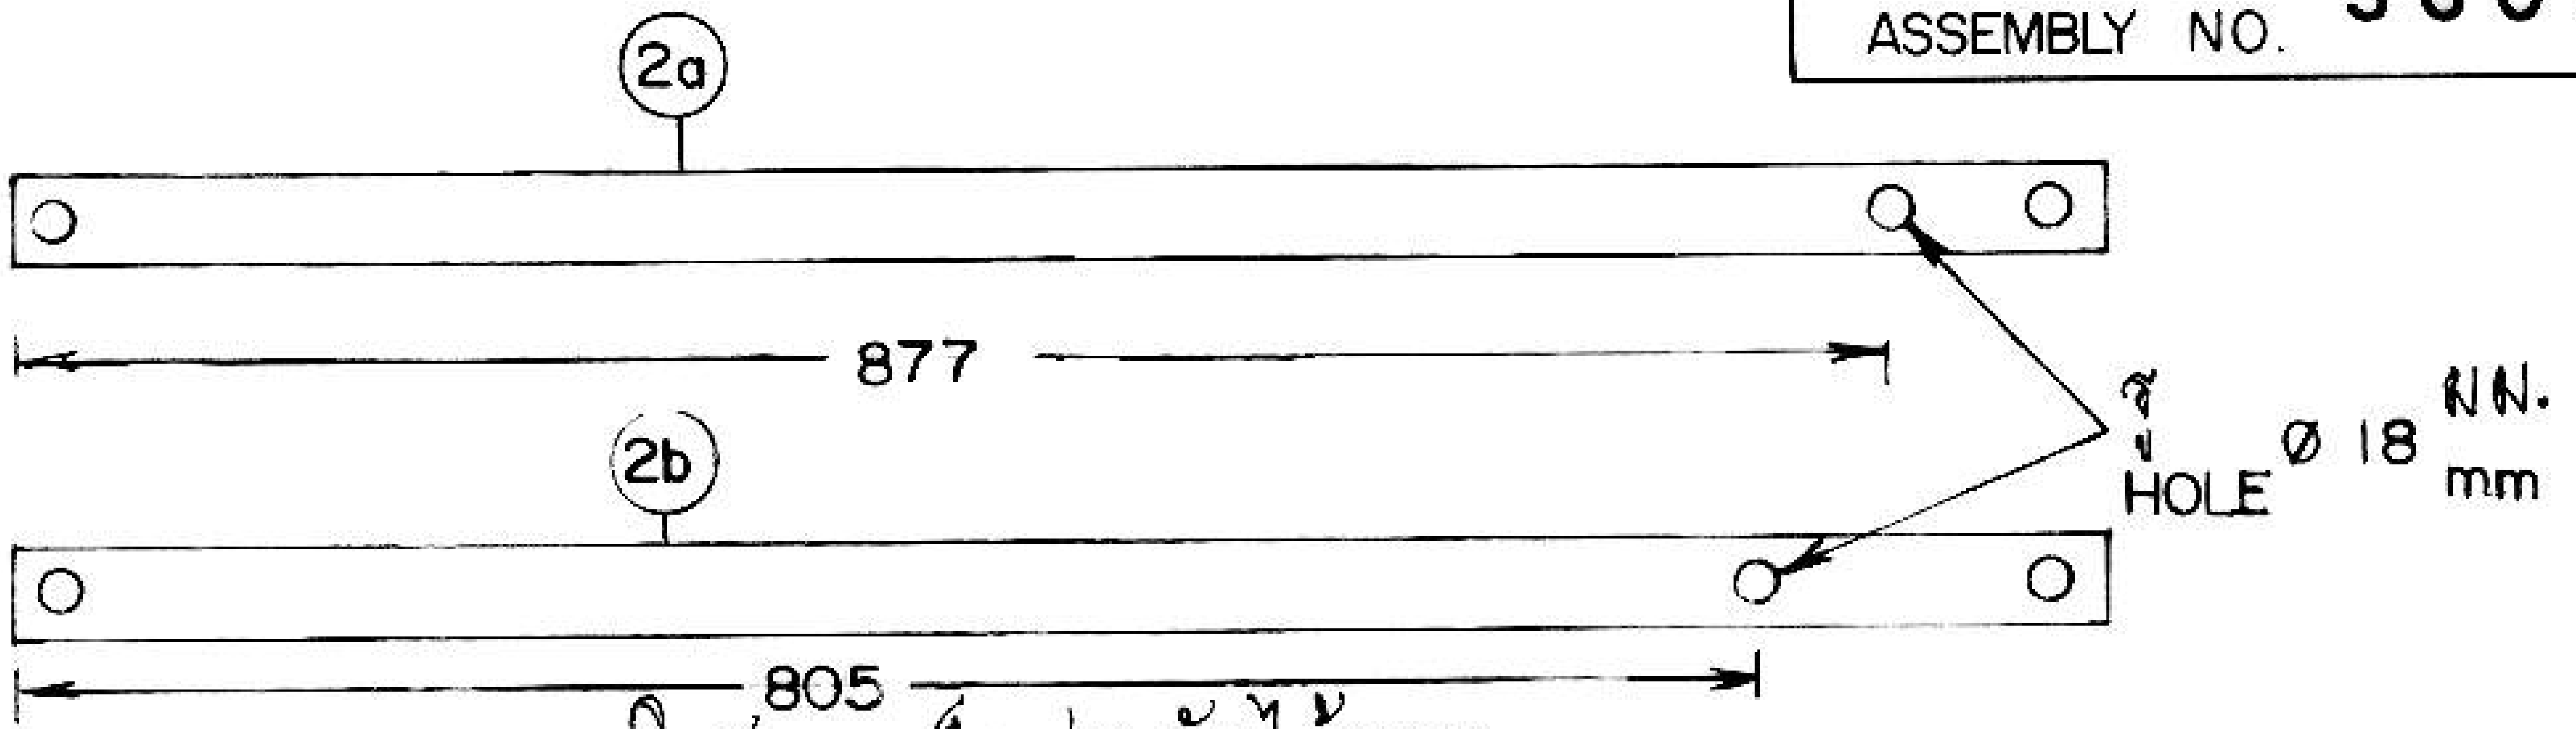

การเจาะรูพิเศษเหล็กประกับไม้คอน
BRACE, SPECIAL DRILLING

บัญชีวัสดุ
BILL OF MATERIAL

ลำดับที่ ITEM	รายละเอียด DESCRIPTION	จำนวน REQ'D	วัสดุเลขที่ MAT. NO.
1	คอน คอร. สปัน ขนาด 120 X 120 X 3,000 มม. CROSSARM, SPUN, PRESTRESSED CONCRETE 120X120X3,000 mm	1	00110002
2a,b	เหล็กประกับไม้คอน 40X6X1,000 มม. BRACE, FLAT, FOR CROSSARM 40X6X1,000 mm	2	01200002
3	สลักเกลียว M 16X170 มม. BOLT, MACHINE, M 16X170mm	2	01110201
4	สลักเกลียว M 16 X 250 มม. BOLT, MACHINE, M 16 X 250mm	3	01110203
5	สลักเกลียว M 16X 350 มม. BOLT, MACHINE, M 16X 350 mm	1	01110205
6	แหวนสี่เหลี่ยมแบน 52X52X4.5มม. รู Ø 18 มม. มอก. 258 WASHER, SQUARE, FLAT 52X52X4.5mm HOLE Ø 18mm TIS 258	9	01180100
7	ดรอพเอาท์ ฟิวส์คัตเอาท์ หนึ่งอินซูเลเตอร์ 33 kV 100 แอมป์ CUT-OUT, FUSE, OPEN TYPE, SINGLE INSULATOR, DROP-OUT, 33 kV, 100A	3	04010100
8	ล่อฟ้าแรงสูง 30 kV 5 กิโลแอมป์ LIGHTNING ARRESTER 30 kV, 5 kA	3	04000100
9	คะแปซิเตอร์ หนึ่งเฟสใช้นอกอาคาร 33 GRDY/19 kV 100 กิโลวาร์ CAPACITOR, POWER, SINGLE PHASE, OUTDOOR 33 GRDY/19 kV 100 kVar	6	05050100
10	ที่แขวนคะแปซิเตอร์ 11-33 kV 1X6 ชุด HANGER, CAPACITOR, 11-33 kV 1X6 SETS	1	05110001
11	ยูแคล้มป์ สลัก 1 ตัว M 8 (ไวร์ โร้ป คลิป) CLAMP, SINGL U-BOLT, M 8 (WIRE ROPE CLIP)	7	01230000
12	ลวดเหล็กตีเกลียว 25 ต.มม. มอก. 404 WIRE, STEEL STRANDED 25 mm^2 TIS 404	2 ม. m	01100002
13	ลวดเหล็กตีเกลียว 50/7 ต.มม. มอก. 404 พร้อมอุปกรณ์ยึด WIRE, STEEL STRANDED 50/7 TIS 404, COMP. WITH FIXING ACCESSORIES	24 ม. m	01100004
14	สายอะลูมิเนียมเปลือย 35 ต.มม. มอก. 85 CONDUCTOR 35 mm^2 TIS 85	6 ม. m	02010001
15	พีจี. คอนเนคเตอร์ สลักคู่ สำหรับสายอะลูมิเนียม 25-95 ต.มม. CONNECTOR, PARALLEL GROOVE, DOUBLE BOLT, Al 25-95 mm^2	3	02300102
16	หลักดิน 60 X 60 X 5 มม.ยาว 2,000 มม. GROUND ROD, 60X60X5 mm, 2,000 mm LONG	2	01220002

กองวิศวกรรมไฟฟ้าและเครื่องกล
ฝ่ายวิศวกรรม

ผู้เขียน
ผู้สำรวจ
วิศวกร
หัวหน้าแผนก
หัวหน้ากอง
ผู้อำนวยการฝ่าย
รองผู้ว่าการฝ่ายเทคนิค

การไฟฟ้าส่วนภูมิภาค

ผู้ว่าการ

2? พ.ย. 2520

การติดตั้งคะแปซิเตอร์ 33 KV
(สำหรับคอนแบบก้าวแขน)

CAPACITOR INSTALLATION 33 kV
(FOR ALLEY ARM)

ใช้แทนแบบ
ถูกแทนโดยแบบ
เขียนเสร็จวันที่ 17 พ.ย. 20
แก้แบบวันที่ 15 มีค.32
มิติเป็น มม.
มาตราส่วน 1 : 20

แบบเลขที่ SA1-015/20028
แผ่นที่ 2 ของจำนวน 3 แผ่น

การประกอบเลขที่
ASSEMBLY NO. 3602

บัญชีวัสดุ
BILL OF MATERIAL

ลำดับที่ ITEM	รายละเอียด DESCRIPTION	จำนวน REQ'D	วัสดุเลขที่ MAT. NO
17	ท่อ PVC แข็ง ขนาด Ø 20 X 2,500-4,000 มม. พร้อมอุปกรณ์ยึด CONDUIT, PVC RIGID, Ø 20 X 2,500-4,000 mm ; COMP. WITH FIXING ACCESS.	2	08040002 or 08040001
18	ฮอทไลน์แคล้มป์ สำหรับสายอะลูมิเนียม ขนาดตามต้องการ CLAMP, HOT LINE, FOR Al SIZE AS REQUIRED	3	02330100 or 02330101
19	สเตอร์รัพแคล้มป์ หรือเบลแคล้มป์ฮอทไลน์ ขนาดตามต้องการ CLAMP, STIRRUP OR BAIL, HOT LINE, MAIN LINE, Al SIZE AS REQUIRED	3	02330000 02330001
20	สายทองแดง หรืออะลูมิเนียมหุ้มฉนวน PVC, 750 โวลต์ ขนาด 35-50 ต.มม. มอก. 11 หรือ 293 CABLE, Cu OR AL, PVC INSULATED, 750 V, SIZE 35-50 mm² TIS 11 OR 293	7 ม. m	or 02070001 02070002

หมายเหตุ ระยะห่างที่ปลอดภัยทางไฟฟ้า ให้เป็นไปตามค่า ในแบบเลขที่ S02-015/17068

NOTE SAFETY CLEARANCE SHALL BE ACCORDING TO DRAWING NO. S02-015/17068.

อดิวิทย์ ทองลา พชง.3 ผปร. กฟส.อล. กฟจ.กบ. กฟต.2 สายงาน (ต) ผวก. @PEA

กองวิศวกรรมไฟฟ้าและเครื่องกล
ฝ่ายวิศวกรรม

ผู้เขียน
ผู้สำรวจ
วิศวกร
หัวหน้าแผนก
หัวหน้ากอง
ผู้อำนวยการฝ่าย

รองผู้ว่าการฝ่ายเทคนิค

การไฟฟ้าส่วนภูมิภาค

ผู้ว่าการ

25 พ.ย. 2520

การติดตั้งคะแปซิเตอร์ 33 KV
(สำหรับคอนแบบท้าวแขน)

CAPACITOR INSTALLATION 33 kV
(FOR ALLEY ARM)

ใช้แทนแบบ
ถูกแทนโดยแบบ
เขียนเสร็จวันที่ 17 พ.ย. 20
แก้แบบวันที่ 15 ธค. 32
มิติเป็น
มาตราส่วน

แบบเลขที่ SAI-015/20028
แผ่นที่ 3 ของจำนวน 3 แผ่น