การประกอบเลขที่
ASSEMBLY NO. 0516

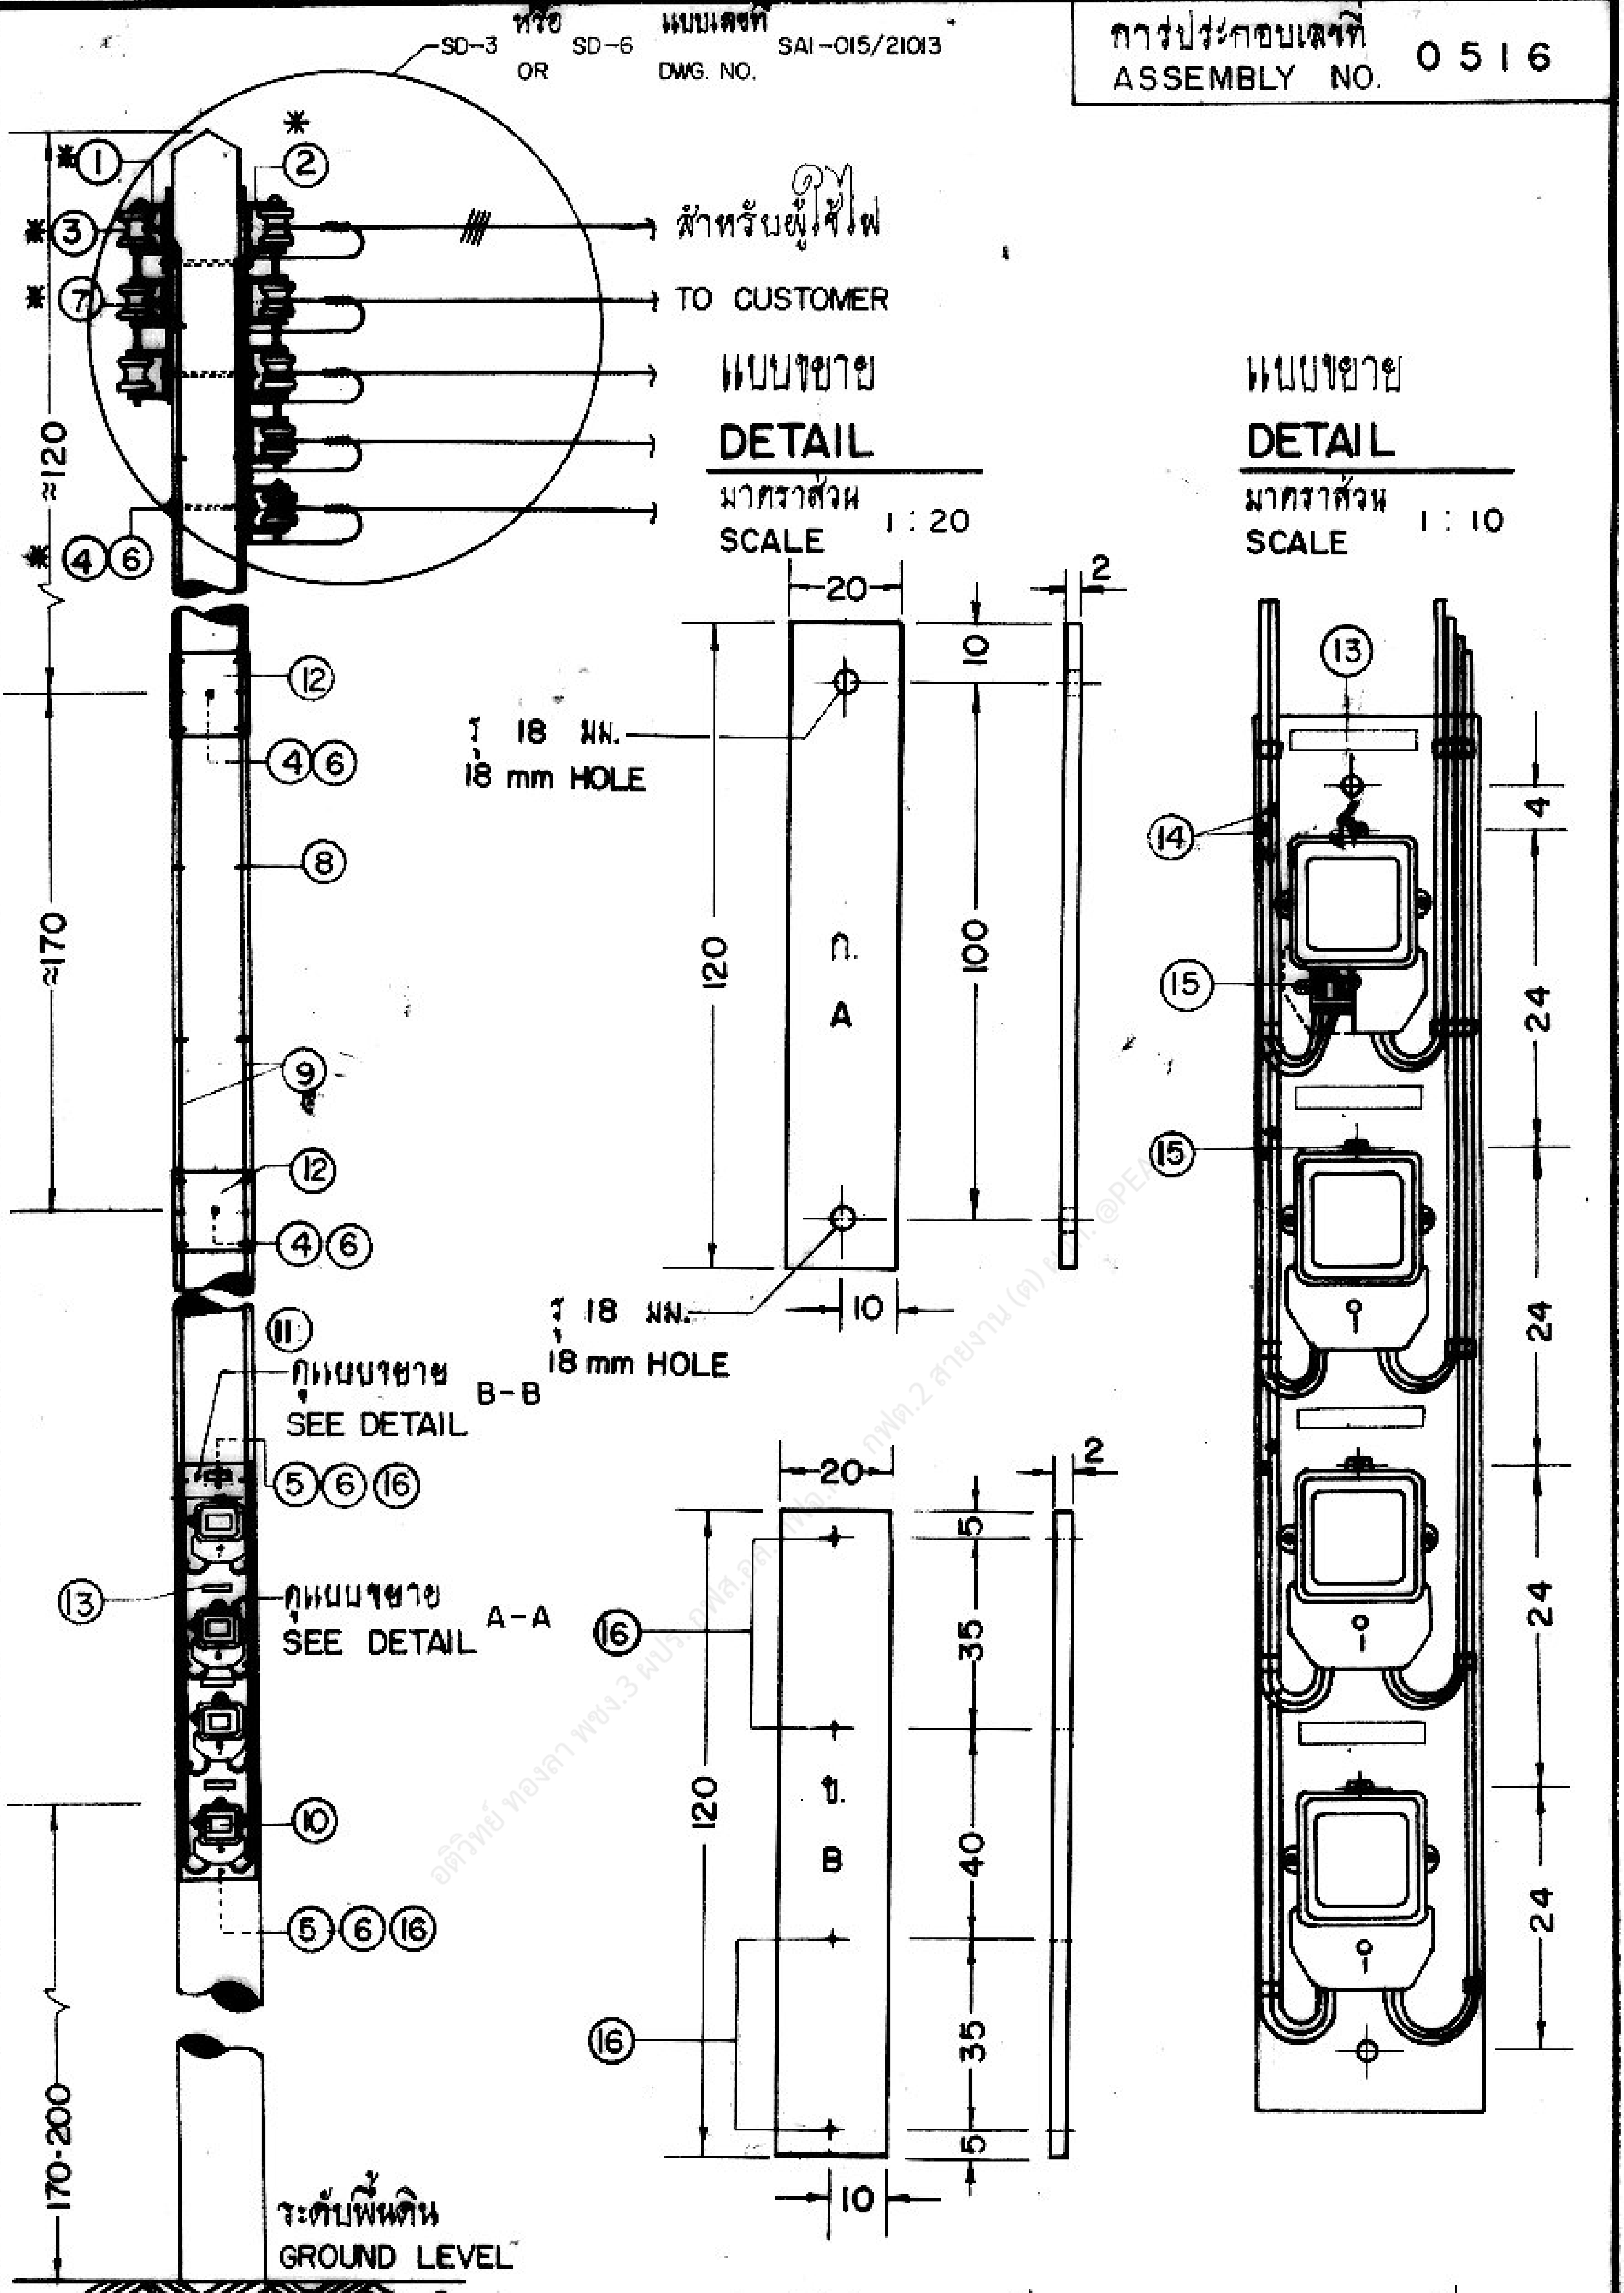
SD-3 หรือ OR SD-6 แบบเลขที่ DWG. NO. SAI-015/21013
*①
*②
*③
*⑦
*④⑥
≈120
สำหรับผู้ใช้ไฟ
TO CUSTOMER
แบบขยาย
DETAIL
มาตราส่วน
SCALE 1 : 20
แบบขยาย
DETAIL
มาตราส่วน
SCALE 1 : 10
⑫
④⑥
⑧
≈170
⑨
⑫
④⑥
⑪
ดูแบบขยาย B-B
SEE DETAIL
⑤⑥⑯
⑬
ดูแบบขยาย A-A
SEE DETAIL
⑩
⑤⑥⑯
170-200
ระดับพื้นดิน
GROUND LEVEL
รู 18 มม.
18 mm HOLE
20
10
120
100
ก.
A
2
รู 18 มม.
18 mm HOLE
10
20
2
⑯
5
35
120
ข.
B
40
⑯
35
5
10
⑬
⑭
4
⑮
24
⑮
24
24
24

* จำนวนอุปกรณ์ให้ดูแบบการประกอบอุปกรณ์ที่หัวเสา แบบเลขที่ SAI-015/21013 (การประกอบเลขที่ 0519)
NUMBER OF MATERIALS, SEE DWG. FOR POLE TOP ASSEMBLY, DWG. NO. SAI-015/21013 (ASSEMBLY NO. 0519)

กองวิศวกรรมและวางแผน

การไฟฟ้าส่วนภูมิภาค

ผู้เขียน
สถาปนิก
วิศวกร
หัวหน้าแผนก
ผู้อำนวยการกอง
รองผู้ว่าการฝ่ายเทคนิค

ผู้ว่าการ

การติดตั้งมิเตอร์ 1 เฟส สำหรับมิเตอร์ 3-4 ตัว
ขนาด 3-5 แอมแปร์

1-Ø METER INSTALLATION FOR 3-4 METERS
RATING 3-5 AMPERES

ใช้แทนแบบ I51-11003/1 OF 2
ถูกแทนโดยแบบ
เขียนเสร็จวันที่ 12 ม.ค. 15
แก้แบบวันที่ 17 ก.ค. 21
ผิดเป็น ชม.
มาตราส่วน

แบบเลขที่ I50-015/150003
แผ่นที่ 1 ของจำนวน 2 แผ่น

การประกอบเลขที่
ASSEMBLY NO. 0516

บัญชีวัสดุ
BILL OF MATERIAL

ลำดับที่ ITEM	รายละเอียด DESCRIPTION	จำนวน REQ'D ก/A	จำนวน REQ'D ข/B	วัสดุเลขที่ MAT. NO.
1	แร็คตามต้องการ RACK, SECONDARY, AS REQUIRED	–	–	03130000-2
2	แร็คสำหรับต่อเข้าบ้านผู้ใช้ไฟตามต้องการ RACK, SECONDARY TO CUSTOMER AS REQUIRED	–	–	03130000-2
3	ลูกรอกแรงต่ำ มอก. 227 แบบ ข (แบบ 53-2) INSULATOR, SPOOL TYPE, L.T. TIS 227 TYPE B (CLASS 53-2)	-	-	03030000
4	สลักเกลียวหัวเหลี่ยม M 16 X200 มม. พร้อมนัทเหลี่ยม BOLT, MACHINE M 16 X200 mm COMPLETE WITH SQUARE NUT	2	-	01110202
5	สลักเกลียวหัวเหลี่ยม M 16 X 250 มม. พร้อมนัทเหลี่ยม BOLT, MACHINE M 16 X 250 mm COMPLETE WITH SQUARE NUT	2	-	01110203
6a	แหวนเหลี่ยมแบนขนาด 52 X 52 X 4.5 มม. รู Ø 18 มม.มอก. 258 WASHER, SQUARE FLAT, 52 X 52 X 4.5 mm, HOLE Ø 18 mm, TIS 258	8	–	01180100
6b	แหวนเหลี่ยมโค้งขนาด 50X50X 5 มม. ขนาดรู 18 มม. WASHER, SQUARE CURVE, 50X50X 5 mm 18 mm HOLE	–	–	01180200
7	คอนเนคเตอร์สำหรับสายอะลูมิเนียมกับสายอะลูมิเนียมพันด้วย PVC เทป หุ้มด้วยคอมเปาด์ CONNEC. Al TO Al WRAPPED WITH PVC TAPE & COATED WITH INSUL.COM.	–	–	02300100-1 and 02180001
8	เข็มขัดรัดสายไฟ ช่วงระยะ 50 ซม. STRAP, CABLE, AT 50 cm INTERVALS			
9	สายอะลูมิเนียมหุ้มฉนวนเข้ามิเตอร์แรงต่ำ 0.6/1 kV CONDUCTOR, NAYY OR NAY 0.6/1 kV, Al	ม. m	ม. m	02070100-1
10	วัตต์อาวร์มิเตอร์ 1 เฟส METER, WATTHOUR, 1-Ø WITH EXTENDED TERMINAL COVER	3-4	3-4	06000000-1
11	แป้นไม้รองรับมิเตอร์ไสแล้ว ขนาด 120X20X2 ซม. METER PLATE (HARD WOOD) SURFACE FINISHED SIZE 120X20X2 cm	1	1	
12	แป้นไม้สำหรับยึดสายเข้าและออกจากมิเตอร์ไสแล้ว ขนาด 20X20X2 ซม. CABLE PLATE (HARD WOOD) SURFACE FINISHED SIZE 20X 20X2 cm	2	-	
13	หมายเลขผู้ใช้ไฟ NUMBER OF CUSTOMER	3-4	3-4	
14	ทีจี.คอนเนคเตอร์สลักเดียว สำหรับสายอะลูมิเนียมกับสายอะลูมิเนียมพันด้วย PVC เทป CONNECTOR, Al TO Al WRAPPED WITH PVC TAPE	4-6	4-6	02300201 and 02180001
15	ตะปูเกลียวขนาด 25 มม. SCREW, WOOD, SIZE 25 mm	9-12	9-12	
16	ตะปูเหล็กหัวกลมแบน ยาว 60 มม. Ø 2.80 มม. มอก. 113-2517 NAIL, ROUND MILD STEEL WIRE 60 mm LONG Ø 2.80 mm TIS 113-2517	-	4	

หมายเหตุ
1. ก สำหรับเสาคอนกรีตแรงต่ำ และ ข สำหรับเสาไม้แรงต่ำ
2. บัญชีวัสดุใช้เฉพาะการติดตั้งมิเตอร์แรงต่ำเท่านั้น ส่วนการประกอบอุปกรณ์ที่หัวเสาให้ดูแบบเลขที่ SAI-015/21013
3. สำหรับการติดตั้งบนเสาคอนกรีตแรงสูง 12 ม. ให้ใช้บัญชีวัสดุของเสาคอนกรีตแรงต่ำแต่ให้เพิ่มความยาวของสลักเกลียวอีก 50 มม.

NOTES
1. A. FOR L.T. CONCRETE POLE & B. FOR L.T. WOOD POLE.
2. BILL OF MATERIALS USE ONLY FOR L.T. METER INSTALLATION, SEE DWG. FOR POLE TOP ASSEMBLY, DWG. NO. SAI-015/21013
3. FOR INSTALLATION ON 12 m H.T. CONCRETE POLE, USE BILL OF MATERIAL FOR L.T. CONCRETE POLE BUT ADD 50 mm TO THE LENGTH OF MACHINE BOLT.

กองวิศวกรรมและวางแผน	การไฟฟ้าส่วนภูมิภาค	ใช้แทนแบบ 151-1003/2OF2 ถูกแทนโดยแบบ
ผู้เขียน สถาปนิก วิศวกร หัวหน้าแผนก ผู้อำนวยการกอง	ผู้ว่าการ	เขียนเสร็จวันที่ 12 ม.ค. 15 แก้แบบวันที่ 17 ก.ค. 21
	การติดตั้งมิเตอร์ 1 เฟส สำหรับมิเตอร์ 3 - 4 ตัว ขนาด 3 - 5 แอมแปร์	มิติเป็น มาตราส่วน
รองผู้ว่าการฝ่ายเทคนิค	1Ø METER INSTALLATION FOR 3-4 METERS RATING 3 - 5 AMPERES	แบบเลขที่ 150-015/150003 แผ่นที่ 2 ของจำนวน 2 แผ่น