
การประกอบเลขที่ ASSEMBLY NO. 5254

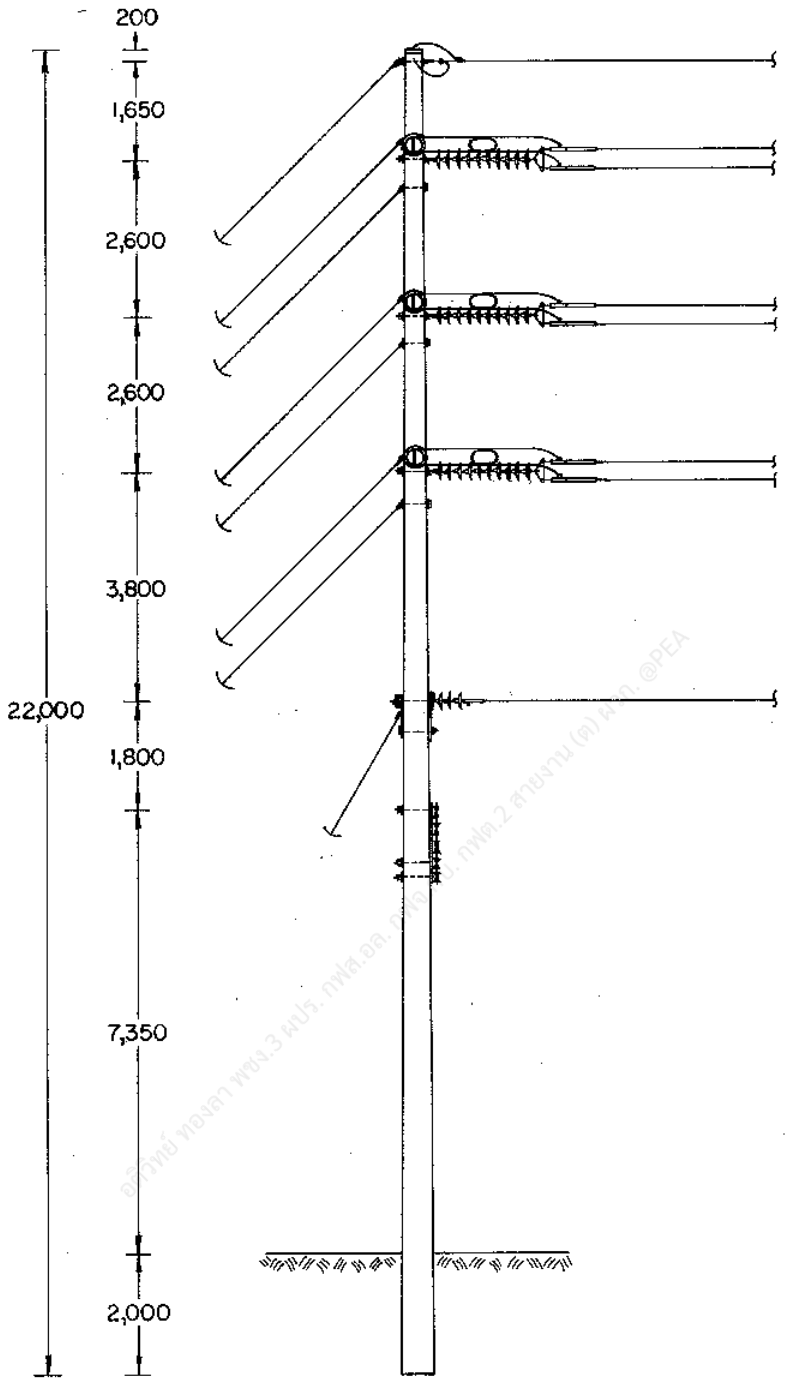

กองวิศวกรรมไฟฟ้าและเครื่องกล
ฝ่ายวิศวกรรม

ผู้เขียน
ผู้สำรวจ
วิศวกร
หัวหน้าแผนก
หัวหน้ากอง
ผู้อำนวยการฝ่าย
ผู้ว่าการฝ่ายเทคนิค

การไฟฟ้าส่วนภูมิภาค

ผู้ว่าการ

115 kV วงจรเดี่ยว สายไฟฟ้าคู่
เสาเดี่ยวสำหรับทางโค้ง 90°
แบบ SD-LA-1


115 kV SINGLE CIRCUIT DOUBLE CONDUCTOR
SINGLE POLE, 90° ANGLE STRUCTURE
TYPE SD-LA-1

ใช้แทนแบบ
ถูกแทนโดยแบบ
เขียนเสร็จวันที่ 2 N.A. 23
แก้แผนวันที่
มิติเป็น M.
มาตราส่วน 1 : 125

แบบเลขที่ SAI-015/23008
แผ่นที่ 1 ของจำนวน 3 แผ่น

19 มี.ค. 2523

การประกอบเลขที่ ASSEMBLY NO. 5254

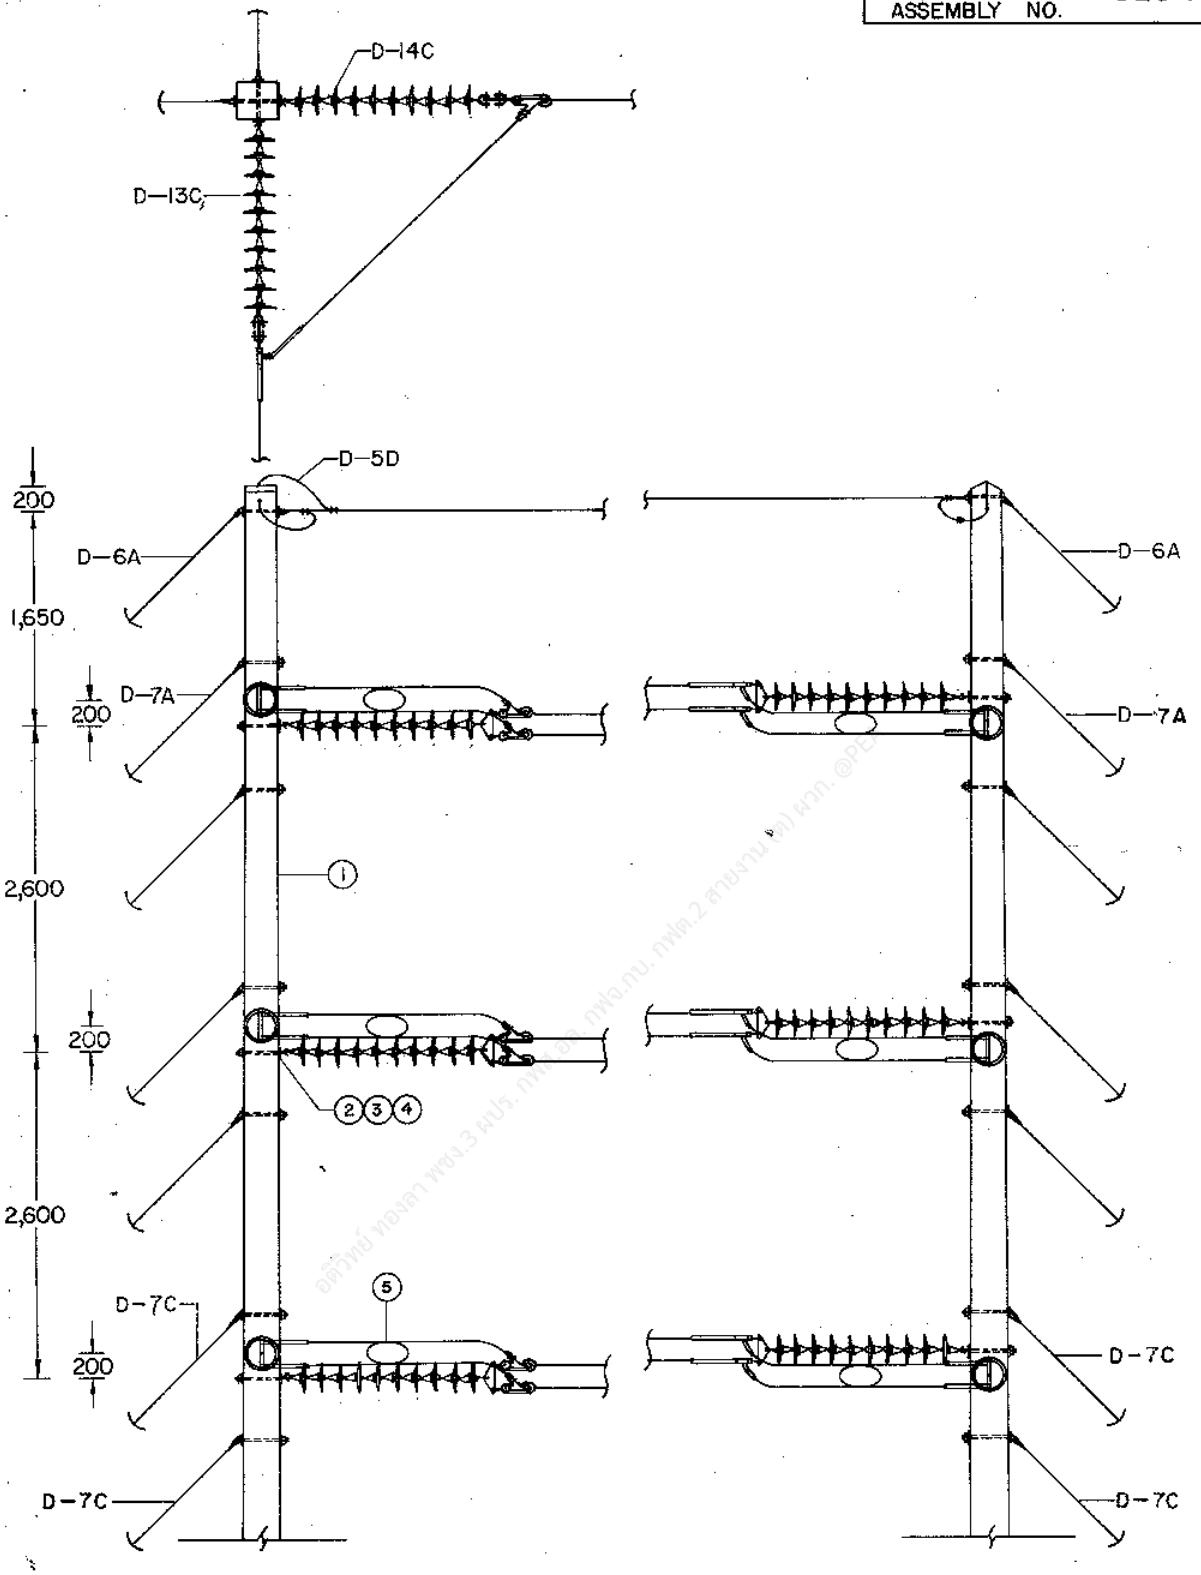

กองวิศวกรรมไฟฟ้าและเครื่องกล ฝ่ายวิศวกรรม	การไฟฟ้าส่วนภูมิภาค	ใช้แทนแบบ ถูกแทนโดยแบบ เขียนเสร็จวันที่ 2 ม.ค. 23 แก้แบบวันที่ 15 ก.ย. 40 มิติเป็น MM. มาตราส่วน 1 : 60
ผู้เขียน ผู้สำรวจ วิศวกร หัวหน้าแผนก หัวหน้ากอง ผู้อำนวยการฝ่าย รองผู้ว่าการฝ่ายเทคนิค	ผู้ว่าการ 115 kV วงจรเดียว สายไฟฟ้าคู่ เสาเดี่ยวสำหรับทางโค้ง 90° แบบ SD-LA-1 115 kV SINGLE CIRCUIT DOUBLE CONDUCTOR SINGLE POLE, 90° ANGLE STRUCTURE TYPE SD-LA-1	แบบเลขที่ SAI-015/23008 แผ่นที่ 2 ของจำนวน 3 แผ่น

14 มี.ค. 2523

การประกอบเลขที่ ASSEMBLY NO. **5254**

บัญชีวัสดุ
BILL OF MATERIAL

ลำดับที่ ITEM	รายละเอียด DESCRIPTION	จำนวน REQ'D	รหัสวัสดุเลขที่ MAT. NO.
1	เสาคอนกรีต 22 ม. POLE, CONCRETE 22 m LONG	1	00010011 (0041)
2	สลักห่วงโอเวล M 20X350 มม. BOLT, OVAL EYE M 20 X 350 mm.	6	01150100 (0260)
3	แหวนสี่เหลี่ยมแบน 62X62X6 มม. รู Ø 22 มม. มอก. 258 WASHER, SQUARE, FLAT 62X62X6 mm, HOLE Ø 22 mm, TIS 258	12	01180101 (0356)
4	แหวนสปริง M 20 มอก. 259 WASHER, LOCK, M 20, TIS 259	6	01180302 (0366)
5	สเปเซอร์ม้วนแยกสาย SPACER, HELICAL ROD, PREFORMED	3	02240000 (0918)

รายละเอียด
DETAIL

D-13C	การประกอบลูกถ้วยแขวน SUSPENSION INSULATOR ASSEMBLY	3	
D-14C	การประกอบลูกถ้วยแขวน SUSPENSION INSULATOR ASSEMBLY	3	
D-5D	การต่อสายล่อฟ้า OVERHEAD GROUND WIRE CONNECTION	1	
D-6A	การประกอบสายยึดโยงลวดเหล็กตีเกลียว 50 ต.มม. STEEL STRANDED WIRE 50 mm^2 GUY ASSEMBLY	2	
D-6C	การประกอบสายยึดโยงลวดเหล็กตีเกลียว 50 ต.มม. STEEL STRANDED WIRE 50 mm^2 GUY ASSEMBLY	1	
D-7A	การประกอบสายยึดโยงลวดเหล็กตีเกลียว 95 ต.มม. STEEL STRANDED WIRE 95 mm^2 GUY ASSEMBLY	8	
D-7C	การประกอบสายยึดโยงลวดเหล็กตีเกลียว 95 ต.มม. STEEL STRANDED WIRE 95 mm^2 GUY ASSEMBLY	4	
D-9A	สมอบกคอนกรีต CONCRETE ANCHOR	2	
D-10A	ฐานราก เสา POLE FOUNDATION	1	

กองวิศวกรรมไฟฟ้าและเครื่องกล
ฝ่ายวิศวกรรม

ผู้เขียน
ผู้สำรวจ
วิศวกร
หัวหน้าแผนก
หัวหน้ากอง
ผู้อำนวยการฝ่าย

รองผู้ว่าการสายเทคนิค

การไฟฟ้าส่วนภูมิภาค

ผู้ว่าการ

115 kV วงจรเดี่ยว สายไฟฟ้าคู่
เสาเดี่ยวสำหรับทางโค้ง 90°
แบบ SD-LA-1

115 kV SINGLE CIRCUIT DOUBLE CONDUCTOR
SINGLE POLE, 90° ANGLE STRUCTURE
TYPE SD-LA-1

ใช้แทนแบบ
ถูกแทนโดยแบบ
เขียนเสร็จวันที่ 2 พ.ค. 23
แก้แบบวันที่ 15 ก.ย. 40
มิติเป็น
มาตราส่วน

แบบเลขที่ SAI-015/23008
แผ่นที่ 3 ของจำนวน 3 แผ่น

19 มี.ค. 2523