

การประกอบเลขที่ ASSEMBLY NO. 0509

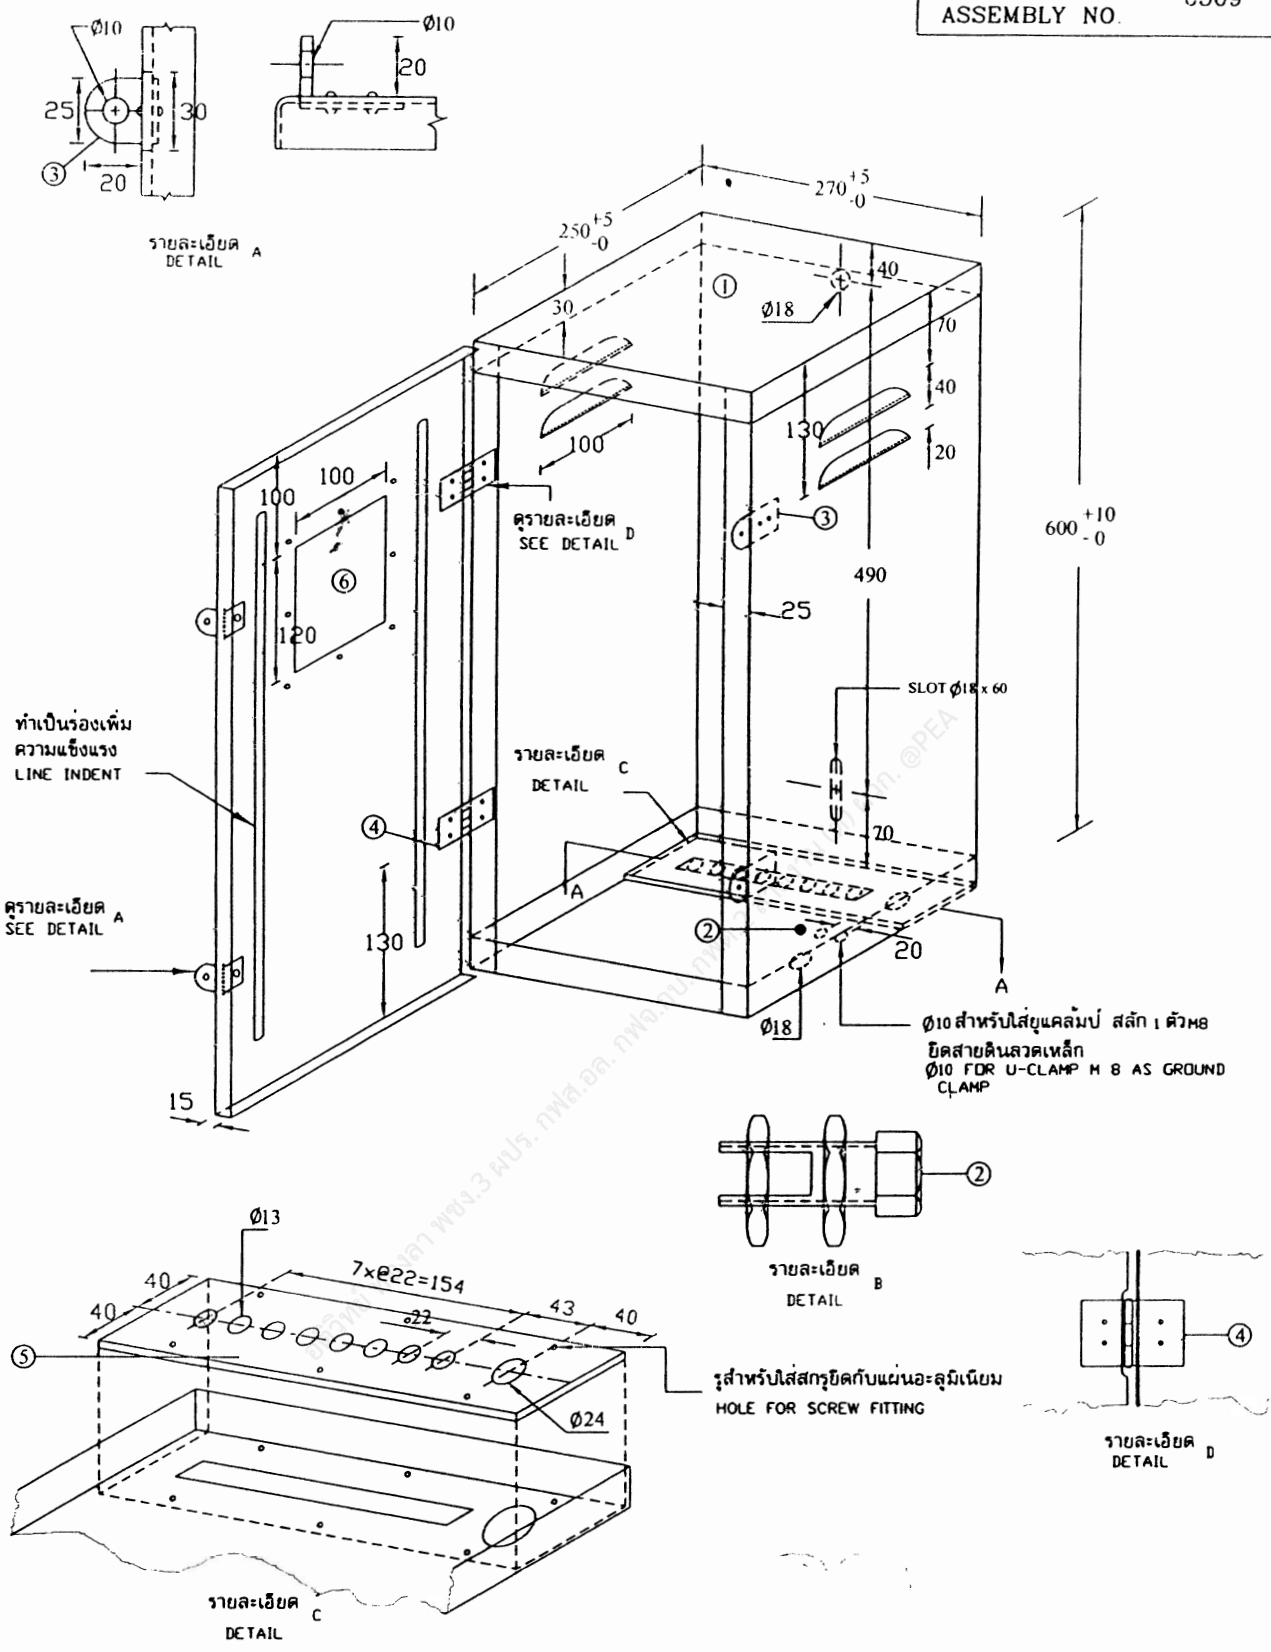


กองมาตรฐานระบบไฟฟ้า ฝ่ายมาตรฐานและความปลอดภัย	การไฟฟ้าส่วนภูมิภาค	ใช้แทนแบบ SA1-015/22042 SA1-015/22048
ผู้เขียน สิทธิพงษ์ มีโส	ผู้ว่าการ	ถูกแทนโดยแบบ -
ผู้สำรวจ		เขียนเสร็จวันที่ 15 ต.ค. 2552
วิศวกร	ตู้อะลูมิเนียมใช้นอกอาคาร สำหรับมิเตอร์ 3เฟส และมิเตอร์ทีโอยู	แก้แบบวันที่ -
หัวหน้าแผนก		มิติเป็น มิลลิเมตร
ผู้อำนวยการกอง		มาตราส่วน -
ผู้อำนวยการฝ่าย		
รองผู้ว่าการวางแผนและพัฒนาระบบไฟฟ้า	OUTDOOR ALUMINIUM CABINET FOR THREE-PHASE METER AND TOU METER	แบบเลขที่ SA2-015/52013
		แผ่นที่ 1 ของจำนวน 2 แผ่น

การประกอบเลขที่ ASSEMBLY NO.	0509

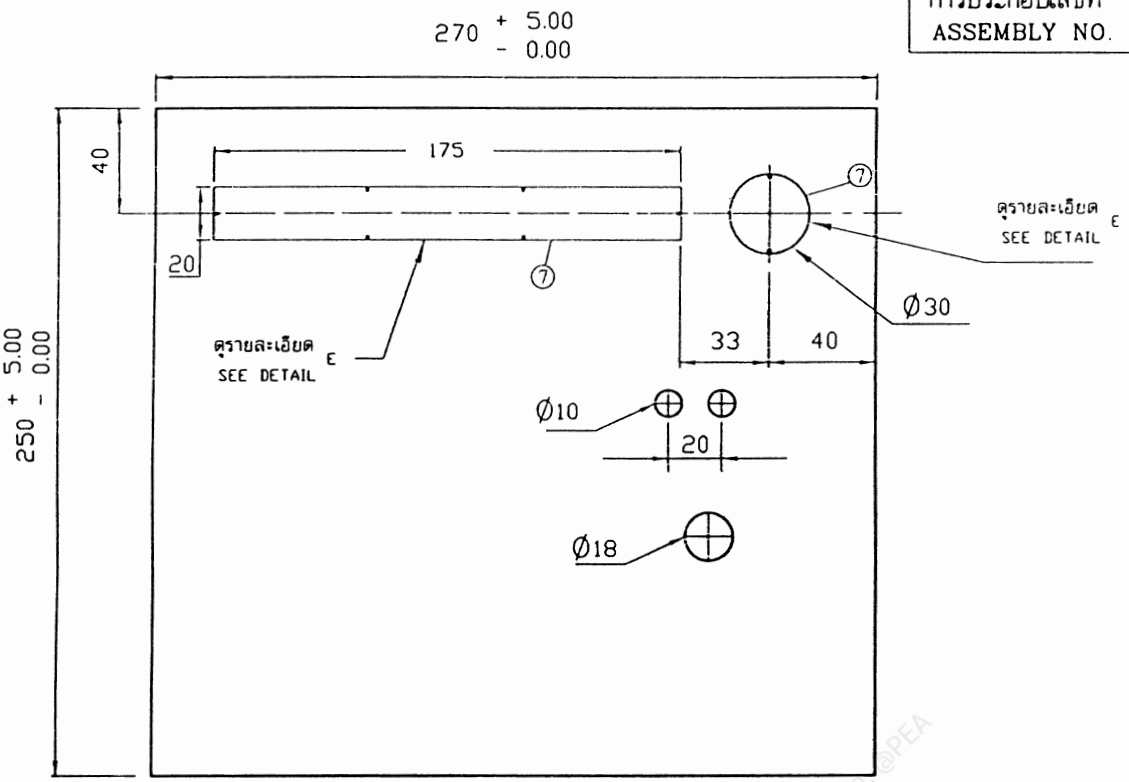

ภาพตัด A-A
SECTION

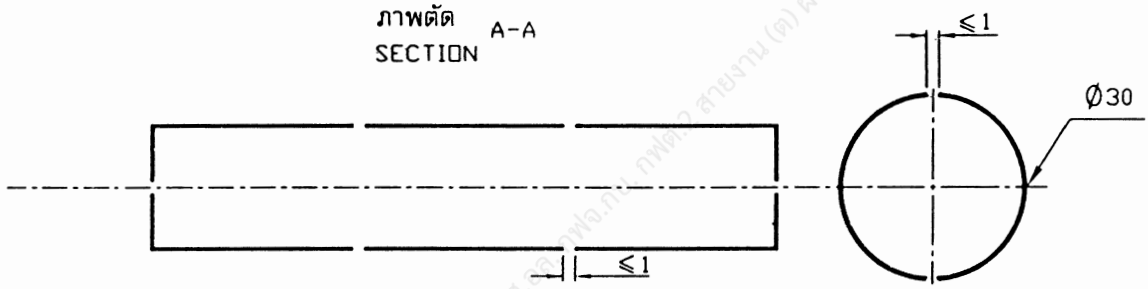

รายละเอียด E
DETAIL

1. ตู้ทำด้วยแผ่นอะลูมิเนียมความหนา 1.5 มม.
2. ขั้วยึดสายดินจับสายทองแดง ขนาด 4-16 มม. ประกอบด้วยสกรูทองเหลืองพร้อมนัท 2 ตัว (ดูรายละเอียด B)
3. แผ่นเหล็กอาบสังกะสี ความหนา 1.2 มม. และหมุดย้ำแบบไม่เป็นสนิม
4. บานพับทองเหลือง และหมุดย้ำแบบไม่เป็นสนิม
5. แผ่นเบ็คเกอร์ไลท์ (BAKELITE) หนา 8 มม. (5/16") เจาะรูสำหรับเข้าสายไฟฟ้าพร้อมสกรูยึดกับแผ่นอะลูมิเนียม 6 ตัว
6. หน้าต่างโพลีคาร์บอเนตใส (POLYCARBONATE)
7. ช่องเข้าสายไฟฟ้าทำเป็นแบบน็อกเอาท์ (KNOCKOUT)

หมายเหตุ
ค่าความคลาดเคลื่อนของรูเข้าสายไฟฟ้าเป็น ±0.1 ม.ม.

กองมาตรฐานระบบไฟฟ้า ฝ่ายมาตรฐานและความปลอดภัย	การไฟฟ้าส่วนภูมิภาค	ใช้แทนแบบ SA1-015/22042 SA1-015/22048
ผู้เขียน สิทธิพงษ์ มีโส ผู้สำรวจ วิศวกร หัวหน้าแผนก ผู้อำนวยการกอง ผู้อำนวยการฝ่าย	ผู้ว่าการ	ถูกแทนโดยแบบ – เขียนเสร็จวันที่ 15 ต.ค. 2552 แก้แบบวันที่ – มิติเป็น มิลลิเมตร มาตราส่วน –
รองผู้ว่าการวางแผนและพัฒนาระบบไฟฟ้า	ตู้อะลูมิเนียมใช้นอกอาคาร สำหรับมิเตอร์ 3เฟส และมิเตอร์ทีโอยู OUTDOOR ALUMINIUM CABINET FOR THREE-PHASE METER AND TOU METER	แบบเลขที่ SA2-015/52013 แผ่นที่ 2 ของจำนวน 2 แผ่น